




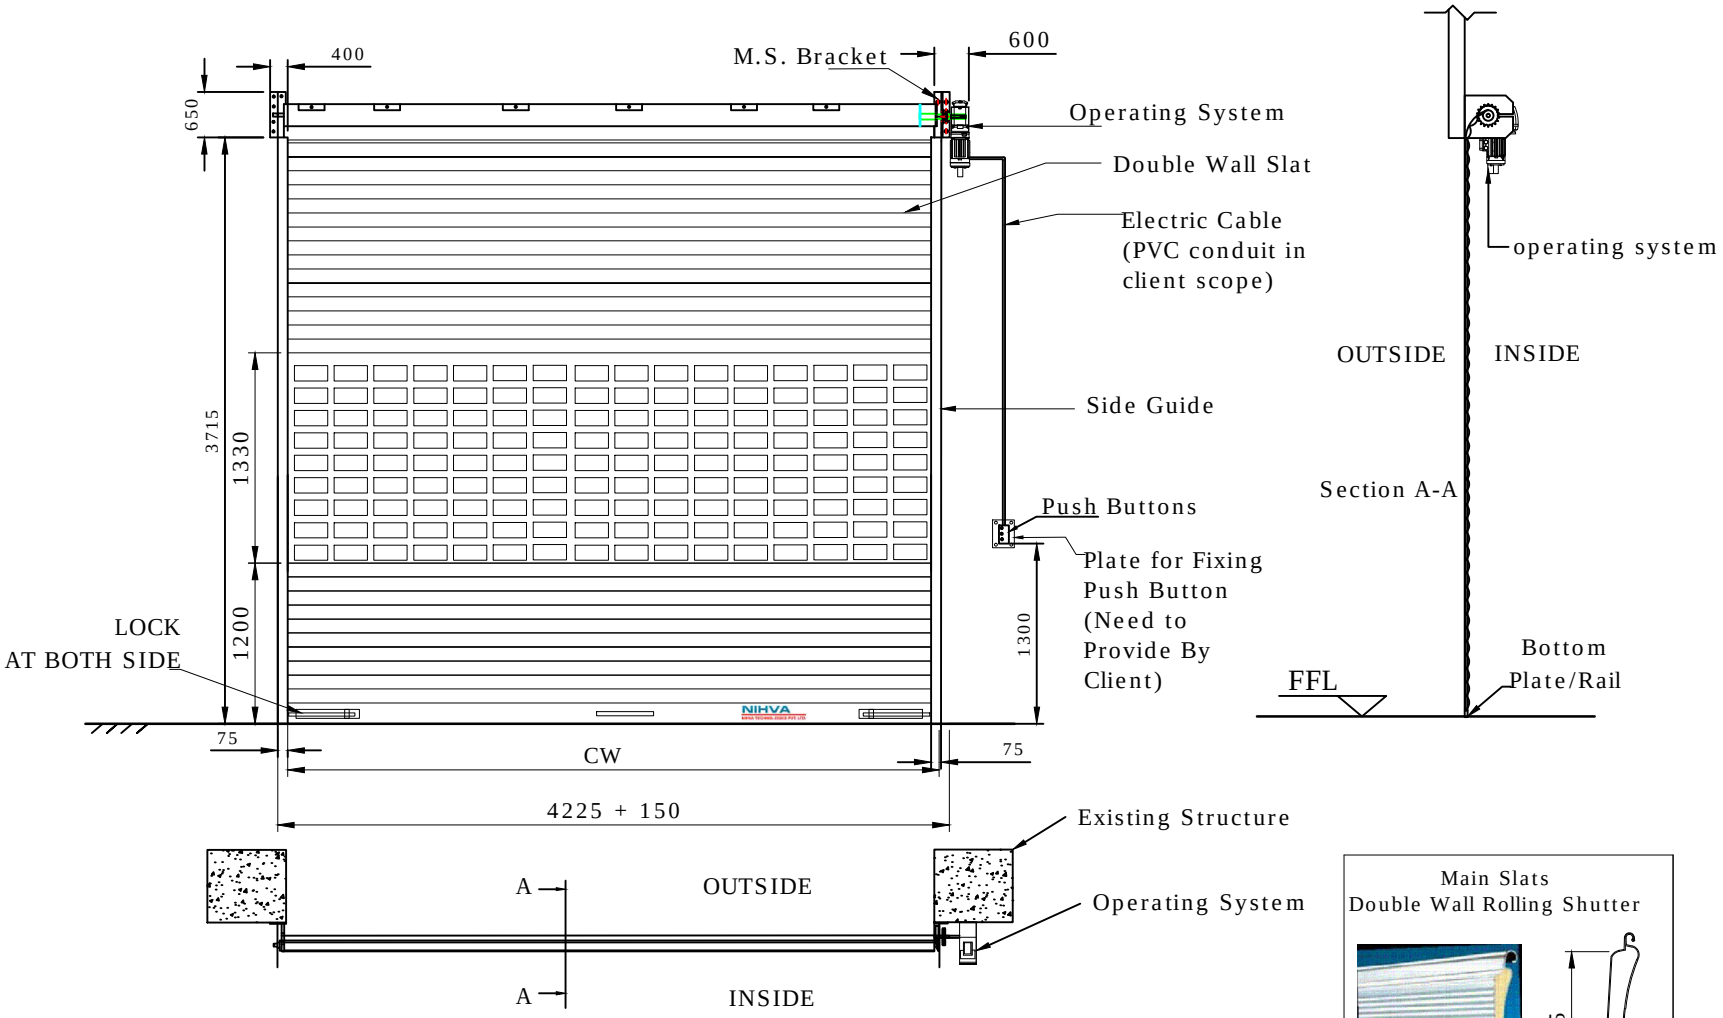

Main Slats
Double Wall Rolling Shutter

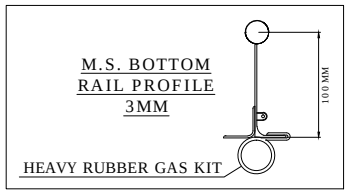

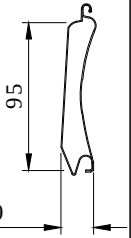

CLEAR WIDTH (CW)	CLEAR HEIGHT (CH)	QUANTITY
4225mm	3715mm	1 NOS

DIMENSION :

CLEAR WIDTH	CLEAR HEIGHT	QUANTITY
4225mm	3715mm	1NOS

MATERIAL :

THICKNESS :

NIHVA TECHNOLOGIES PVT. LTD.

NIHVA TECHNOLOGIES PVT. LTD. PUNE
Email:- info@nihva.com
Website:- www.nihva.com

TITLE:

DOUBLE WALL ROLLING SHUTTER

CLIENT'S APPROVAL :

CLIENT - SKF INDIA LTD.

PROJECT -

SITE LOCATION -CHINCHWAD

DWG. NO. : NIHVA/17-18/0018

SCALE: NTS	WT:	SHEET:1 OF 1

DRAWN BY: SURAJ	DATE: 18-04-2017
CHECK BY: OMKAR	DATE: 18-04-2017
APPROVED BY : R.K	DATE: 18-04-2017

If any queries contact : projects@nihva.com

NOTE: ALL DIMENSIONS ARE IN mm

THIS DRAWING & DESIGN IS THE PROPERTY OF NIHVA TECHNOLOGIES. NOT TO BE SOLD OR COPIED TO ANY OTHER CONCERN.