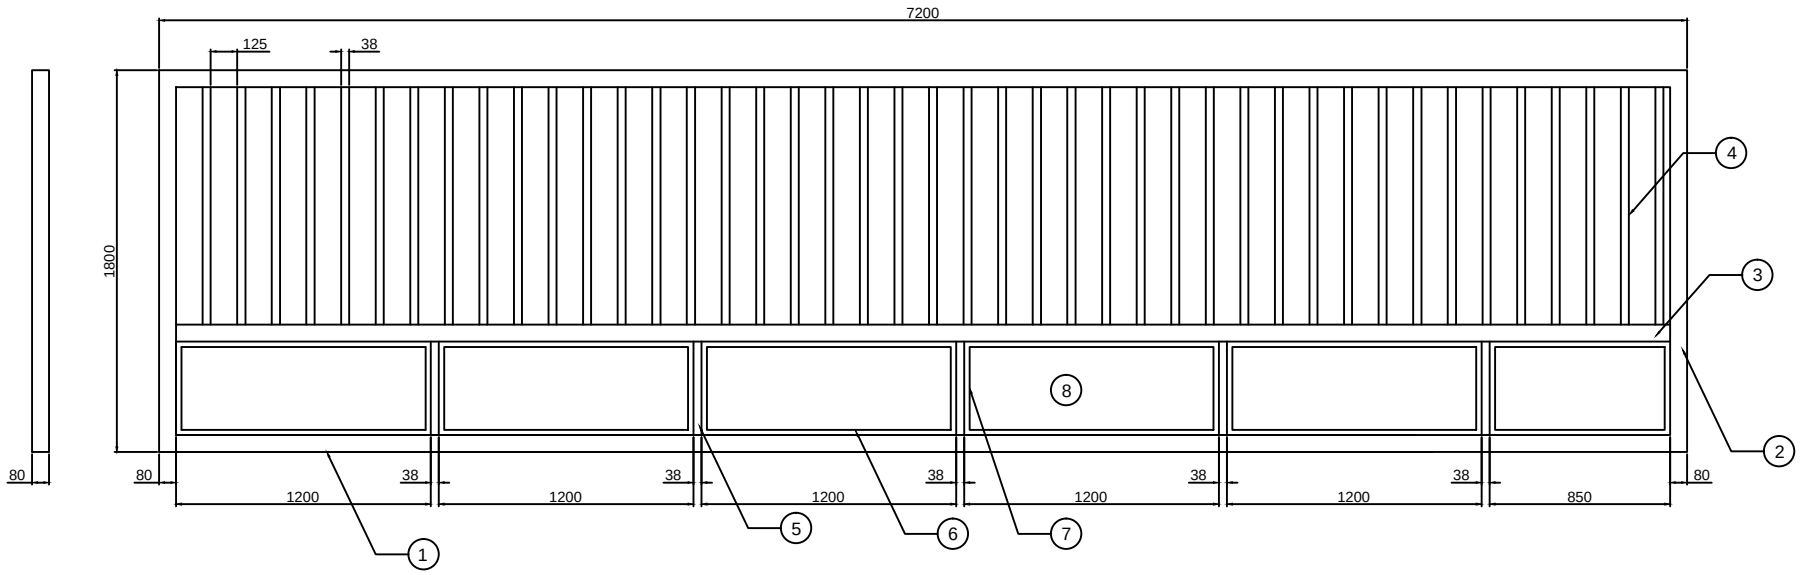

SR NO	DESCRIPTION	SPECIFICATION	QTY
8	PERFORATED SHEET	1190 X 1 MM X 430L	6 NOS
7	ISA	25 X 3 X 440L	12 NOS
6	ISA	25 X 3 X 1200L	12 NOS
5	SQ. TUBE	40 X 40 X 2.6 THK X 440L	5 NOS
4	SQ. TUBE	40 X 40 X 2.6 THK X 1120L	43 NOS
3	SQ. TUBE	80 X 80 X 3.2 THK X 7040L	1 NO
2	SQ. TUBE	80 X 80 X 3.2 THK X 1800L	2 NOS
1	SQ. TUBE	80 X 80 X 3.2 THK X 7200L	2 NOS

This drawing & designing is the property of NIHVA TECHNOLOGIES. Not be sold or copy to any other concern.

TITLE
MOTORIZED SLIDING GATE

NIHVA TECHNOLOGIES PVT. LTD.
NIHVA TECHNOLOGY PVT. LTD. PUNE
Tel : 020 66304033
Email:- info@nihva.com
Website:- www.nihva.com

	NAME	SIGN	DATE
DRAWN	P.V.A		26.09.2019
CHECK	G.J		26.09.2019
APPROVAL			

CLIENT -
PROJECT -
SITE LOCATION -
DWG. NO. : NIHVA/19-20/VDR/165 REV: R00
If any queries contact : projects@nihva.com
SCALE: 01 WT: SHEET: 01 OF 01
ALL DIMENSION ARE IN mm