
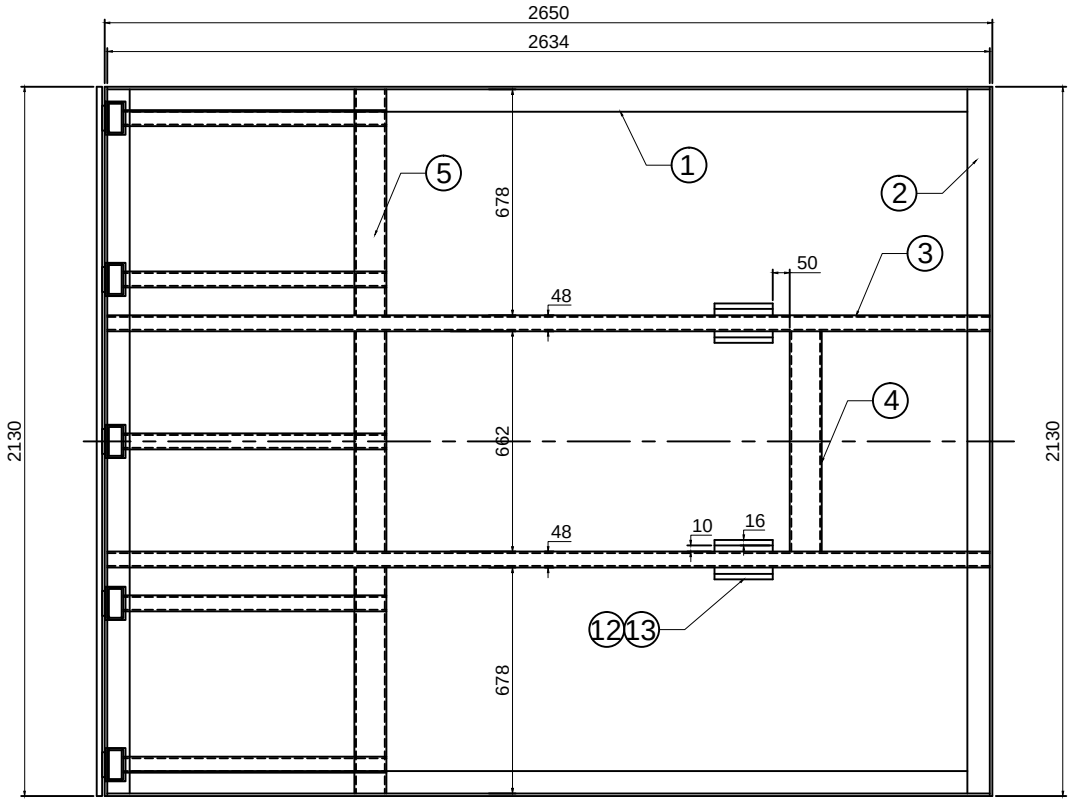


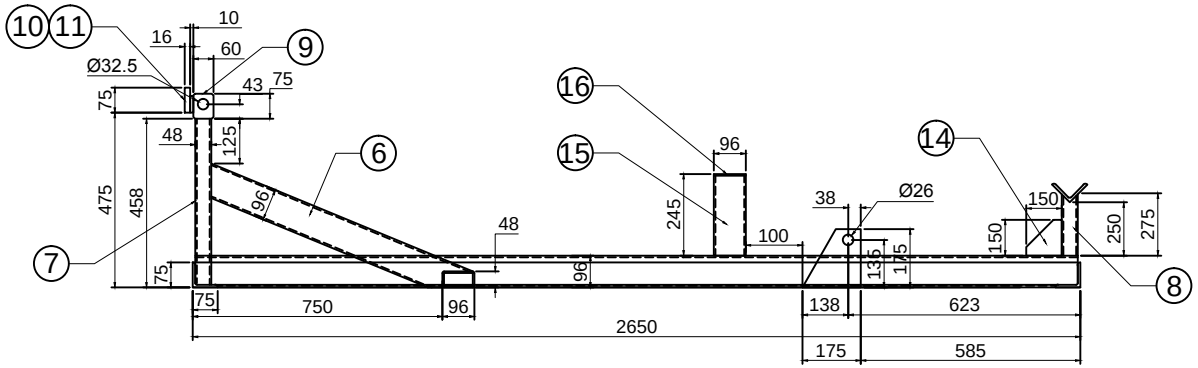

NOTE:~ MTL : MS

PART NO.	PART NAME	DESCRIPTION	QTY
1.	ISA	75 X 75 X 8 X 2640L (NOTCH)	2 NOS
2.	ISA	75 X 75 X 8 X 2130L	2 NOS
3.	R.TUBE	96 X 48 X 4.8 THK X 2632L	2 NOS
4.	R.TUBE	96 X 48 X 4.8 THK X 662L	2 NOS
5.	R.TUBE	96 X 48 X 4.8 THK X 678L	2 NOS
6.	R.TUBE	96 X 48 X 4.8 THK X 835L	5 NOS
7.	R.TUBE	96 X 48 X 4.8 THK X 450L	5 NOS
8.	R.TUBE	96 X 48 X 4.8 THK X 275L	2 NOS
9.	SOLID	75 X 60 X 100L	5 NOS
10.	FLAT	50 X 10 X 75L	5 NOS
11.	FLAT	75 X 16 X 2200L	2 NOS
12.	FLAT	100 X 20 X 150L	4 NOS
13.	PROFILE	175 X 16 X 175L	4 NOS
14.	PROFILE	150 X 10 X 150L	2 NOS
15.	R.TUBE	96 X 48 X 4.8 THK X 240L	2 NOS
16.	FLAT	50 X 5 X 100L	2 NOS

TITLE				
BASE FRAME ASSLY				
	NAME	SIGN	DATE	
DRAWN	P.V.A		28.06.2019	CLIENT -
CHECK	V.M.T		28.06.2019	PROJECT - NDL456
APPRD.				SITE LOCATION -
If any queries contact : design@nihva.com				DWG. NO. : NIHVA/19-20/VDR/094
ALL DIMENSION ARE IN mm				SCALE: NTS / WT: / REV- 01

NIHVA TECHNOLOGIES PVT. LTD.
NIHVA TECHNOLOGIES PVT. LTD, PUNE
Tel : 020 66304033
Email:- info@nihva.com
Website:- www.nihva.com