
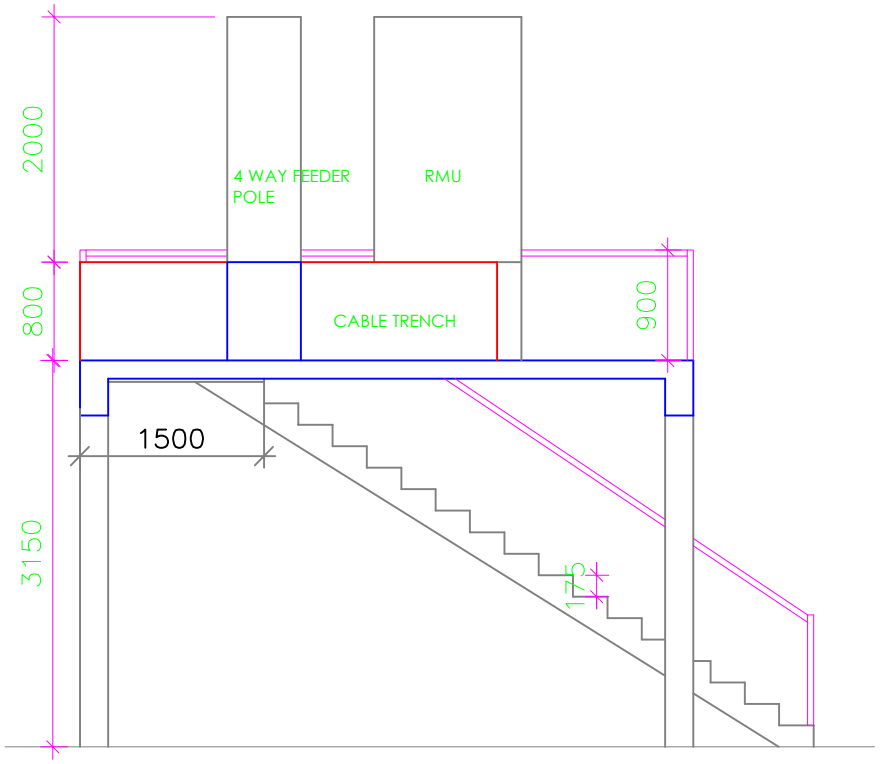


SECTION AA

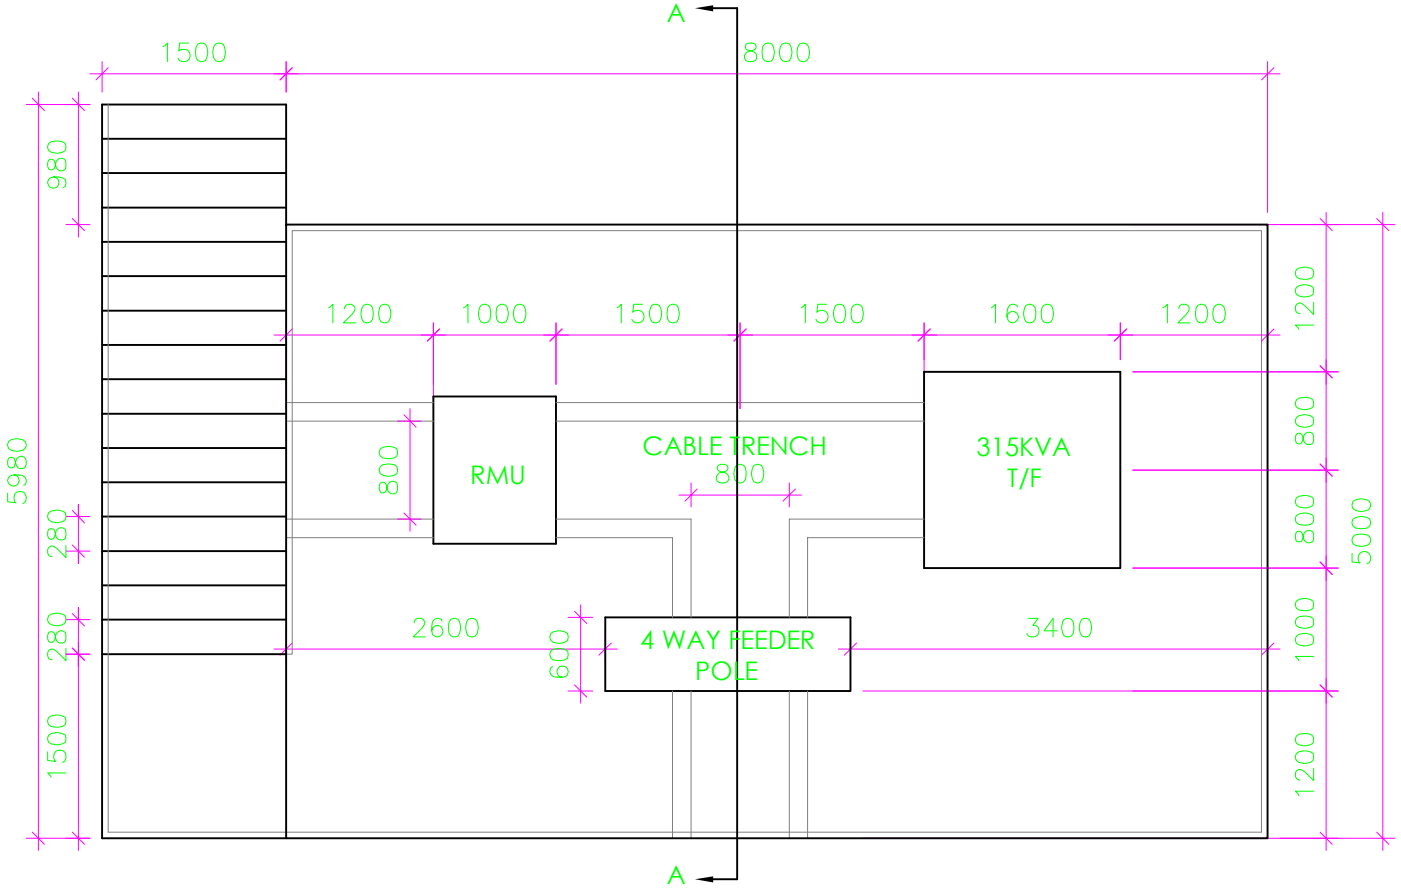

SUBSTATION PLAN

NOTES :

1) ONLY WRITTEN DIMENSIONS ARE TO BE FOLLOWED.
2) READ THIS DRAWING ALONG WITH THE RELEVANT DEPT. DRAWING.
3) ANY AMBIGUITY IN THIS DRAWING TO BE REFERED TO THE CONSULTANT BEFORE EXECUTION OF THE WORK
4) ALL DIMENSIONS ARE IN mm

TITLE:

SUBSTATION LAYOUT

CLIENT: MANIK ENGINEERING

ADDRESS: PROPOSED BUILDING AT NAHRE FOR MANIK ENGINEERING

DWG.No. MAN575/AR037/WD/06

REVISION :	R0	DRAWN BY :	
SCALE :	NTS	CHECKED BY :	SAGAR
DATE :	09/10/24	APPROVED BY :	

ARCHIVISTA
ENGINEERING PROJECTS PVT.LTD.
Office No.201&202,Sai Empire, Baner,
PUNE-411045, MAHARASHTRA,INDIA.
PH.91-20-6629444,460
www.archivistaindia.com