



SLIDING DIRECTION

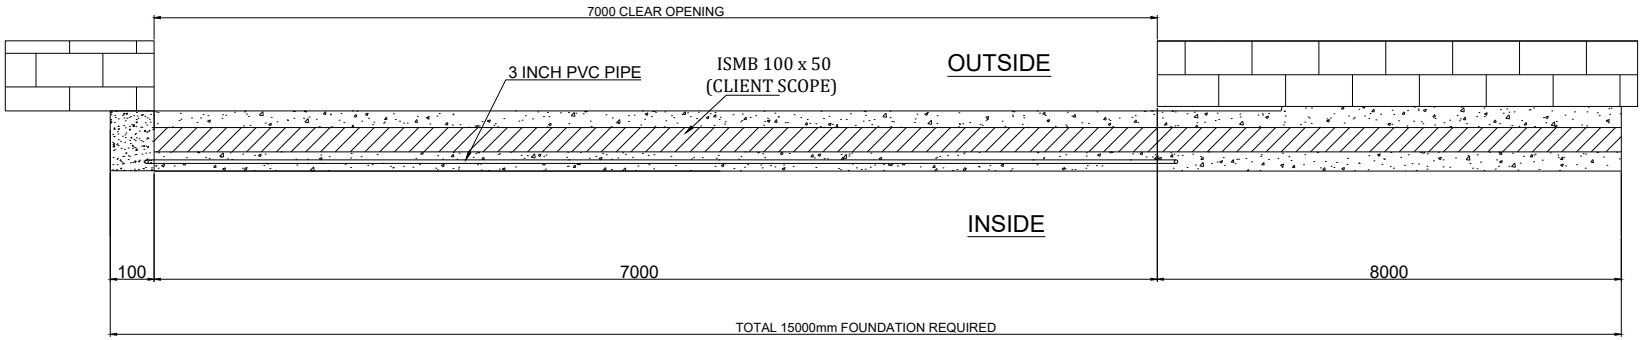

PLAN

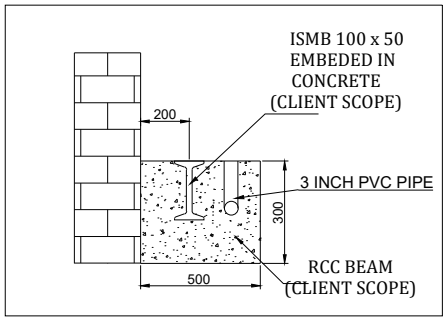

This drawing & design is the property of NIHVA TECHNOLOGIES. Not to be sold or copied to any other concern.

TITLE	FOUNDATION OF SLIDING GATE			NIHVA TECHNOLOGIES PVT. LTD. PUNE Tel : 020 66304033 Email:- info@nihva.com Website:- www.nihva.com	
	NAME	SIGN	DATE		
DRAWN	B.S		15.04.2026	CLIENT - CG POWER	
CHECK	V.T		15.04.2026	PRODUCT - SLIDING GATES	
APPRD.	V.T		15.04.2026	FORMAT NO - NIHVA-DD-F-03	
If any queries contact : design2@nihva.com				DWG. NO. : NIHVA/26-27	REV- R00
ALL DIMENSION ARE IN mm				SCALE: NTS	WT: SHEET: