

REV.	DESCRIPTION.	REVISED BY	SIGN	DATE
000	RELEASED GA DWG FOR APPROVAL	MAHESH S.		07.11.22
001	MODIFIED GA DWG PER SITE VISIT CHANGES	MAHESH S.		29.11.22
002	MODIFIED GA DWGs PER SPECIFIC ROOF OUT OF TWO	MAHESH S.		30.12.22

PROPOSED PLAN LAYOUT

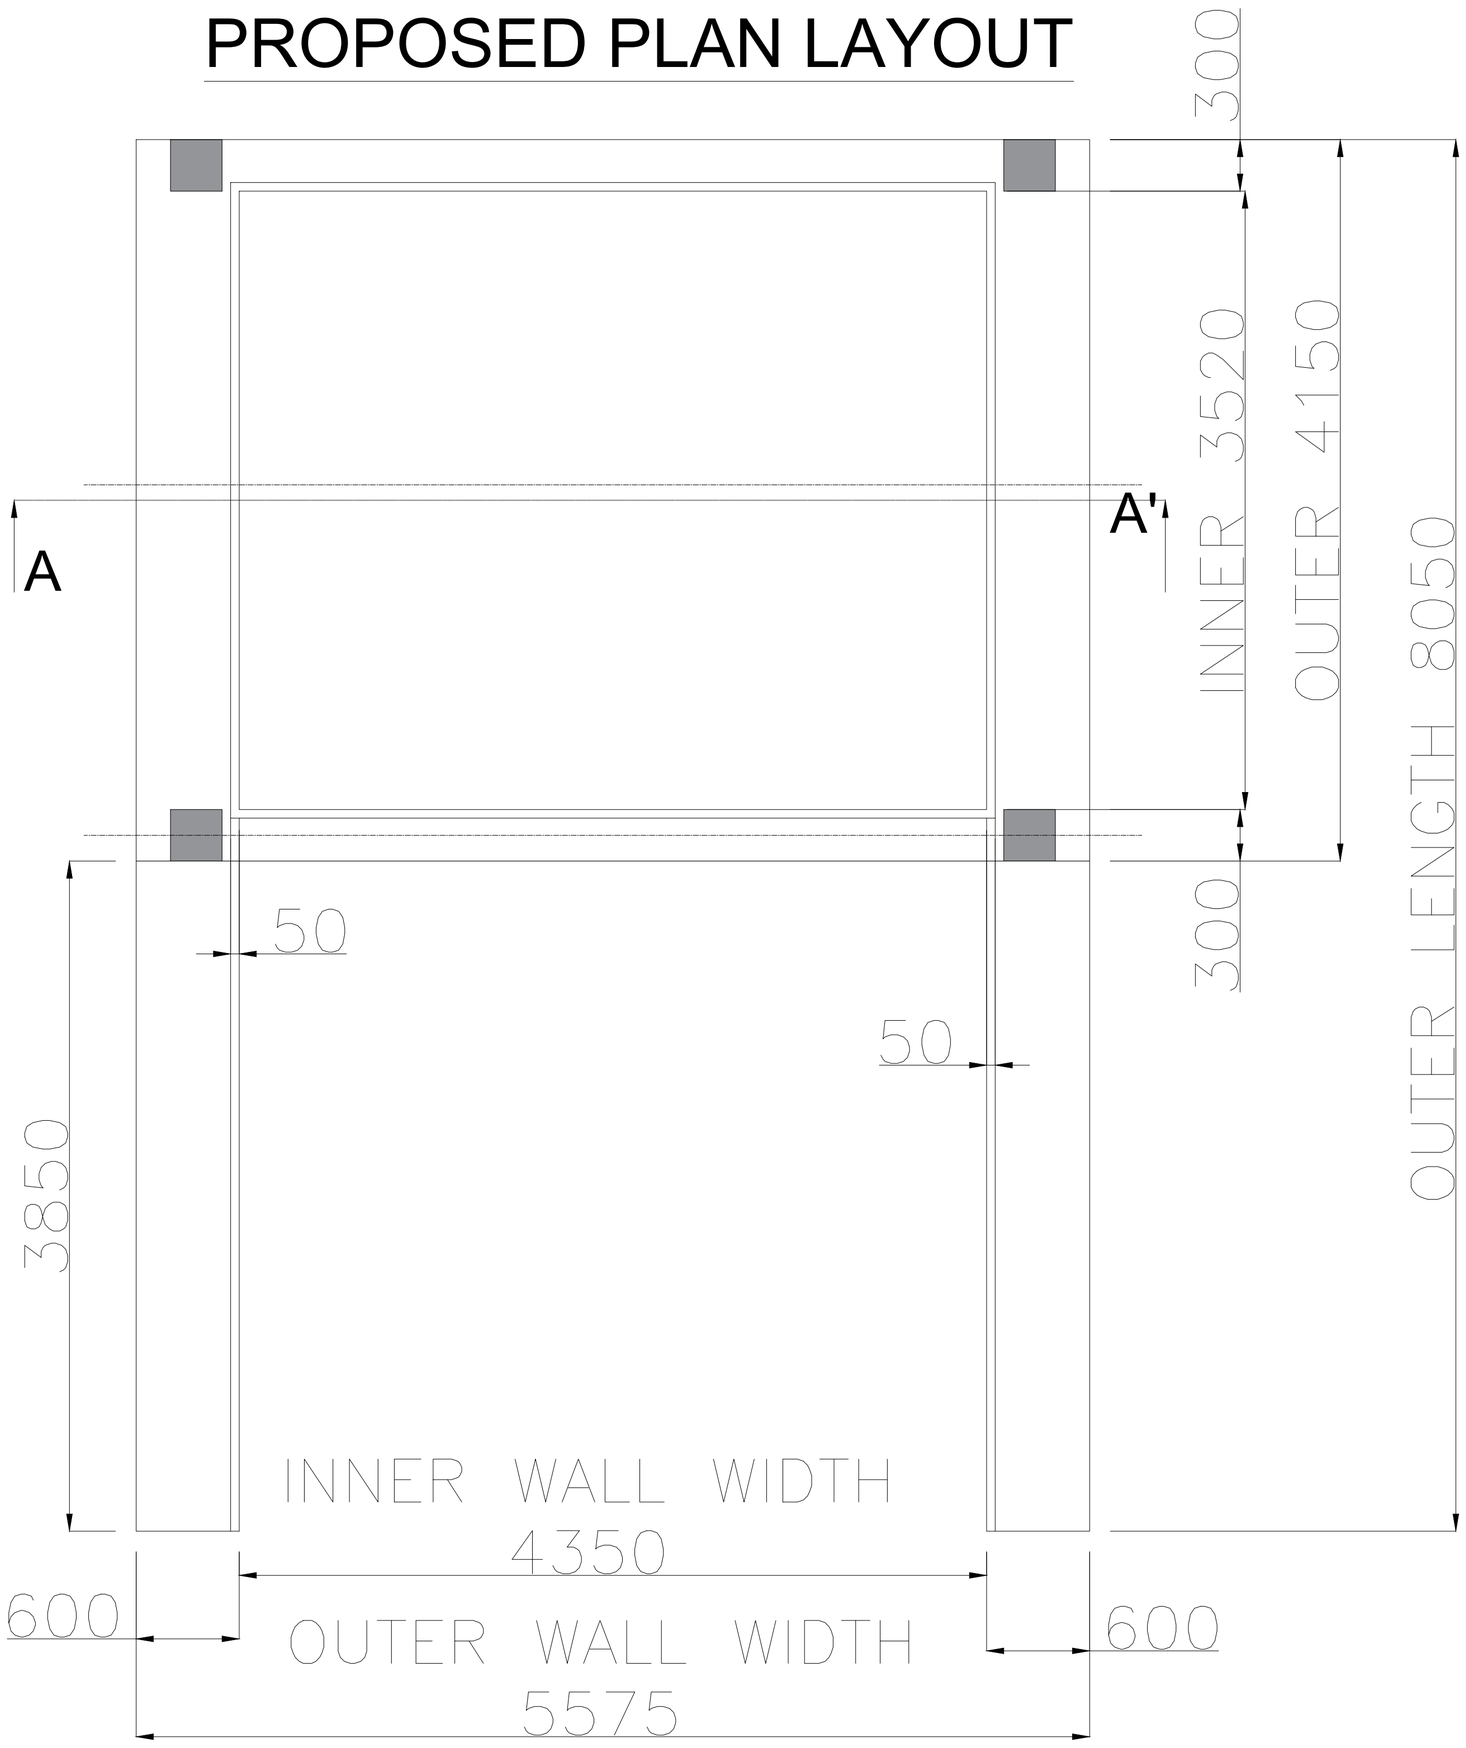

PROPOSED PLAN

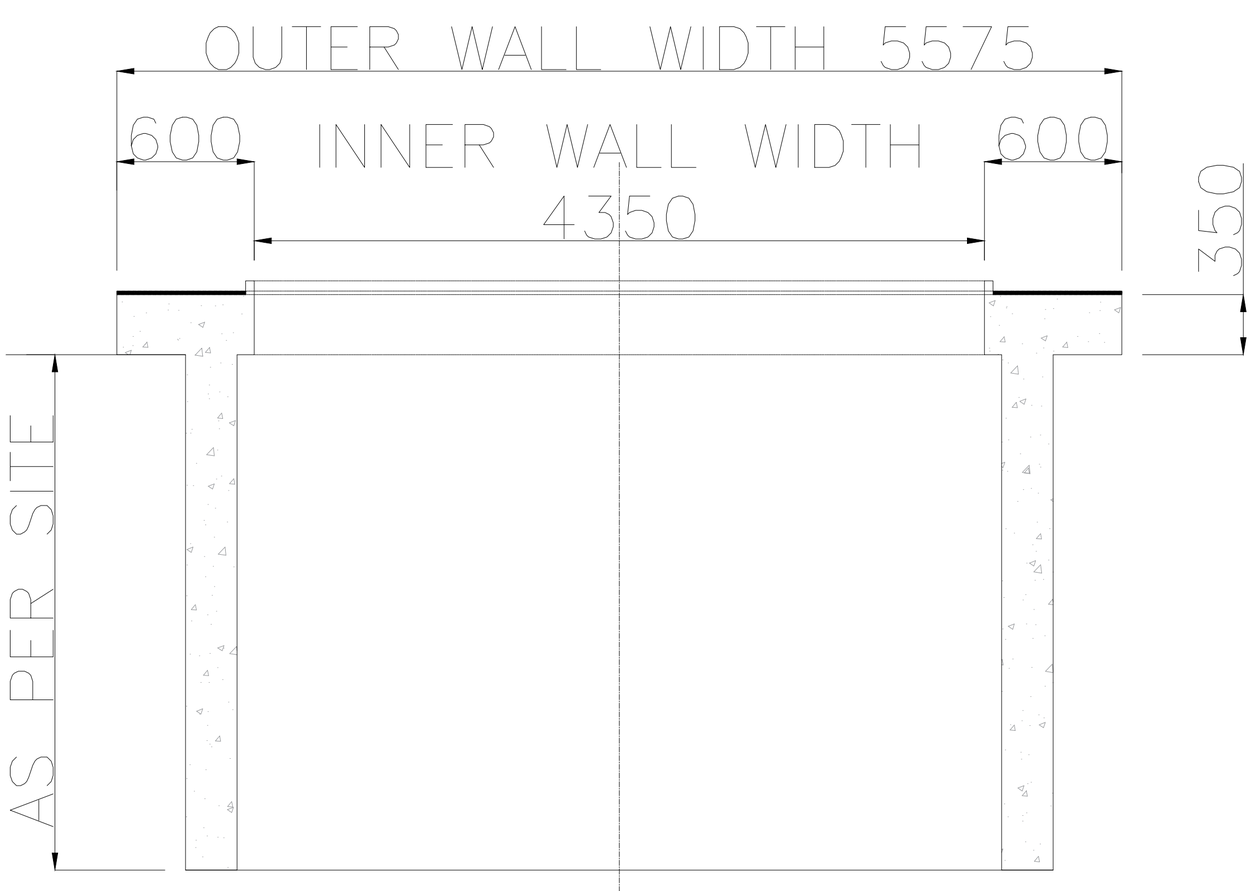

SECTION A-A'

1. THE STRUCTURE AROUND THE CUT OUT SHOULD BE OF CONCRETE FOR FOR PROPER FASTENING OF ROOF.
2. TOP SURFACE SHOULD BE OF GRANITE 20MM FOR SMOOTH FUNCTIONING OF ROOF.
3. ROOF EXTENSION IS SHOWN FOR ONLY REFERENCE. IT CAN BE MODIFIED AS PER THE WORK UNDERTAKEN.
4. GRADIENT OF 50MM NEED TO BE PROVIDED ALONG THE OUTER LENGTH TO AVOID WATER STAGNANCY IN GUIDE RAIL.
5. AL PROFILE - POWDER COATED
6. GASKET - EPDM
7. MOTOR - ITALIAN/GERMAN MAKE
8. ALL DIMENSION IN MM.
9. PROPOSED CIVIL PLAN LAYOUT (IN CLIENT SCOPE)

This drawing & design is the property of NIHVA TECHNOLOGIES. Not to be sold or copied to any other concern.

TITLE				
PROPOSED CIVIL PLAN LAYOUT 3600 X 4350 MM (IN CLIENT SCOPE)				NIHVA TECHNOLOGIES PVT. LTD.
	NAME	SIGN	DATE	
DRAWN	MAHESH S.		07.11.22	CLIENT - MEHTA HOUSE
CHECK	MAHESH S.		07.11.22	LOCATION - AHMEDABAD
APPRD.	VIJAY T.		07.11.22	PRODUCT - RETRACTABLE ROOF
If any queries contact : projectsautomation@nihva.com				NIHVA\22-23\02XX / REV- 0
ALL DIMENSION ARE IN mm				SCALE: NTS / SHEET: 01 OF 01