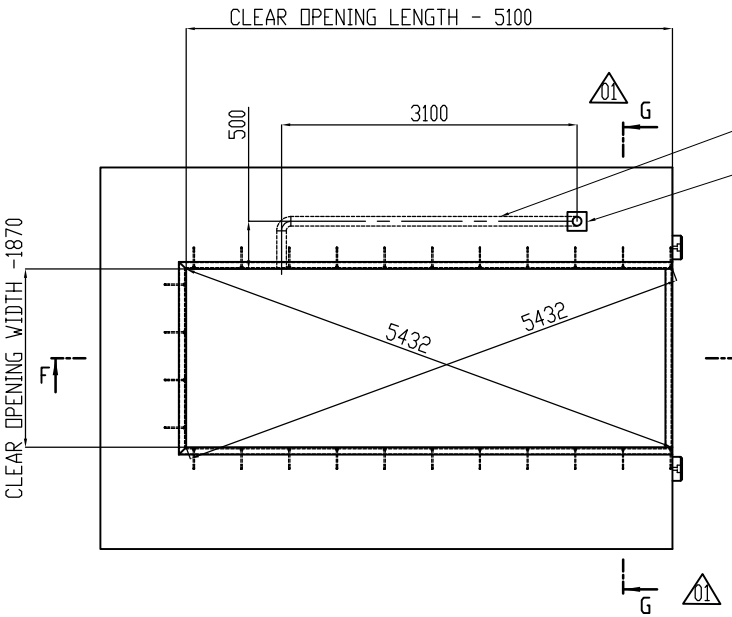
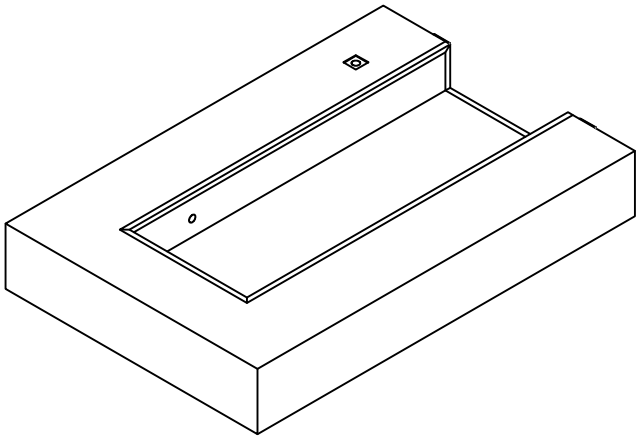
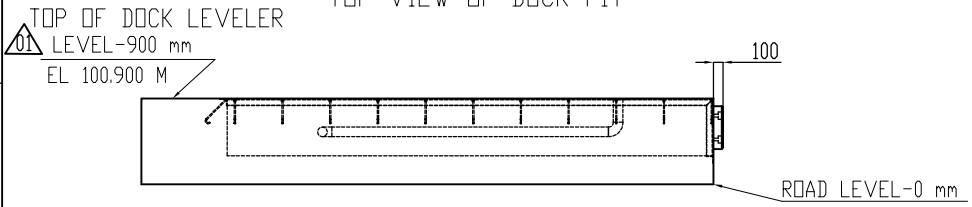




TOP VIEW OF DOCK PIT




ISOMETRIC VIEW OF DOCK LEVELER PIT



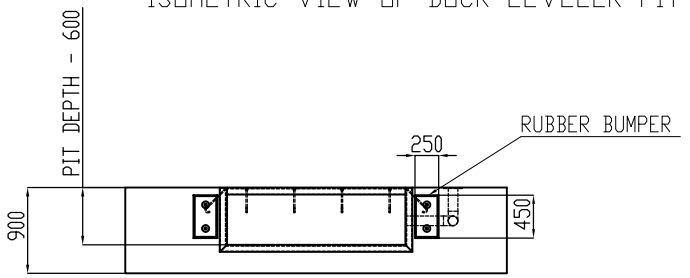

FRONT VIEW OF DOCK PIT





SIDE VIEW OF DOCK PIT

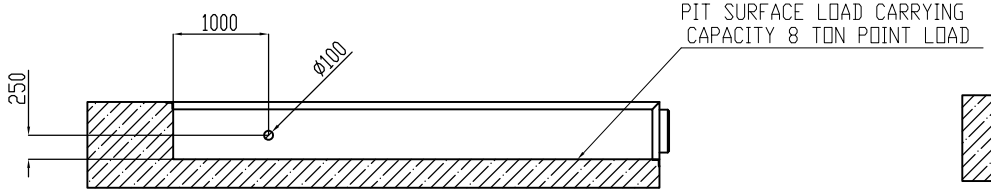


SECTION F-F
SCALE 1 : 28

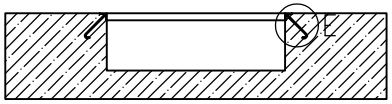

SECTION G-G 01
SCALE 1 : 28

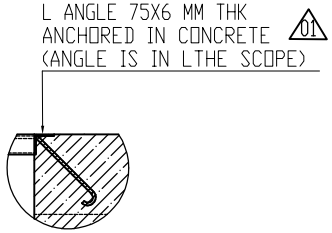


DETAIL E
SCALE 1 : 10

NOTES - 01

1. PIT & ALL CIVIL WORK IS IN LTHE SCOPE .
2. AT ALL EDGES OF PIT ANGLE 75X6 MM THK(ANGLE IN LTHE SCOPE ) TO BE ANCHORED IN CONCRETE .
3. PIT SURFACE SHOULD BE PLAIN & LOAD CARRYING CAPACITY FOR PIT SURFACE SHOULB OF 8 TON POINT LOAD .
4. MINIMUM 4 INCH DUCT TO BE PROVIDED FROM CONTROL PANEL TO PIT OPENING BY LTHE FOR ELECTRICAL CABLE ROUTING . REQUIRED DUCT IS IN LTHE SCOPE.
5. CONTROL PANEL IS PROVIDED WITH ELECTRICAL CABLE. CONTROL PANEL SHOULD BE LOCATED NEAR DOCK LEVELER FOR EASY VIEW OF LIP RESTING ON VEHICLE .

ALL RIGHTS RESERVED
THIS DOCUMENT AND ANY DATA AND INFORMATION ARE CONFIDENTIAL AND THE PROPERTY OF L&T HYDROCARBON ENGINEERING (LTHE) AND THE COPYRIGHT THEREIN IS VESTED IN LTHE. NO PART OF THIS DOCUMENT SHALL BE REPRODUCED, STORED IN A RETRIEVAL SYSTEM OR TRANSMITTED IN ANY FORM OR BY ANY MEANS, ELECTRONIC, MECHANICAL OR OTHERWISE, WITHOUT THE PRIOR WRITTEN PERMISSION OF LTHE. OR USED FOR ANY PURPOSE OTHER THAN THAT FOR WHICH IT IS SUPPLIED, WITHOUT THE PRIOR WRITTEN CONSENT OF LTHE.

| | | |
|---|---|---|
| 504-LZ-930A/B | GAD OF DOCK LEVELER 01 | 01 |
| DRAWING NO. | DRAWING TITLE | REV |

REFERENCE DOCUMENTS / DRAWINGS

DRG. CATEGORY: (USE TICK MARK) [R] [I]
EIL REVIEW/APPROVAL CODE:
VPTL NO.:
SCH. DATE OF SUBMISSION
DOCUMENT STATUS
STATEMENT OF SUB: [1st] [2nd] [3rd]
☐ FINAL FOR CODE-1 ☐ AS BUILT
ISSUED FOR
☐ AS BUILT ☐ CONSTRUCTION ☐ INFORMATION ☐ REVIEW
SIGN: DATE:

☐ REVIEW CODE 1 – NO COMMENTS PROCEED WITH MANUFACTURE / FABRICATION/ CONSTRUCTION AS PER THE DOCUMENT.
☐ REVIEW CODE 2 – PROCEED WITH MANUFACTURE / FABRICATION / CONSTRUCTION AS PER THE COMMENTED DOCUMENT. REVISED DOCUMENT REQUIRED.
☐ REVIEW CODE 3 – DOCUMENT DOES NOT CONFORM TO BASIC REQUIREMENTS AS MARKED. RESUBMIT FOR REVIEW.
☐ R – DOCUMENT IS RETAINED FOR RECORDS. PROCEED WITH MANUFACTURE / FABRICATION
☐ V-VOID

| | NAME | DISCIPLINE | SIGN. | DATE |
|---|---|---|---|---|
| | | | | |

| REV. | DESCRIPTION | DRN | CHECKED | APPROVED | REVIEWED | APPROVED | DATE |
|---|---|---|---|---|---|---|---|
| 01 | ISSUED FOR APPROVAL | SMS | VJ | AK | | | |

OWNER: HINDUSTAN PETROLEUM CORPORATION LIMITED
VISAKH REFINERY MODERNIZATION PROJECT
EPCC-03 PACKAGE FOR RESIDUE UP-GRADATION FACILITY (RUF)

PMC : ENGINEERS INDIA LIMITED (A Govt. of India Undertaking)

LSTK CONTRACTOR: L&T Hydrocarbon Engineering

DETAILED ENGINEERING CENTER: L&T - CHIYODA LIMITED

L&T - CHIYODA LIMITED

☐ REVIEW CODE 1 – NO COMMENTS PROCEED WITH MANUFACTURE / FABRICATION/ CONSTRUCTION AS PER THE DOCUMENT.
☐ REVIEW CODE 2 – PROCEED WITH MANUFACTURE/ FABRICATION /CONSTRUCTION AS PER THE COMMENTED DOCUMENT. REVISED DOCUMENT REQUIRED.
☐ REVIEW CODE 3 – DOCUMENT DOES NOT CONFORM TO BASIC REQUIREMENTS AS MARKED. RESUBMIT FOR REVIEW.
☐ R – DOCUMENT IS RETAINED FOR RECORDS. PROCEED WITH MANUFACTURE / FABRICATION
☐ V-VOID

| COMMENTED BY | REVIEWED BY | APPROVED BY | DATE |
|---|---|---|---|
| | | | |

THIS REVIEW / APPROVAL DOES NOT RELIEVE THE VENDOR / MANUFACTURER OF THE FULL RESPONSIBILITY AS TO DESIGN CORRECTNESS OF DIMENSIONS & COMPLIANCE WITHALL APPLICABLE REGULATIONS AND WITH THE REQUIREMENTS MADE IN PURCHASER SPECIFICATIONS.

VENDOR : NDVA TECHNOLOGIES PVT LTD
VENDOR PO NO: REFINERY/75000-82256/VMM
VENDOR DWG. NO: NDVA_20-21_0158

| DATE | SCALE |
|---|---|
| 29.3.21 | 1:6 |

DEPT: DESIGN
DRN BY: SMS
CHK BY: VJ
APP BY: AK

TITLE: CIVIL DRAWING FOR DOCK LEVELER (504-LZ-930A/B) 01
PROJECT: L&T-RUF
PWO NO.:
DRG. NO.: 3656-RUF-LT-504-HP-SV-NTPLCD-13605
SH. 4 OF 4
REV. 01

CAD FILE: