



DRAWING

REV DESCRIPTION	DATE	REV NO
1.	11-11-2025	REV 00

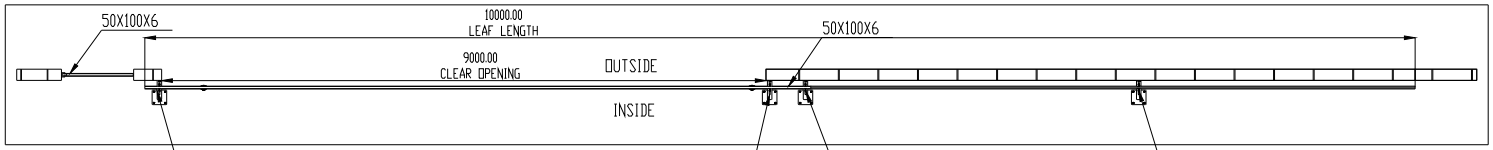


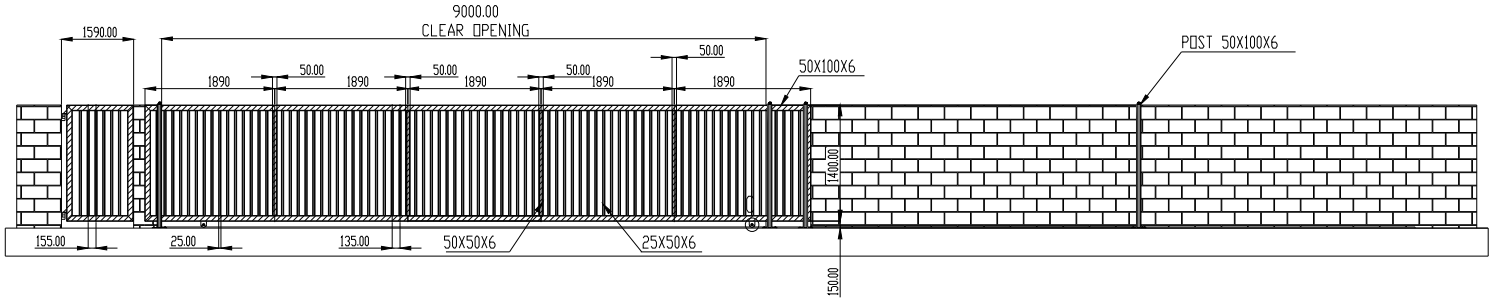

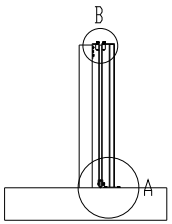


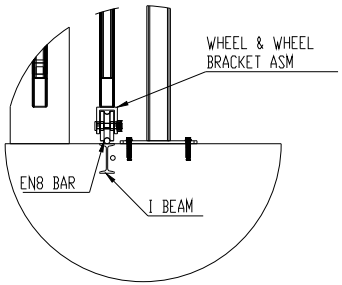

DETAIL A
SCALE 1 : 11

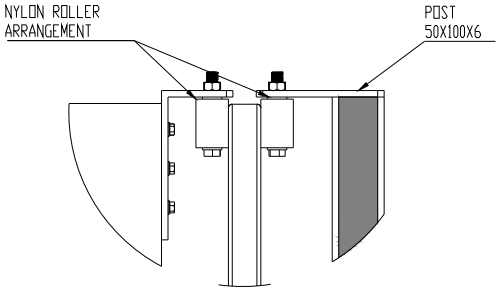

DETAIL B
SCALE 1 : 5

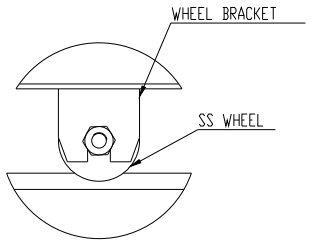

DETAIL C
SCALE 1 : 4

SS WHEEL ARRANGEMENT

NOTE :

SPECIAL INSTRUCTION'S :

TITLE - DOOR AUTOMATION

DWG NO - NTPL-000-PM

NIHVA TECHNOLOGIES PVT.LTD.PUNE
Website - www.nihva.com

	NAME	SIGNATURE	DATE
DRAWN	V.W.		11-11-2025
CHK'D	B.S.		12-11-2025
APPV'D	V.T.		12-11-2025

PRODUCT - SLINDING GATE
PROJECT NO - NTPL-000-PM
REVISION - 00
SITE LOCATION -
WEIGHT -
MATRIAL -
QTY - 1
If any queries contact - Design@nihva.com
ALL DIMENSION ARE IN mm
A2
PROJECTION METHOD
SCALE :
SHEET 1 OF 1