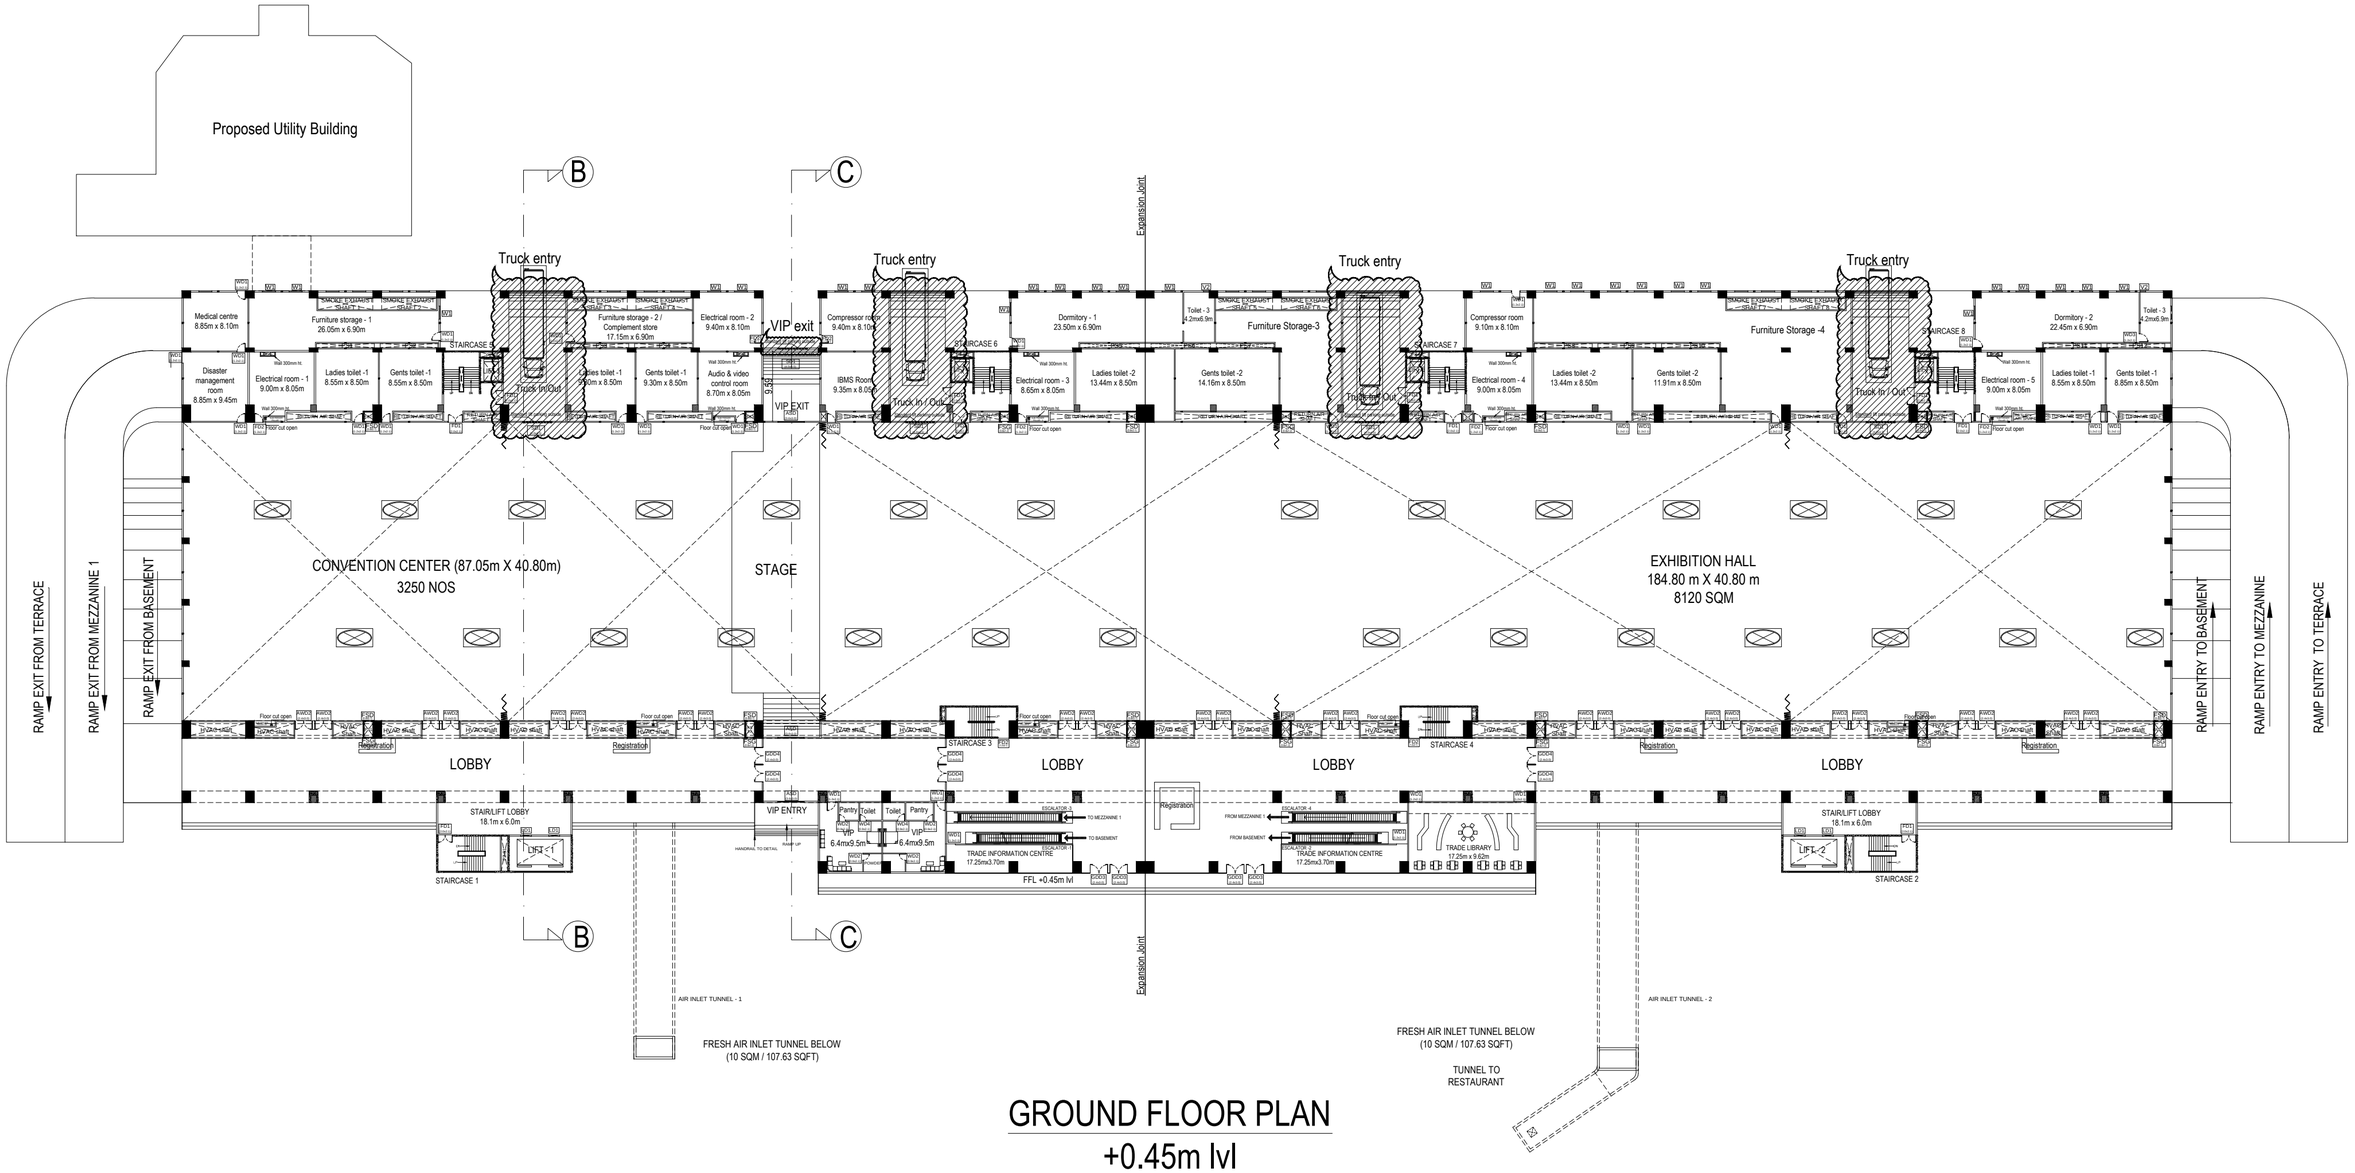



# GROUND FLOOR PLAN
## +0.45m lvl

| SCHEDULE OF JOINERY | | | | |
|---|---|---|---|---|
| Type | Description | Width | Height | NOs |
| SD1 | SECTIONAL DOOR | 4000 | 4500 | 5 |

PROPOSED EXPANSION PROJECT OF CHENNAI TRADE CENTRE CAMPUS , NANDAMBAKKAM, CHENNAI.

Note:

| | | |
|---|---|---|
| P.S | — | Plumbing shaft |
| F.S | — | Fire shaft |
| E.S | — | Electrical shaft |
| T.S | — | Telecommunication shaft |
| PZ.S | — | Pressurization shaft |

COPYRIGHT

THIS DRAWING IS A COPYRIGHT. IT IS NOT TO BE REPRODUCED, COPIED HANDED OVER TO A THIRD PARTY OR USED FOR ANY PURPOSE OTHER THAN FOR THE PROJECT INVOLED.WITHOUT THE KNOWLEDGE OF TAAMAESEK.

ARCHITECTS & ENGINEERS

Taamaesek Engineering Consortium

New no. 5, Old no.2a, Bishop Wallers Avenue west, Mylapore, Chennai - 600 004. Ph : 044-24671157/1139. Fax : 044-24672237.
url:www.taamaesek.com
e-mail: info@taamaesek.com