

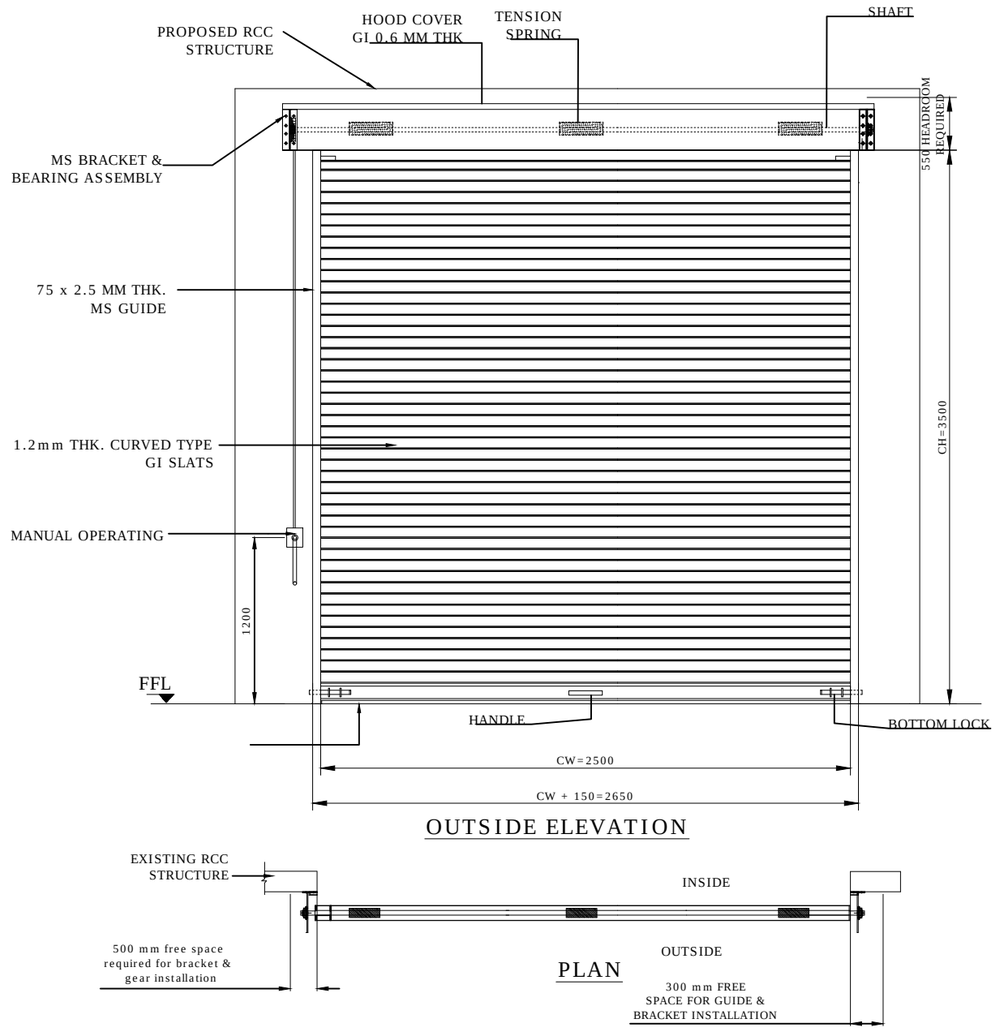


OUTSIDE ELEVATION


PLAN

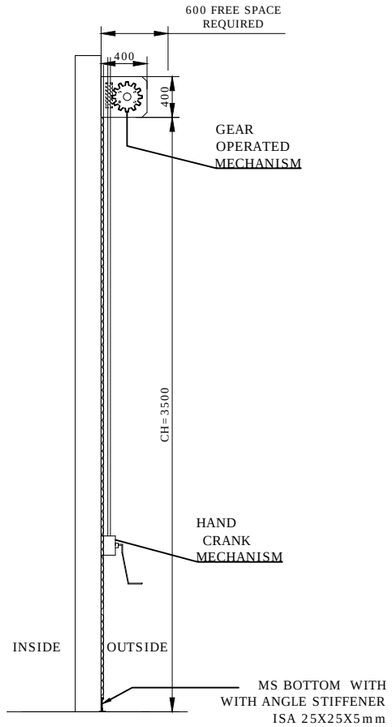

SIDE VIEW

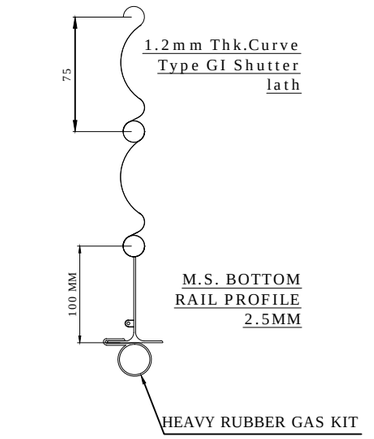

M.S. BOTTOM RAIL PROFILE 2.5MM

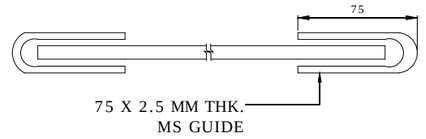

RAL CODE	RAL COLOR	APPROVAL
RAL 7040	WINDOW GREY	APPROVED

SR NO	(CW) CLEAR WIDTH	(CH) CLEAR HEIGHT	QUANTITY
1	2500	3500	01 NO

TOLERANCE - ±10mm

NOTE-
1. ALL DIMENSIONS ARE IN MM.
2. SURFACE FINISH: POWDER COATING OF APPROVED RAL CODE.
3. MOUNTING ON OUTSIDE CONCRETE STRUCTURE.
4. MOUNTING OF LEVER WILL BE ON LEFT SIDE.

This drawing & design is the property of NIHVA TECHNOLOGIES. Not to be sold or copied to any other concern.

TITLE: GEAR OPERATED ROLLING SHUTTER

	NAME	SIGN	DATE
DRAWN	G.I.P		23.02.2022
CHECK	A.K.		23.02.2022
APPRD.	V.T.		23.02.2022

NIHVA TECHNOLOGIES PVT. LTD.
NIHVA TECHNOLOGIES PVT. PUNE
Tel : 020 66304033
Website:- www.nihva.com
Email:- info@nihva.com
If any queries contact : design@nihva.com

CLIENT -

PROJECT -GEAR OPERATED ROLLING SHUTTER

SITE LOCATION -

DWG. NO. : NIHVA/21-22/VDR/032 | REV- R0

ALL DIMENSION ARE IN mm | SCALE: NTS | WT: | SHEET: 01 OF 01