




SLIDING ROLLER DETAIL 'A'

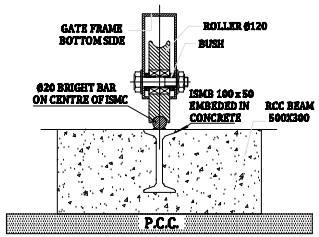


SLIDING ROLLER DETAIL 'A'

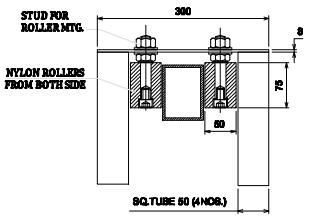


SLIDING BRACKET DETAIL 'B'

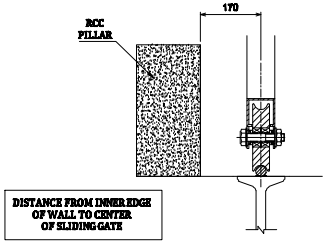


DETAIL 'C'

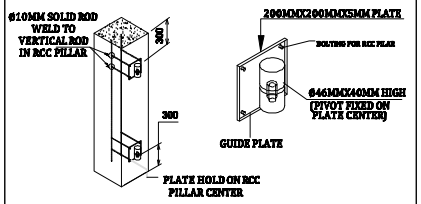


PIVOT FIXING DETAIL FOR WICKET GATE DETAIL 'F'

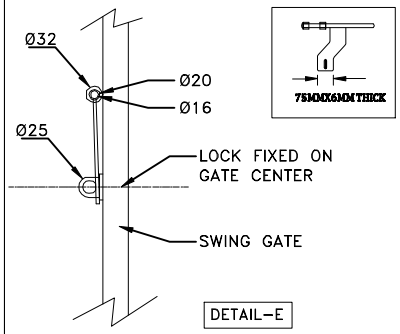


DETAIL–E

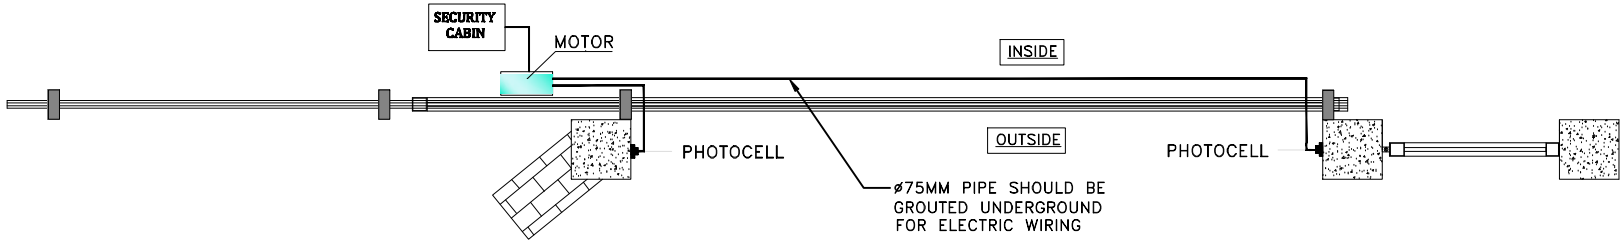

SLIDING GATE WIRING

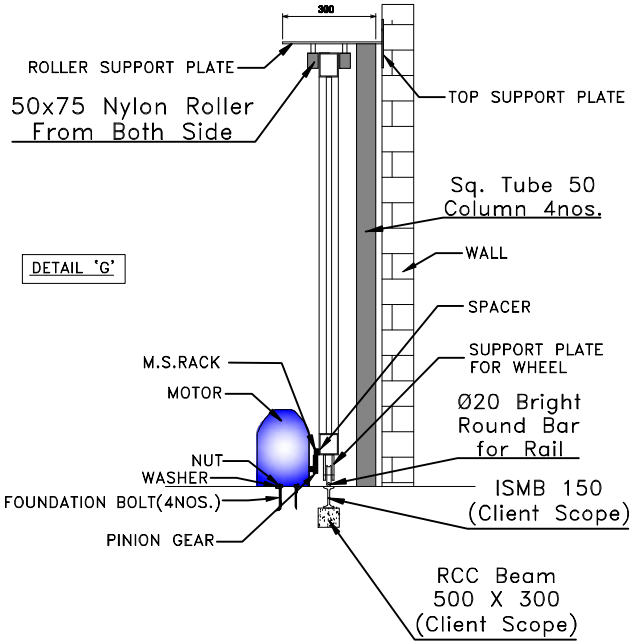

DETAIL 'G'

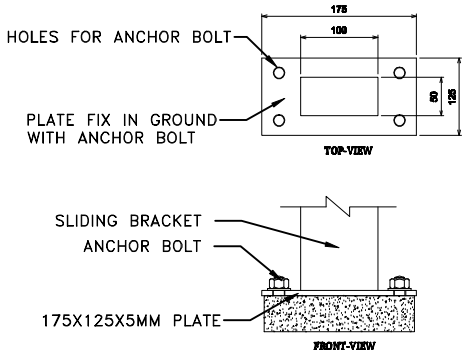

CLEAR OPENING	9,000 (W) X 1800 (H)
SLIDING GATE SIZE	10500 (W) X 1800 (H), QTY = 1NOS.
WICKET GATE SIZE	1800(W) X 1800 (H), QTY = 1NOS.
OUTER FRAME	100 X 50 X 3 mm
INNER FRAME	25 X 25 X 2.5 mm
GAP B/W FRAME	100 c/c
C'COLUMN(V) SUPPORT	4 NOS.
TOTAL WEIGHT	625 kg (APPORX)
MOTOR POWER	240 W
DEG. OF PROTECTION	IP 24

This drawing & designing is the property of NIHVA TECHNOLOGIES. Not be sold or copy to any other concern.

TITLE

SLIDING GATE

CLIENT APPROVAL

ALL DIMENSION ARE IN mm

	SIGN	DATE
DRAWN	ABHIJIT	28/01/15
CHECK	ANIL	28/01/15
REV.	07	
APPRD.		
MFG		
Ref. No.		

NIHVA TECHNOLOGIES PVT. LTD.

NIHVA TECHNOLOGY PVT. LTD. PUNE
Tel : 020 66304033
Email:- info@nihva.com
Website:- www.nihva.com

CLIENT - REWARD CONSTRUCTION

PROJECT -INGRERSOLL RAND

SITE -NARODA , GUJRAT

DWG. NO. - NVA/REWARD/D1/R3

SCALE: 01 | WT: | SHEET: 02 OF 02

If any queries contact : projects@nihva.com