




ELEVATION

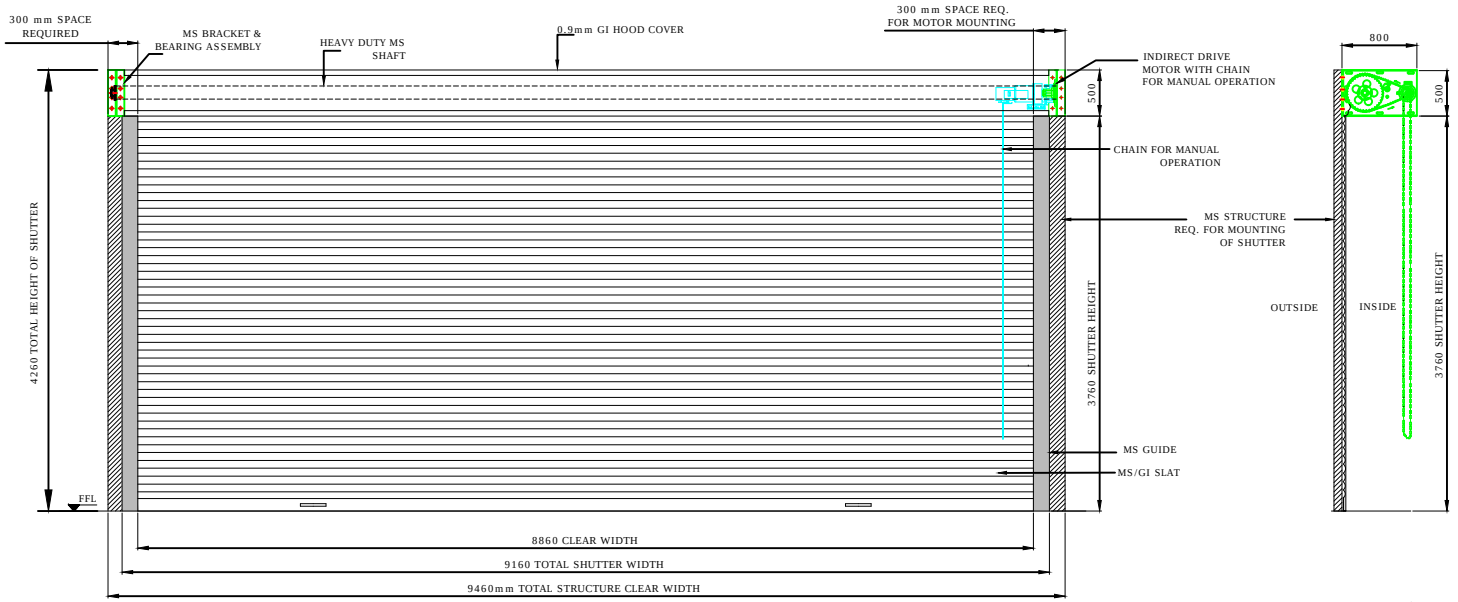

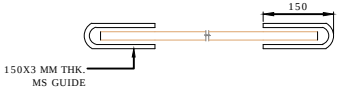


PLAN

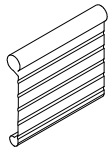


SLAT PROFILE

1.2mm Thick
MS/GI FLAT TYPE
Shutter Slat PROFILE

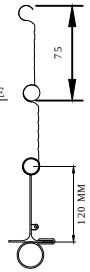


OPTION NO:-02

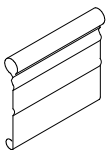

SLAT PROFILE

1.2mm Thick
MS/GI FLAT TYPE
Shutter Slat PROFILE

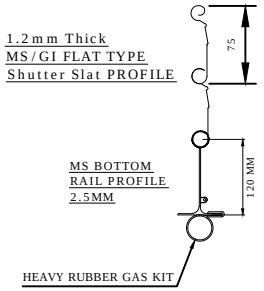

OPTION NO:-01

NOTE:- CLIENT HAS TO CHOOSE THE SLAT PROFILE OUT OF OPTION 1 & OPTION 2.

R01:-SIZE CHANGED

DIMENSION :

CLEAR WIDTH	CLEAR HEIGHT	QUANTITY
8860	3760	1

MATERIAL :

THICKNESS :

NOTE-
1.ONE COAT OF RED OXIDE WILL BE GIVEN TO SHUTTER (ONLY MS PART). PAINT OF APPROVED RAL SHADE WILL BE GIVEN TO THE SHUTTER.
2. HOOD COVER WILL BE IN GI.
3.THREE PHASE SUPPLY SHOULD BE GIVEN TO THE SHUTTER.
4.ALL CIVIL WORK WILL BE IN CLIENT'S SCOPE.

NIHVA TECHNOLOGIES PVT. LTD. PUNE
Email:- info@nihva.com
Website:- www.nihva.com

TITLE:

MOTORIZED ROLLING SHUTTER

CLIENT'S APPROVAL :

CLIENT - JLL

PROJECT - INORBIT MALL

SITE LOCATION - WADGAONSHERI,PUNE

DWG. NO. :NIHVA/17-18/0144/R01

SCALE: NTS	WT:	SHEET:1 OF 1

DRAWN BY: SURAJ	DATE: 31-08-2017
CHECK : SHEKHAR	DATE: 31-08-2017
APPROVED : SHEKHAR	DATE:31-08-2017

If any queries contact : projects@nihva.com

NOTE: ALL DIMENSIONS ARE IN mm

THIS DRAWING & DESIGN IS THE PROPERTY OF NIHVA TECHNOLOGIES. NOT TO BE SOLD OR COPY TO ANY OTHER CONCERN.