




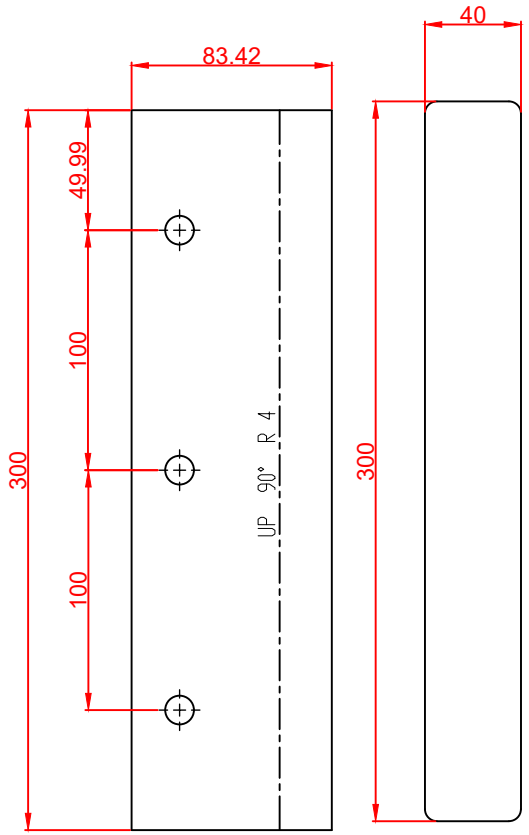

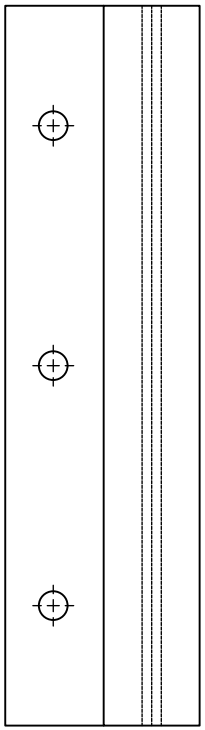

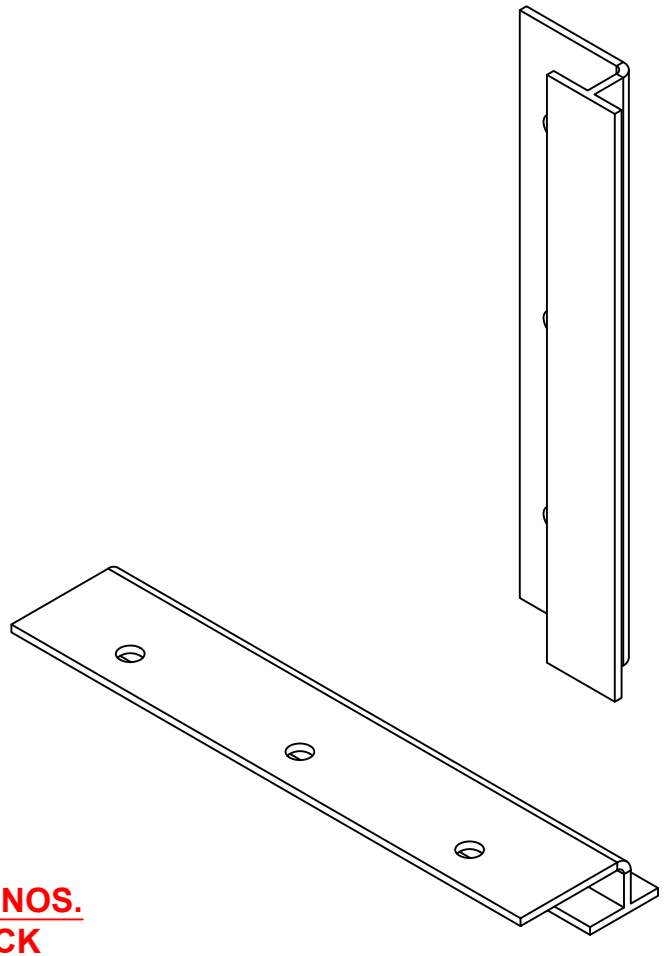

QTY. - 40 NOS.
INTERLOCK
BRACKET - T TYPE
MTRL - MS

This drawing & design is the property of NIHVA TECHNOLOGIES. Not to be sold or copied to any other concern.

TITLE:- 3 LEAF CRM DOOR 04			NIHVA TECHNOLOGIES PVT. LTD. PUNE Tel : 020 66304033 Email:- info@nihva.com Website:- www.nihva.com
	NAME	DATE	SIGN
DRAWN	M.SUTAR	03/05/2022	
CHECK	M.SUTAR	03/05/2022	
APPRD.			
CLIENT - NIHVA TECHNOLOGIES PVT.LTD			
LOCATION -			
PRODUCT - SLIDING DOOR			
If any queries contact : design@nihva.com	DWG NO:-NIHVA/22-23/VDR/0016		REV- 0
ALL DIMENSION ARE IN mm	SCALE: NTS	SCALE:-- 1:1	SHEET: 01 OF 01

	Date	Revised By

