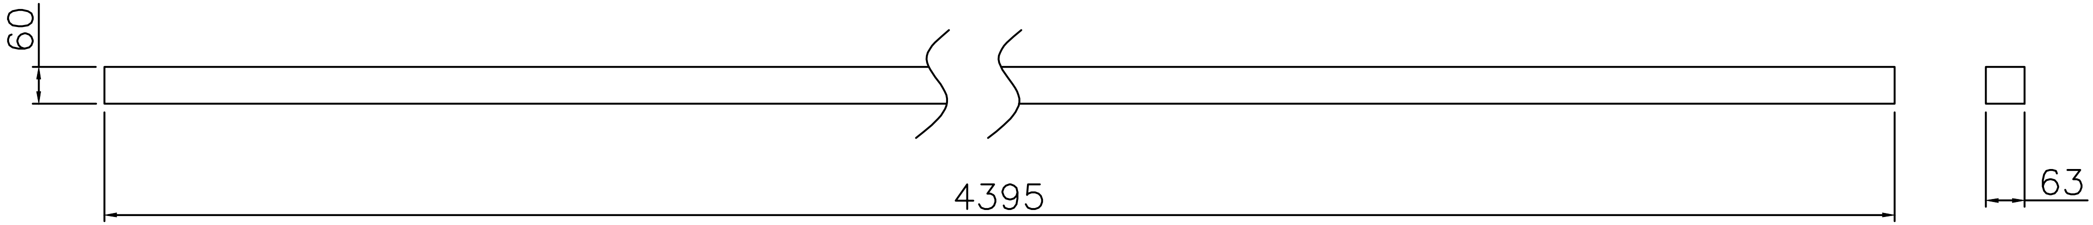

⑧ ENDCLOSER BOTTOM STRAIGHT PROFILE GNT- 6

QTY - 2 NOS

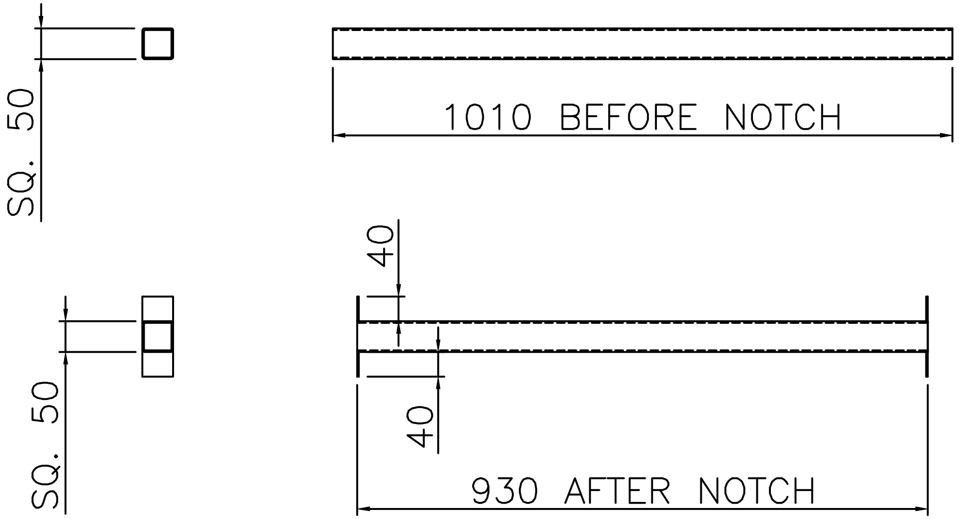

⑨ MIDDLE SUPPORT TUBE

QTY - 20 NOS

REV.	DESCRIPTION.	REVISED BY	SIGN	DATE
000	RELEASED DWG FOR MANUFACTURING	N.K.		25.02.23
001	NOTCH SIZE ADDED TO 50x50x2.6 THK SQ. TUBE	N.K.		27.02.23

This drawing & design is the property of NIHVA TECHNOLOGIES. Not to be sold or copied to any other concern.

TITLE
ENDCLOSER BOTTOM PROFILE
AND MIDDLE SUPPORT TUBE

NIHVA
NIHVA TECHNOLOGIES PVT. LTD.

	NAME	SIGN	DATE	
DRAWN	N.K.		25.02.23	CLIENT - MEHTA HOUSE - 1
CHECK	P.M.		25.02.23	LOCATION -
APPRD.	V.T.		25.02.23	PRODUCT - RETRACTABLE ROOF

If any queries contact : projectsautomation@nihva.com	NIHVA\22-23\02XX		REV- 0
ALL DIMENSION ARE IN mm	SCALE: NTS		SHEET: 01 OF 01