




INSIDE ELEVATION

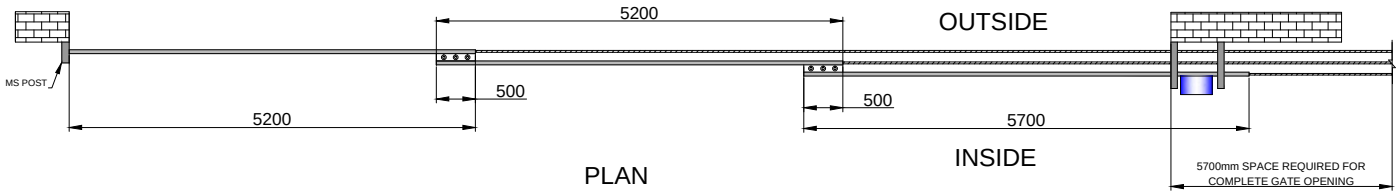

PLAN

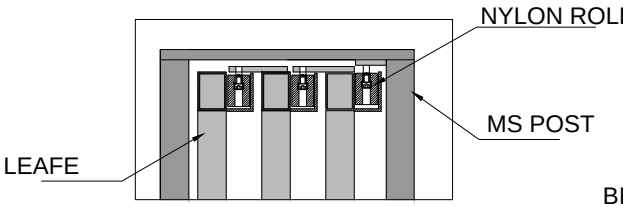

DETAILED VIEW OF 'B'

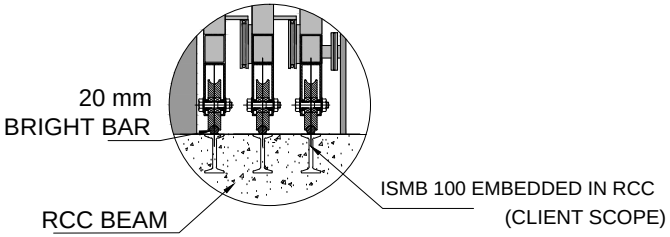

DETAILED VIEW OF 'A'

SR NO	TUBE SPECIFICATION	
1	100X50X3mm	OUTER FRAME
2	50X25X2.5mm	INNER PATTERN
3	90X50X3mm	INNER PATTERN
4	100X50X3mm	INNER PATTERN
5	50X50X2mm	INNER PATTERN
6	100X50X3mm	FOR MS POST

CLEAR WIDTH	CLEAR HEIGHT	QUANTITY
14000mm	2000mm	1 NOS

TOLERANCE- ±10mm

DIMENSION :

CLEAR WIDTH	CLEAR HEIGHT	QUANTITY
14000mm	2000mm	1 NOS

MATERIAL:

THICKNESS :

NOTE-
1. ALL REQUIRED CIVIL WORK WILL BE IN CLIENTS SCOPE.
2. ONE COAT OF RED OXIDE SHADE WILL BE GIVEN TO THE GATE.

NIHVA TECHNOLOGIES PVT. LTD.

NIHVA TECHNOLOGIES PVT. PUNE
Email:- info@nihva.com
Website:- www.nihva.com

TITLE:

3 LEAF TELESCOPIC (MOTORIZED)

CLIENT'S APPROVAL :

CLIENT - INDO COOL COMPOSITES PVT. LTD
PROJECT - LANDTECH ENGINEERS PVT. LTD
SITE LOCATION - CHENNAI
DWG. NO. : NIHVA/17-18/0150

SCALE: NTS	WT:	SHEET:1 OF 1
DRAWN BY: SURAJ		DATE: 10-08-2017
CHECK BY : SAGAR P		DATE: 10-08-2017
APPROVED BY : SHEKHAR		DATE: 10-08-2017

If any queries contact : projects@nihva.com

NOTE: ALL DIMENSIONS ARE IN mm

THIS DRAWING & DESIGN IS THE PROPERTY OF NIHVA TECHNOLOGIES. NOT TO BE SOLD OR COPIED TO ANY OTHER CONCERN.