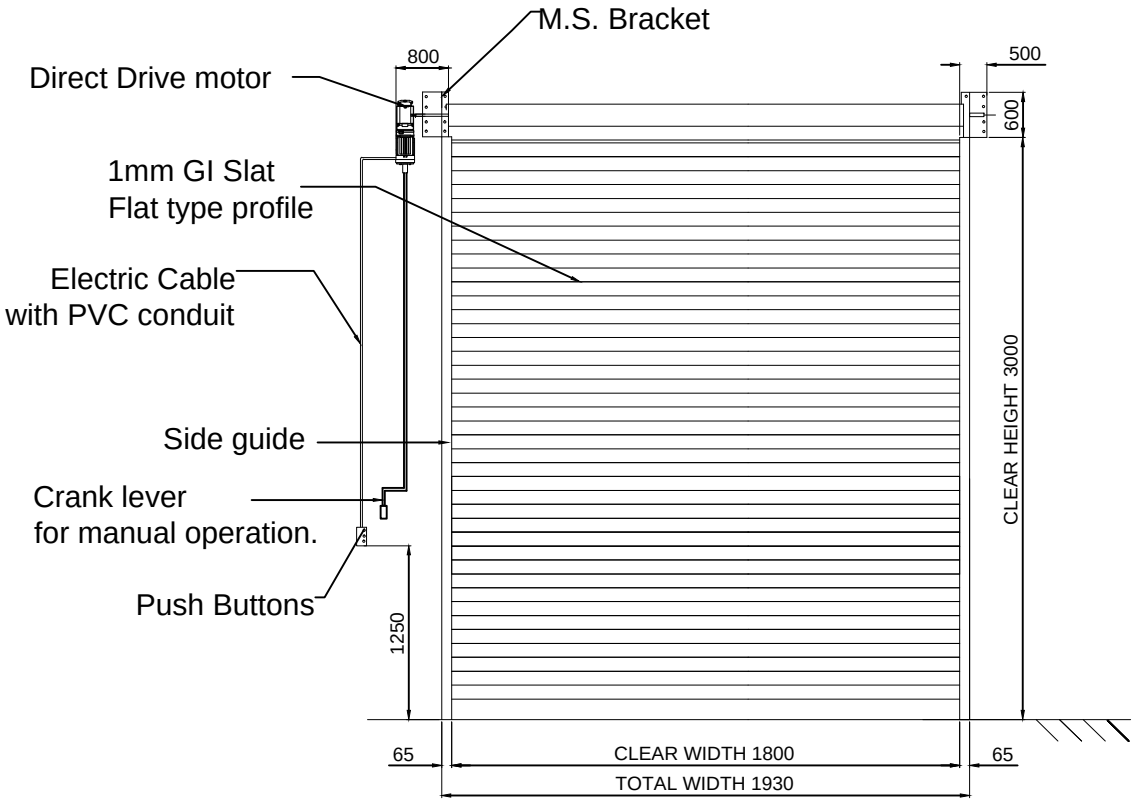

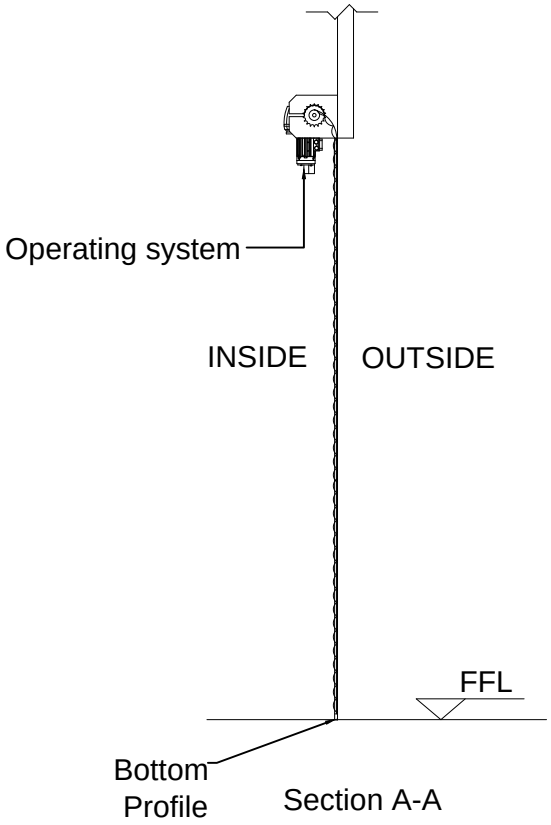

Section A-A

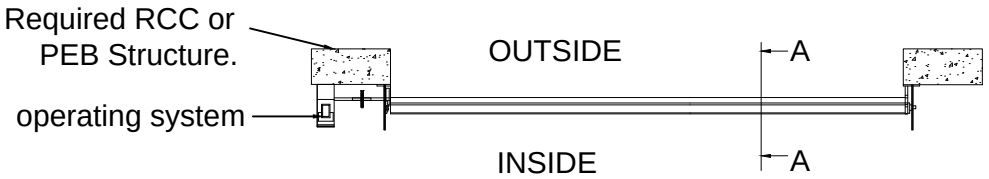

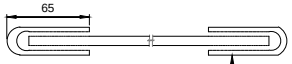

65x 2.5 mm THK
MS GUIDE

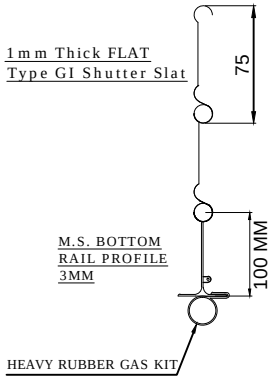

(NOTE: REQUIRED STRUCTURE FOR SHUTTER WILL BE IN CLIENT SCOPE.)

DIMENSION :		
CLEAR WIDTH	CLEAR HEIGHT	QUANTITY
1800 mm	3000 mm	02 NOS.

MATERIAL :

THICKNESS :

CLIENT'S COMMENTS :

NIHVA TECHNOLOGIES PVT. LTD.

NIHVA TECHNOLOGY
PVT. LTD. PUNE
Email:- info@nihva.com
Website:- www.nihva.com

TITLE:

MOTORIZED ROLLING SHUTTER

CLIENT'S APPROVAL :

CLIENT -SCHREIBER DYNAMIX DAIRIES PVT.LTD

PROJECT -

SITE LOCATION - BARAMATI

DWG. NO. : NIHVA/16-17/0049/R01

SCALE: NTS	WT:	SHEET:1 OF 1
DRAWN BY: OMKAR		DATE: 05-08-2016
CHECK : ANIL		DATE: 05-08-2016

If any queries contact : projects@nihva.com

NOTE: ALL DIMENSION ARE IN mm

THIS DRAWING & DESIGNING IS THE PROPERTY OF NIHVA TECHNOLOGIES. NOT BE SOLD OR COPY TO ANY OTHER CONCERN.