

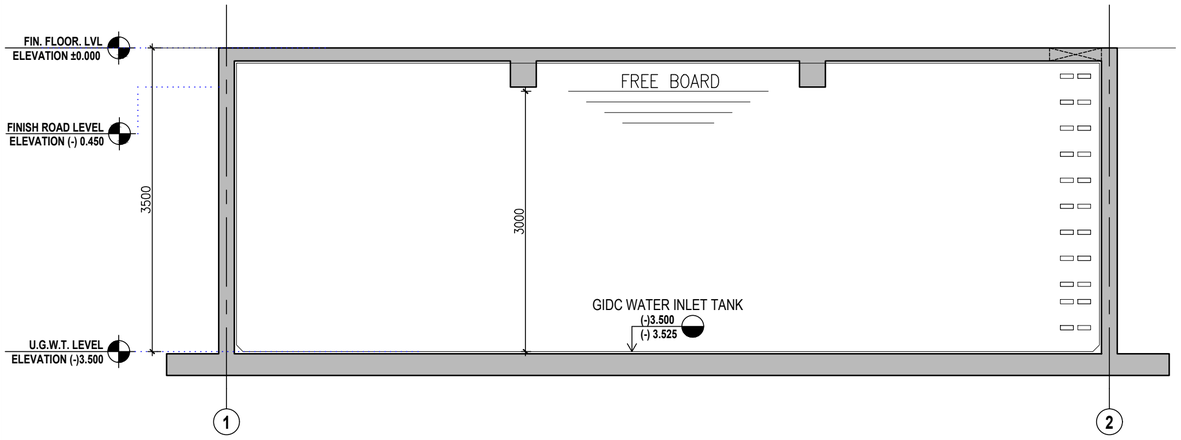


02 SECTION
SCALE 1:50

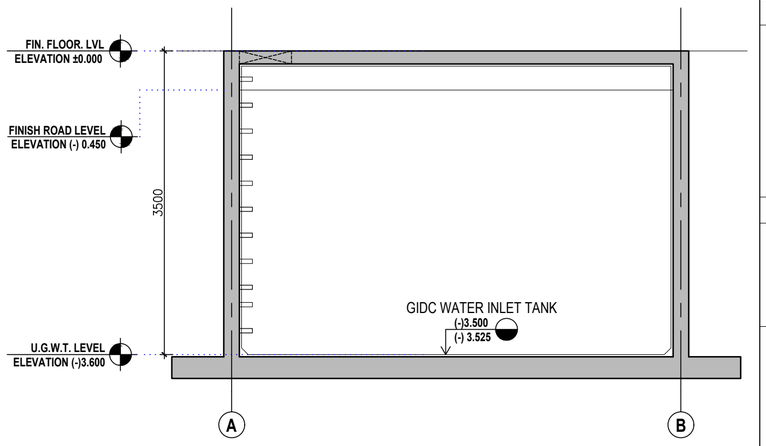

03 SECTION
SCALE 1:50

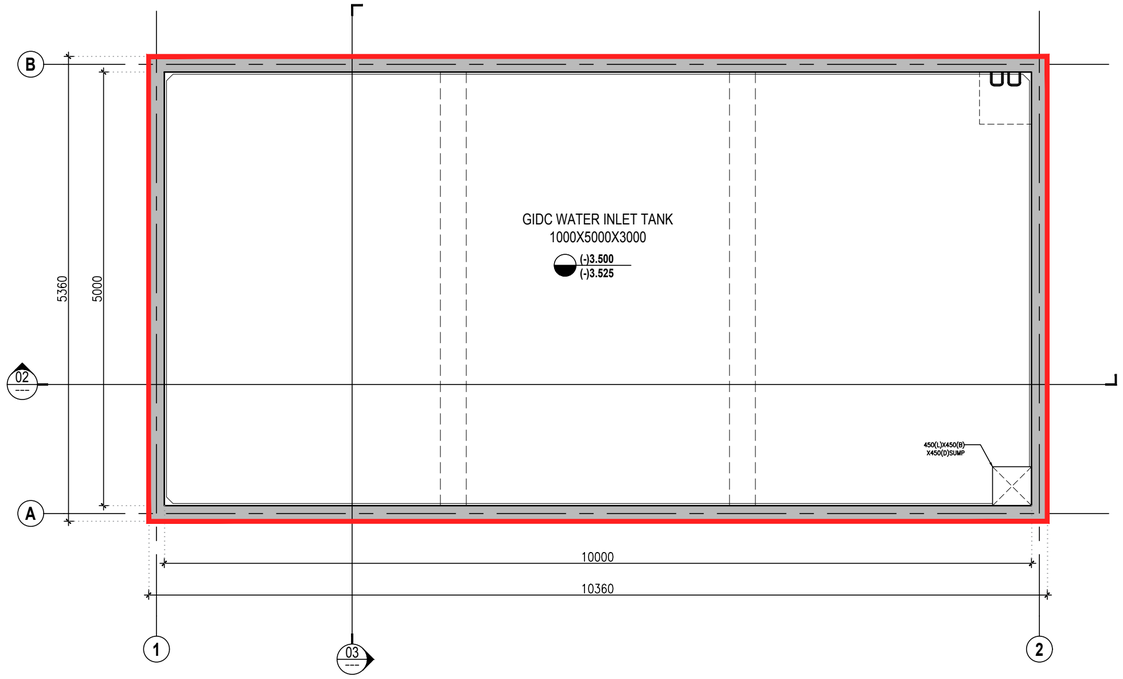

01 TANK LVL PLAN
SCALE 1:50

THIS DRAWING & DESIGN IS THE SOLE PROPERTY OF VMS & SHALL NOT BE COPIED, TRACED OR REPRODUCED BY ANY MEANS WITHOUT PRIOR WRITTEN CONSENT OF THE FIRM.

GENERAL NOTES :

1. ALL THE DIMENSIONS ARE UNFINISHED DIMENSIONS.
2. ALL DIMENSIONS ARE IN MM AND LEVELS ARE IN MT, UNLESS OTHERWISE MENTIONED.
3. ALL THE DIMENSIONS SHALL BE READ & NOT TO BE MEASURED.
4. IN CASE OF ANY DISCREPANCY, BRING IT TO THE NOTICE OF THE ARCHITECT IMMEDIATELY.
5. DETAIL DRAWING PRECEDES THE GENERAL DRAWING

STANDARD DRAWING SYMBOLS:

+ FINISHED LEVEL
+ UNFINISHED LEVEL

SECTION SYMBOL
UPPER HALF INDICATES DIAGRAM NO.
(NUMERICAL VALUE) IN DRAWING SHEET &
LOWER HALF INDICATES DRAWING NO.

ELEVATION SYMBOL
UPPER HALF INDICATES DIAGRAM NO. IN DRAWING
SHEET & LOWER HALF INDICATES DRAWING NO.

GRAPHIC LEGEND :

MASONRY CUT IN PLAN/SECTION.


RCC COLUMN CUT IN PLAN.

FOR TENDER

NO.	DATE	DESCRIPTION	DRN BY	CHK BY
R0	-	-	-	-

REVISION HISTORY

KEY PLAN
SCALE : N.T.S.

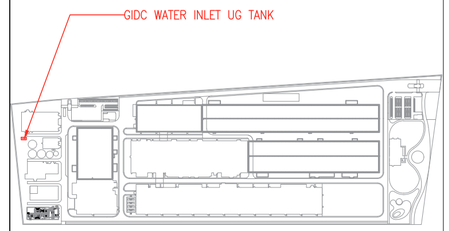

REFERENCE DRAWINGS :

01. ARCHITECTURAL :	-
02. STRUCTURAL :	-
03. HVAC :	-
04. ELECTRICAL :	-
05. UTILITIES :	-

PLAN & SECTIONS

GIDC WATER INLET UG TANK

AGRAWAL METAL WORKS(P) LTD.

PROJECT NO.	SCALE :	DRAWN :	BHAKTI B.
3824	AS SHOWN	CHECKED:	BHAKTI B.
	DATE : 03-12-2024	APPROVED :	DARSH D.
		CO. CHECKED:	DARSH D.

VMS ENGINEERING & DESIGN SERVICES (P) LTD.
CHITRAKOOT FLATS, B/H TIMES OF INDIA, OFF ASHRAM ROAD,
AHMEDABAD-380 009. PHONE: +91 (079) 2658-8829, 4023-6236
WWW.VMSCONSULTANTS.COM

SHEET SIZE	DRAWING NO.	TENDER	REVISION:
A2	T.A.10a.101	T	R0