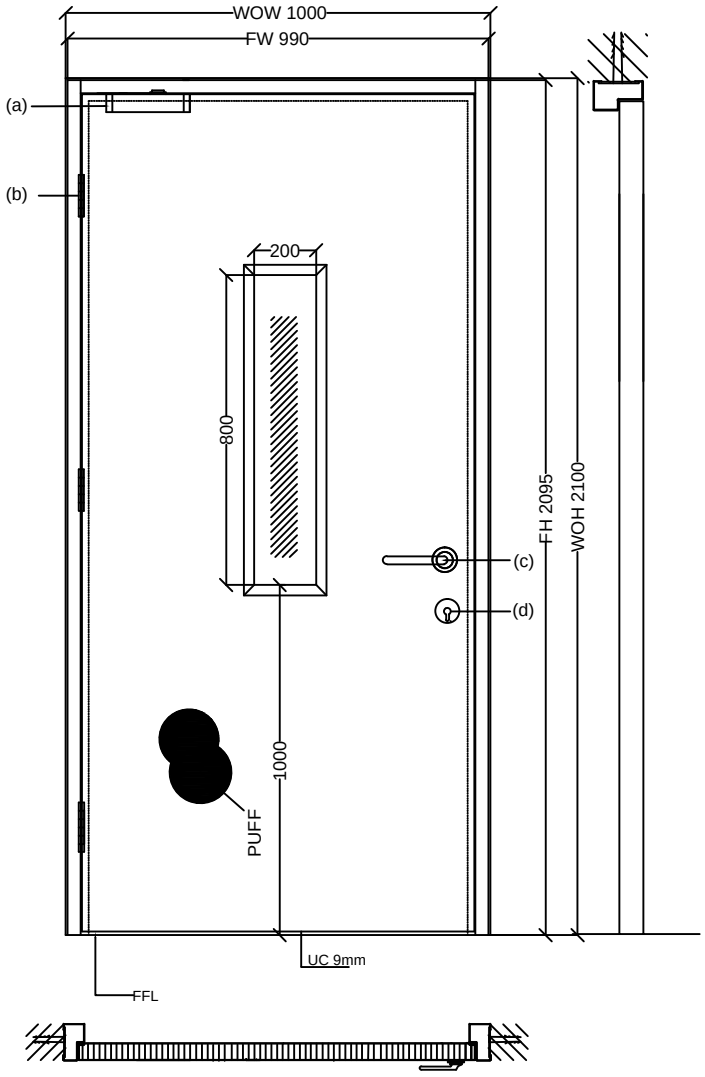


Abbrevation's:
WOW-Wall Opening Width
FW-Frame Width
WOH-Wall Opening Height
FH-Frame Height
UC-Under Cut
FFL-Finished Floor Level

ITEM	HARDWARE	ITEM DESCRIPTION
a	DOOR CLOSER	Door Closer B4 W Std Arm.
b	HINGES	SS Ball Bearing Butt Hinges(100X75X3mm)
c	HANDLE	SS Lever Handle
d	LOCK	Mortice Sash Lock With Both Side Key Operation

SHUTTER & FRAME & FIXING DETAILS

SHUTTER THICKNESS	47mm	Color	paint
SHUTTER SHEET THICKNESS	0.8mm		
FRAME SHEET THICKNESS	1.2mm	Quantity	2 NO's
MATERIAL	GI		
FIXING ON	Solid Brick Plastered Wall		

NOTE:- All Dimensions are in mm.
The Drawing Is For Location of Hardware only.
Drawing Does Not Represent The Actual Hardware.
For More Clarity,Please Go Through Hardware Brochure.

TOLERANCE : All Linear Dimensions ±3 mm,Others ±1mm

DOOR TYPE	WOW	WOH	RO=TYPE 3	RI=TYPE 1	LO=TYPE 4	LI=TYPE2	TOTAL
STEEL DOOR	1000	2100					2

COLOR - LIGHT GREY (RAL 7035)

This drawing & designing is the property of NIHVA TECHNOLOGIES. Not be sold or copy to any other concern.

TITLE
SINGLE LEAF STEEL DOOR

NIHVA TECHNOLOGIES PVT. LTD.
NIHVA TECHNOLOGY PVT. LTD. PUNE
Tel : 020 66304033
Email:- info@nihva.com
Website:- www.nihva.com

	SIGN	DATE
DRAWN	OMKAR	25/07/16
CHECK	ANIL	25/07/16
REV.		
APPROVAL		

If any queries contact : projects@nihva.com

ALL DIMENSION ARE IN mm

CLIENT - TAIIN STEELS FAB & INFRA PVT.LTD.
PROJECT - HYOSUNG T&D
SITE -
DWG. NO. : NIHVA/16-17/0041/R01
SCALE: NTS | WT: | SHEET: 01 OF 01