



1.DIA 75 mm CONDUIT WITH 4 CORE 1 SQ. mm WIRE FROM MAIN SUPPLY TO BOOM BARRIER & BOOM BARRIER TO CONTROL PANEL
2. SINGLE PHASE 230V, 50HZ SUPPLY IS REQUIRED.

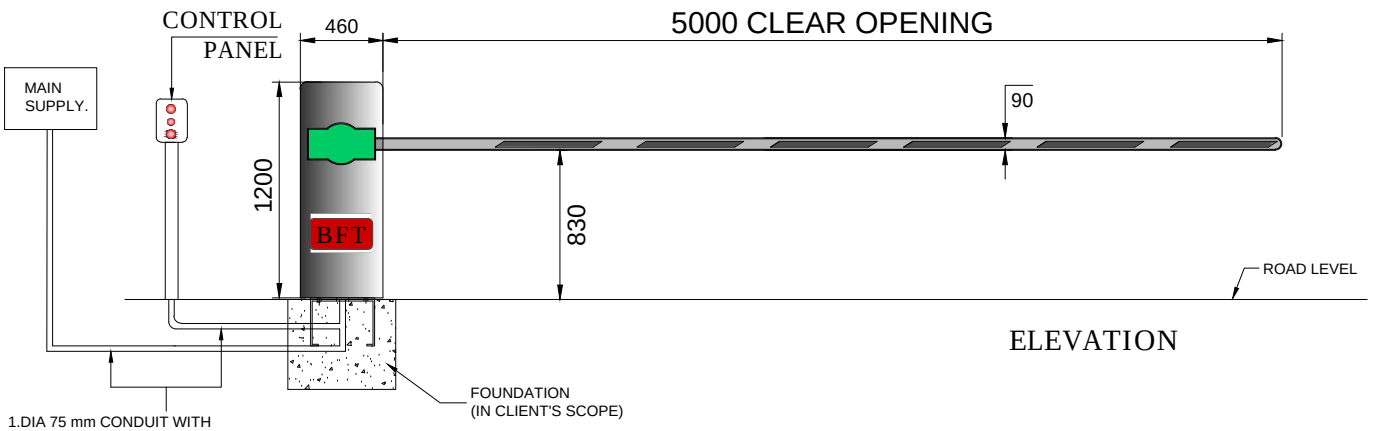

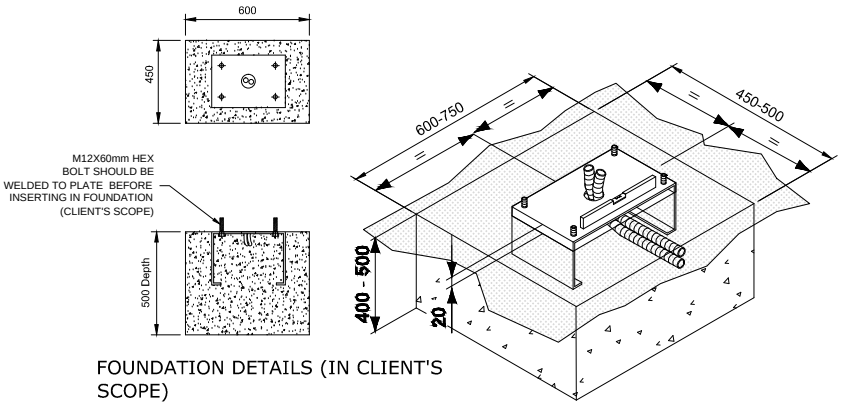

FOUNDATION DETAILS (IN CLIENT'S SCOPE)

SR NO	CLEAR WIDTH	QTY.
1	5000mm	01 NOS

TOLERANCE - ±10mm

This drawing & design is the property of NIHVA TECHNOLOGIES. Not to be sold or copied to any other concern.

TITLE: BOOM BARRIER 5m

NIHVA TECHNOLOGIES PVT. LTD. PUNE
Tel : 020 66304033
Email:- info@nihva.com
Website:- www.nihva.com

	NAME	SIGN	DATE
DRAWN	SURAJ		05-02-2018
CHECK	OMKAR		05-02-2018
APPRD.	SHEKHAR		05-02-2018

If any queries contact : design@nihva.com

ALL DIMENSION ARE IN mm

CLIENT - DEV TECHNO SKILL

PROJECT -AMAR TEA

SITE LOCATION - VASAI,MUMBAI.

DWG. NO. : NIHVA/17-18/0351 | REV- 0

SCALE: NTS | WT: | SHEET: 01 OF 01