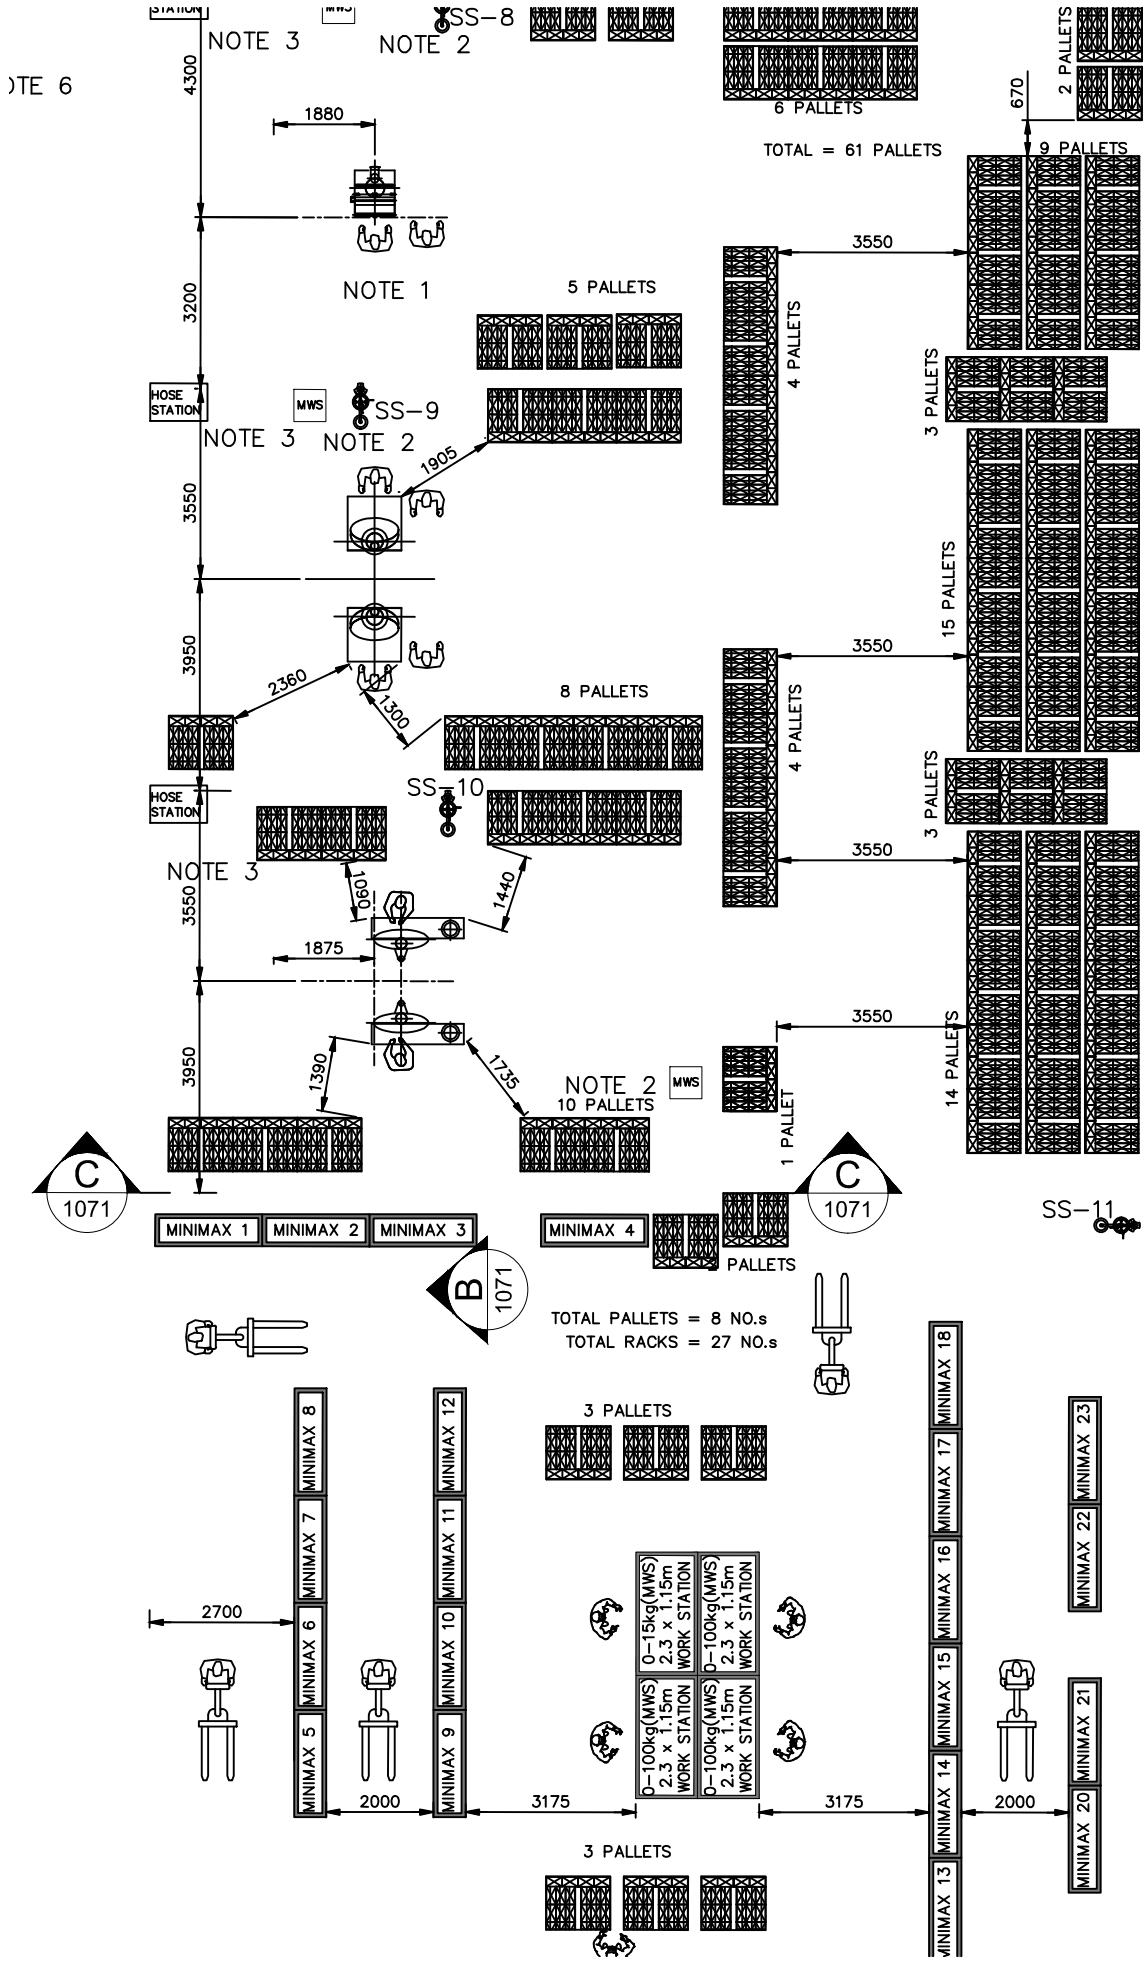

)TE 6
NOTE 3
NOTE 2
SS-8
6 PALLETS
2 PALLETS
670
TOTAL = 61 PALLETS
9 PALLETS
4300
1880
NOTE 1
5 PALLETS
3200
3550
4 PALLETS
3 PALLETS
HOSE STATION
MWS
SS-9
NOTE 3
NOTE 2
1905
3550
15 PALLETS
3950
2360
1300
8 PALLETS
SS-10
HOSE STATION
NOTE 3
1090
1440
3550
1875
3950
1390
1735
NOTE 2
10 PALLETS
1 PALLET
14 PALLETS
C
1071
C
1071
SS-11
MINIMAX 1
MINIMAX 2
MINIMAX 3
MINIMAX 4
PALLETS
B
1071
TOTAL PALLETS = 8 NO.s
TOTAL RACKS = 27 NO.s
3 PALLETS
MINIMAX 8
MINIMAX 7
MINIMAX 6
MINIMAX 5
MINIMAX 12
MINIMAX 11
MINIMAX 10
MINIMAX 9
MINIMAX 18
MINIMAX 17
MINIMAX 16
MINIMAX 15
MINIMAX 14
MINIMAX 13
MINIMAX 23
MINIMAX 22
MINIMAX 21
MINIMAX 20
2700
0–15kg(MWS) 2.3 x 1.15m WORK STATION
0–100kg(MWS) 2.3 x 1.15m WORK STATION
0–100kg(MWS) 2.3 x 1.15m WORK STATION
0–100kg(MWS) 2.3 x 1.15m WORK STATION
2000
3175
3175
2000
3 PALLETS