

TOP VIEW


INSIDE

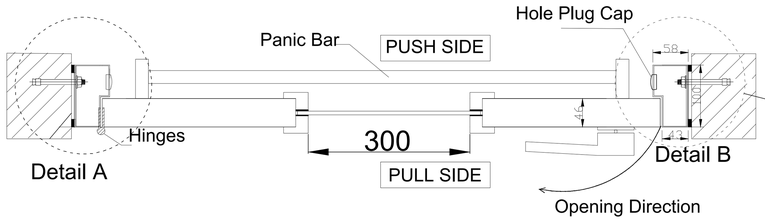

OUT SIDE

SECTION 'X'-'X'

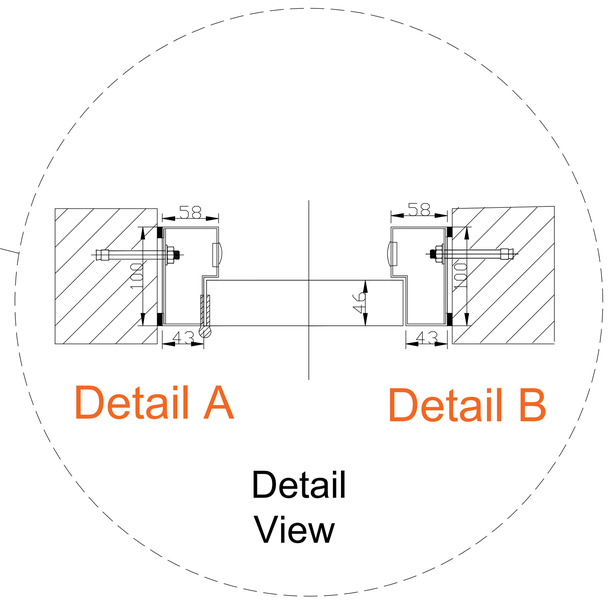

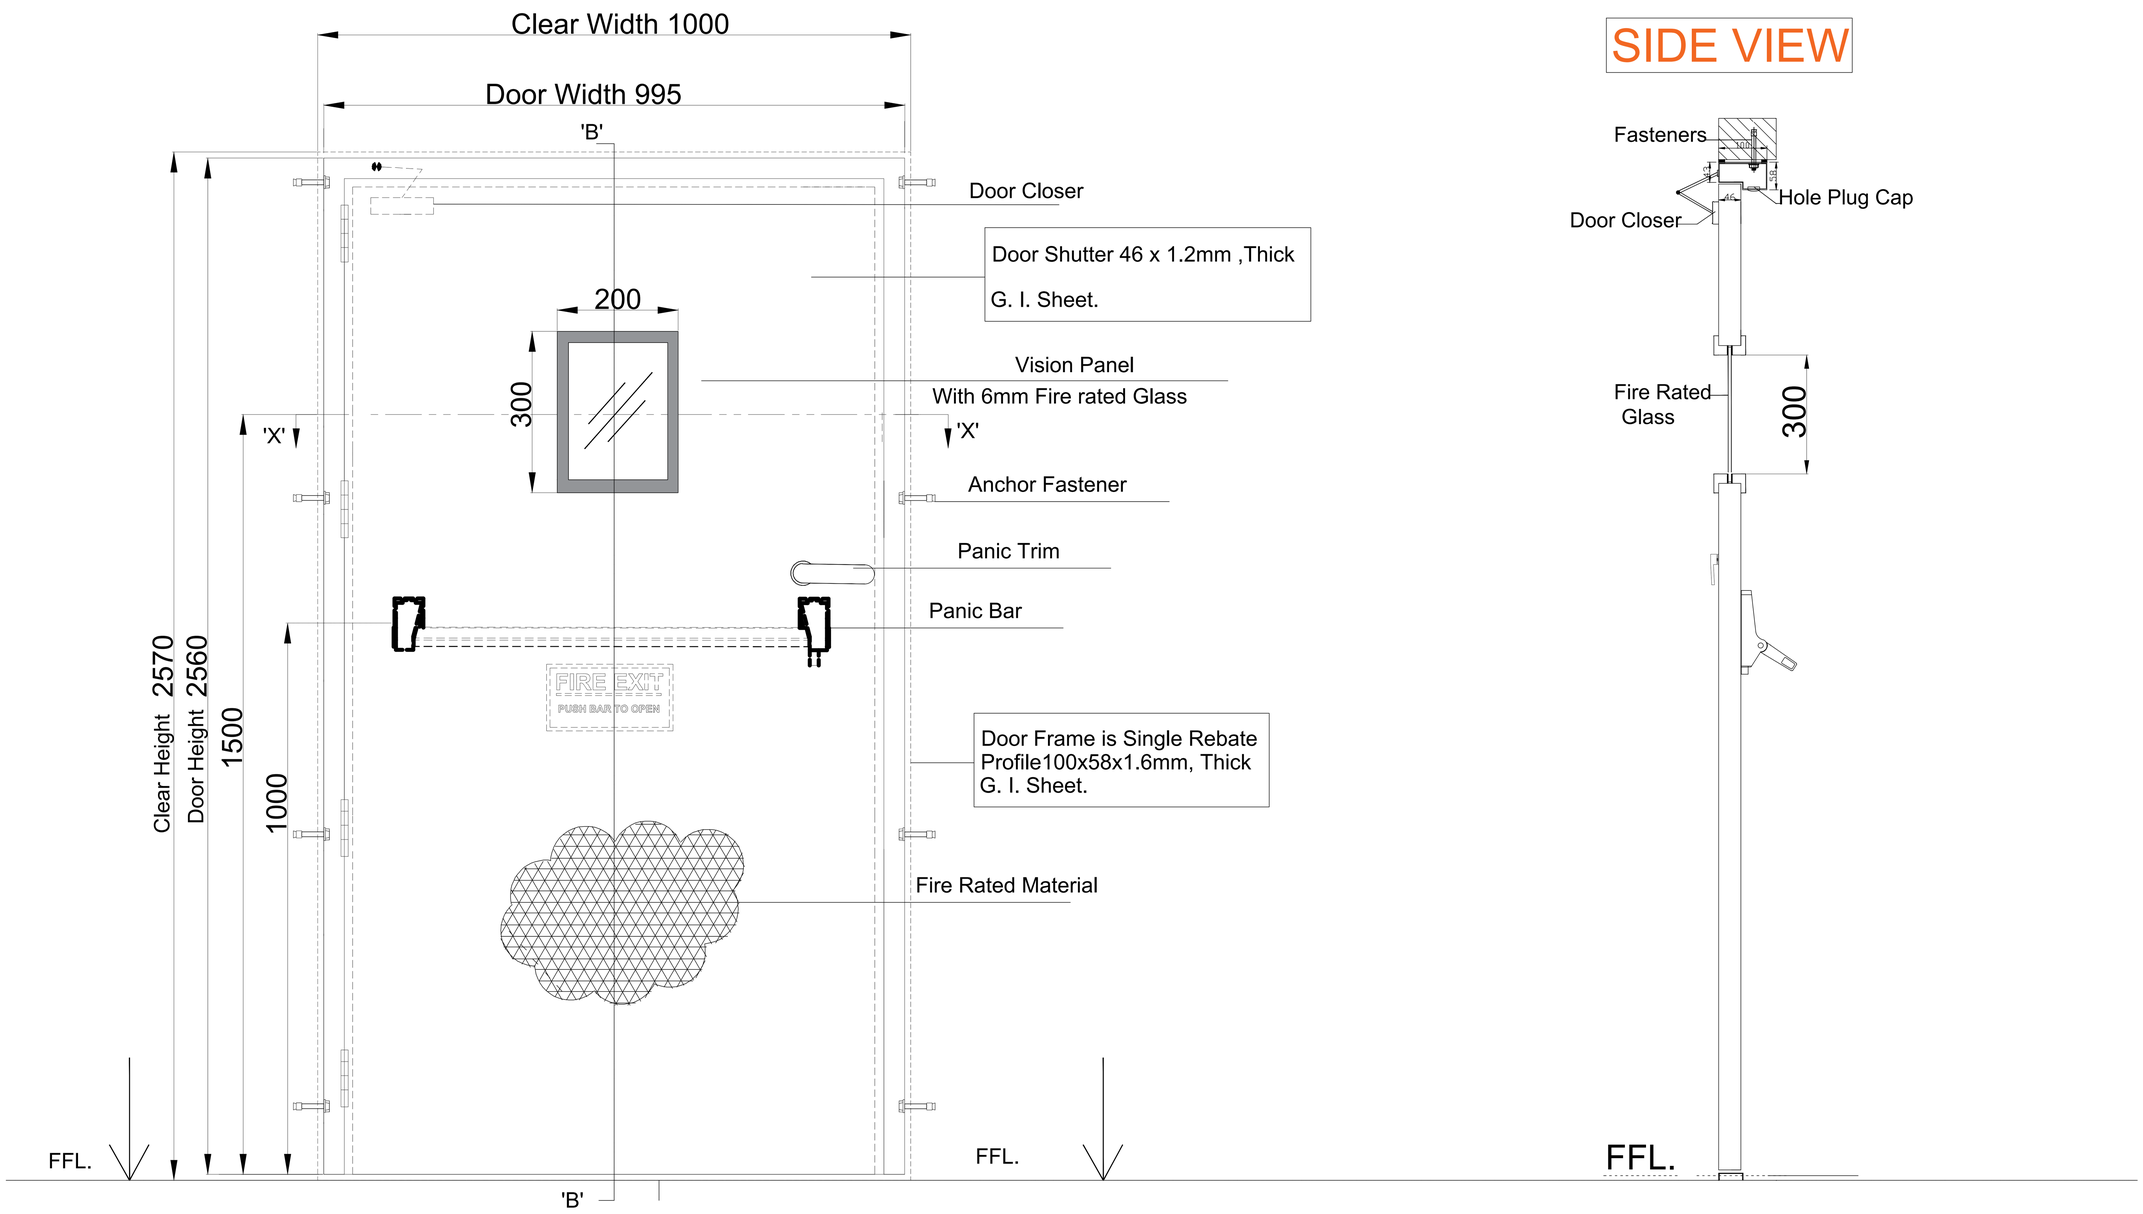

ELEVATION

SIDE VIEW

SECTION B-B

TECHNICAL SPECIFICATION :

Sr.	DESCRIPTION & DETAILS
01	Door frame - 100X58 mm x1.6mm thick G.I. Sheet
02	Door Shutter - 46 mm x1.2mm thick G.I. Sheet
03	SS Ball Bearing Hinges 4"x3"x3mm
04	Single Leaf Panic Bar
05	External Panic Trim
06	Anchor Fasteners (M10x100mm Dia)
07	Heavy Duty Door Closer (TS 1000)
08	Vision Window With 6mm Fire Rated Glass
09	Fire Rating - 120 Minutes

Note :-

1. All Dimension are in mm
2. This drawing is only for understanding purpose
3. RAL code confirm by client

SIZE:

Sr.	Clear Width	Clear Height	Qty
01	1000	2570	01

This Drawing & Design is the property of NIHVA TECHNOLOGIES. Not to be sold or copied to any other concern.

TITLE :- FIRE DOOR

NIHVA TECHNOLOGIES PVT. LTD. PUNE
Tel : 020 66304033
Email : info@nihva.com
Website : www.nihva.com

NAME	DATE	SIGN
S.J	03/10/2024	
S.W	03/10/2024	
V.T	03/10/2024	

CLIENT -TATA MOTOR

LOCATION - CHINCHWAD,PUNE

PRODUCT - FIRE DOOR | QTY-01 Nos

If any queries contact : design2@nihva.com | DWG NO - NIHVA/24-25/00XX | REV- 0

All dimensions are in MM | SCALE : NTS | SHEET : 01 OF 01