


NOTE :
1. DOOR HINGES : GEZE MAKE.
2. DOOR CLOSER : GEZE MAKE.
3. DOOR PANIC BAR : YELE MAKE.
4. DOOR CORDINATOR : GEZE MAKE.

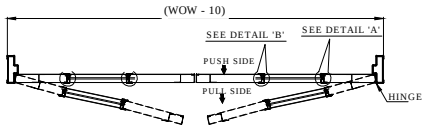

TOP VIEW

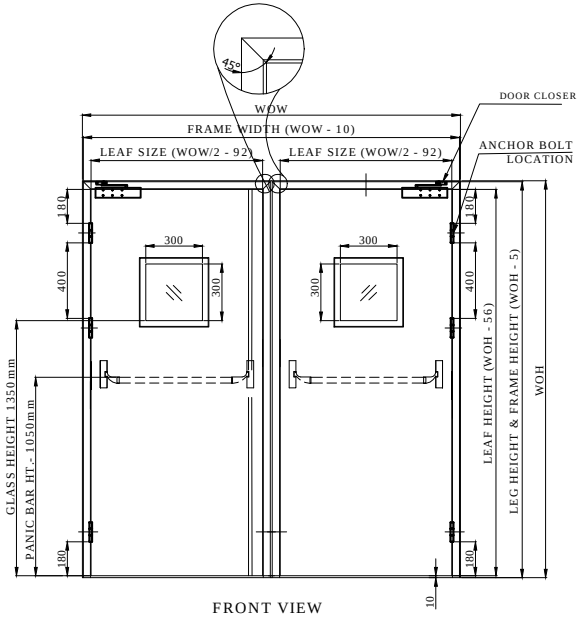


FRONT VIEW

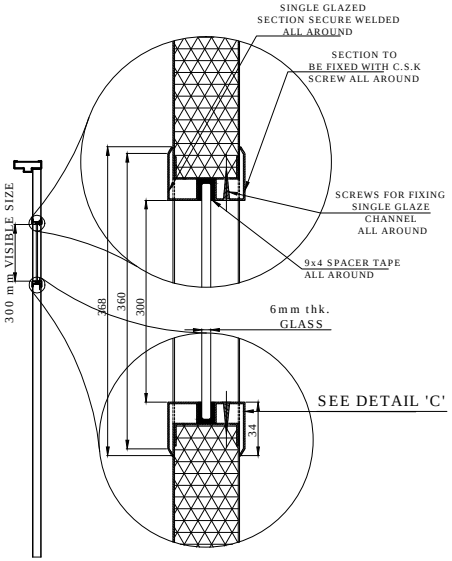


SIDE VIEW
SECTION A-A'

SINGLE GLAZE FIXING DETAIL

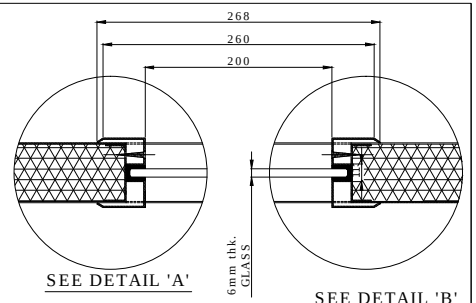



SEE DETAIL 'A'

SEE DETAIL 'B'

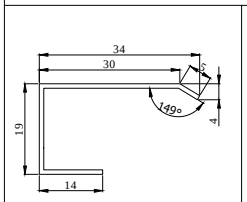


SEE DETAIL 'C'

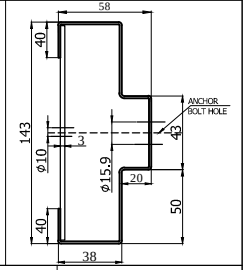

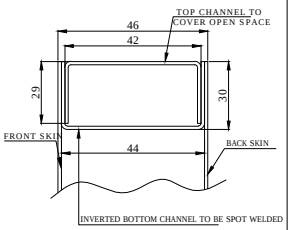

DOOR TOP SECTION DETAIL

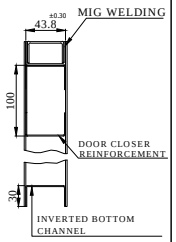

DOOR BOTTOM & TOP DETAIL

REV. NO	DATE	DRAWN	REMARK
R01	27.03.19	P.V.A	1.SPECIFICATION ADDED.

NOTE :
1. Up to 2 hours fire resistance in accordance with BS 476 part 22, UL 10B & UL 10C dependent on construction.
2. CORES : Honeycomb Paper.

SR. NO	WALL OPENING WIDTH	WALL OPENING HEIGHT	QTY	RAL	LOCATION	HARDWARE
02	1500	2140	01	9002	Admin Building (FD5B) - Stair Entry	Double leaf Fire door with Glass vision panel, Panic bar Inside and Pull handle outside
01	1500	2215	01	9002	Admin Building (GD5B) - Stair Exit	Double leaf metal door with glass vision panel , Panic bar inside , pull handle outside

TOLERANCE - ±05mm

This drawing & design is the property of NIHVA TECHNOLOGIES. Not to be sold or copied to any other concern.

TITLE: DOUBLE LEAF FIRERATED STEEL DOOR

	NAME	SIGN	DATE
DRAWN	P.V.A		21.03.2019
CHECK	V.M.T		21.03.2019
APPRD.			

If any queries contact : design@nihva.com

ALL DIMENSION ARE IN mm

NIHVA TECHNOLOGIES PVT. LTD.
NIHVA TECHNOLOGIES PVT. LTD. PUNE
Tel : 020 66304033
Email:- info@nihva.com
Website:- www.nihva.com

CLIENT - SYNERGY
PROJECT - EMBASSY
SITE LOCATION - CHAKAN, PUNE.
DWG. NO. : NIHVA/18-19/0299/R01 | REV- R01
SCALE: NTS | WT: | SHEET: 01 OF 01