


PRODUCED BY AN AUTODESK EDUCATIONAL PRODUCT

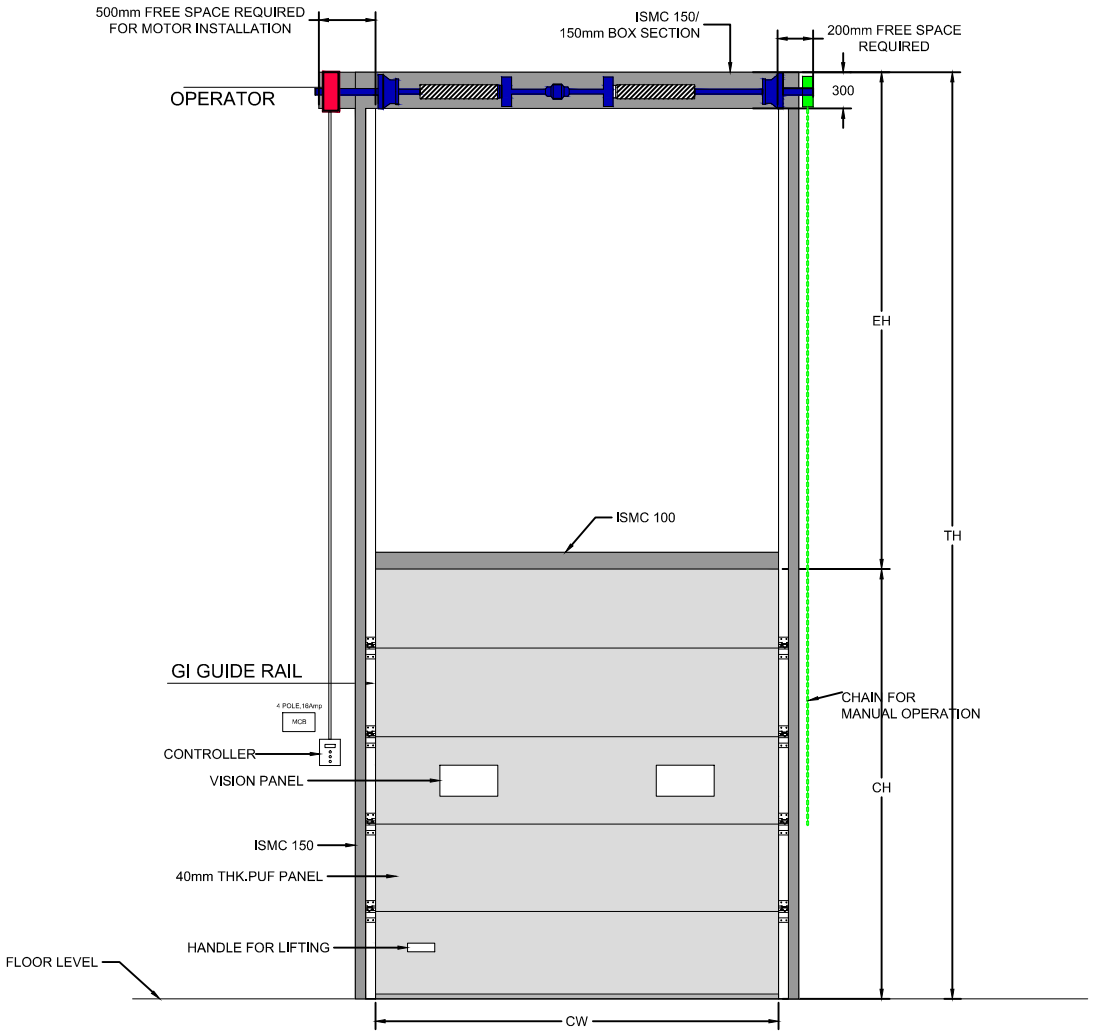

INSIDE VIEW

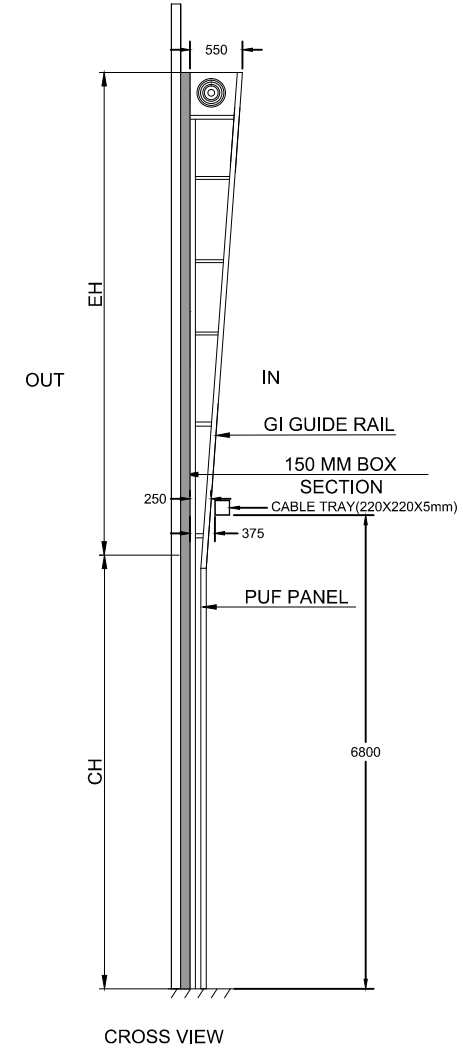

CROSS VIEW

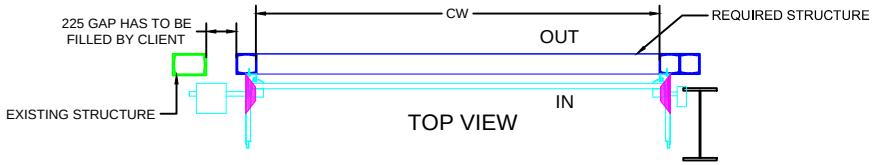

TOP VIEW

SR NO	CLEAR WIDTH	CLEAR HEIGHT	QTY	TH	EH	LOCATION (w.r.t PEB A01-R1)	MOTOR POSITION
9	3475mm	6000mm	1	12300	6300	1-C2'	LEFT

This drawing & design is the property of NIHVA TECHNOLOGIES. Not to be sold or copied to any other concern.

TITLE: SECTIONAL DOOR

NIHVA TECHNOLOGIES PVT. LTD. PUNE
Tel : 020 66304033
Email:- info@nihva.com
Website:- www.nihva.com

	SIGN	DATE
DRAWN	OMKAR	12/05/17
CHECK	SAGAR P.	12/05/17
APPROVAL		

CLIENT - TATA PROJECTS
PROJECT - MADHEPURA ELECTRIC LOCOMOTIVE PVT. LTD.
SITE - MADHEPURA,BIHAR
DWG. NO. : NIHVA/17-18/0066
If any queries contact : projects@nihva.com
SCALE: NTS | WT: | SHEET: 01 OF 01
ALL DIMENSION ARE IN mm

PRODUCED BY AN AUTODESK EDUCATIONAL PRODUCT
PRODUCED BY AN AUTODESK EDUCATIONAL PRODUCT
PRODUCED BY AN AUTODESK EDUCATIONAL PRODUCT