

NOTE :
1. DOOR HINGES : GEZE MAKE.
2. DOOR CLOSER : GEZE MAKE.
3. DOOR EXTERNAL TRIM : YELE MAKE.

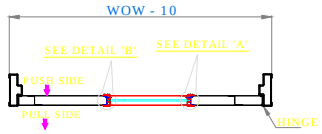


TOP VIEW

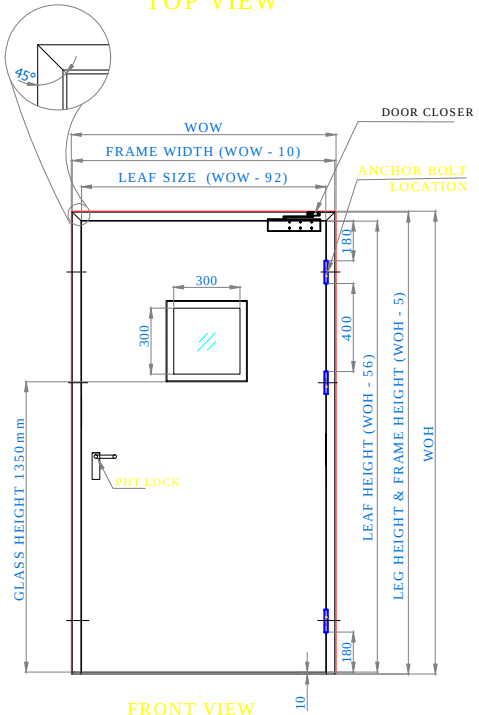


FRONT VIEW





SIDE VIEW
SECTION A-A'

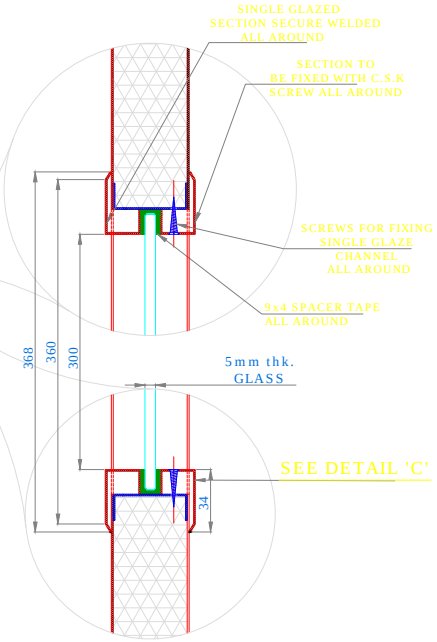


SINGLE GLAZE FIXING DETAIL

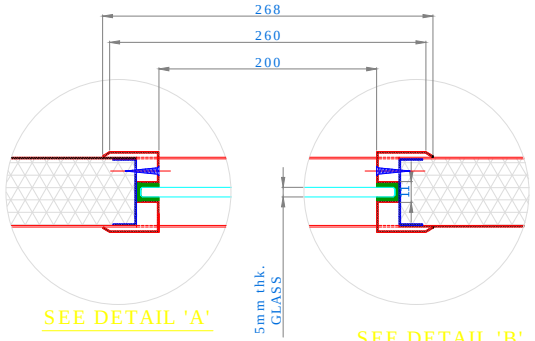


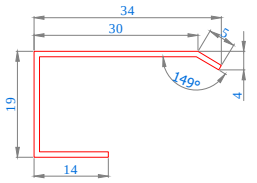

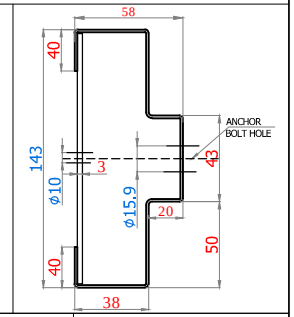

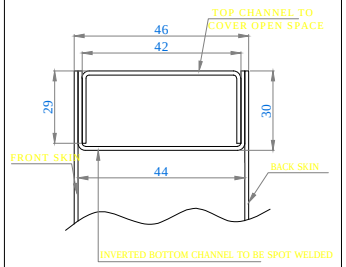

DOOR TOP SECTION DETAIL

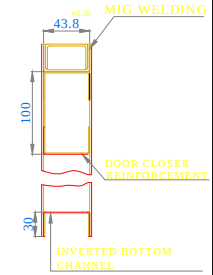

DOOR BOTTOM & TOP DETAIL

SR. NO	WALL OPENING WIDTH	WALL OPENING HEIGHT	QTY	HARDWARE
01	1200	2400	02	Single leaf metal door with Vision Panel, Hinges , Door closer ,with external trim

TOLERANCE - ±05mm

This drawing & design is the property of NIHVA TECHNOLOGIES. Not to be sold or copied to any other concern.

TITLE				
SINGLE LEAF STEEL DOOR				NIHVA TECHNOLOGIES PVT. LTD. PUNE Tel : 020 66304033 Email:- info@nihva.com Website:- www.nihva.com
	NAME	SIGN	DATE	
DRAWN	P.V.A		22.03.2019	CLIENT - UNITED ARCHITECT
CHECK	V.M.T		22.03.2019	PROJECT - ESR
APPRD.				SITE LOCATION - BHIWAANDI
If any queries contact : design@nihva.com				DWG. NO. : NIHVA/18-19/0304 REV- R00
ALL DIMENSION ARE IN mm				SCALE: NTS WT: SHEET: 01 OF 01