


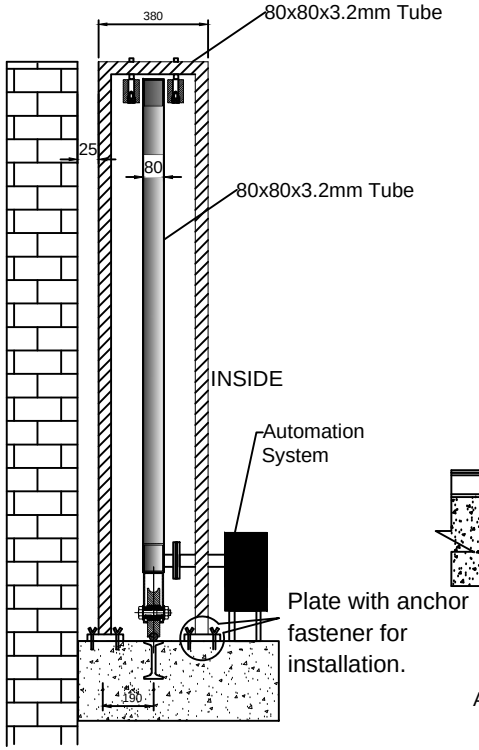


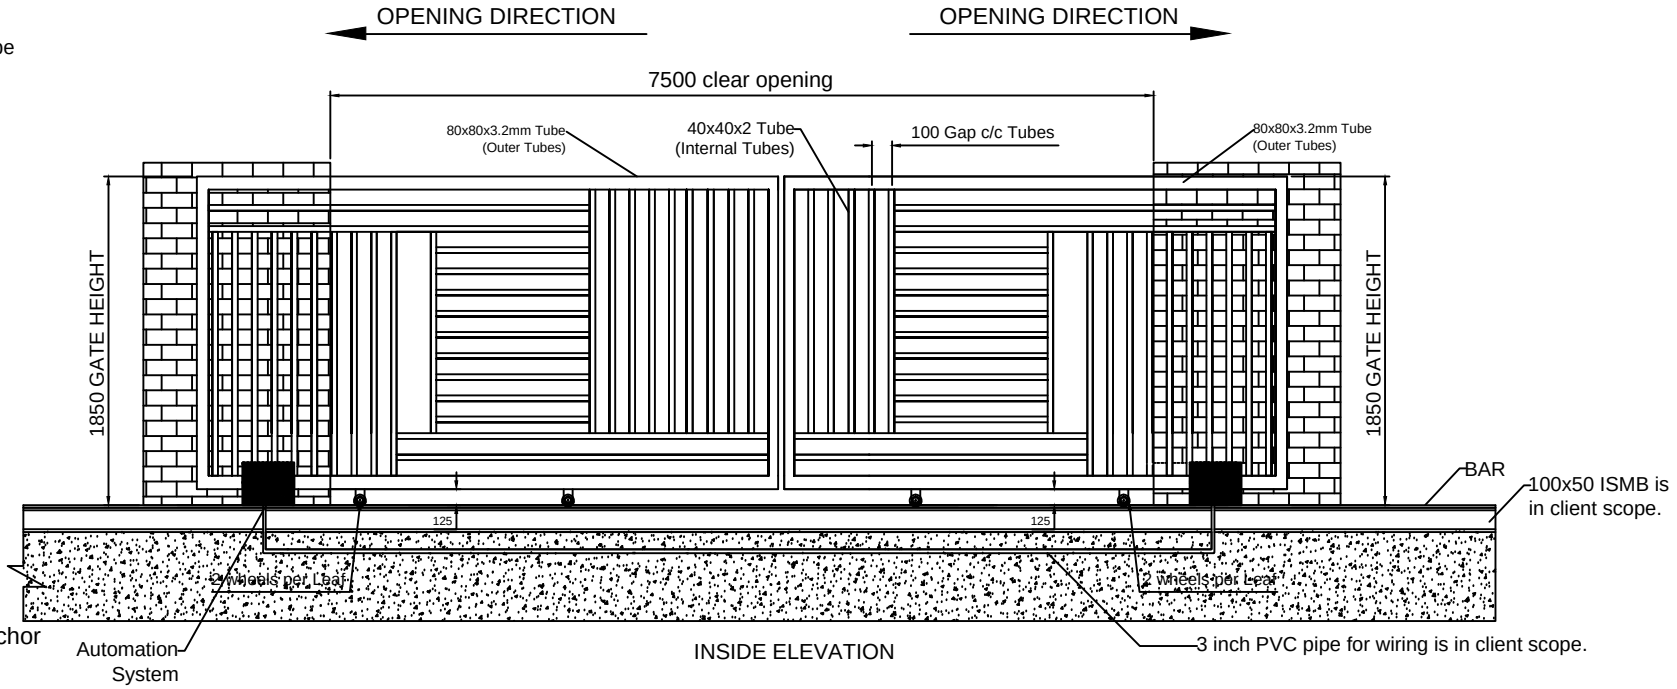

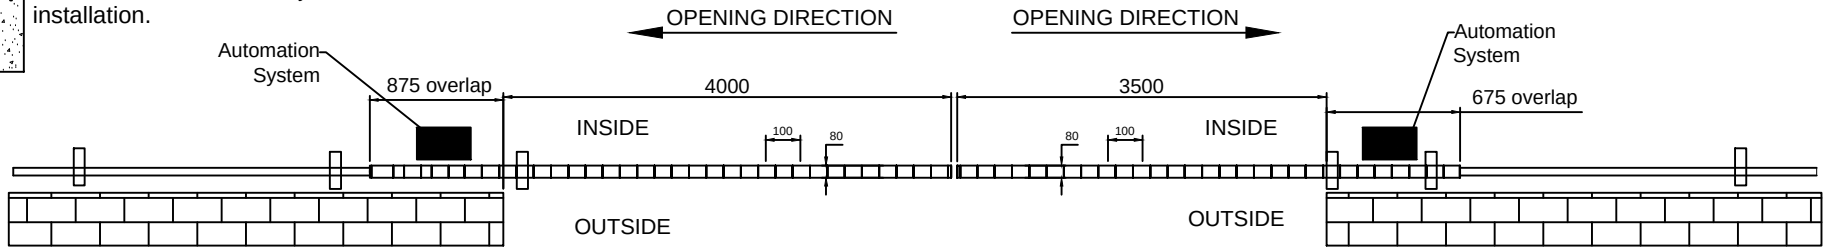

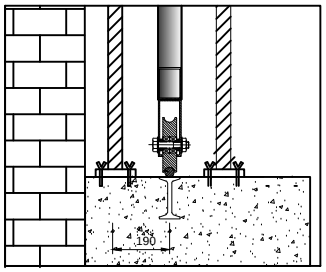

Clear Opening size -7500mm x 1850mm
Total No. of Leaf - 2 Leaf
NOTE :- *ALL REQ. CIVIL WORK WILL BE IN CLIENT SCOPE.

DOUBLE UNEQUAL LEAF SLIDING GATE

This drawing & designing is the property of NIHVA TECHNOLOGIES. Not be sold or copy to any other concern.

TITLE	DOUBLE LEAF MOTORISED SLIDING GATE	
	SIGN	DATE
DRAWN	OMKAR	25/02/16
CHECK	ANIL	25/02/16
REV.	01	
APPROVAL		
If any queries contact : projects@nihva.com		
ALL DIMENSION ARE IN mm		

NIHVA TECHNOLOGIES PVT. LTD.
NIHVA TECHNOLOGY PVT. LTD. PUNE
Tel : 020 66304033
Email:- info@nihva.com
Website:- www.nihva.com

CLIENT -		
PROJECT -		
SITE -		
DWG. NO. : NIHVA/15-16/		
SCALE: 01	WT:	SHEET: 01 OF 01