
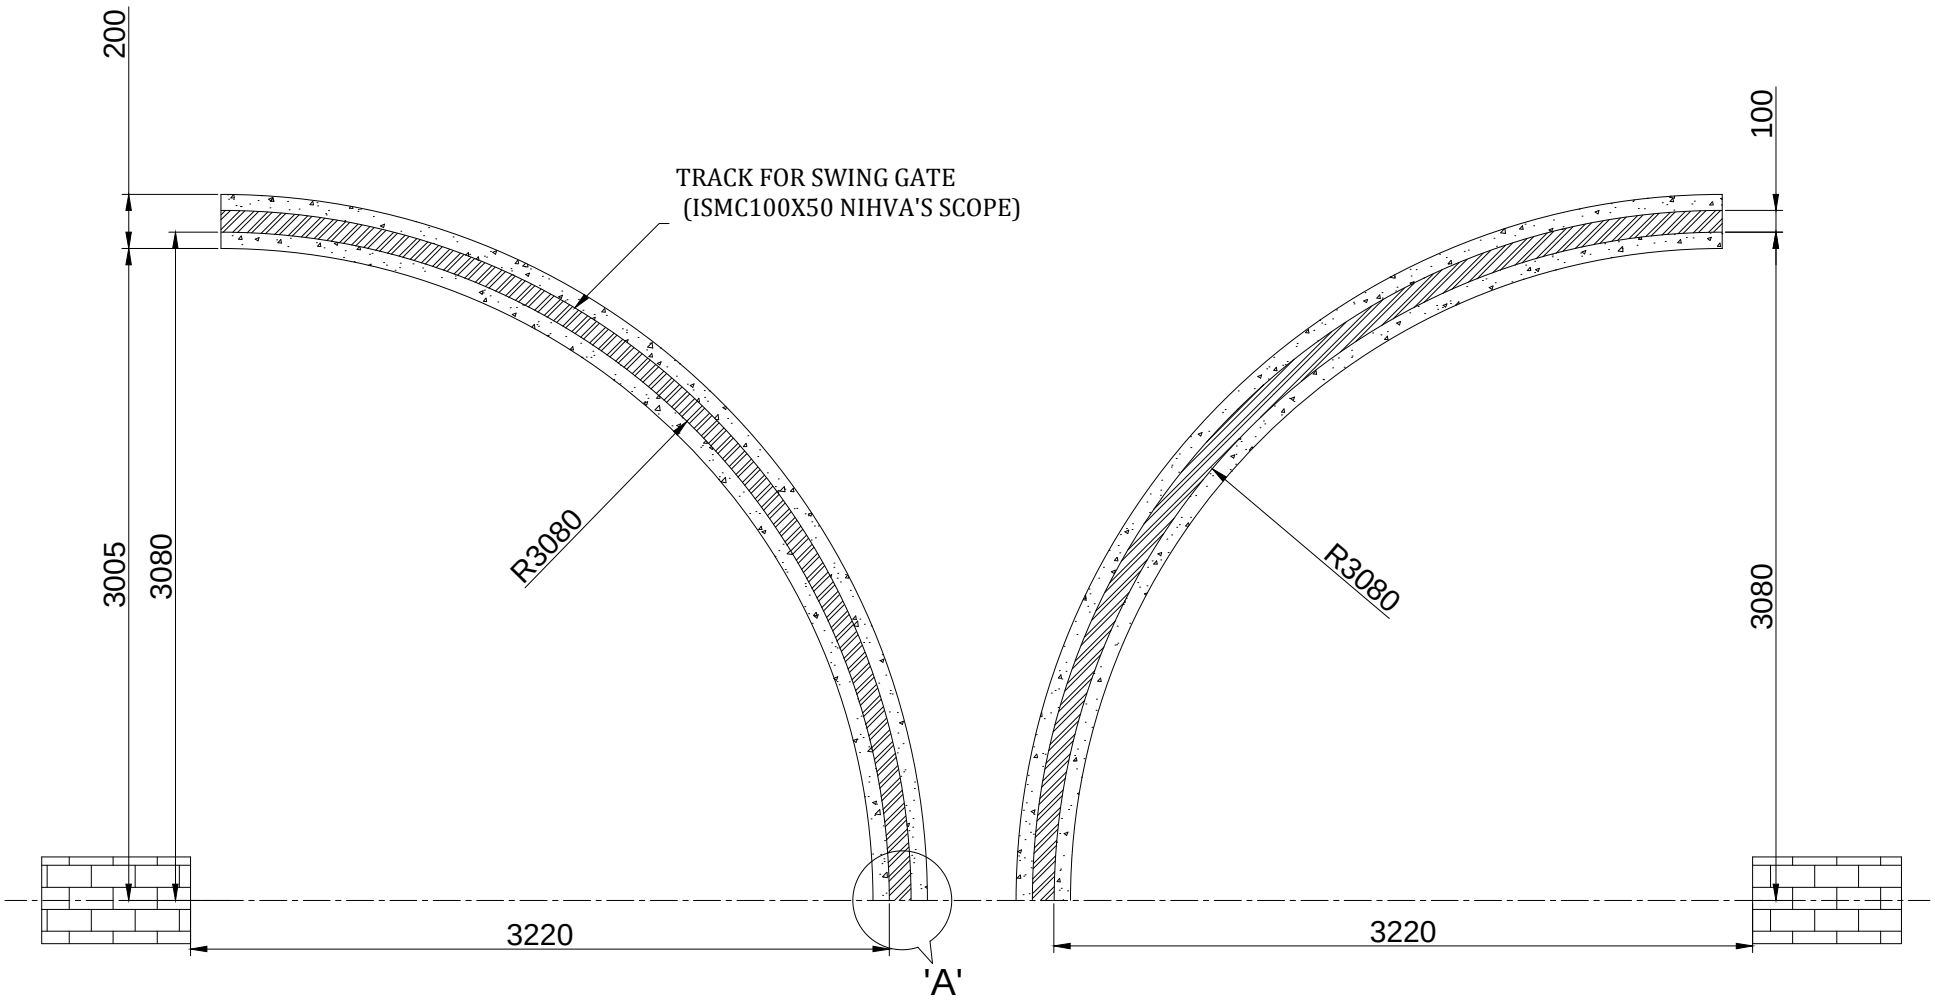


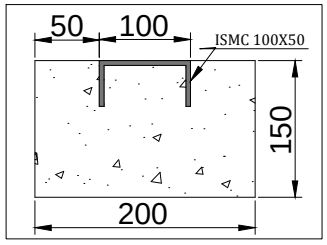

DETAIL VIEW OF 'A'

This drawing & design is the property of NIHVA TECHNOLOGIES. Not to be sold or copied to any other concern.

TITLE
FOUNDATION OF MANUAL SWING GATE 7.2X1.8m

NIHVA TECHNOLOGIES PVT. LTD.
NIHVA TECHNOLOGIES PVT. LTD. PUNE
Tel : 020 66304033
Email:- info@nihva.com
Website:- www.nihva.com

	SIGN	DATE
DRAWN	SURAJ	18/05/17
CHECK	SAGAR P.	18/05/17
REV.		
APPROVAL	S.S	18/05/17

CLIENT - TATA PROJECT
PROJECT - ALSTOM
SITE LOCATION -MADHEPURA,(M.P)
DWG. NO. : NIHVA/17-18/0084
If any queries contact : projects@nihva.com
SCALE: NTS | WT: | SHEET: 01 OF 01
ALL DIMENSION ARE IN mm