ASSA ABLOY

Installation documents

Nihva Poonawala

Project No. 84470

Installation Manual

Project handover, installation checklist, Installation report,

Daily field report, changes during installation 1

Shall always be filled out and sent back to AAES Skellefteå.

Interface drawing, main assembly drawings 2

Sub assembly drawings 3

Load diagram 4

Electrical installation diagram 5

Fabric folding instruction 6

Project Hand Over

84470 Nihva Poonawala

Project description: ***Megadoor in size 20000 mm X 7000 mm acc. to assembly drawing No. A1- 69426***

Contract/file: *ASSA ABLOY quotation 219-355*

Installation: ***Done in accordance to "Installation manual" and with Megadoor certified supervisor.***

Actual project is hereby approved and accepted for hand over to the Purchaser:

Warranty period for material: ***12 months from Project Hand Over***

For ASSA ABLOY (Supplier)

For: (Purchaser)

…… ……..

Date: Date:

ASSAABLOY Entrance System
Servicegatan 6
SE- 931 76 Skellefteå

Tel: + 46 (0)10 47 47 190
Fax : + 46 (0)910 166 20
www.assaabloyentrance.com

Org. No: 556059-9523
Vat. No: SE55605995230

Project Hand Over

84470 Nihva Poonawala

Project description: ***Megadoor in size 20000 mm X 7000 mm acc. to assembly drawing No. A1- 69426***

Contract/file: *ASSA ABLOY quotation 219-355*

Installation: ***Done in accordance to "Installation manual" and with Megadoor certified supervisor.***

Actual project is hereby approved and accepted for hand over to the Purchaser:

Warranty period for material: ***12 months from Project Hand Over***

For ASSA ABLOY (Supplier)

For: (Purchaser)

…… ……..

Date: Date:

ASSAABLOY Entrance System
Servicegatan 6
SE- 931 76 Skellefteå

Tel: + 46 (0)10 47 47 190
Fax : + 46 (0)910 166 20
www.assaabloyentrance.com

Org. No: 556059-9523
Vat. No: SE55605995230

AAES Production Skellefteå AB
Servicegatan 6
931 76 Skellefteå
Sweden
www.megadoor.com

INSTALLATION CHECK LIST MEGADOOR PROJECTS

Project Name: Nihva Poonawala	Project Number: 84470	Engineers on site:
	Sheet Number:	

	Check list pre-installation	OK	NOT OK	N/A
1	**Documentation**			
1.1	- Installation documentation has been studied and understood	☐	☐	☐
1.2	- Deviations from documentation have been reported and approved	☐	☐	☐
2	**Building**			
2.1	- Has appropriate stability	☐	☐	☐
2.2	- Has been load tested	☐	☐	☐
2.3	- Measurements are in accordance with agreements	☐	☐	☐
	Check during installation			
3	**Door machinery**			
3.1	- Belts intact, not chafing or twisted	☐	☐	☐
3.2	- Belt loops have sewn flap facing toward TW	☐	☐	☐
3.3	- Belt drum segments and belt rotate in correct direction	☐	☐	☐
3.4	- Adjustable roller holders are adjusted and locked	☐	☐	☐
3.5	- Wire rope fleet angle within 4 degrees	☐	☐	☐
3.6	- Wire rope lubricated correctly	☐	☐	☐
3.7	- Hoist and sheave grooves lubricated correctly	☐	☐	☐
4	**Chain hoist**			
4.1	- Chain secured, exit stop fitted	☐	☐	☐
4.2	- Chain intact, not twisted	☐	☐	☐
4.3	- Enough slack at lower position	☐	☐	☐
4.4	- Hoist free to swing	☐	☐	☐
4.5	- Hoist is directly above lifting pipe	☐	☐	☐
4.6	- Chain lubricated correctly	☐	☐	☐
5	**Gear motors**			
5.1	- Air plug fitted	☐	☐	☐
5.2	- Motor brake working	☐	☐	☐
5.3	- Crank interlock working	☐	☐	☐
5.4	- Crank and brake lever correct size	☐	☐	☐
6	**Guiderail and Side Seal Angles**			
6.1	- Joints are even, tight, and dressed	☐	☐	☐
6.2	- Roll pins are in place, in both guiderail and seal angles	☐	☐	☐

6.3	- Pieces are aligned at mullion hinge joint	☐	☐	☐
6.4	- Arresters and guide blocks are not chafing	☐	☐	☐
6.5	- Guide blocks are adjusted with correct gap to guiderail	☐	☐	☐
7	**Safety Arresters**			
7.1	- Actuates freely without binding	☐	☐	☐
7.2	- Catching function works	☐	☐	☐
7.3	- Wind locks correctly positioned and re-verified after door has hung	☐	☐	☐

	Check during installation	OK	NOT OK	N/A
7.4	- Axial guide rollers adjusted with correct gap to guiderail	☐	☐	☐
7.5				
8	**Seals**			
8.1	- Installed, trimmed, and effective	☐	☐	☐
8.2	- Bottom rubber seal isolated from fabric to prevent out-gassing mark	☐	☐	☐
9	**Mullion**			
9.1	- Mullion swings up under door leaf	☐	☐	☐
9.2	- Pivot joint actuates smoothly	☐	☐	☐
9.3	- Pillow blocks greased	☐	☐	☐
9.4	- Pivot joint actuates smoothly	☐	☐	☐
9.5	**At normally loaded building:**			
9.6	- Floor pin centered and running easily in guide	☐	☐	☐
9.7	- Correct clearance between mullion end and floor	☐	☐	☐
9.8	- Pit covers fit and operate correctly	☐	☐	☐
10	**Door leaf**			
10.1	- Door leaf built with correct pitch	☐	☐	☐
10.2	- Fabric intact and clean	☐	☐	☐
10.3	- Fabric tensioned well at last few feet on each edge of door for tight seal	☐	☐	☐
10.4	- Fabric trimmed at sides, flush with batten strips	☐	☐	☐
10.5	- All fabric screws fitted	☐	☐	☐
10.6	- Batten strips not bent	☐	☐	☐
10.7	- Batten strips do not press against side seal angles	☐	☐	☐
10.8	- Batten strips trimmed with correct gap to TW	☐	☐	☐
10.9	- Top beam batten strip screwed into side seal at last hole location	☐	☐	☐
10.10	- Header box sheet metal installed and clean	☐	☐	☐
10.11	- Beam clamps have correct engagement onto support steel	☐	☐	☐
10.12	- Wooden blocks or shipping supports removed from door leaf / top beam	☐	☐	☐
10.13	- End of header box closed off with sheet metal if exposed	☐	☐	☐

11	**Joints**			
11.1	- Screws tightened with correct torque	☐	☐	☐
11.2	- Welds professionally done	☐	☐	☐
11.3	- Primer applied / touched up	☐	☐	☐
12	**Electric equipment**			
12.1	- Permanent power is connected	☐	☐	☐
12.2	- Control panel disconnect functions correctly	☐	☐	☐

	Check during installation	**OK**	**NOT OK**	**N/A**
12.3	- E-stops function correctly	☐	☐	☐
12.4	- Pushbuttons do not stick	☐	☐	☐
12.5	- Phase monitor adjusted	☐	☐	☐
12.6	- Current monitors adjusted	☐	☐	☐
12.7	- Audible/visual alarm functioning	☐	☐	☐
12.8	- No loose connections in panels	☐	☐	☐
13	**Limit switches**			
13.1	- Door and mullion limits adjusted and actuating correctly	☐	☐	☐
13.2	- Slack wire rope limit assembly adjusted and locked	☐	☐	☐
13.3	- Limit plunger extensions installed	☐	☐	☐
13.4	- 3-phase limit plungers correctly adjusted	☐	☐	☐
14	**Function**			
14.1	- Door is working in accordance with function description	☐	☐	☐
14.2	- Doors and mullions reach intended positions	☐	☐	☐
14.3	- Interlocks work as planned	☐	☐	☐
14.4	- Door has been operated through at least two complete cycles	☐	☐	☐
15	**Labelling**			
15.1	- Warning labels fitted	☐	☐	☐
15.2	- Instruction labels fitted	☐	☐	☐
15.3	- Instruction labels fitted	☐	☐	☐
16	**General**			
16.1	- User informed about door functions	☐	☐	☐
16.2	- User informed about six-inch-stop door closing procedure	☐	☐	☐
16.3	- Installation report approved and signed	☐	☐	☐
16.4	- Rental equipment return called in (record conformation numbers below)	☐	☐	☐
16.5	- Ship as-built prints to office within two days	☐	☐	☐
16.6	- Returned Material Form filled out if shipping any material back to Megadoor	☐	☐	☐

Notes, observations not previously recorded, customer comments.

Place: .....

Date: .....

Sign: .....

Name: .....

Supervisor

Date: .....

Sign: .....

Name: .....

Purchaser representative

Date: .....

Sign: .....

Name: .....

Third party representative

Address: Servicegatan 6
931 76 Skellefteå, Sweden
Tel: +46 10 47 47 190 Fax: +46 910 166 20

Project name: Nihva Poonawala
Project number: 84470
Supervisor:

Installation report

Date/Day	Weather impact on inst?	Supervisor: hours worked	Helpers: hours worked	Installation progress	Problems: Daily field report no.

Megadoor AB

Address: Servicegatan 6
931 76 Skellefteå, Sweden
Tel: +46 10 47 47 190 Fax: +46 910 166 20

Changes during installation

The installation has been completed; the following changes need to be implemented on Megadoor AB's documentation:

No changes ☐

Drawing # / Change

-

-

-

-

-

-

-

-

-

-

-

-

-

Date:_____

Signature:_____

Name in printing/Organization:_____

ASSA ABLOY

DAILY FIELD REPORT no:1


Job Name:	Nihva Poonawala	Date / Day:	
Job Number:	84470	Weather / Temp:	
Lead Installer:		Hours Worked: from	to
Helpers / Hours Worked:			

Anticipated or Current Delays: (Mark applicable item and explain)
Due to: ☐ dwg, ☐mat'l, ☐ equipment, ☐ subcontractor, ☐GC, ☐other


Subjects discussed with GC today: (Mark applicable item and explain)
☐ progress/schedule, ☐ extra work, ☐ manpower, ☐other

Installation Highlights: (Mark applicable item and explain)
☐ work completed, ☐ significant scope of work change, ☐ mat'l/equip problems,
☐ safety violations, ☐ anticipated construction problems, ☐ visitors


Attest by GC/Customer: _____

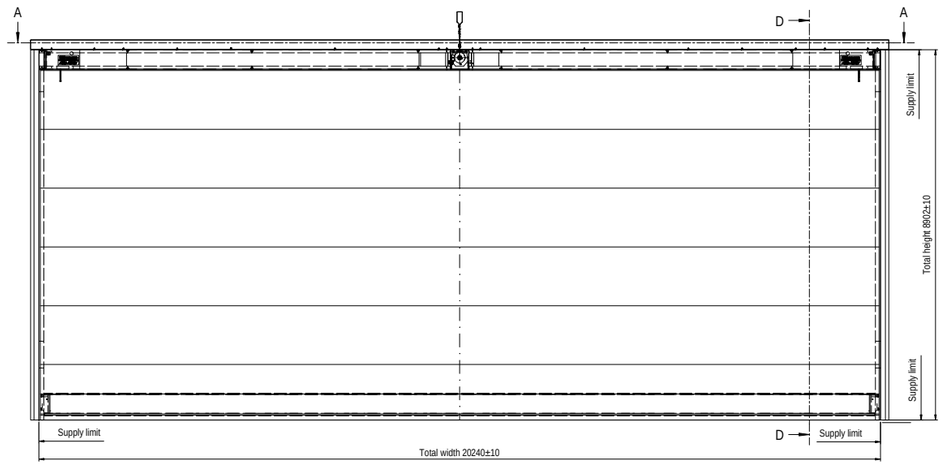

Interior view, Door closed

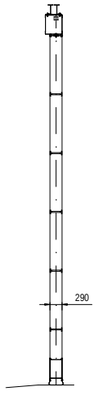


SECTION D-D

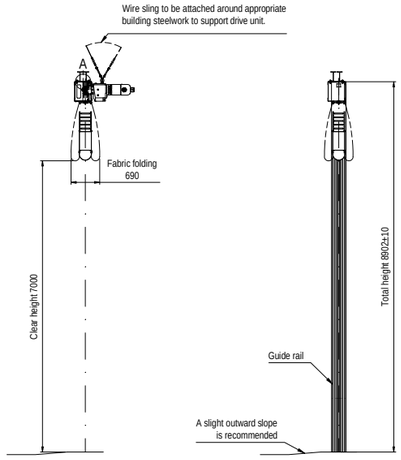


SECTION E-E


SECTION F-F

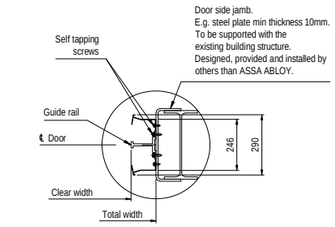


DETAIL B, SCALE (1:10)

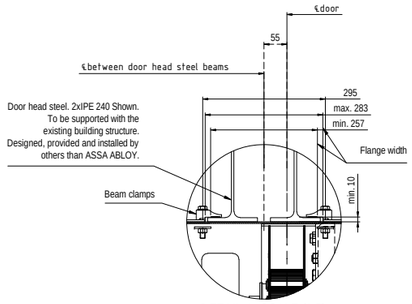


DETAIL A, SCALE (1:5)

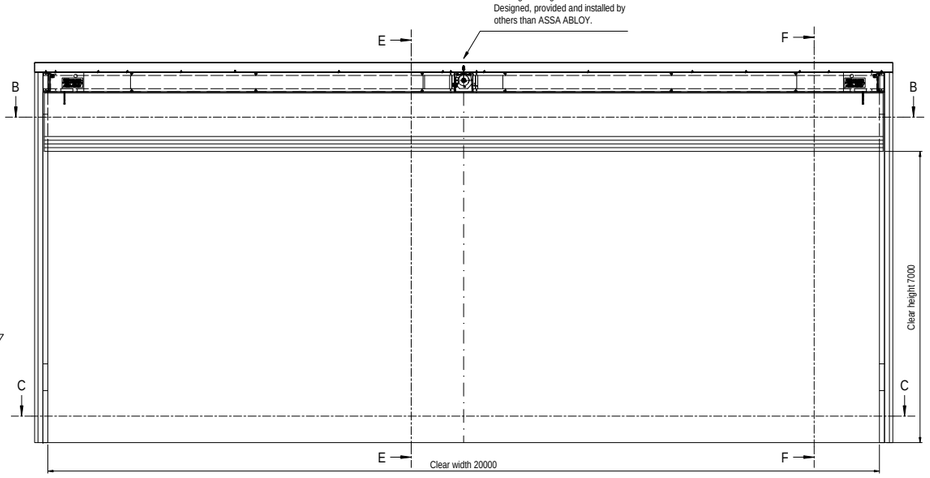


Interior view, Door open

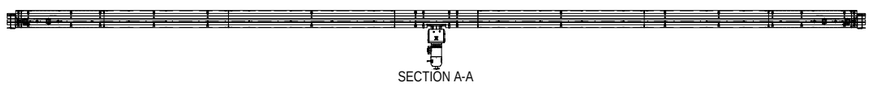

SECTION A-A

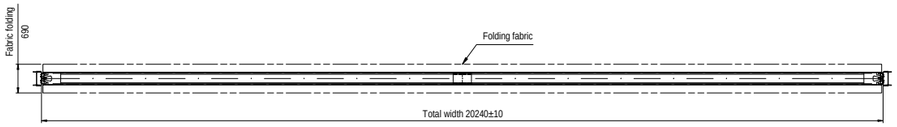

SECTION B-B

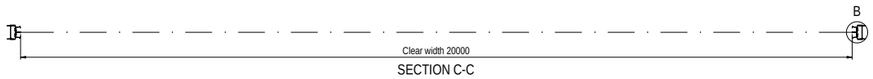

SECTION C-C

DOOR IDENTITY NUMBER: 84470001


LOAD DIAGRAM & NOTES, ref. to drwng. no. 69425

DESIGNED: FV		SIZE: A1F	SCALE: 1:50
CODE: 84470	If not otherwise stated: Tolerances ISO 2768-m EN ISO 13920-B Coating class ISO 9013-442 Weld class ISO 5817-C Surface finish Smooth raw surface		
ITEM NO:			
DATE: 2019-10-08			
ASSA ABLOY		DRAWING NO: 69424	REVISION: --


Nihva Poonawalla
India
Megadoor 20000 x 7000
Interface

PLOT DATE


This document is the property of ASSA ABLOY Entrance Systems AB and may not be copied or otherwise reproduced or disclosed to a third party or used for any other unauthorized purpose.

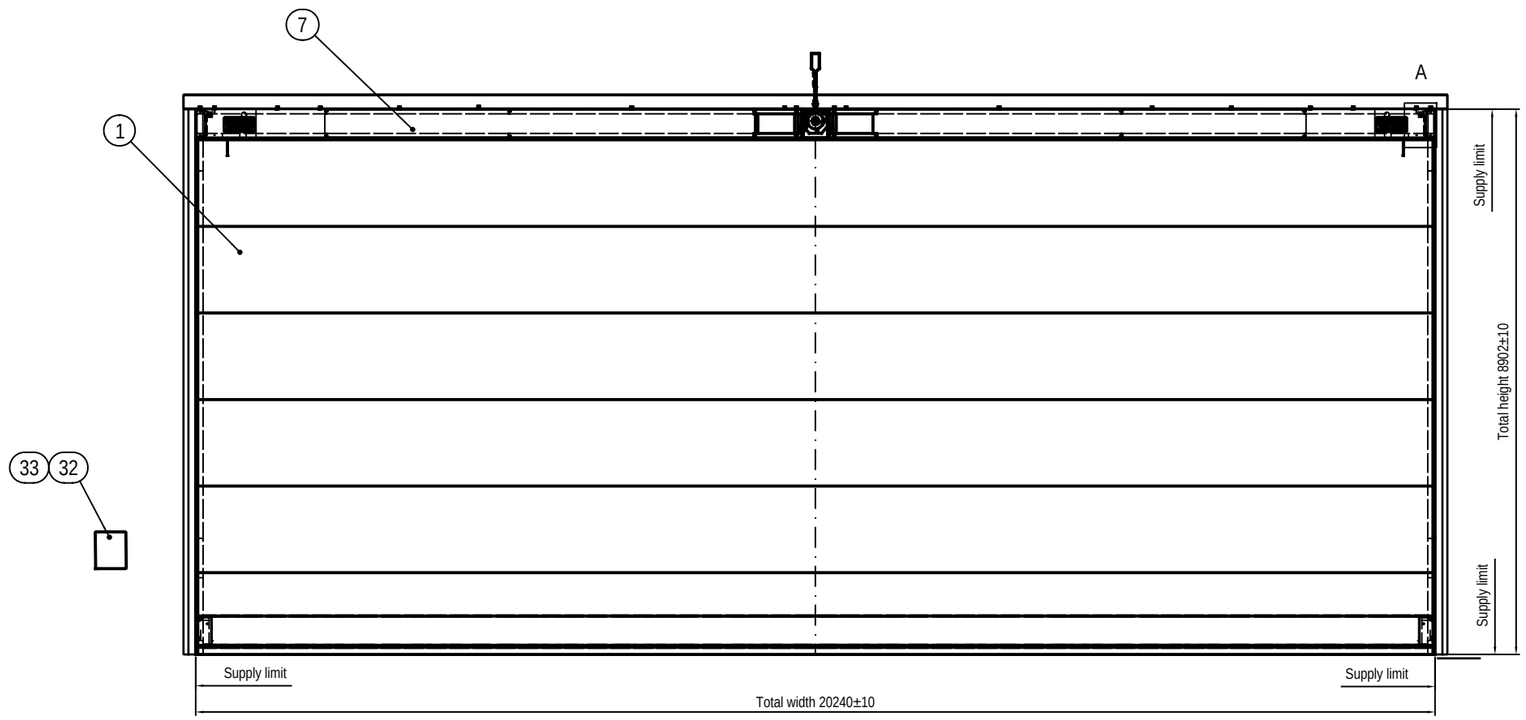


Interior view, Door closed

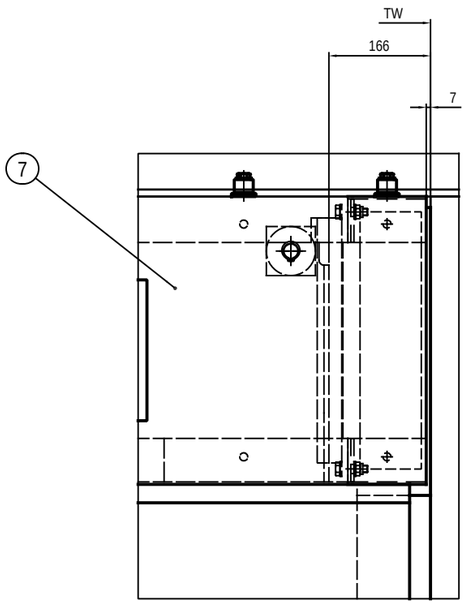


DETAIL A, SCALE (1:5)

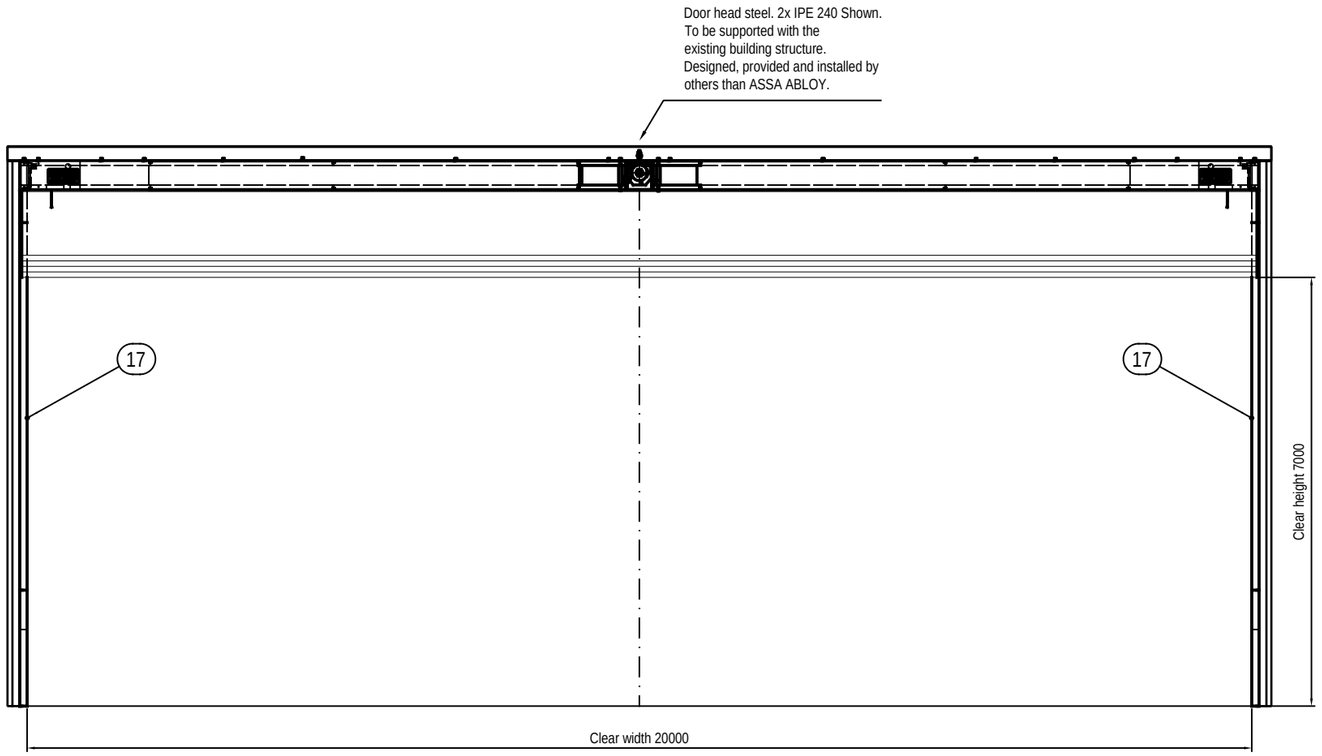

Interior view, Door open

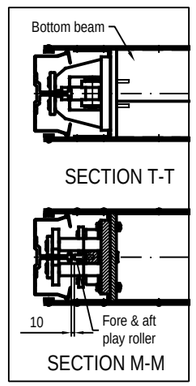

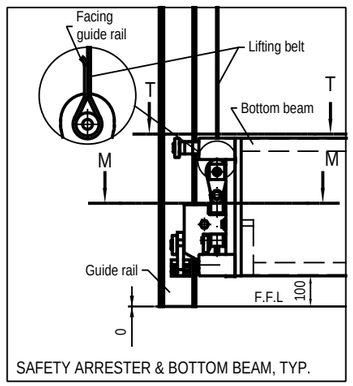

SAFETY ARRESTER & BOTTOM BEAM, TYP.

DOOR IDENTITY NUMBER: 84470001

PARTS LIST, ref. to drwng. no. 69426.XLS

LOAD DIAGRAM & NOTES, ref. to drwng. no. 69425

SECTIONS, ref. to drwng. no. 69428

PLAN VIEWS, ref. to drwng. no. 69427

Stated tightening torque refers to dry screw and nut, unless noted otherwise, and a torque wrench with max. tolerance of ±5%. At re-check, the tightening torque must be within ±25% of stated torque.

DESIGNED KCL
CODE 84470
ITEM NO
DATE 2019-10-09
ASSA ABLOY

SIZE A1 SCALE 1:50

If not otherwise stated:
Tolerances ISO 2768-m EN ISO 13920-B
Cutting class ISO 9013-442
Weld class ISO 5817-C
Surface finish Smooth raw surface

Nihva Poonawalla
India
Megadoor 20000 x 7000
Assembly drawing, Elevation

DRAWING NO 69426
REVISION --
PLOTDATE

This document is the property of ASSA ABLOY Entrance Systems AB and shall not be reproduced or copied, the contents published to a third party or used for any other unauthorized purpose.

Electrical

35							
34							
33	1	Set of cables					
32	1	Control panel					

Additional equipment

31	1	Stabilisation kit		Wire L= 6000		66079	

Installation

30	1	Installation manual					
29	2	Belt attachment kit, Building				19150735	
28	2	Pulley box belt attachment kit				19150715	
27							

Side jamb related

26							
25							
24	4	Washer	HB 200	BRB 10.5x22		19200200	0,0046
23	4	Screw	Cl. 8.8	M6S 10x50		19200435	0,038
22	4	Locking lug				19113128	0,57
21	8	Parallel pin	SMS 2374	CP 5x40 A2		19200363	
20	6	Tension pin	SMS 1663	FRP 6x10 A2		19200373	
19	48	Screw		M6SF-GF 8x20 zib		19200233	0,035
18	56	Screw		M6SF-GF 10x30 zib		19200455	0,065
17	1	Set of guide rails & seal angles				69439	167

Header box related

16							
15							
14	18	Nut		M6M 12		19200225	0,016
13	18	Washer		S4B 13,5x40x4		19200210	0,074
12	18	Washers		50x35x5 d=14		19146368	0,063
11	18	Washer	HB200	BRB 13x24		19200333	
10	18	Screw	Cl. 8.8	M6S 12x70 h		19203176	0,074
9	18	Beam clamp	Lindapter	B 12P3777 M12		19203066	0,138
8							
7	1	Header box				69429	1154

Bottom beam

6	1	Bottom beam				69436	1216

Door leaf related


5							
4	22	Washer		S4B 13,5x40x4 fzv		19200210	0,074
3	22	Screw	Cl. 8.8	M6S 12x80h fzv		19201041	0,09
2							
1	1	Door leaf				69432	1430
item	**qty**	**description**	**material**	**dimension**		**drwng.no /art.no**	**weight kg/pc.**

Nihva Poonawalla
India
Megadoor 20000 x 7000
Parts list no. 69426.xls
Ref. to assembly no. 69426-69428.dwg


Date: 2019-10-09
Project no: 84470
Designed by: KCL
Revision: --

Total weight (kg): 3985


Door identity number **84470001**
Quantity of identical doors: **1**

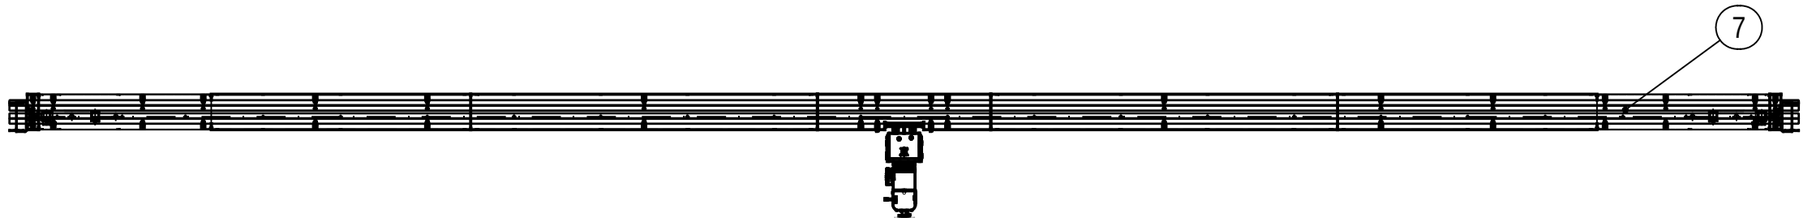


SECTION A-A

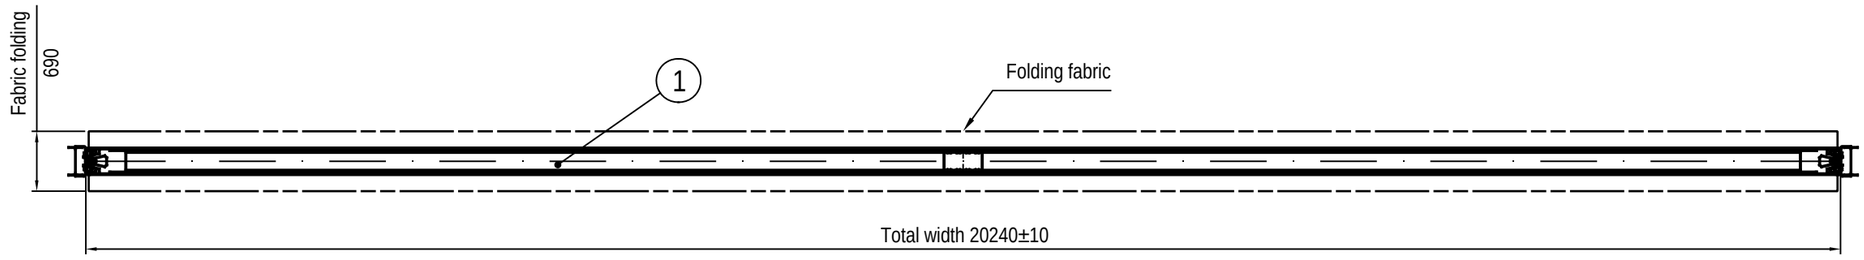


SECTION B-B

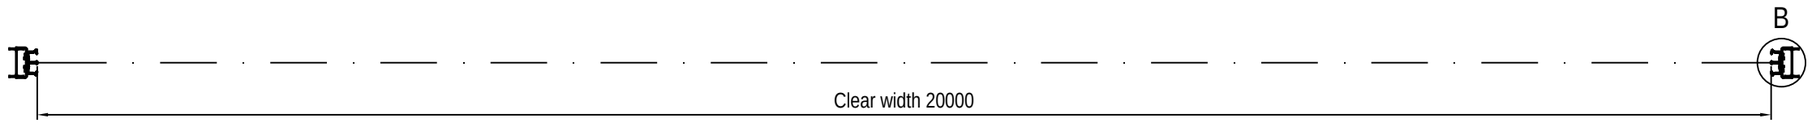

SECTION C-C

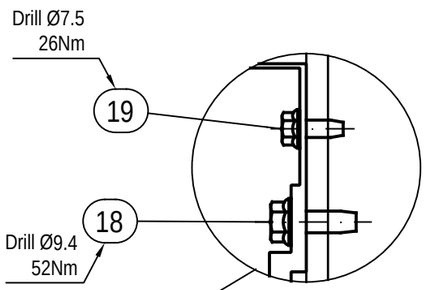

DETAIL C, SCALE (1:2)

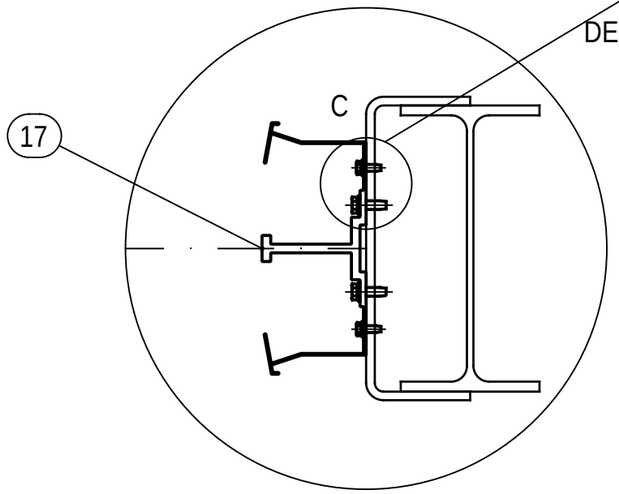

DETAIL B, SCALE (1:5)

DOOR IDENTITY NUMBER: 84470001

PARTS LIST, ref. to drwng. no. 69426.XLS

LOAD DIAGRAM & NOTES, ref. to drwng. no. 69425


SECTIONS, ref. to drwng. no. 69428

ELEVATION, ref. to drwng. no. 69426


Stated tightening torque refers to dry screw and nut, unless noted otherwise, and a torque wrench with max. tolerance of ±5%. At re-check, the tightening torque must be within ±25% of stated torque.

DESIGNED KCL		SIZE A2	SCALE 1:50
CODE 84470	If not otherwise stated:	Nihva Poonawalla	
ITEM NO	Tolerances ISO 2768-m EN ISO 13920-B	India	
DATE 2019-10-09	Cutting class ISO 9013-442	Megadoor 20000 x 7000	PLOT DATE
ASSA ABLOY	Weld class ISO 5817-C	Assembly drawing, Plan views	
	Surface finish Smooth raw surface	DRAWING NO 69427	REVISION --


This document is the property of ASSA ABLOY Entrance Systems AB and shall not without our written permission be copied, imparted to a third party or used for any other unauthorized purpose.

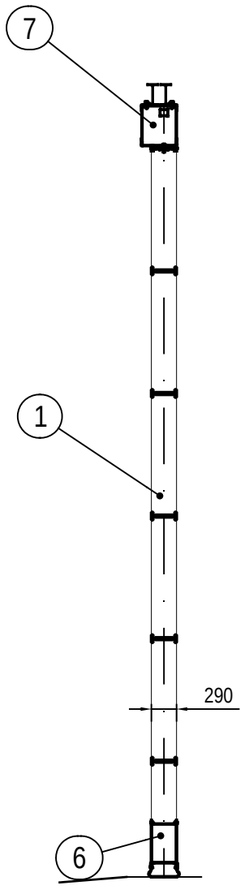


SECTION D-D

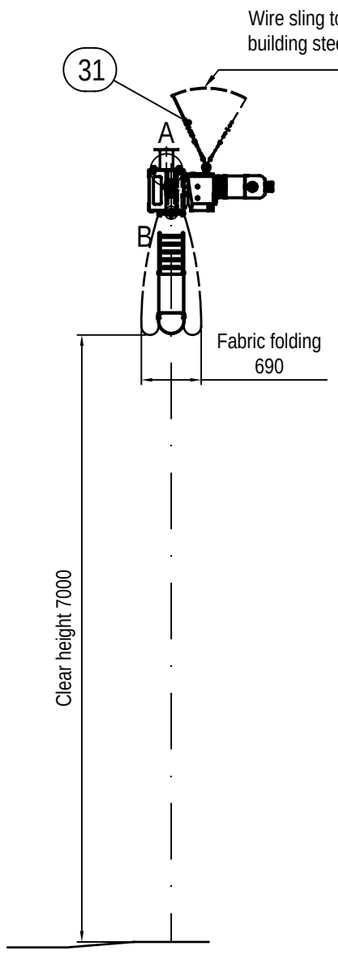


SECTION E-E

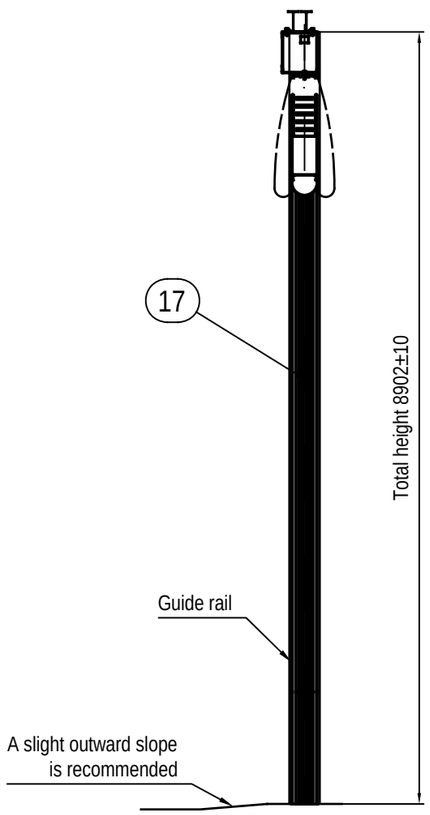


SECTION F-F

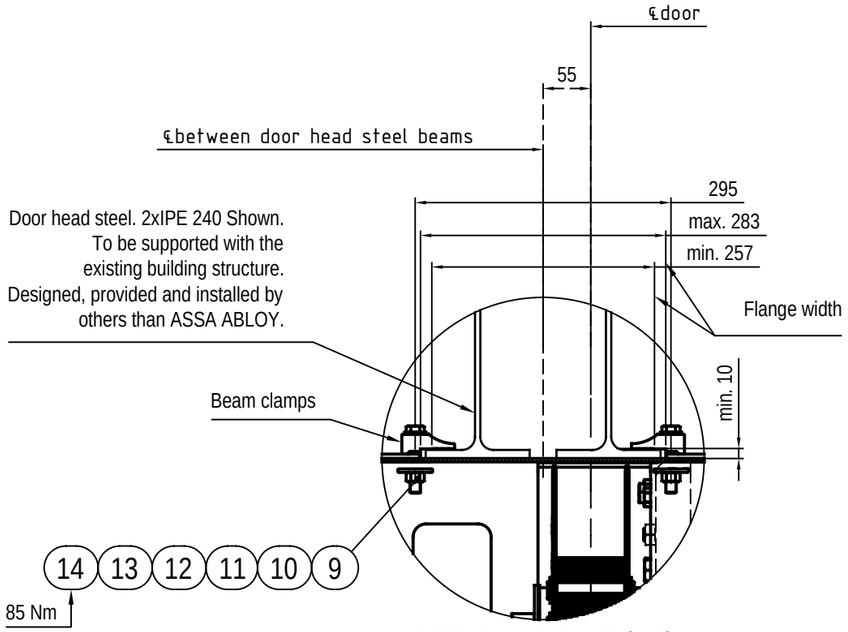


DETAIL A, SCALE (1:5)

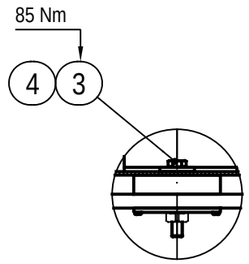

DETAIL B, SCALE (1:5)

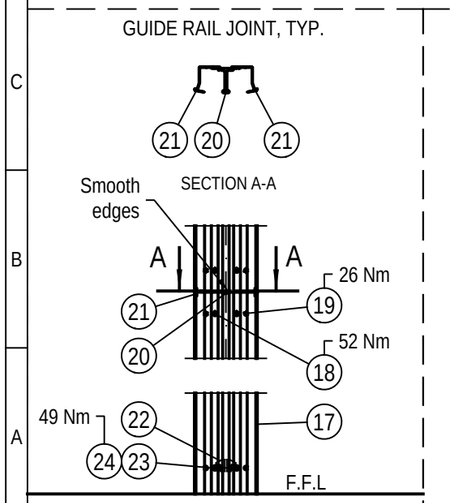

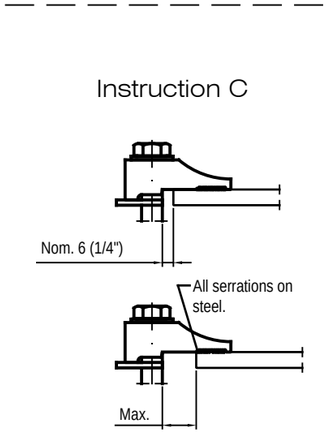

DOOR IDENTITY NUMBER: 84470001

PARTS LIST, ref. to drwng. no. 69426.XLS

LOAD DIAGRAM & NOTES, ref. to drwng. no. 69425

ELEVATION ref. to drwng. no. 69426

PLAN VIEWS, ref. to drwng. no. 69427

Stated tightening torque refers to dry screw and nut, unless noted otherwise, and a torque wrench with max. tolerance of ±5%. At re-check, the tightening torque must be within ±25% of stated torque.

DESIGNED KCL		SIZE A2	SCALE 1:50
CODE 84470	If not otherwise stated:		
ITEM NO	Tolerances ISO 2768-m EN ISO 13920-B		
DATE 2019-10-09	Cutting class ISO 9013-442		
ASSA ABLOY	Weld class ISO 5817-C		
	Surface finish Smooth raw surface		

Nihva Poonawalla
India
Megadoor 20000 x 7000
Assembly drawing, Sections


PLOT DATE

DRAWING NO 69428


REVISION --

This document is the property of ASSA ABLOY Entrance Systems AB and shall not without our written permission be copied, imparted to a third party or used for any other unauthorized purpose.


For installation in building using Drive unit as hoisting equipment see drawing 50737

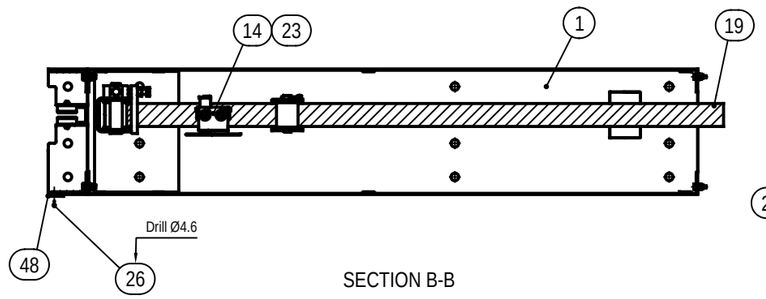


SECTION B-B

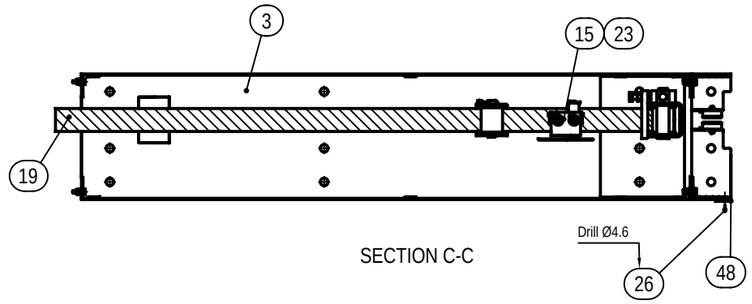


SECTION C-C

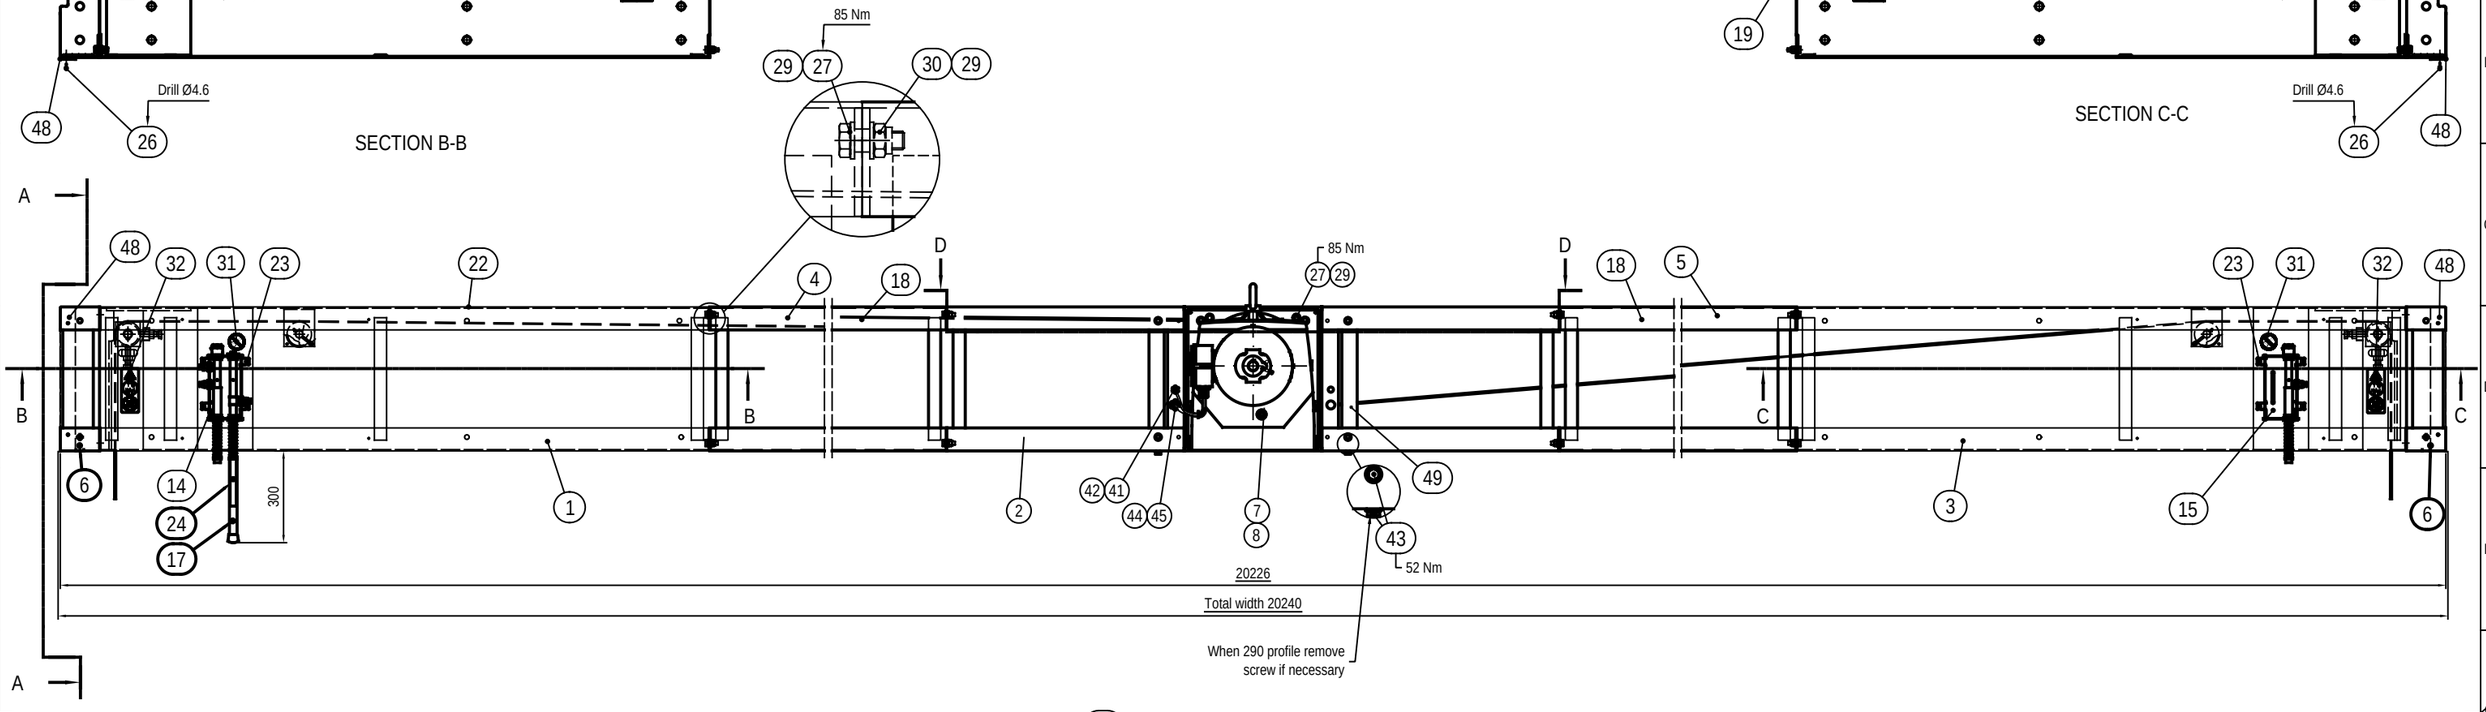


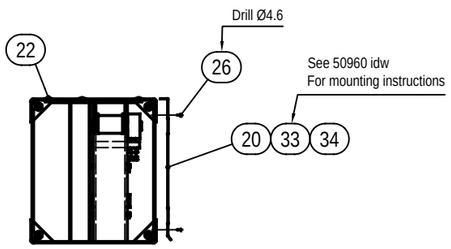

View A-A

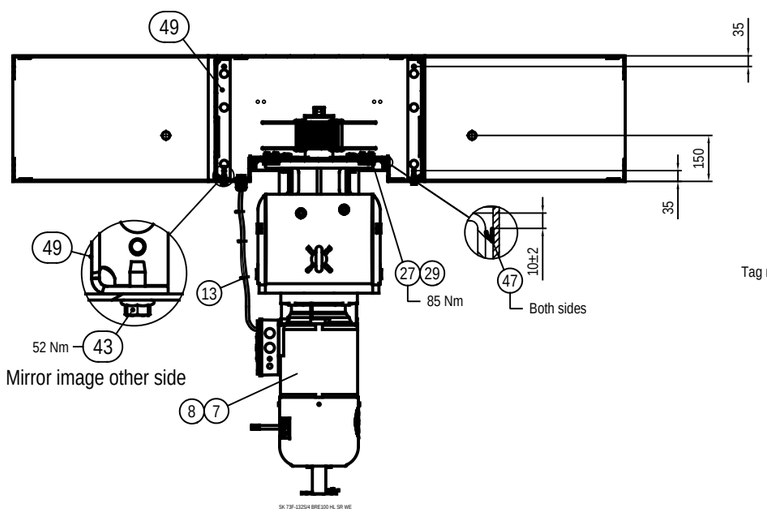

SECTION D-D

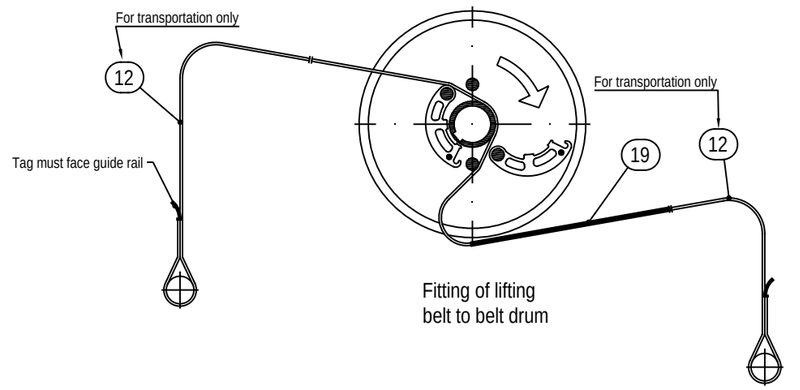

Fitting of lifting
belt to belt drum

PARTS LIST ACC. 69429.xls

DESIGNED KCL	APPROVED	SIZE A1	SCALE 1:10
CODE 84470		If not otherwise stated:	
ITEM NO		Tolerances ISO 2768-m EN ISO 13920-B	
DATE 2019-10-08		Cutting class ISO 9013-442	
ASSA ABLOY		Weld class ISO 5817-C	
		Surface finish Smooth raw surface	

Nihva Poonawalla
India
Megadoor 20000 x 7000
Header box, assembly

DRAWING NO 69429
REVISION --
PLOTDATE


This document is the property of ASSA ABLOY Entrance Systems AB and may not be copied or otherwise reproduced or disclosed to a third party or used for any other unauthorized purpose.

item	qty	description	material	dimension	remarks	art.no. /drawing no.	weight kg/pc.
56							
55							
54							
53							
52							
51							
50							
49	2	Reinforcement				19151167	0,4
48	2	Cover plate for header box				19150432	0,4
47	2	Sealing strip			L=440 mm	19203387	
46							
45	1	Cable fitting		M25x1.5	E 14 761 64 long	19203425	
44	1	Nut		M25x1.5	E 14 765 34	19203396	
43	8	Screw		M6SF-GF 10x25 zib		19202544	
42	1	Nut		M16x1.5	E 14 765 32	19203395	
41	1	Cable fitting		M16x1.5	E 14 761 61 long	19203394	
40							
39							
38							
37							
36							
35							
34	10	Metal trim	Covered motor-side		L= 2000	19150937	5,0
33	2	Metal trim	Covered motor-side		L= 1070	19150985	2,0
32	2	Warning, prohibition & mandatory sign				19150935	
31	2	Caution sign				19102180	
30	24	Nut		M6M 12 ISO 4032-8		19200225	0,0166
29	56	Washer	HB200	BRB 13x24	fzv	19200333	0,005
28							
27	32	Screw	Class 8.8	M6S 12x35	fzv	19200812	0,0532
26	76	Screw		MRT-GF 5x12		19201960	
25							
24	1	Screw		RTS TX 4.8x19	geomet	19200327	
23	8	Screw		MRT-GF 6x16	zib	19200452	0,0062
22							
21							
20	2	Sticker, Megadoor / ASSA ABLOY				19200836	
19	1	Lifting belt		75/80RV	L=41000	19202657	13,2
18	2	Intermediate frame, 4m			Installation holes: Top	60095	142,4
17	1	Extension tube				19151017	0,33
16							
15	1	Limit switch box, Right				19150901	1,5
14	1	Limit switch box, Left				19150900	1,7
13	30	Cable tie		4,8x188		19200190	
12	6	Cable tie		4,8x368		19200192	
11							
10							
9							
8	1	Motor				19204987	
7	1	Drive unit	Nord SK73F-132S/4	i=124.17		19151164	308
6	2	Header box extension		L=128		19150440	12,9
5	1	Intermediate frame, Right	355 MCD	L=2992	Installation holes: Top	69431	107
4	1	Intermediate frame, Left	355 MCD	L=2992	Installation holes: Top	69430	107
3	1	Pulley frame, Right				19150930	92
2	1	Motor frame				19150272	65
1	1	Pulley frame, Left				19150928	92


Nihva Poonanwalla
Pune
Megadoor
Header box
Parts list 69429.xls
Ref. to assembly drawing no. 69429

Total weight (kg): 1154


Date: 2019-10-09
Project no.: 84470
Designed: KCL
Revision: --

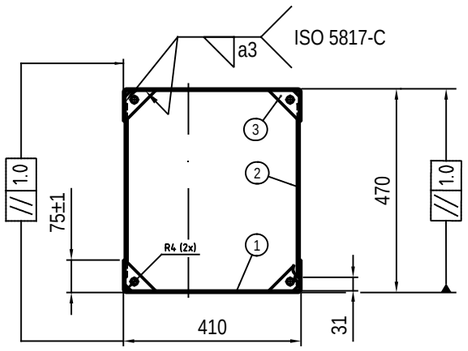


VIEW B-B

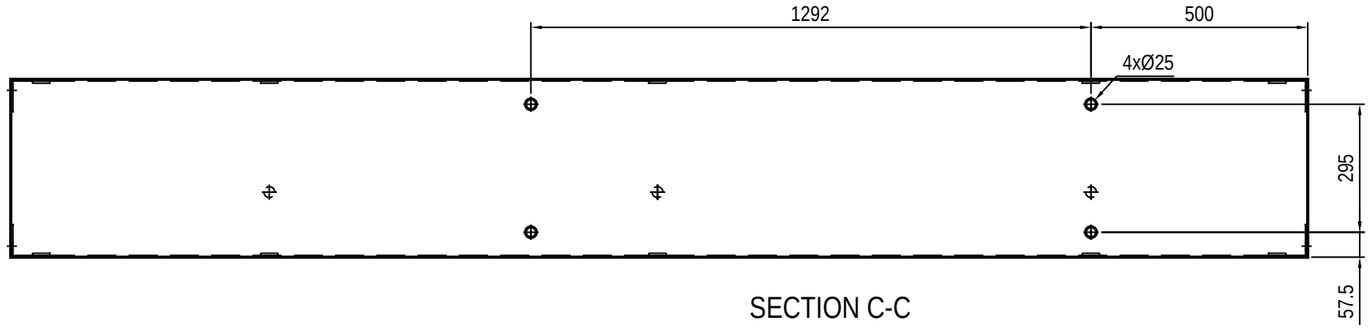

SECTION C-C

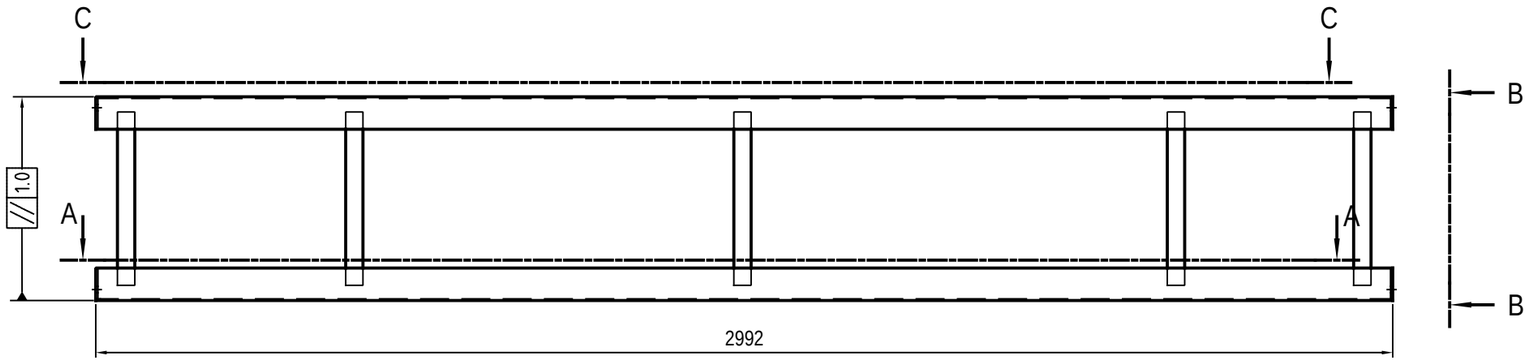

VIEW FROM MOTOR SIDE

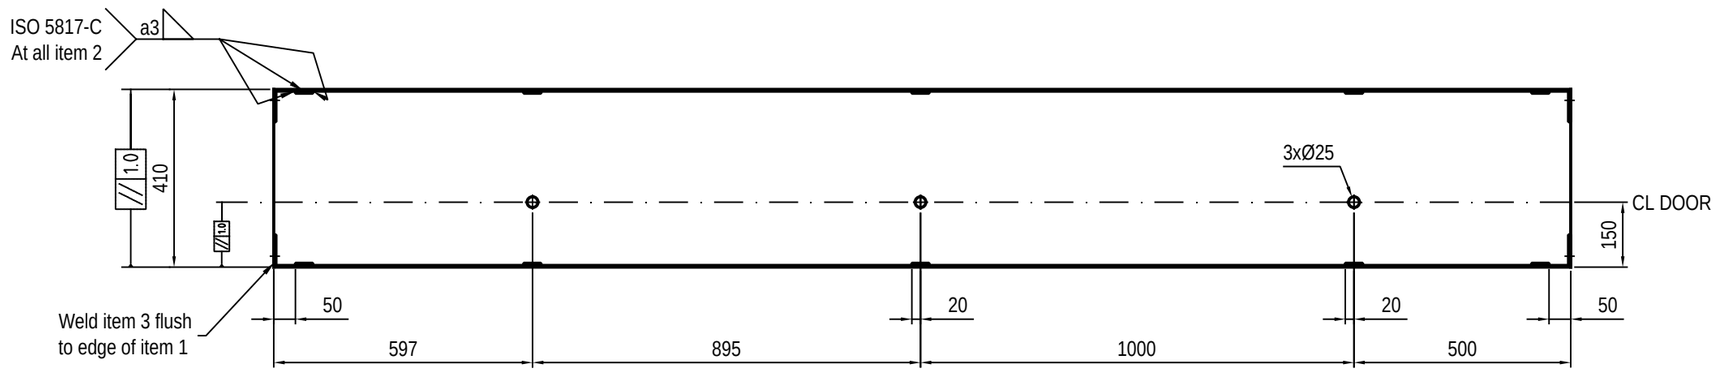

SECTION A-A

ITEM	QTY	DESCRIPTION	DIMENSION	MATERIAL	REMARKS	kg/pc
3	8	Attachment plate			A4-50329	
2	10	Flat bar	400x40x5	S236JRG2	19202157	
1	2	U-profile	2992x75x410x75, T=4	355 MCD	19203264	

Re(min) = 220 MPa, Rm(min) = 360 MPa

Surface treatment area = 230 dm²/m
Weight = 35,6 kg/m

Surface treatment: See order specification

Tolerance according to ISO 2768-m and SS-EN ISO 13920 unless otherwise specified.

Surface smoothness unless otherwise specified: alt. 25

DESIGNED: KCL

CODE: 84470

ITEM NO:

DATE: 2019-10-09

ASSA ABLOY

SIZE: A2 | SCALE: 1:10

If not otherwise stated:
Tolerances: ISO 2768-m, EN ISO 13920-B
Cutting class: ISO 9013-442
Weld class: ISO 5817-C
Surface finish: Smooth raw surface

Nihva Poonawalla

India

Megadoor 20000 x 7000


Intermediate frame, left

PLOT DATE


DRAWING NO: 69430

REVISION


This document is the property of ASSA ABLOY Entrance Systems AB and shall not without our written permission be copied, imparted to a third party or used for any other unauthorized purpose.

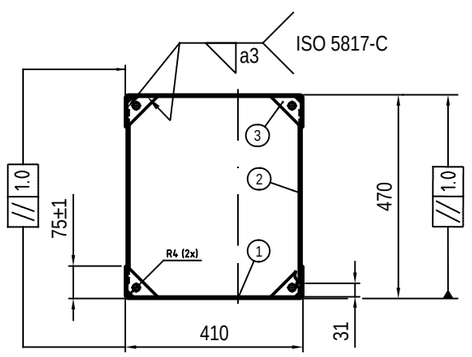


VIEW B-B

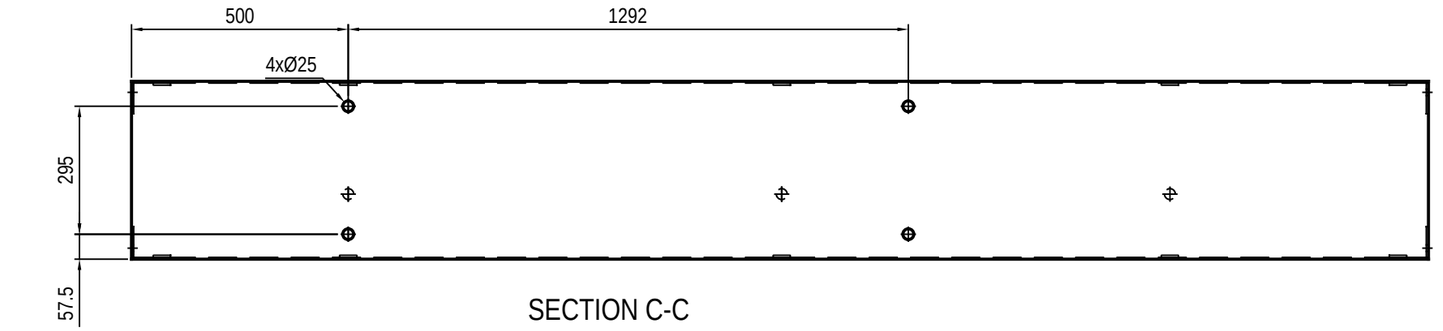

SECTION C-C

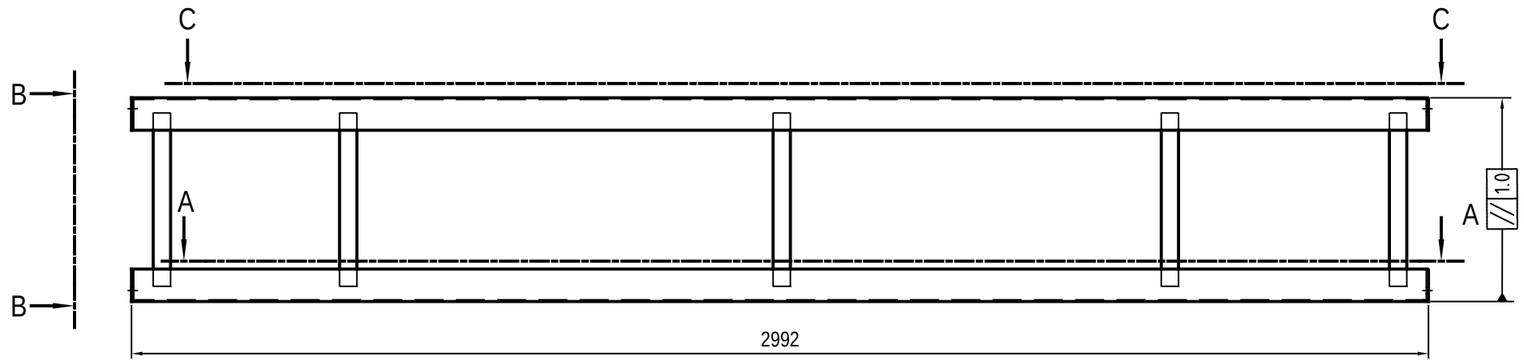

VIEW FROM MOTOR SIDE

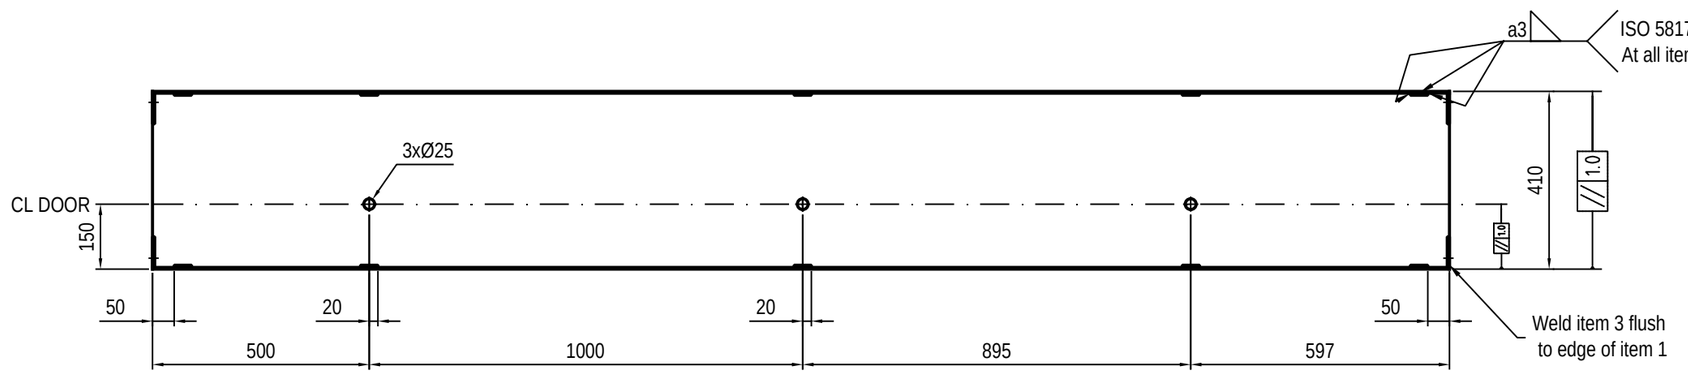

SECTION A-A

ITEM	QTY	DESCRIPTION	DIMENSION	MATERIAL	REMARKS	kg/pc
3	8	Attachment plate			A4-50329	
2	10	Flat bar	400x40x5	S236JRG2	19202157	
1	2	U-profile	2992x75x410x75, T=4	355 MCD	19203264	

Re(min) = 220 MPa, Rm(min) = 360 MPa

Surface treatment area = 230 dm²/m
Weight = 35,6 kg/m

Surface treatment: See order specification

Tolerance according to ISO 2768-m and SS-EN ISO 13920 unless otherwise specified.

Surface smoothness unless otherwise specified: alt. 25

DESIGNED: KCL
CODE: 84470
ITEM NO:
DATE: 2019-10-09
ASSA ABLOY

SIZE: A2
SCALE: 1:10


If not otherwise stated:
Tolerances: ISO 2768-m, EN ISO 13920-B
Cutting class: ISO 9013-442
Weld class: ISO 5817-C
Surface finish: Smooth raw surface


Nihva Poonawalla
India
Megadoor 20000 x 7000
Intermediate frame, right


PLOT DATE


DRAWING NO: 69431
REVISION: ---


This document is the property of ASSA ABLOY Entrance Systems AB and shall not without our written permission be copied, imparted to a third party or used for any other unauthorized purpose.

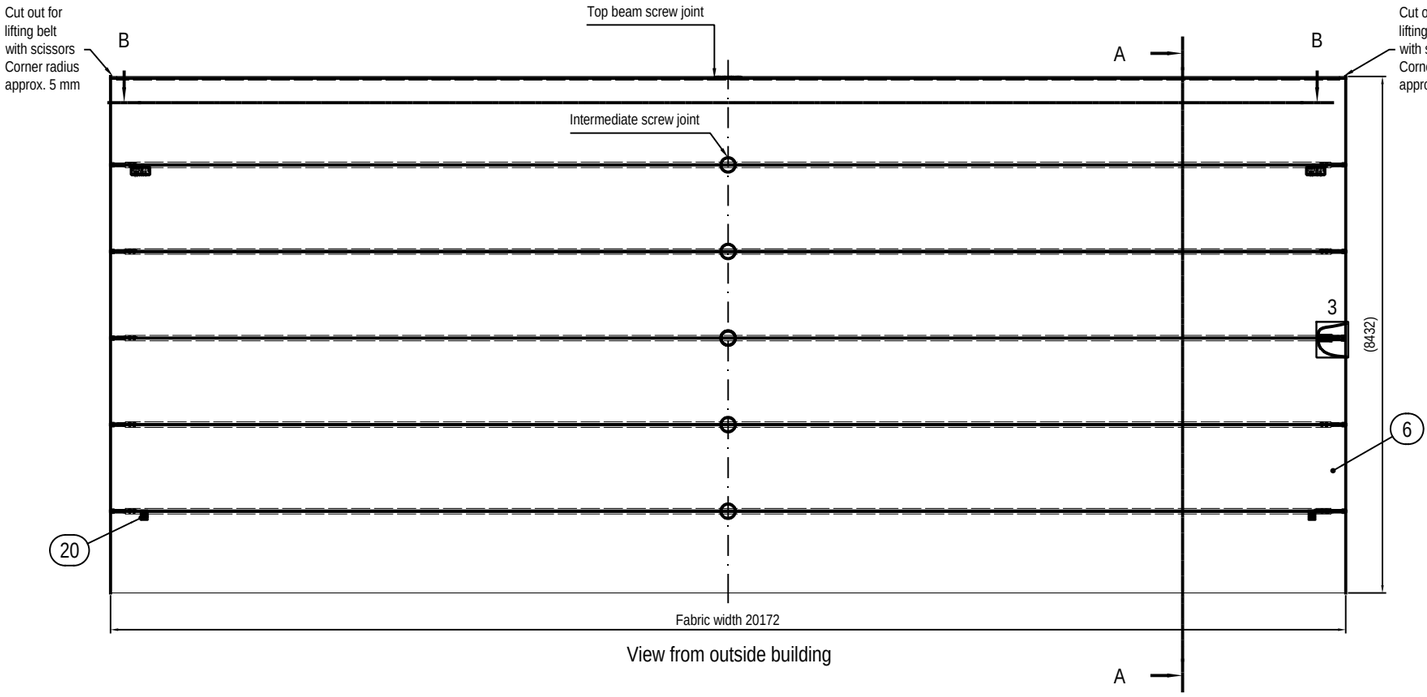


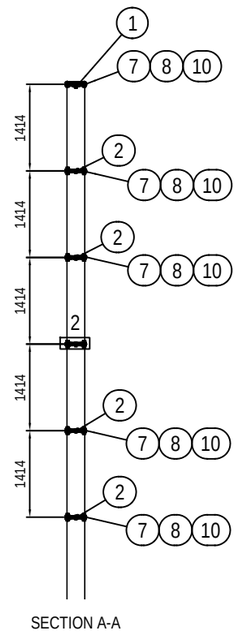


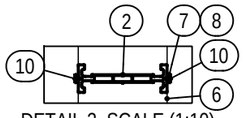

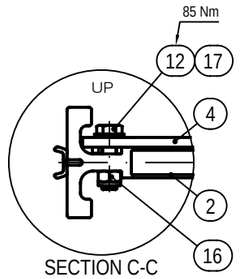


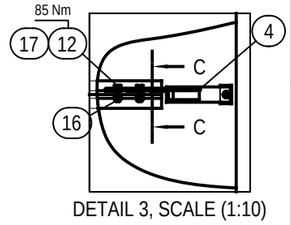

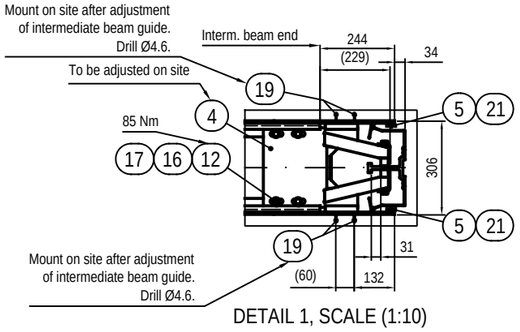


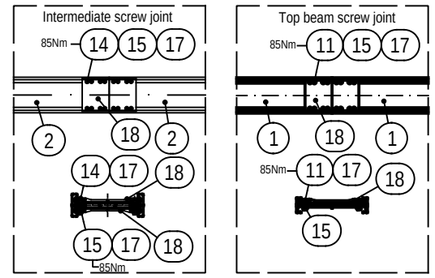



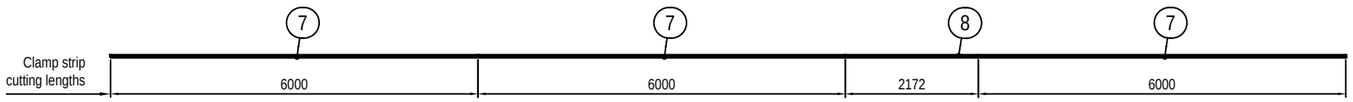

Cut out in door fabric at each end of top beam for guide rail and belt penetration.
All cuts must be done with scissors.
Make sure cut outs have radius corners as shown.

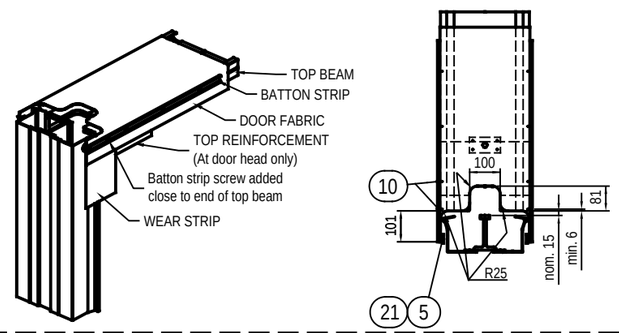

PARTS LIST, ref. to drwng 69432.xls

Stated tightening torque refers to dry screw and nut, unless noted otherwise, and a torque wrench with max. tolerance of ±5%. At re-check, the tightening torque must be within ±25% of stated torque.

DESIGNED	KCL
CODE	84470
ITEM NO	
DATE	2019-10-08
SIZE	A1
SCALE	1:50
If not otherwise stated:	
Tolerances	ISO 2768-m EN ISO 13920-B
Cutting class	ISO 9013-442
Weld class	ISO 5817-C
Surface finish	Smooth raw surface

Nihva Poonawalla
India
Megadoor 20000 x 7000
Door leaf, Assembly

DRAWING NO 69432
REVISION --
PLOTDATE

This document is the property of ASSA ABLOY Entrance Systems AB and shall not be reproduced or copied without permission. It is not to be communicated or disclosed or exploited to a third party or used for any other unauthorized purpose.

Item	Qty	Description	Material	Dimension	Remarks	Drawing/ art.no.	Weight kg/pc.
29							
28							
27							
26							
25							
24							
23							
22							
21	24	Screw		RTS TX 4.8x13		19200242	0,00
20	1	Door leaf signs			Placed as shown on drawing A2-23486	19123486	
19	40	Screw	ZIB	MRT-GF 5x16	Mount on site	19200263	
18	11	Splice plate	AA 6005-T6	440x266		19162369	4,3
17	216	Washer	HB200	BRB 13x24		19200333	0,005
16	40	Nut	BH8	M12 DIN 985		19203172	0,017
15	96	Nut	BH 8	M6M 12		19200225	0,016
14	80	Screw	Cl. 8.8	M6S 12x60		19201680	0,06
13							
12	40	Screw	Cl. 8.8	M6S 12x45		19203177	0,051
11	16	Screw	Cl. 8.8	M6S 12x35		19200812	0,051
10	1610	Screw	Cl. 8.8	RTS TX5.5x16		19204942	0,00
9							
8	12	Painted Clamp strip Alt. 2		L= 2172	Grey (RAL7004)	51119	0,6
7	36	Painted Clamp strip Alt. 2		L= 6000	Grey (RAL7004)	51119	1,7
6	1	Door fabric	(W=20232 L=18000) Ordering	W=20172 L=17154 Finished dimension		69435	260
5	24	Protective stud		Dia.20x10		19100902	
4	10	Intermediate beam guide				19113002	12
3							
2	5	Intermediate beam		290x90	L=19685	69434	261
1	1	Top beam		290x60	L=19970	69433	135

Om Megadoor logo 65803 19165803

Om ventilerade mellanprofiler


Color: BLUE (NCS S3560-R80 19101367
Color: GREEN (NCS 8010-G1(19101625
Color: GREY (NCS 3500, RAL 19101368
Color: RED (NCS S2070-R, RA 19101366
Color: TAN (NCS 2010-Y40R, 19201446
Color: Translucent white 19202970
Color: WHITE (NCS 0500, RAI 19101369
Color: YELLOW (NCS S0570-Y 19202929

Antracite grey (RAL7016)	Painted Clamp strip Alt. 2	51124	Antracite grey (RAL7016)	51134
Blue (RAL5005)	Painted Clamp strip Alt. 2	51118	Blue (RAL5005)	51128
Custom color:	Painted Clamp strip Alt. 2	51125	Custom color:	51136
Green (RAL6009)	Painted Clamp strip Alt. 2	51123	Green (RAL6009)	51133
Grey (RAL7004)	Painted Clamp strip Alt. 2	51119	Grey (RAL7004)	51129
Red (RAL3001)	Painted Clamp strip Alt. 2	51117	Red (RAL3001)	51127
Standard	Clamp strip	19151078	Standard	19151087
Tan (RAL1001)	Painted Clamp strip Alt. 2	51121	Tan (RAL1001)	51131
White (RAL9016)	Painted Clamp strip Alt. 2	51120	White (RAL9016)	51130
Yellow (RAL1003)	Painted Clamp strip Alt. 2	51122	Yellow (RAL1003)	51132


Nihva Poonawalla
India
Megadoor 20000 x 7000
Door leaf assembly
Parts list no. 69432.xls
Ref. to assembly drawing no. 69432

Date: 2019-10-09
Project no: 84470
Designed by: KCL
Revision: ---


Total weight (kg): **1430**

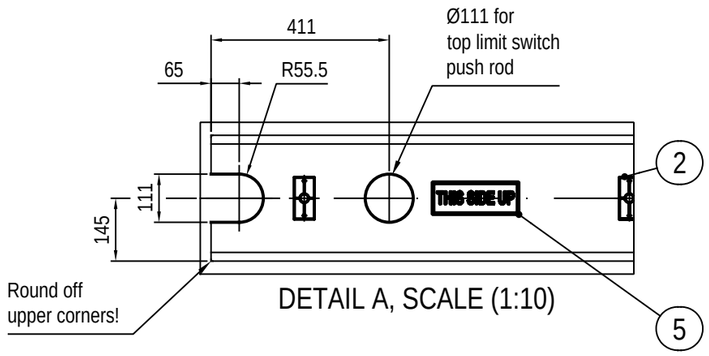


DETAIL A, SCALE (1:10)

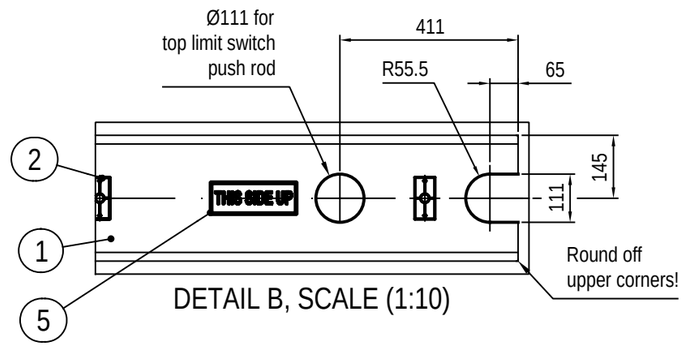


DETAIL B, SCALE (1:10)

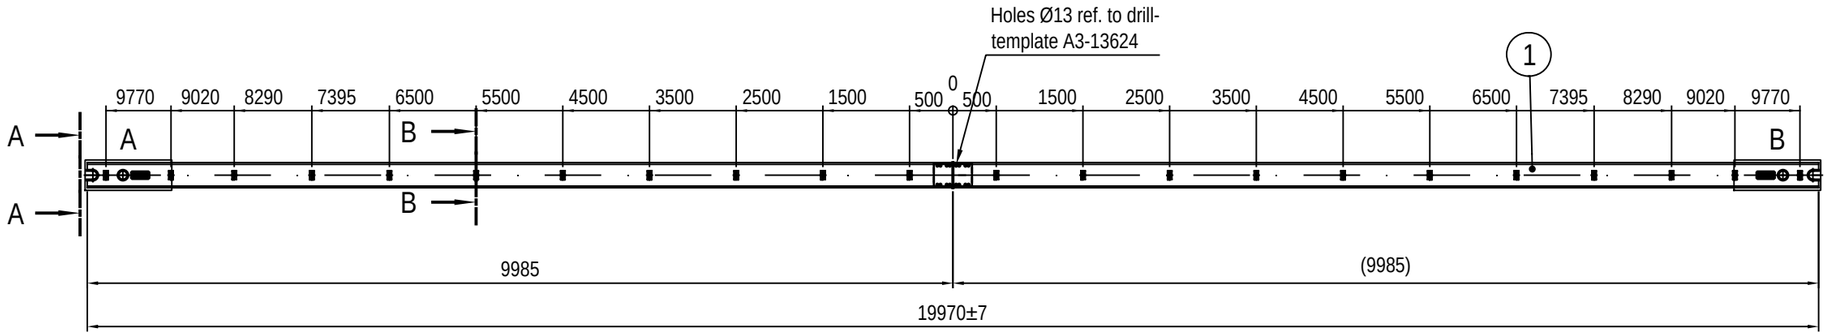

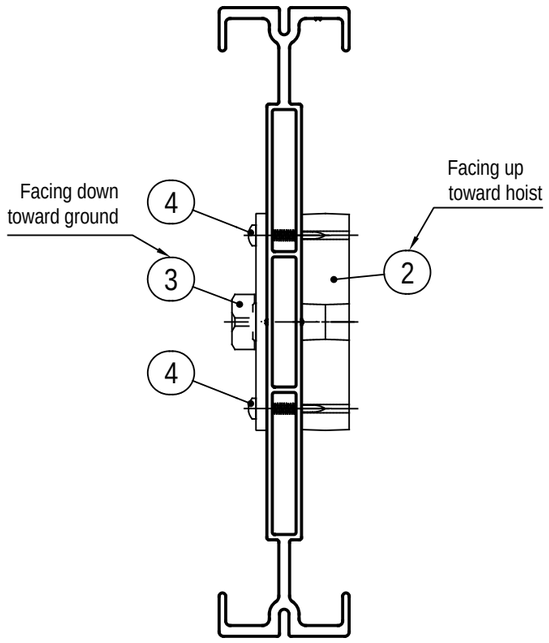

A - A Scale 1:2

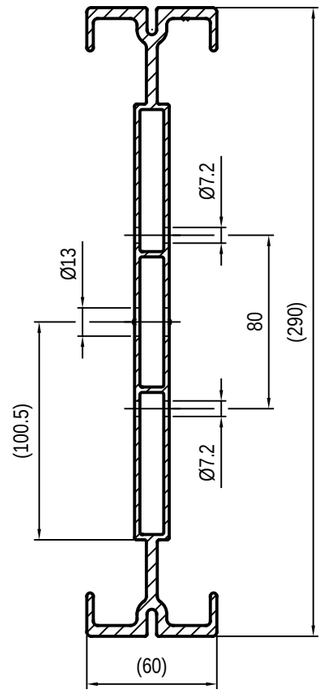

B - B Scale 1:2
Hole drilling typ. @ all
spacers & nut plates

Weight: 135 kg.


ITEM	QTY	DESCRIPTION	DIMENSION	MATERIAL	REMARKS	kg/pc
5	2	Sign	200 x 75		19150987	
4	44	Screw	RTS TX 4,8x38		19203815	
3	22	Nut plate			19113194	0.3
2	22	Spacer			19123449	
1	2	Profile 290x60	L= 9985	6005-T6	19162359	64.0


DESIGNED: KCL
CODE: 84470
ITEM NO:
DATE: 2019-10-08
SIZE: A2
SCALE: 1:50
If not otherwise stated:
Tolerances: ISO 2768-m, EN ISO 13920-B
Cutting class: ISO 9013-442
Weld class: ISO 5817-C
Surface finish: Smooth raw surface
ASSA ABLOY

Nihva Poonawalla
India
Megadoor 20000 x 7000
Top beam


PLOT DATE
DRAWING NO: 69433
REVISION: --

This document is the property of ASSA ABLOY Entrance Systems AB and shall not without our written permission be copied, imparted to a third party or used for any other unauthorized purpose.

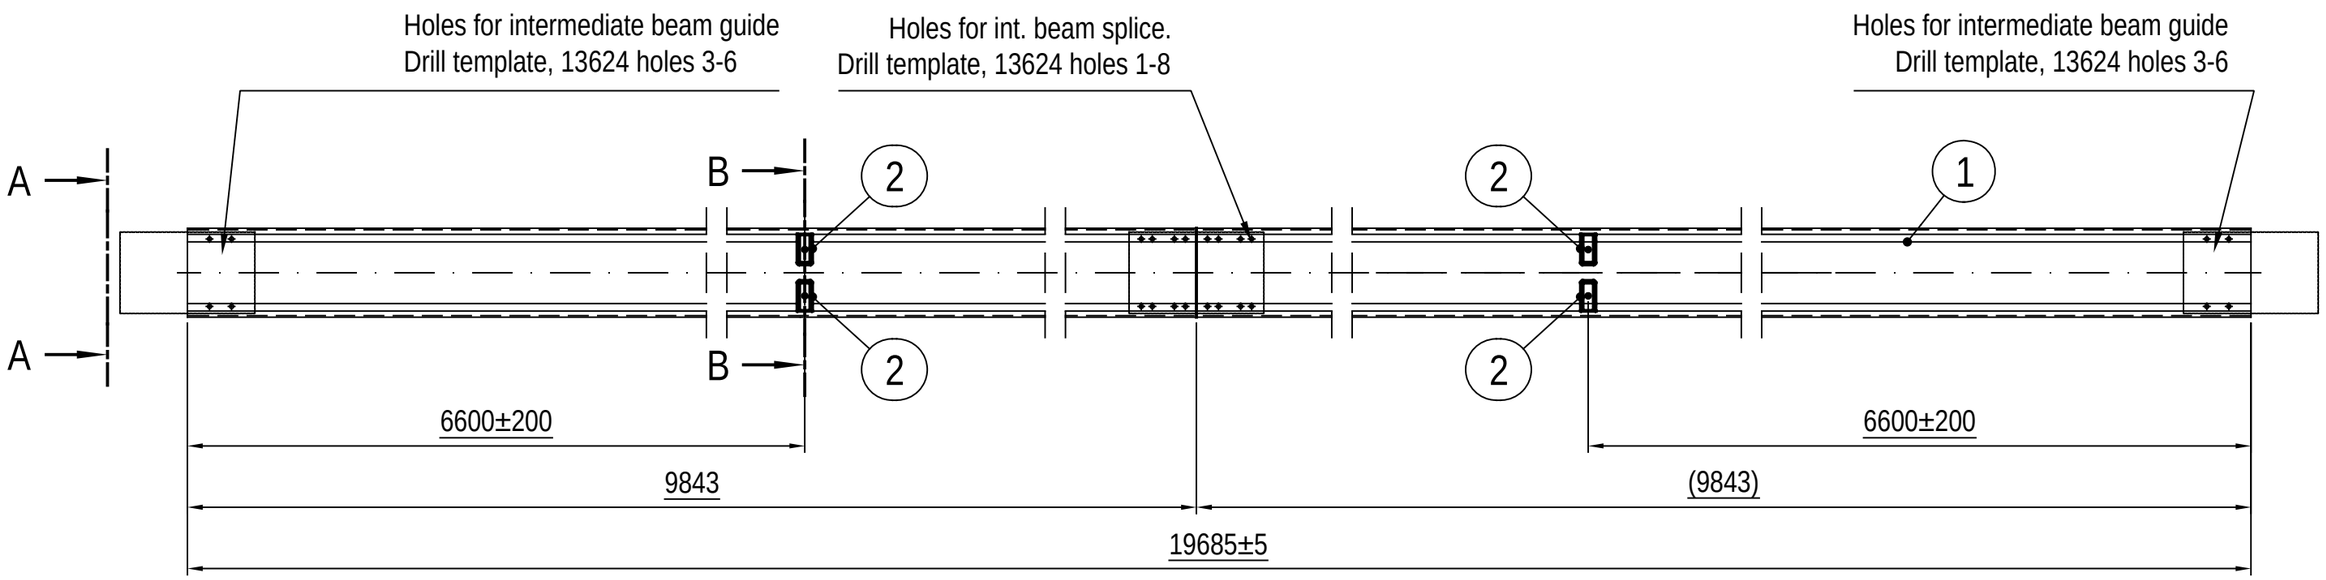

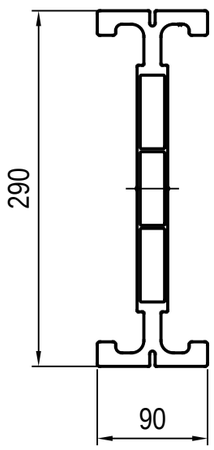

A - A Scale 1:5

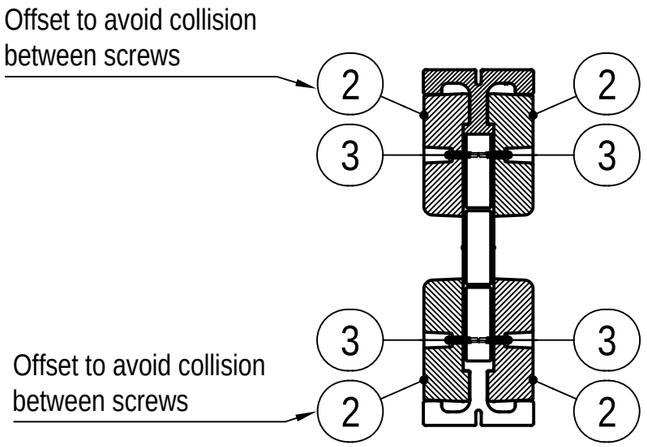

B - B Scale 1:5

Weight= 261 (kg)
Weight= 13.217 (kg/m)

ITEM	QTY	DESCRIPTION	DIMENSION	MATERIAL	REMARKS	kg/pc
3	8	Screw	RTB ST4.8x22		19202674	
2	8	Spacer			19134315	0.1
1	2	Profile 290x90	L= 9843	6005-T6	19162361	130.1

DESIGNED: KCL
SIZE: A3
SCALE: 1:20
CODE: 84470
ITEM NO:
DATE: 2019-10-08

If not otherwise stated:
Tolerances
ISO 2768-m
EN ISO 13920-B
Cutting class
ISO 9013-442
Weld class
ISO 5817-C
Surface finish
Smooth raw surface

ASSA ABLOY

Nihva Poonawalla

India

Megadoor 20000 x 7000


Intermediate beam

PLOT DATE

DRAWING NO: 69434

REVISION: --

This document is the property of ASSA ABLOY Entrance Systems AB and shall not without our written permission be copied, imparted to a third party or used for any other unauthorized purpose.

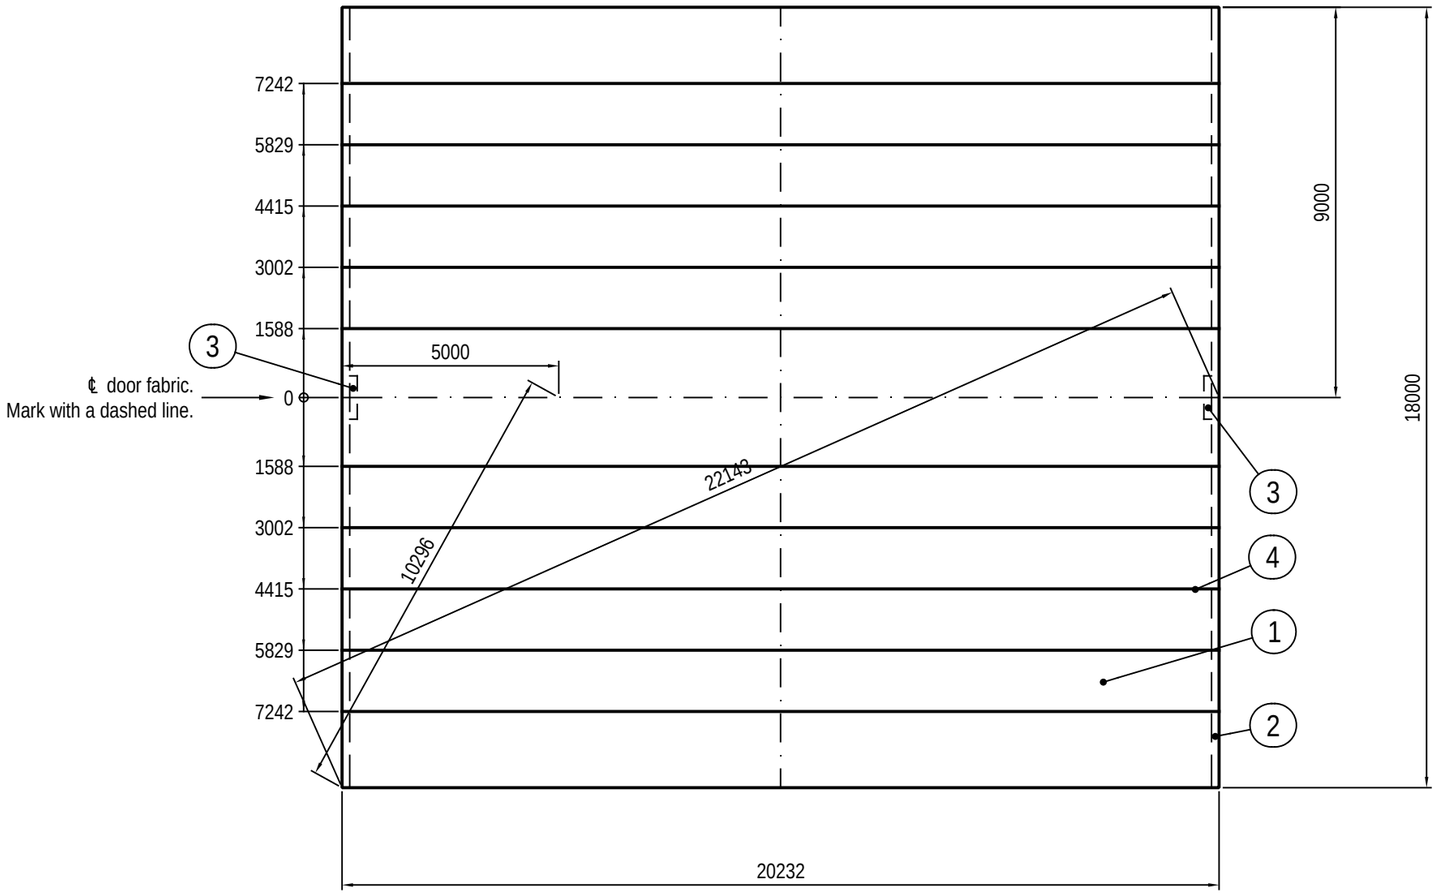

Top reinforcement and wear strip welding acc. to A3-19944

Weight: 260 kg

ITEM	QTY	DESCRIPTION	DIMENSION	MATERIAL	REMARKS	kg/pc
4	10	Scribe line	L=20232		19204697 tape & ink	
3	2	Top reinforcement	W= 175 x L= 1000			0.1
2	2	Wear strip	W= 175 x L= 18000			2.2
1	1	Door Fabric	W= 20232 x L= 18000		Color: Aluminum White	254.9

DESIGNED KCL

SIZE A2 SCALE 1:100

CODE 84470

ITEM NO

DATE 2019-10-08

If not otherwise stated:
Tolerances ISO 2768-m EN ISO 13920-B
Cutting class ISO 9013-442
Weld class ISO 5817-C
Surface finish Smooth raw surface

ASSA ABLOY

Nihva Poonawalla

India

Megadoor 20000 x 7000

Door fabric


PLOT DATE


DRAWING NO 69435


REVISION --

This document is the property of ASSA ABLOY Entrance Systems AB and shall not without our written permission be copied, imparted to a third party or used for any other unauthorized purpose.

DETAIL 3, SCALE (1:4)

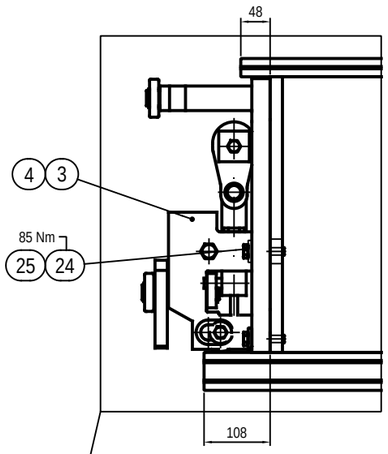

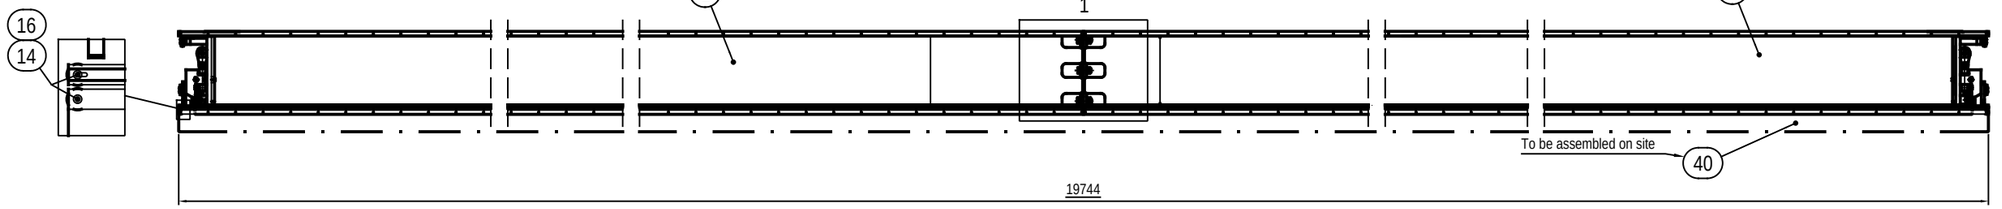


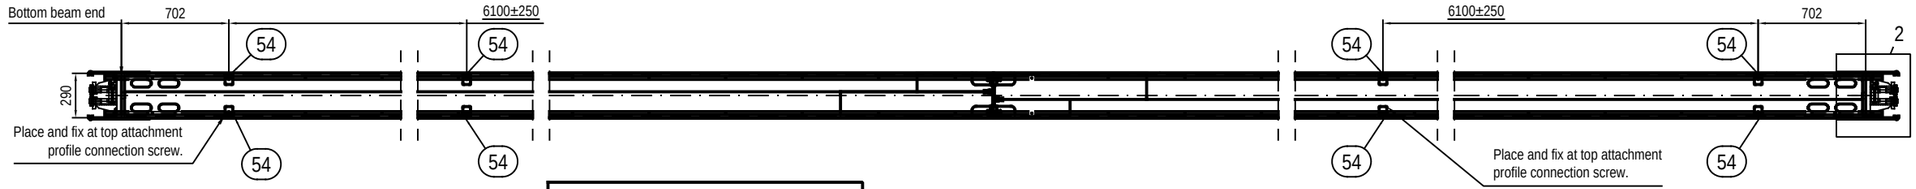


DRILL INSTRUCTIONS
Drill additional holes Ø5.5 thru attachment profiles into bottom beam if distance between bottom beam splice & 1st predrilled hole exceeds 250mm. Drill holes close to joint.

3


BOTTOM BEAM PREPARED FOR TRANSPORTATION
SCALE 1:10

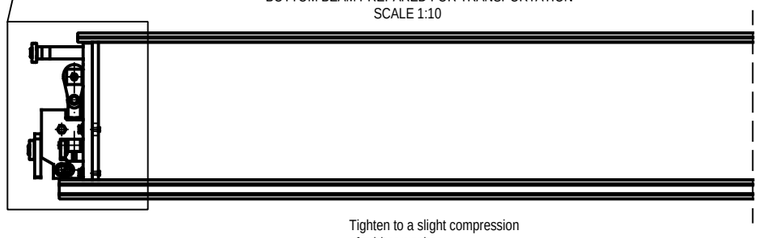

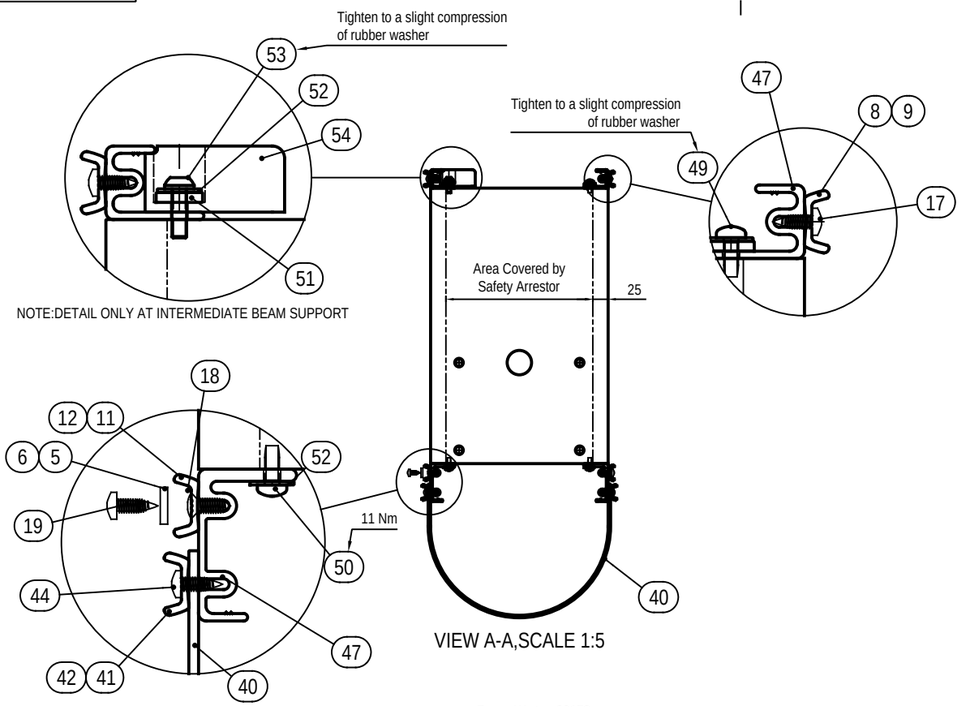


NOTE:DETAIL ONLY AT INTERMEDIATE BEAM SUPPORT

VIEW A-A,SCALE 1:5

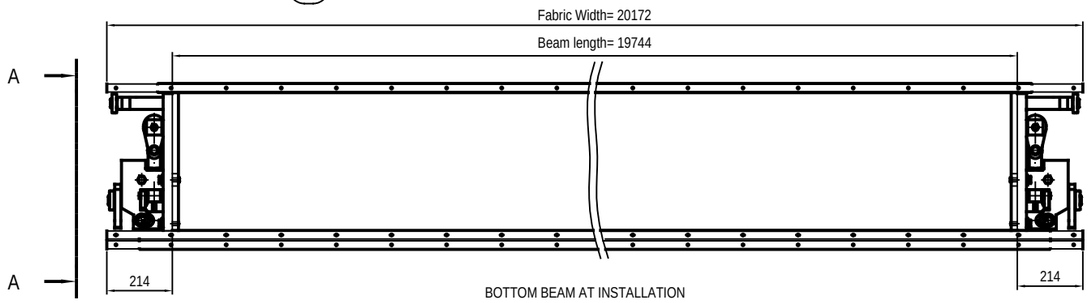


BOTTOM BEAM AT INSTALLATION

SCALE 1:10

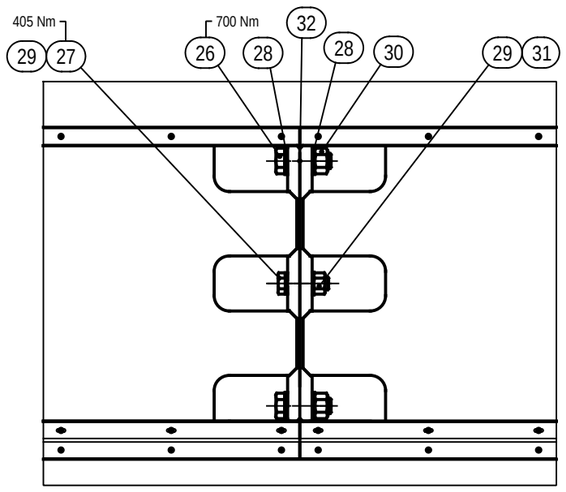

DETAIL 1, SCALE (1:5)

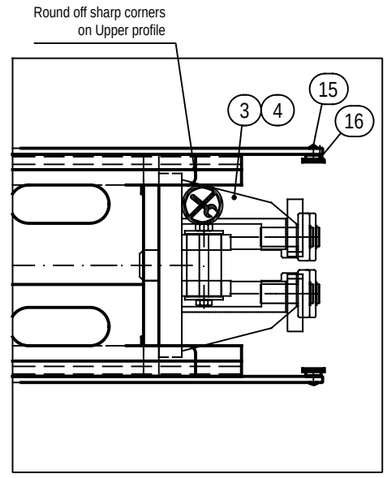

DETAIL 2, SCALE (1:4)

PARTS LIST, ref. to drwng 69436.XLS

Total weight:1144kg

Stated tightening torque refers to dry screw and nut, unless noted otherwise, and a torque wrench with max. tolerance of ±5%. At re-check, the tightening torque must be within ±25% of stated torque.

DESIGNED	KCL
CODE	84470
ITEM NO	
DATE	2019-10-08
SIZE	A1
SCALE	1:20
If not otherwise stated:	
Tolerances	ISO 2768-m EN ISO 13920-B
Cutting class	ISO 9013-442
Weld class	ISO 5817-C
Surface finish	Smooth raw surface

ASSA ABLOY

Nihva Poonawalla
India
Megadoor 20000 x 7000
Bottom beam, assembly

DRAWING NO 69436

REVISION --

PLOTDATE

This document is the property of ASSA ABLOY Entrance Systems AB and shall not be reproduced or disclosed to a third party or used for any other unauthorized purpose.

Attachment profile related

54	6	Int. Beam support				19162433	0,08	Minst 4, 1 i varje hörn på ovansidan, Max 8m delning
53	6	Screw		MRT-GF 6x20		19200324	0,0066	
52	86	Washer		RB 6,4 x 18 x 1,5		19200203	0,0015	
51	6	Washer, rubber				19130693	0,0014	
50	80	Screw		MRT-GF 6x16		19200452	0,006	**Radera hela rubriken om**
49	74	Screw sat.				19145476	0,0	**ej infästningsprofiler används**
48								
47	1	Set of clamp strip attachment profiles				69438	167	
46								

Bottom seal related

45							
44	269	Screw		RTS TX 5.5x19	Geomet	19204943	0,00
43							ied
42	2	Clamp strip		30x6 #2	L= 2172	19151078	0,6
41	6	Clamp strip		30x6 #2	L= 6000	19151078	1,7
40	1	Rubber seal	600 EPDM Grey	4x600	L= 20172 Finished Dimension	19203299	68,7

Bottom beam related

39							
38							
37							ied
36							
35							
34							
33							
32	1	Shims for bottom beam screw joint				19128506	
31	2	Nut	Class 8.8	M6M 20		19201687	0,053
30	4	Nut	Class 8.8	M6M 24		19203273	0,073
29	4	Washer	HB 200	21x36 t=3		19200202	0,011
28	8	Washer	HB 200	25x45 t=4		19203274	0,016
27	2	Screw	Class 8.8	M6S 20x70		19203191	0,22
26	4	Screw	Class 8.8	M6S 24x75		19203422	0,3
25	8	Washer		TBRSUB 13x36		19200211	0,041
24	8	Screw	Class 8.8	M6S 12x50		19201681	0,055
23							
22							
21							
20							
19	269	Screw		RTS TX 5.5x19		19204943	0,00
18	269	Screw		KFTS S.5x16		19204944	0,00
17	269	Screw		RTS TX 5.5x16		19204942	0,00
16	12	Protective stud		Dia.20x10		19100902	
15	4	Screw		RTS TX 4.8x13		19200242	0,00
14	8	Screw		RTS TX 4.8x16		19200320	0,00
13							
12	2	Clamp strip		30x6 #3	L= 2172	19151079	0,6
11	6	Clamp strip		30x6 #3	L= 6000	19151079	1,7
10							
9	2	Clamp strip	Grey (RAL7004)	30x6 #2	L= 2172	19151078	0,6
8	6	Clamp strip	Grey (RAL7004)	30x6 #2	L= 6000	19151078	1,7
7							
6	2	Clamp strip		15x3 #1	L= 2172	19151077	0,3
5	6	Clamp strip		15x3 #1	L= 6000	19151077	0,7
4	2	Link			Belt	19122916	7
3	2	Safety arrester				19123814	50
2							
1	2	Bottom beam half		L= 9872	290x450	69437	409
Item	**Qty**	**Description**	**Material**	**Dimension**	**Remarks**	**Drawing/ art.no.**	**Weight kg/pc.**

Screw splice screws

				M6S 12x50	19201681		0,0546	
M12x85 för BB T=2				M6S 12x85	19201223		0,0654	
	8	Clamp strip support				19112596	0,2	Använd vid klämlistskruvar direkt i Bottenbalk (ex.mellanbottenbalk)
	16	Screw	Class 8.8	M6S 6x10		19203178	0,004	Använd vid klämlistskruvar direkt i Bottenbalk (ex.mellanbottenbalk)

1	Shims for bottom beam screw joint			19128506	
2	Nut	Class 8.8	M6M 20	19201687	0,053
4	Nut	Class 8.8	M6M 24	19203273	0,073
4	Washer	HB 200	21x36 t=3	19200202	0,011
8	Washer	HB 200	25x45 t=4	19203274	0,016
2	Screw	Class 8.8	M6S 20x70	19203191	0,22
4	Screw	Class 8.8	M6S 24x75	19203422	0,3

1000 EPDM Grey	4x1000	19203303	1000
1000 ESBR56SHTS14	4x1000	19201527	1000
1100 EPDM Grey	4x1100	19203304	1100
1100 ESBR56SHTS14	4x1100	19203076	1100
400 EPDM Grey	4x400	19203296	400
400 ESBR56SHTS14	4x400	19203069	400
450 EPDM Grey	4x450	19203297	450
450 ESBR56SHTS14	4x450	19203083	450
500 EPDM Grey	4x500	19203298	500
500 ESBR56SHTS14	4x500	19200512	500
600 EPDM Grey	4x600	19203299	600

Wire

Band eller vajer dimension?	19122910	20 mm
	19122911	16 mm
	19122912	14 mm
	19122913	11&12 mm
	19122914	9&10 mm
	19122915	7 mm
	19122916	Belt


600 ESBR56SHTS14	4x600	19202415	600
700 EPDM Grey	4x700	19203300	700
700 ESBR56SHTS14	4x700	19203035	700
750 ESBR56SHTS14	4x750	19202114	750
800 EPDM Grey	4x800	19203301	800
800 ESBR56SHTS14	4x800	19203062	800
900 EPDM Grey	4x900	19203302	900
900 ESBR56SHTS14	4x900	19203063	900


Nihva Poonawalla
India
Megadoor 20000 x 7000
Bottom beam assembly
Parts list no. 69436.xls
Ref. to assembly drawing no. 69436

Date: 2019-10-08
Project no: 84470
Designed by: KCL
Revision: ---

Total weight (kg): **1216**


Antracite grey (RAL7016)	Painted Clamp strip Alt. 2	51124	Antracite grey (RAL7016)	51134
Blue (RAL5005)	Painted Clamp strip Alt. 2	51118	Blue (RAL5005)	51128
Custom color:	Painted Clamp strip Alt. 2	51125	Custom color:	51136
Green (RAL6009)	Painted Clamp strip Alt. 2	51123	Green (RAL6009)	51133
Grey (RAL7004)	Painted Clamp strip Alt. 2	51119	Grey (RAL7004)	51129
Red (RAL3001)	Painted Clamp strip Alt. 2	51117	Red (RAL3001)	51127
Standard	Clamp strip	19151078	Standard	19151087
Tan (RAL1001)	Painted Clamp strip Alt. 2	51121	Tan (RAL1001)	51131
White (RAL9016)	Painted Clamp strip Alt. 2	51120	White (RAL9016)	51130
Yellow (RAL1003)	Painted Clamp strip Alt. 2	51122	Yellow (RAL1003)	51132

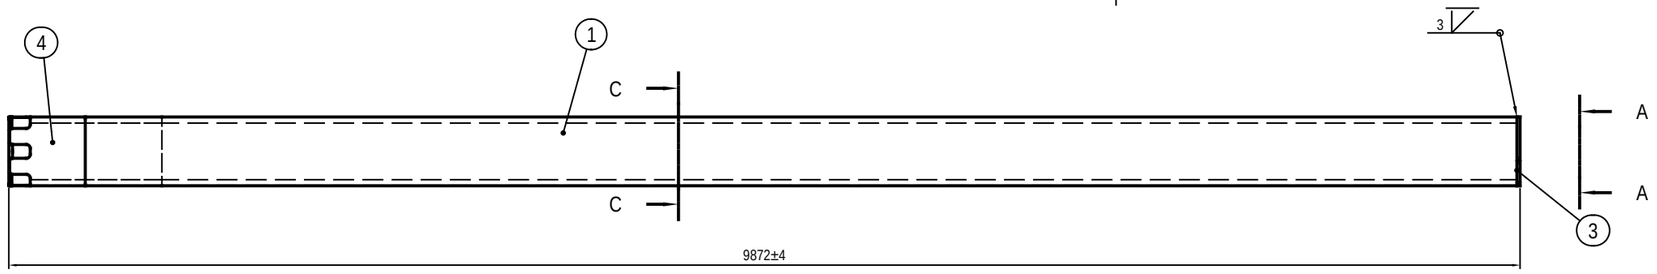

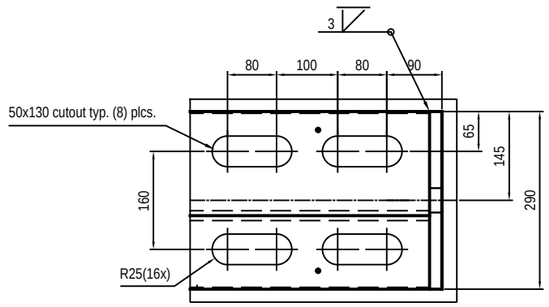



DETAIL A, SCALE (1:5)

HOLE TEMPLATE
Top of Bottom beam

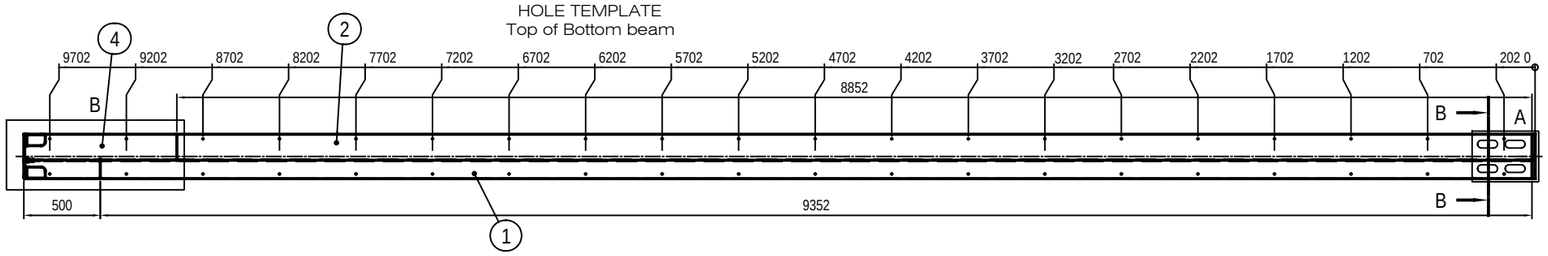


HOLE TEMPLATE
Bottom of Bottom beam

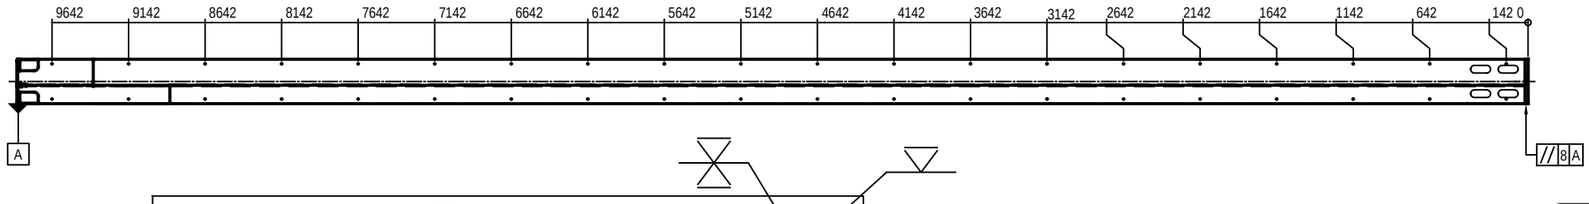


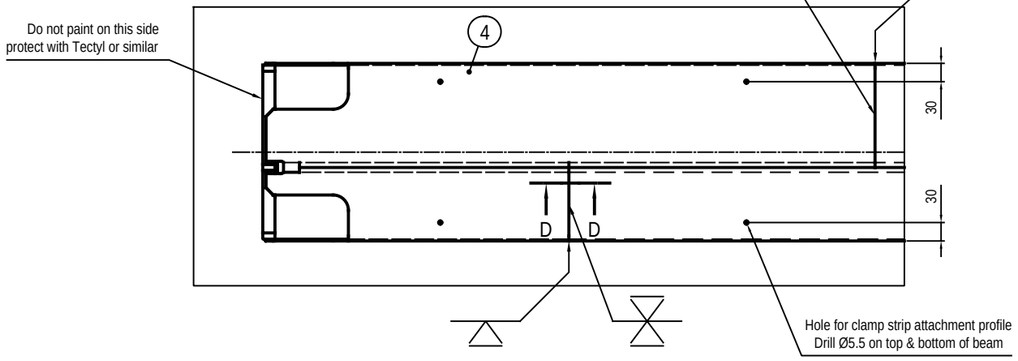

DETAIL B, SCALE (1:5)

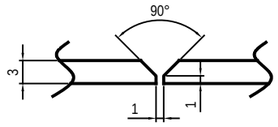


SECTION D-D, SCALE 1:1. Weld prep.

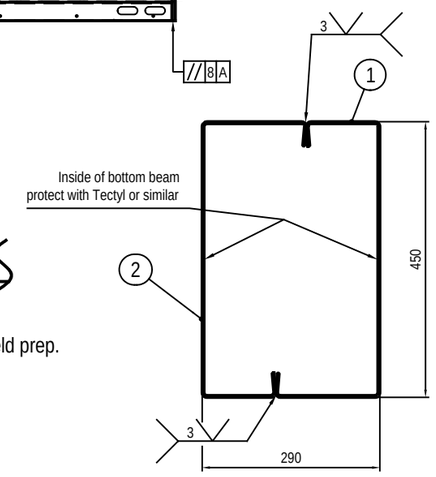

Section C-C
Scale 1:5


Surface treatment:	A4-1500 Standard Color: Light grey (RAL 7047).
Surface treatment area: 1461 dm² Surface treatment area/m: 148.5 dm² Perimeter: 1480 mm Cross section area: 4776 mm² Weight: 409 kg	
Wx = 660 cm3 Zx = 806 cm3 Ix = 14959 cm4	Wy = 460 cm3 Zy = - cm3 Iy = 6668 cm4
Grind all sharp edges and welding sparks after welding. This to prevent fabric wear.	

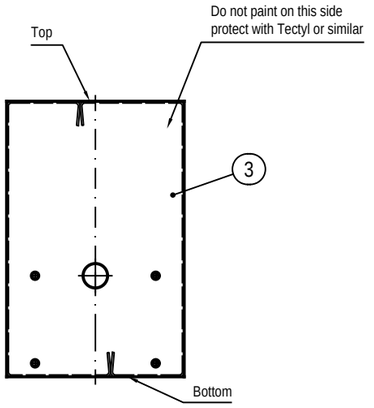

View A-A Scale 1:5



Section B-B
Scale 1:5

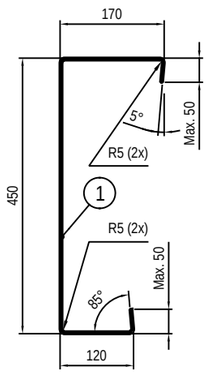

Pos 1 forming layout
Scale 1:5

ITEM	QTY	DESCRIPTION	DIMENSION	MATERIAL	REMARKS	kg/pc
4	1	Screw joint		A1-27101		48.0
3	1	End plate		S355J2+N	A3-28684	20.5
2	1	Plate	Pl 3x795	Re min. 355Mpa	L = 8852	165.7
1	1	Plate	Pl 3x795	Re min. 355MPa	L = 9352	175.0

DESIGNED: FV
SIZE: A1 | SCALE: 1:20
CODE: 84470
ITEM NO:
DATE: 2019-10-08
If not otherwise stated:
Tolerances ISO 2768-m EN ISO 13920-B
Cutting class ISO 9013-442
Weld class ISO 5817-C
Surface finish Smooth raw surface

Nihva Poonawalla

India

Megadoor 20000 x 7000

Bottom beam half


PLOT DATE

DRAWING NO: 69437


REVISION: --


ASSA ABLOY

This document is the property of ASSA ABLOY Entrance Systems AB and shall not be reproduced or used without our permission, be loaned, exhibited to a third party or used for any other unauthorized purpose.

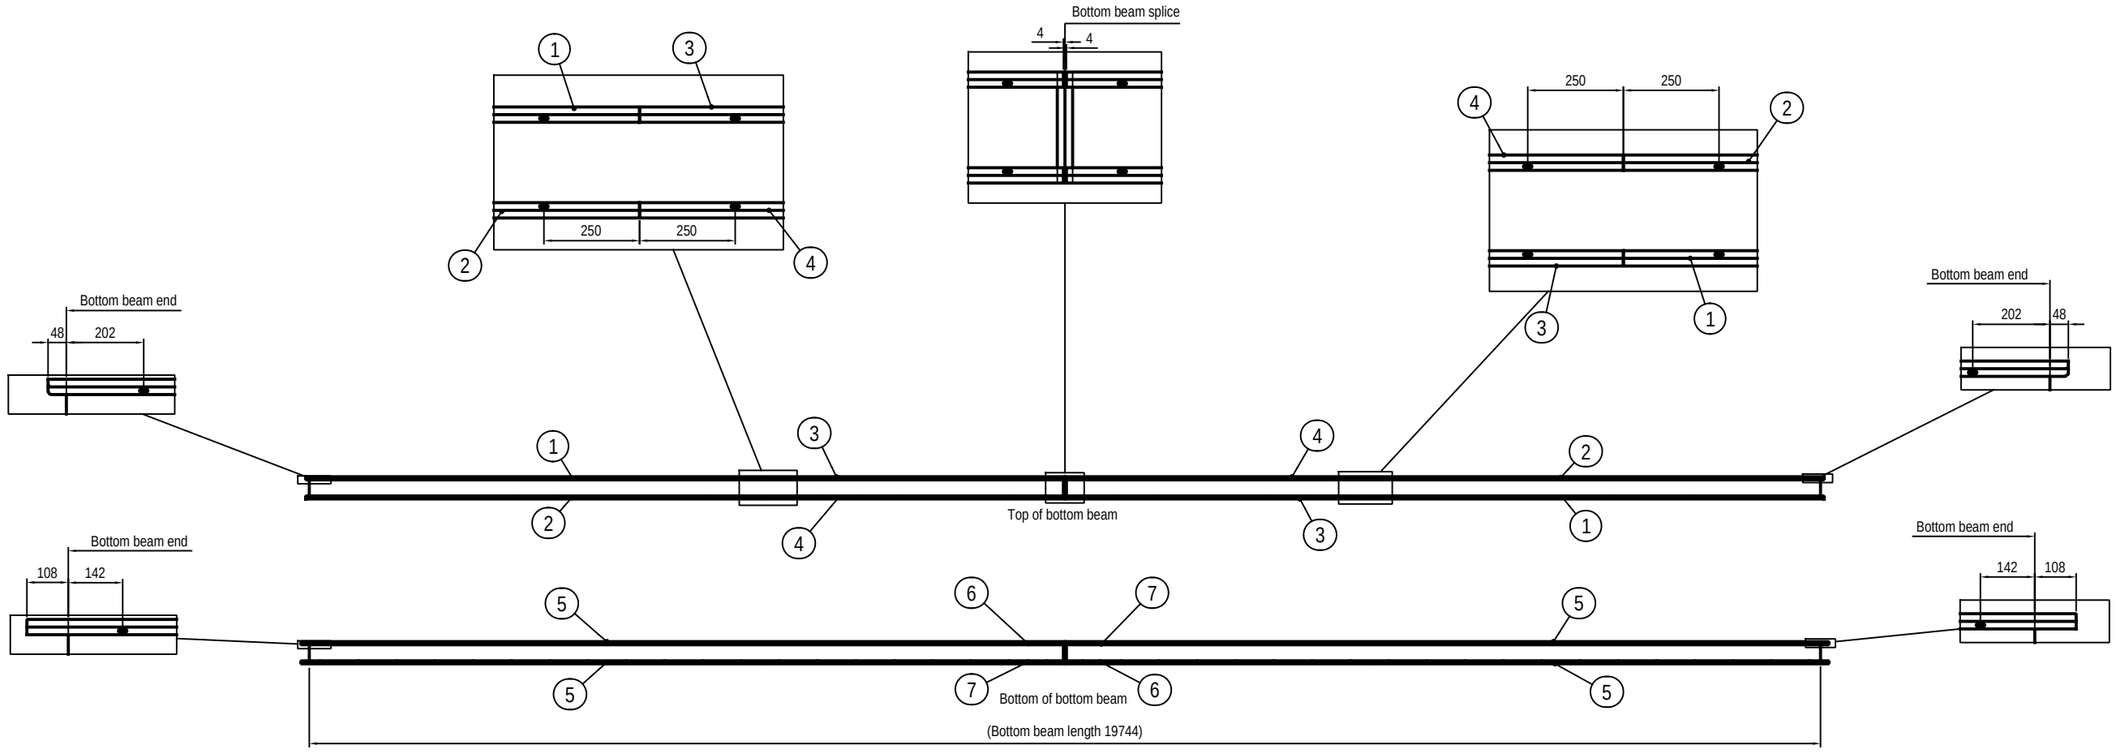

Positioning of clamp strip attachment profiles
Scale 1:40

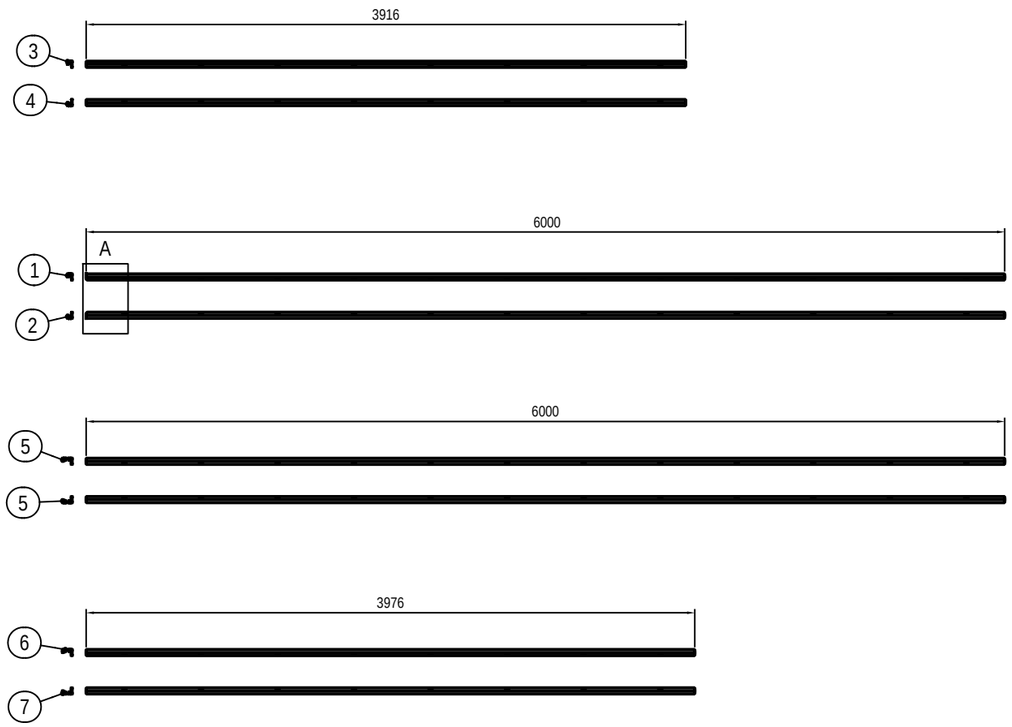

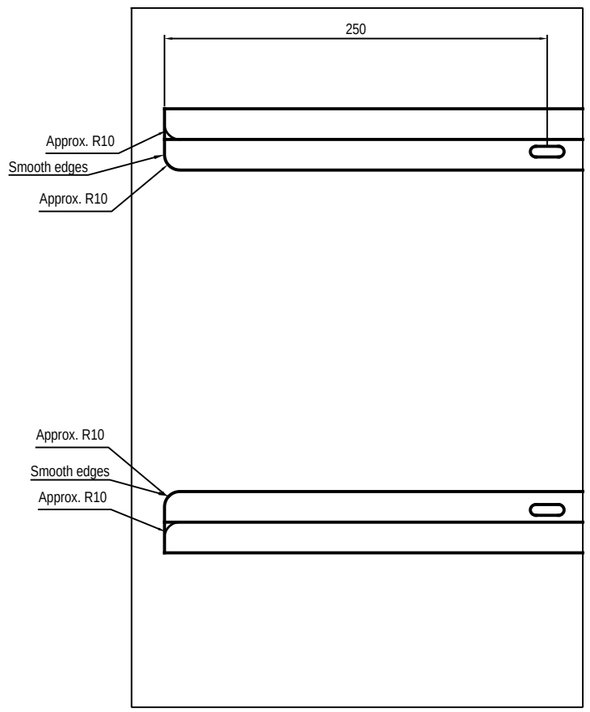

DETAIL A, SCALE (1:2)
Upper profile only
Only one side per profile

Weight: 95 kg

ITEM	QTY	DESCRIPTION	DIMENSION	MATERIAL	REMARKS	kg/pc
7	2	Clamp strip attachment profile, lower	L= 3976		19162431	6.0
6	2	Clamp strip attachment profile, lower	L= 3976		19162431	6.0
5	4	Clamp strip attachment profile, lower	L= 6000		19162431	9.1
4	2	Clamp strip attachment profile, upper	L= 3916		19162430	3.4
3	2	Clamp strip attachment profile, upper	L= 3916		19162430	3.4
2	2	Clamp strip attachment profile, upper	L= 6000		19162430	5.2
1	2	Clamp strip attachment profile, upper	L= 6000		19162430	5.2

DESIGNED: FV
SIZE: A1
SCALE: 1:20
CODE: 84470
ITEM NO
DATE: 2019-10-08
If not otherwise stated:
Tolerances: ISO 2768-m EN ISO 13920-B
Cutting class: ISO 9013-442
Weld class: ISO 5817-C
Surface finish: Smooth raw surface

Nihva Poonawalla

India


Megadoor 20000 x 7000

Clamp strip attachment profiles


ASSA ABLOY


DRAWING NO: 69438
REVISION: --
PLOTDATE


This document is the property of ASSA ABLOY Entrance Systems AB and shall not be reproduced or disclosed to a third party or used for any other unauthorized purpose.

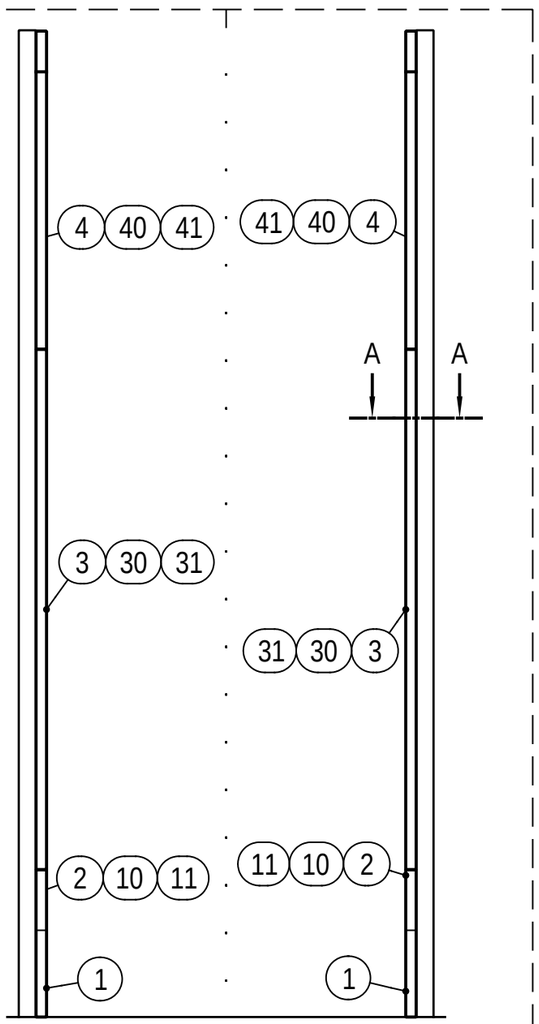

Guide rail location in building
scale 1:50

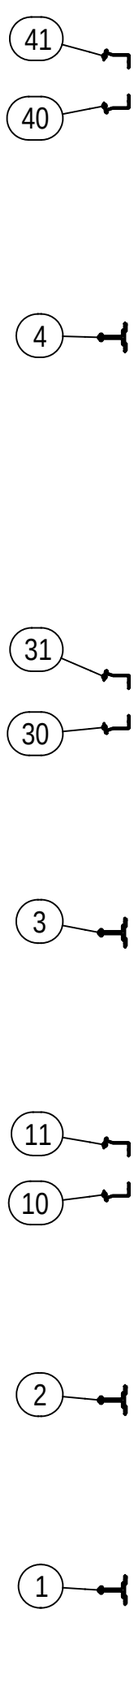


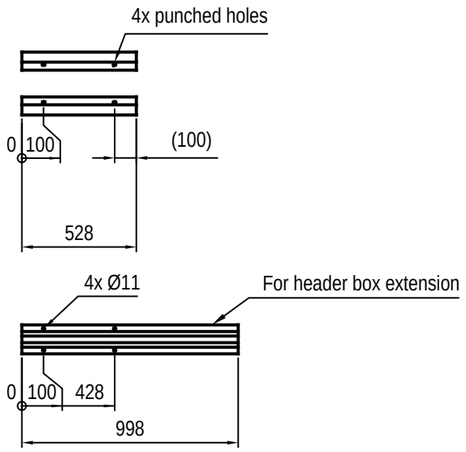


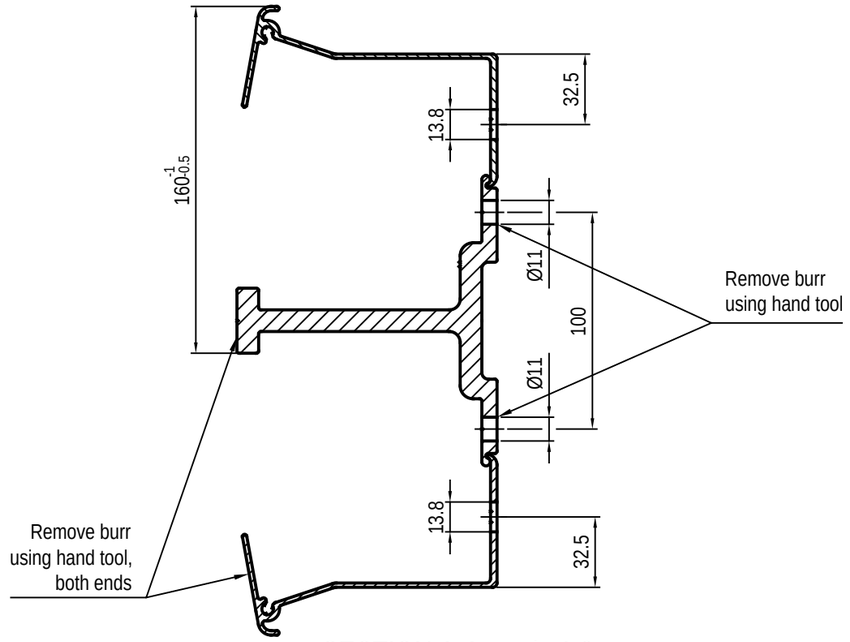



SECTION A-A, scale 1:2

Place this side down
All profiles

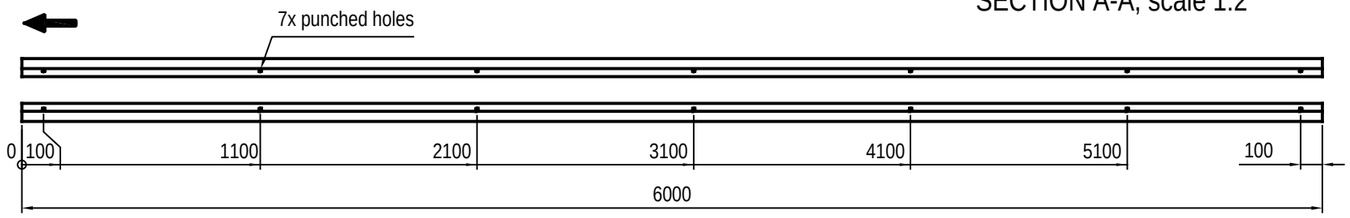

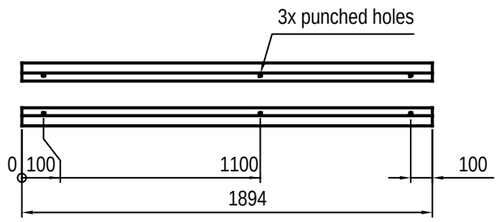

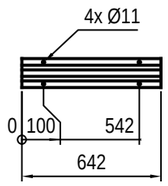

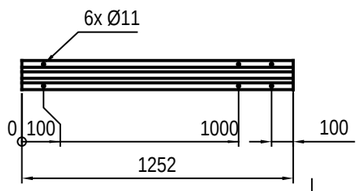

Total rail weight: 167 kg

ITEM	QTY	DESCRIPTION	DIMENSION	MATERIAL	REMARKS	kg/pc
41	2	Seal angle	L= 528		19114552	0.8
40	2	Seal angle	L= 528		19114552	0.8
31	2	Seal angle	L= 6000		19114552	8.7
30	2	Seal angle	L= 6000		19114552	8.7
11	2	Seal angle	L= 1894		19114552	2.7
10	2	Seal angle	L= 1894		19114552	2.7
4	2	Guide rail	L= 998		19114551	6.6
3	2	Guide rail	L= 6000		19114551	39.8
2	2	Guide rail	L= 642		19114551	4.3
1	2	Guide rail	L= 1252		19114551	8.3

DESIGNED: KCL
SIZE: A2
SCALE: 1:20
CODE: 84470
ITEM NO:
DATE: 2019-10-08
If not otherwise stated:
Tolerances
ISO 2768-m
EN ISO 13920-B
Cutting class
ISO 9013-442
Weld class
ISO 5817-C
Surface finish
Smooth raw surface
ASSA ABLOY

Nihva Poonawalla

India

Megadoor 20000 x 7000

Guide rails

PLOT DATE

DRAWING NO: 69439


REVISION: --

This document is the property of ASSA ABLOY Entrance Systems AB and shall not without our written permission be copied, imparted to a third party or used for any other unauthorized purpose.


LOAD DIAGRAM

Nominal static vertical loads are indicated. Value within brackets include dynamic surload factor 1.25 for door leaf loads in open position.
Includes items provided by ASSA ABLOY only.


DISTRIBUTED LOAD: 37.5kN

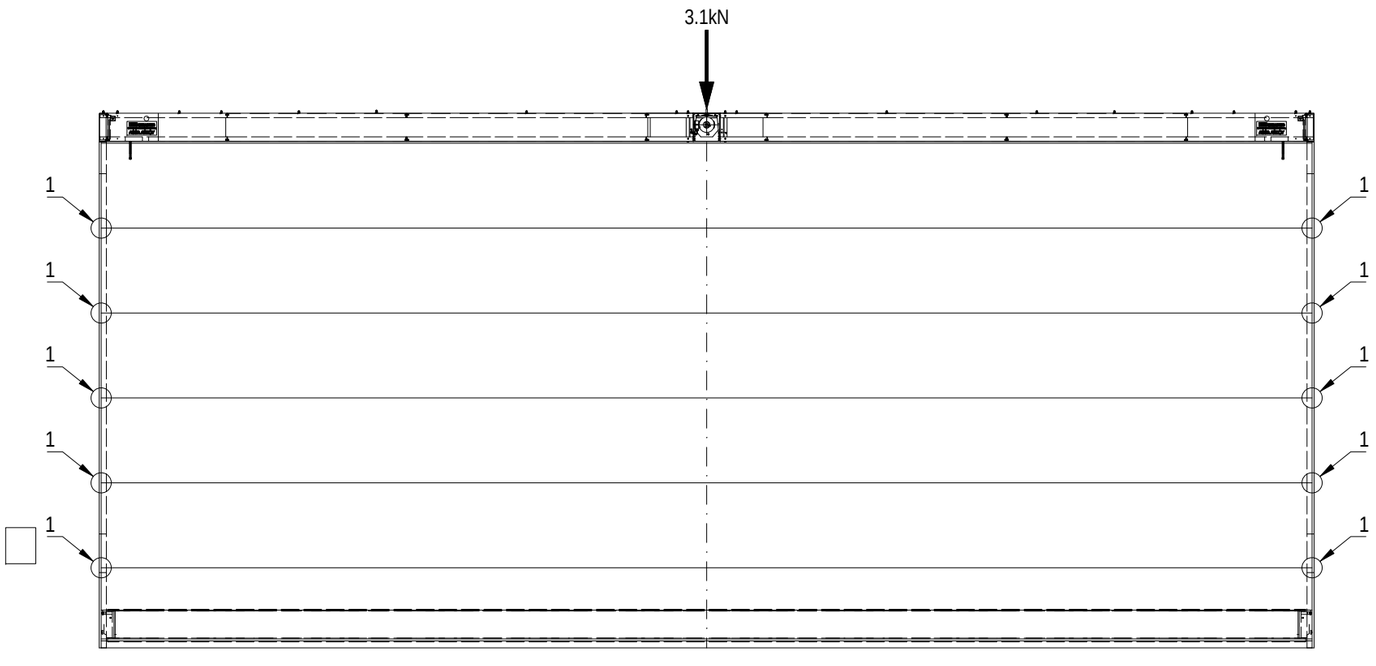

Interior view, Door closed

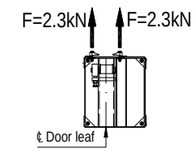


Load on header box attachment (each screw), due to wind load and door weight

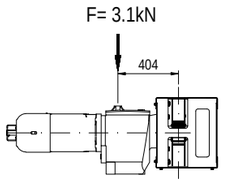


Section @ gear motor
SK 73F-132 S/4
Scale 1:20

DISTRIBUTED LOAD: 8.7kN

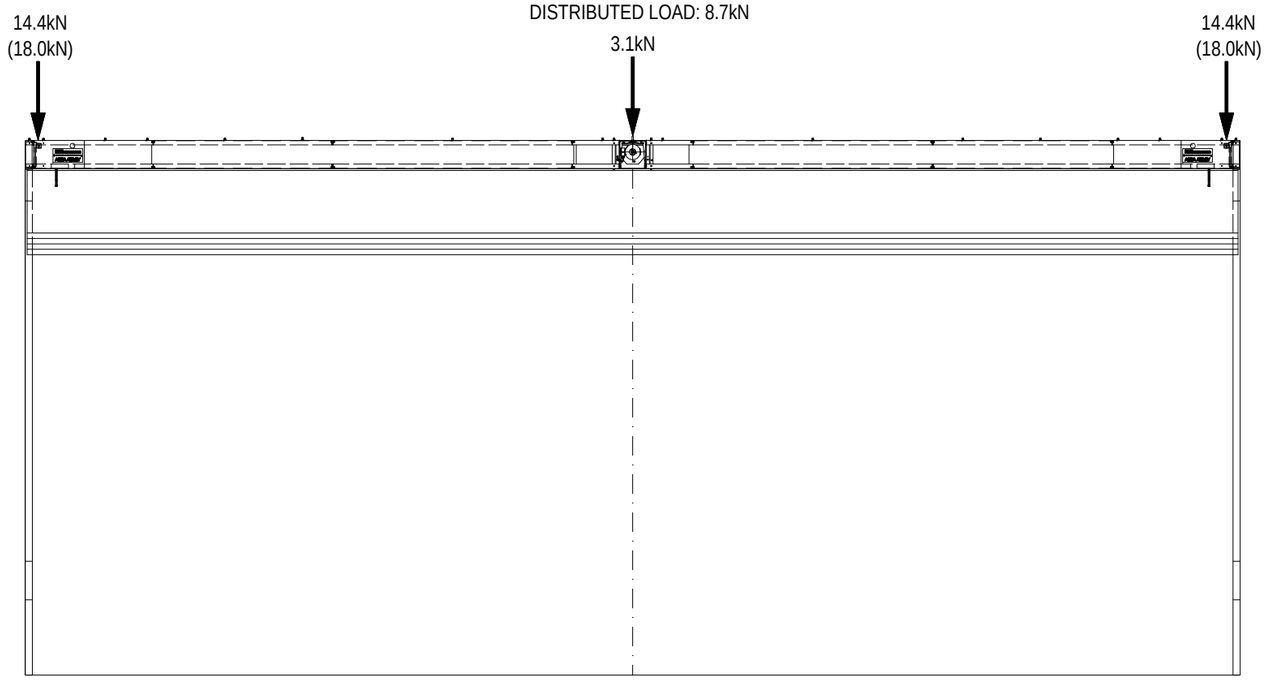

Interior view, Door open

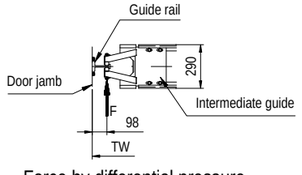

Force by differential pressure transferred to guide rail at each intermediate position.
(located at pos 1)
F=13.4 kN

NOT INCLUDED IN DOOR SUPPLY:

1. Design and supply of all door supporting structural components.
2. Design and supply of all closure between door and adjacent steel.
3. Design and supply of coverage, such as roofing or enclosure, for door components at door head.
4. Door jambs adjustable for overall door width and true to plumb.
5. Paint job after completed door installation.
6. Any frameworks being provided by ASSA ABLOY will be clearly indicated as "by ASSA ABLOY".

REQUIREMENTS ON BUILDING:

7. Door head support must be straight within 1/600 of span in the in/out direction and free from protrusions of any kind.
8. For a single door leaf, door head support should be horizontal and straight within 1/600 of span at distributed full door load.
9. Door side jambs must be smooth, straight and parallel, out of plumb must not exceed 2mm/m (total deviation at full length 5 mm) in any direction.
10. Any footings at bottom of jamb columns must not interfere with installation of guide rails at floor level.
11. At time of installation, finished floor, free from obstructions, out to a distance of 2 m on each side of door centreline must be available.
12. Header box must be accessible from both sides during installation.

DOOR PROPERTIES:

13. The door is designed to withstand a differential pressure of 1kPa.
14. Guide rails, top- and intermediate beams in extruded aluminium with natural finish.
15. Environmental category: Megadoor standard
16. Bottom beam in carbon steel painted: Light grey (RAL7047)
17. Colored clamp strips on both sides: GREY (RAL7004)
18. Door header box enclosed on motor side.
19. Color of header box: BLACK (NCS 9000-N. RAL 9005)
20. The door fabric is a UV stabilized, flame retardant, self-extinguishing, PVC coated polyester fabric with fire technical properties Euroclass C-s2, d0 (according to EN 13501-1:2007).
    Colour of fabric: White Aluminum (RAL 9006)

ELECTRICAL:

21. One main control panel provided of PLC type.
22. Control mode : Impulse up / Constant contact down.
23. Cables are included.
24. Back-up power socket & switch.
25. Audible & visual alarm.
26. Approx. size of main control panel: WxHxD (500x600x250mm),
27. Location of main control panel: Please specify location.
28. Aux. Voltage 24VDC
29. Power supply: 400V /3Ph /50Hz
30. Power: 8.6kW
31. Nom. current: 18.1A
32. Start current: 79.6A
33. (max. allowed voltage drop at start: 5%)

BELT HOIST UNITS:

SK 73F-132S74 OD440
75mm wide polyester belt. Rupture load 108kN/belt.

DOOR IDENTITY NUMBER: 84470001

INTERFACE DRAWING, ref. to drwng. no. 69424

DESIGNED	APPROVED	SIZE	SCALE
FV		A1	1:50

CODE 84470
ITEM NO
DATE 2019-10-08


If not otherwise stated:
Tolerances ISO 2768-m EN ISO 13920-B
Cutting class ISO 9013-442
Weld class ISO 5817-C
Surface finish Smooth raw surface


ASSA ABLOY


Nihva Poonawalla
India
Megadoor 20000 x 7000
Load diagram & Notes

DRAWING NO 69425
REVISION --
PLOT DATE

This document is the property of ASSA ABLOY Entrance Systems AB and shall not without our written permission be copied, imparted to a third party or used for any other unauthorized purpose.

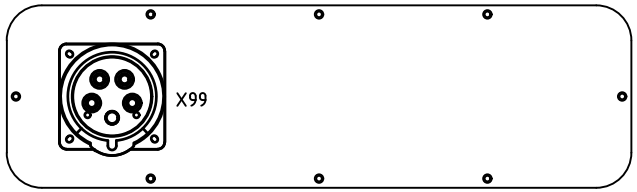

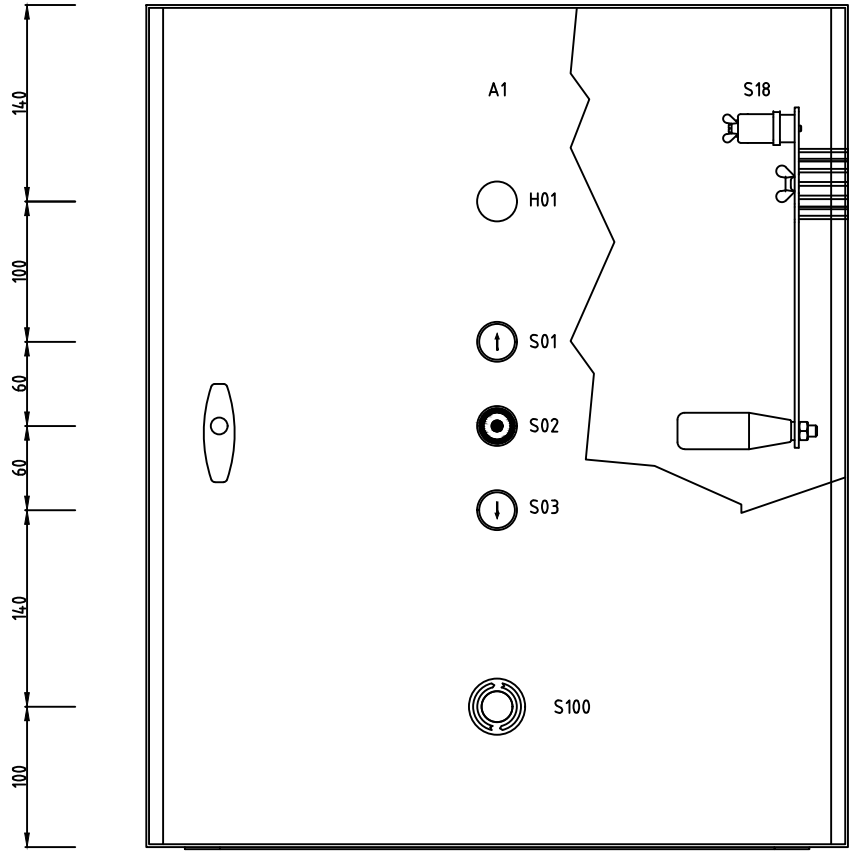

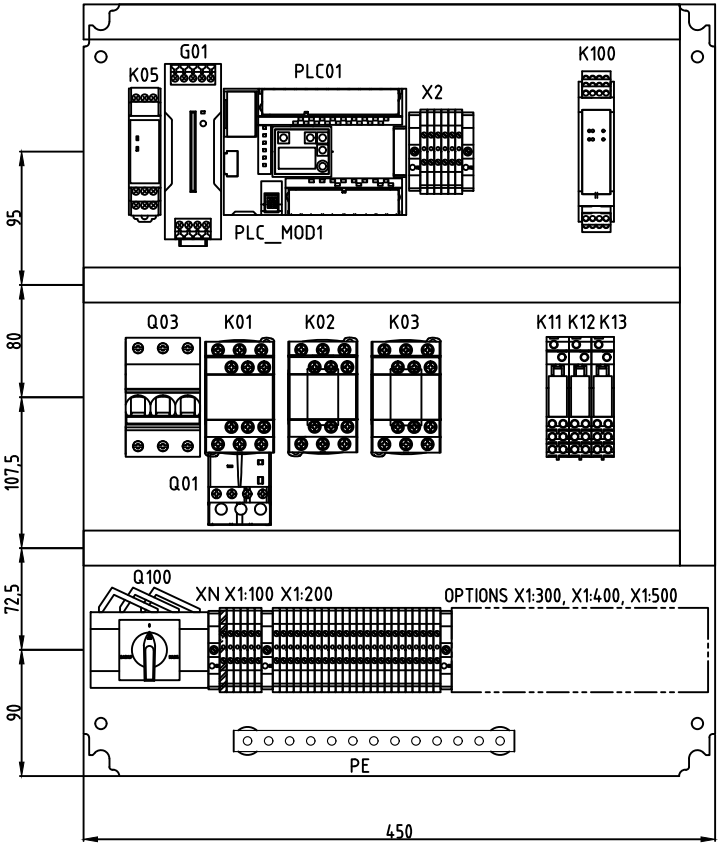

ASSA ABLOY

Property of ASSA ABLOY Entrance Systems AB and shall not without our written permission be copied, imparted to a third party or used for any other unauthorized purpose.

Nihva Poonawalla

Direct drive | Single motor

Panel layout

Designed	Approved	Location	Code
MED	GO		84470001

Page 1/12

Date 191014

Drawing No 60106

Revision --

UNIT	QTY	DESC	TYPE	MFG	TAG	CAT
PCS	1	ENCLOSURE	NSYS3D6525P	SCHNEIDER ELECTRIC	A1	19204653
PCS	1	WALL FIXING LUGS	SYAEFPFSC	SCHNEIDER ELECTRIC		19204015
PCS	1	BOTTOM PLATE	KNOCK OUT	N/A		19148751
PCS	1	ISOLATOR	KG32B T903/S-A308.xVE	KRAUS & NAIMER	Q100	19204137
PCS	1	TERMINAL	WDU 6 BL	WEIDMÜLLER	XN	19204231
PCS	1	TERMINAL MARKER	DEK 5 GW X	WEIDMÜLLER		19204030
PCS	1	TERMINAL MARKER	DEK 5 GW N	WEIDMÜLLER		19204032
PCS	3	TERMINAL	WDU 6	WEIDMÜLLER	X1:101-103	19203770
PCS	2	TERMINAL	WDU 2,5	WEIDMÜLLER	X1:100	19203310
PCS	2	TERMINAL MARKER	DEK 5 GW X	WEIDMÜLLER		19204030
PCS	2	TERMINAL MARKER	DEK 5 GW 1	WEIDMÜLLER		19204031
PCS	5	TERMINAL MARKER	DEK 5 FWZ 101-105	WEIDMÜLLER		19204033
PCS	24	TERMINAL	WDU 2,5	WEIDMÜLLER	X1:200	19203310
PCS	1	CROSS CONNECTOR	ZQV 2,5N/20 GE	WEIDMÜLLER		19204920
PCS	1	CROSS CONNECTOR	ZQV 2,5N/10	WEIDMÜLLER		19204934
PCS	24	TERMINAL MARKER	DEK 5 FW 201-224	WEIDMÜLLER		19204140
PCS	3	END BRACKET	WEW 35/2	WEIDMÜLLER		19204029
PCS	1	MCB	iC60N 3P C6A	SCHNEIDER ELECTRIC	Q03	19204506
PCS	3	CONTACTOR	LC1D25 BL	SCHNEIDER ELECTRIC	K01-K03	19204489
PCS	1	BUS BAR	GV2G354	SCHNEIDER ELECTRIC		19204674
PCS	2	CONTACT BLOCK	LADN11	SCHNEIDER ELECTRIC		19202995
PCS	1	OVERLOAD RELAY	LRD22 16-24A	SCHNEIDER ELECTRIC	Q01	19202987
PCS	1	VOLTAGE MONITOR	K8AK-PH1	OMRON	K05	19204062
PCS	1	POWER SUPPLY	S8VK T12024	OMRON	G01	19204903
PCS	1	PLC	CP1L-EM30DR-D	OMRON	PLC01	19204351
PCS	1	HMI-LCD	CP1W-DAM01	OMRON	PLC_MOD1	19203800
PCS	6	TERMINAL	WDU 2,5	WEIDMÜLLER	X2	19203310
PCS	2	CROSS CONNECTOR	ZQV 2,5N/3	WEIDMÜLLER		19204673
PCS	2	TERMINAL MARKER	DEK 5 GW X	WEIDMÜLLER		19204030
PCS	2	TERMINAL MARKER	DEK 5 GW 2	WEIDMÜLLER		19204478
PCS	6	TERMINAL MARKER	DEK 5 +	WEIDMÜLLER		19204675
PCS	6	TERMINAL MARKER	DEK 5 -	WEIDMÜLLER		19204676
PCS	2	END BRACKET	WEW 35/2	WEIDMÜLLER		19204029

UNIT	QTY	DESC	TYPE	MFG	TAG	CAT
PCS	1	SAFETY RELAY	G9SB-3012-A	OMRON	K100	19204904
PCS	1	PILOT LIGHT	ZB4BVB4	SCHNEIDER ELECTRIC	H01	19203745
PCS	1	PUSH BUTTON	ZB4BA334	SCHNEIDER ELECTRIC	S01	19203365
PCS	1	CONTACT BLOCK	ZB4BZ101	SCHNEIDER ELECTRIC		19203364
PCS	1	PUSH BUTTON	ZB4BA232	SCHNEIDER ELECTRIC	S02	19201807
PCS	1	CONTACT BLOCK	ZB4BZ102	SCHNEIDER ELECTRIC		19203005
PCS	1	PUSH BUTTON	ZB4BA334	SCHNEIDER ELECTRIC	S03	19203365
PCS	1	CONTACT BLOCK	ZB4BZ105	SCHNEIDER ELECTRIC		19204482
PCS	1	EMRG STOP	ZB4BS844	SCHNEIDER ELECTRIC	S100	19201805
PCS	1	CONTACT BLOCK	ZB4BZ104	SCHNEIDER ELECTRIC		19204481
MM	200	PE BAR	JS 75	N/A	PE	19204158
PCS	2	SPACER	-	N/A		19204206
PCS	2	SCREW	MONTB420251	N/A		19204978
PCS	1	HAND CRANK	Ø32	N/A	S18	19151177
MM	1250	DIN RAIL	NS 35/7,5	N/A		19200897
PCS	10	SCREW	MONTB420131	N/A		19204169
PCS	3	BRACKET	TSTR 5/M5	N/A		19204159
PCS	3	SCREW	MRT-GF 5x12 ZIB	N/A		19201960
MM	1675	CABLE DUCT	25x80 PVC	N/A		19204407
PCS	12	SCREW	MONTB420131	N/A		19204169
MM	460	PROTECTIVE HOSE	170-11000	N/A		19204069
PCS	4	CABLE TIE ATTACHMENT	ABM2S-A-D	N/A		19204037
PCS	15	CABLE TIE	2,5x142	N/A		19204011
PCS	1	3-PHASE INLET	432BU6	ABB	X99	19204138
PCS	4	SCREW	M4	N/A		19203361
PCS	4	LOCK WASHER	M4	N/A		-
PCS	4	NUT	M6M 4 A2	N/A		19203202

ASSA ABLOY

Property of ASSA ABLOY Entrance Systems AB and shall not without our written permission be copied, imparted to a third party or used for any other unauthorized purpose.

Nihva Poonawalla

Direct drive | Single motor

Bill of material

Designed	Approved	Location	Code
MED	GO		84470001

Page 2/12

Date 191014

Drawing No 60106

Revision --

UNIT	QTY	DESC	TYPE	MFG	TAG	CAT
		PLACEMENT OF ALL LABELS: REFER TO DRAWING 1835				
PCS	1	LABEL	ALARM	N/A		19204134
PCS	1	LABEL	YELLOW	N/A		19204087
PCS	1	LABEL	PE	N/A		19204068
PCS	1	LABEL	EARTH	N/A		19204086
PCS	1	LABEL	ASSEMBLY	N/A		19101834
PCS	1	LABEL	ASSEMBLY	N/A		19150549
PCS	1	LABEL	EMERGENCY	N/A		19101951
PCS	1	LABEL	DANGER	N/A		19101829
PCS	1	LABEL	CAUTION	N/A		19101952
PCS	4	LABEL	ARROW	N/A		19200182
PCS	1	LABEL	ID CEN	N/A		19146229
PCS	1	LABEL	ASSA ABLOY	N/A		19204680
PCS	1	LABEL	PANEL LAYOUT	N/A		-
PCS	2	CABLE GLAND	M25x1,5	N/A		19202961
PCS	2	LOCK NUT	M25x1,5	N/A		19203396
PCS	4	CABLE GLAND	M16x1,5	N/A		19203314
PCS	4	LOCK NUT	M16x1,5	N/A		19203395
PCS	1	CABLE GLAND	M16x1,5	N/A		19203314
PCS	1	LOCK NUT	M16x1,5	N/A		19203395

UNIT	QTY	DESC	TYPE	MFG	TAG	CAT
PCS	1	SIGNAL LIGHT/SIREN	SONL24/O-H	TOLEKA	P11	19203722
PCS	1	TERMINAL	WDU 2,5	WEIDMÜLLER	X1:400	19203310
PCS	1	TERMINAL MARKER	DEK 5 FW 407	WEIDMÜLLER		19204142
PCS	3	PROXIMITY SWITCH	IGS 232	IFM	L11-L12,L15	19203948

Property of ASSA ABLOY Entrance Systems AB and shall not without our written permission be copied, imparted to a third party or used for any other unauthorized purpose.


ASSA ABLOY

Nihva Poonawalla

Direct drive | Single motor

Bill of material

Designed	Approved	Location	Code	Page	Date	Drawing No	Revision
MED	GO		84470001	3/12	191014	60106	--

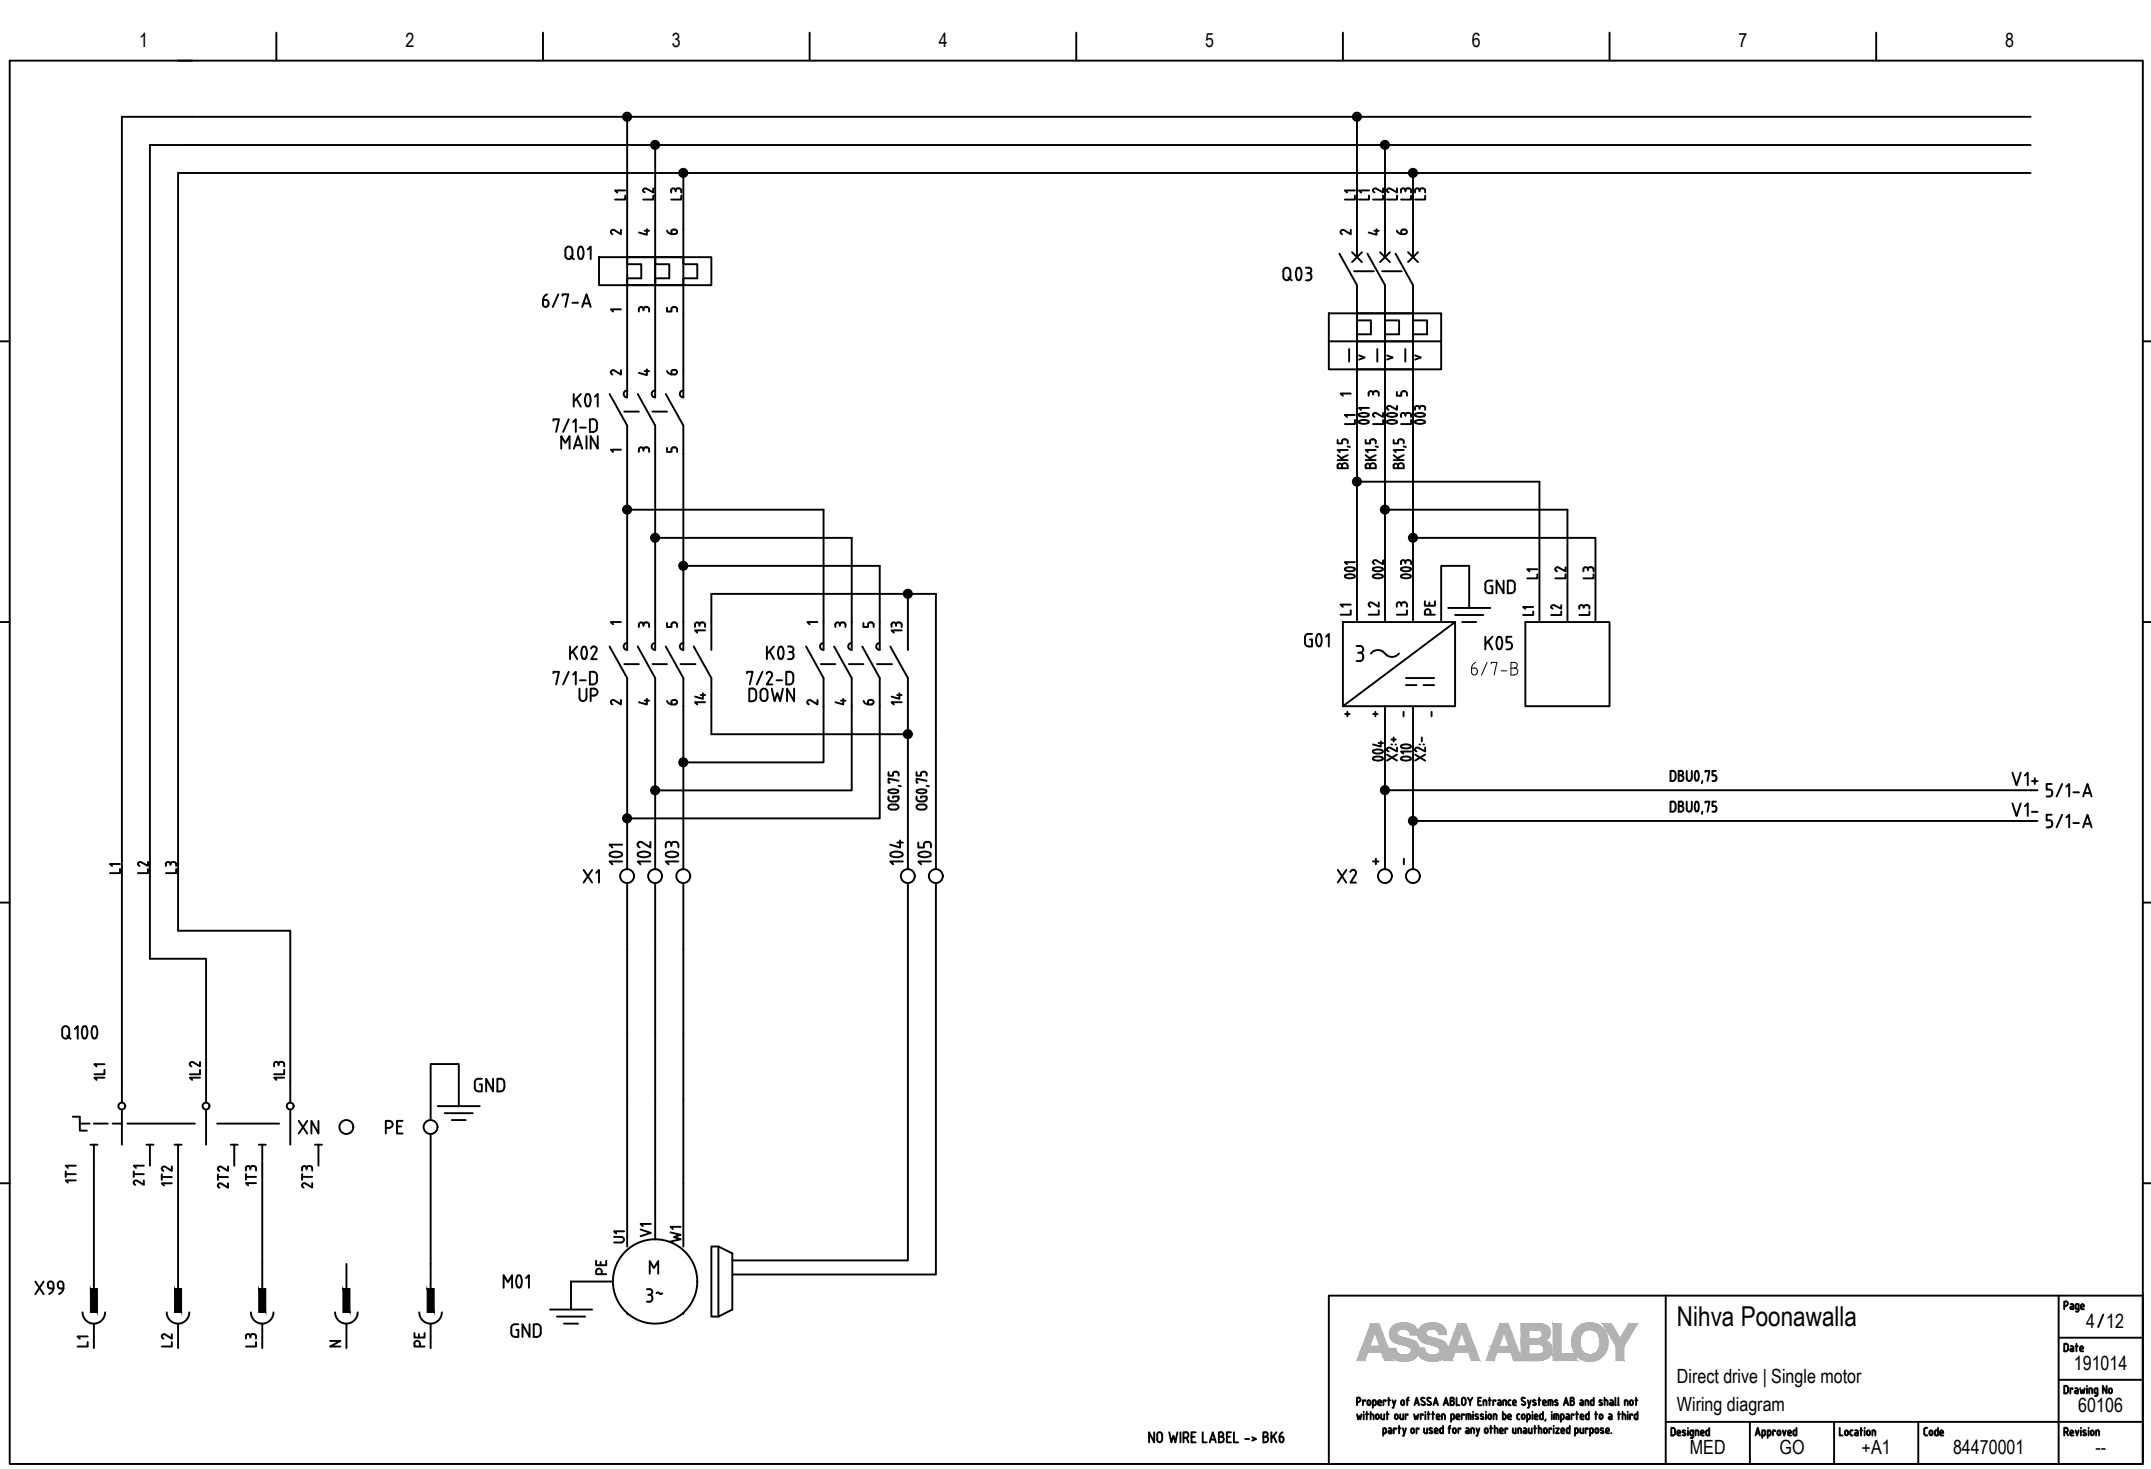

ASSA ABLOY


Property of ASSA ABLOY Entrance Systems AB and shall not without our written permission be copied, imparted to a third party or used for any other unauthorized purpose.

Nihva Poonawalla

Direct drive | Single motor

Wiring diagram

Designed	Approved	Location	Code	Page	Date	Drawing No	Revision
MED	GO	+A1	84470001	4/12	191014	60106	--

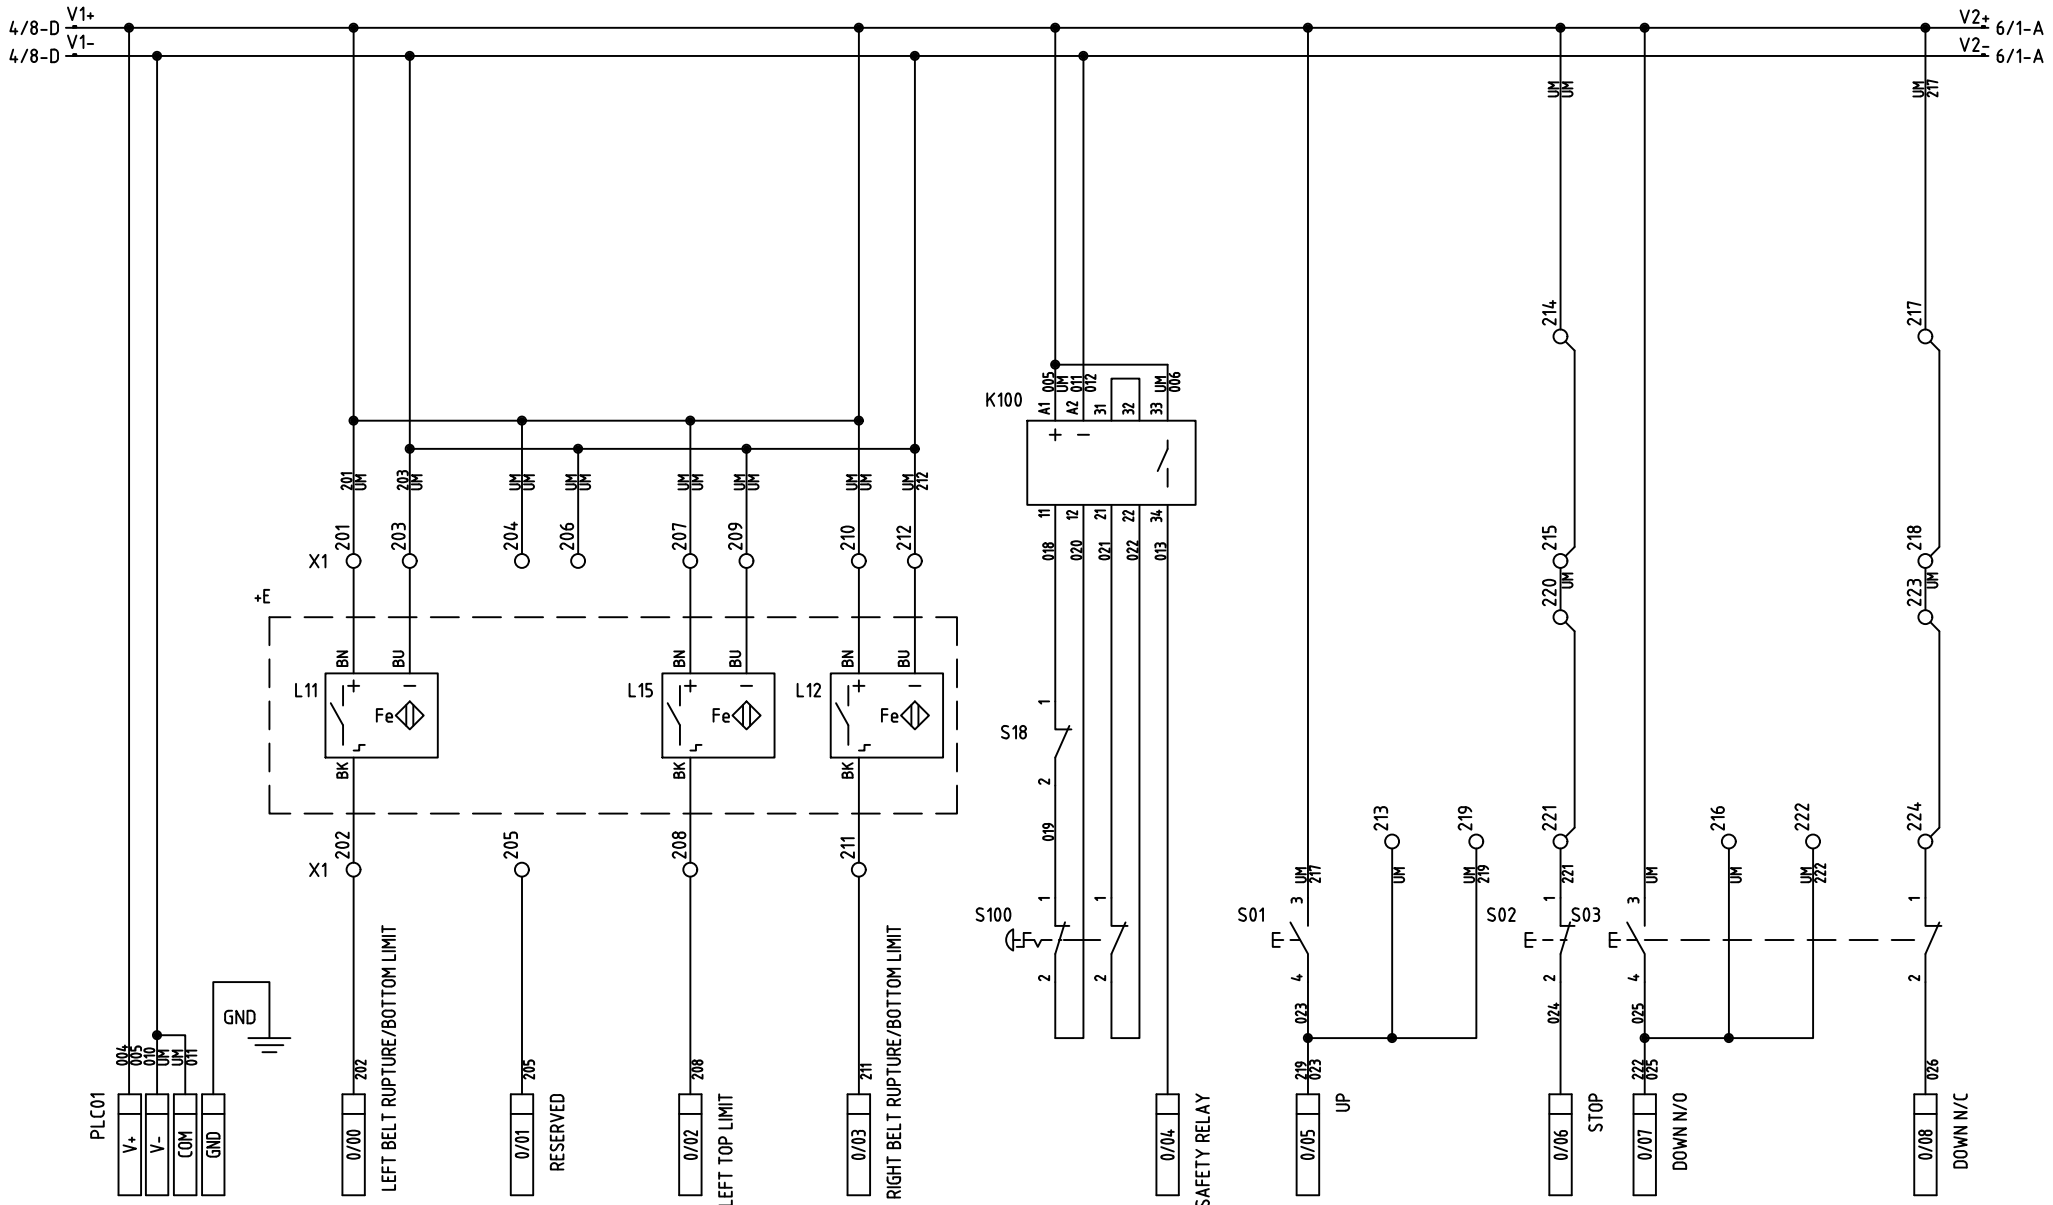

ASSA ABLOY


Property of ASSA ABLOY Entrance Systems AB and shall not without our written permission be copied, imparted to a third party or used for any other unauthorized purpose.

Nihva Poonawalla

Direct drive | Single motor

Wiring diagram

Designed	Approved	Location	Code	Page	Date	Drawing No	Revision
MED	GO	+A1	84470001	5/12	191014	60106	--

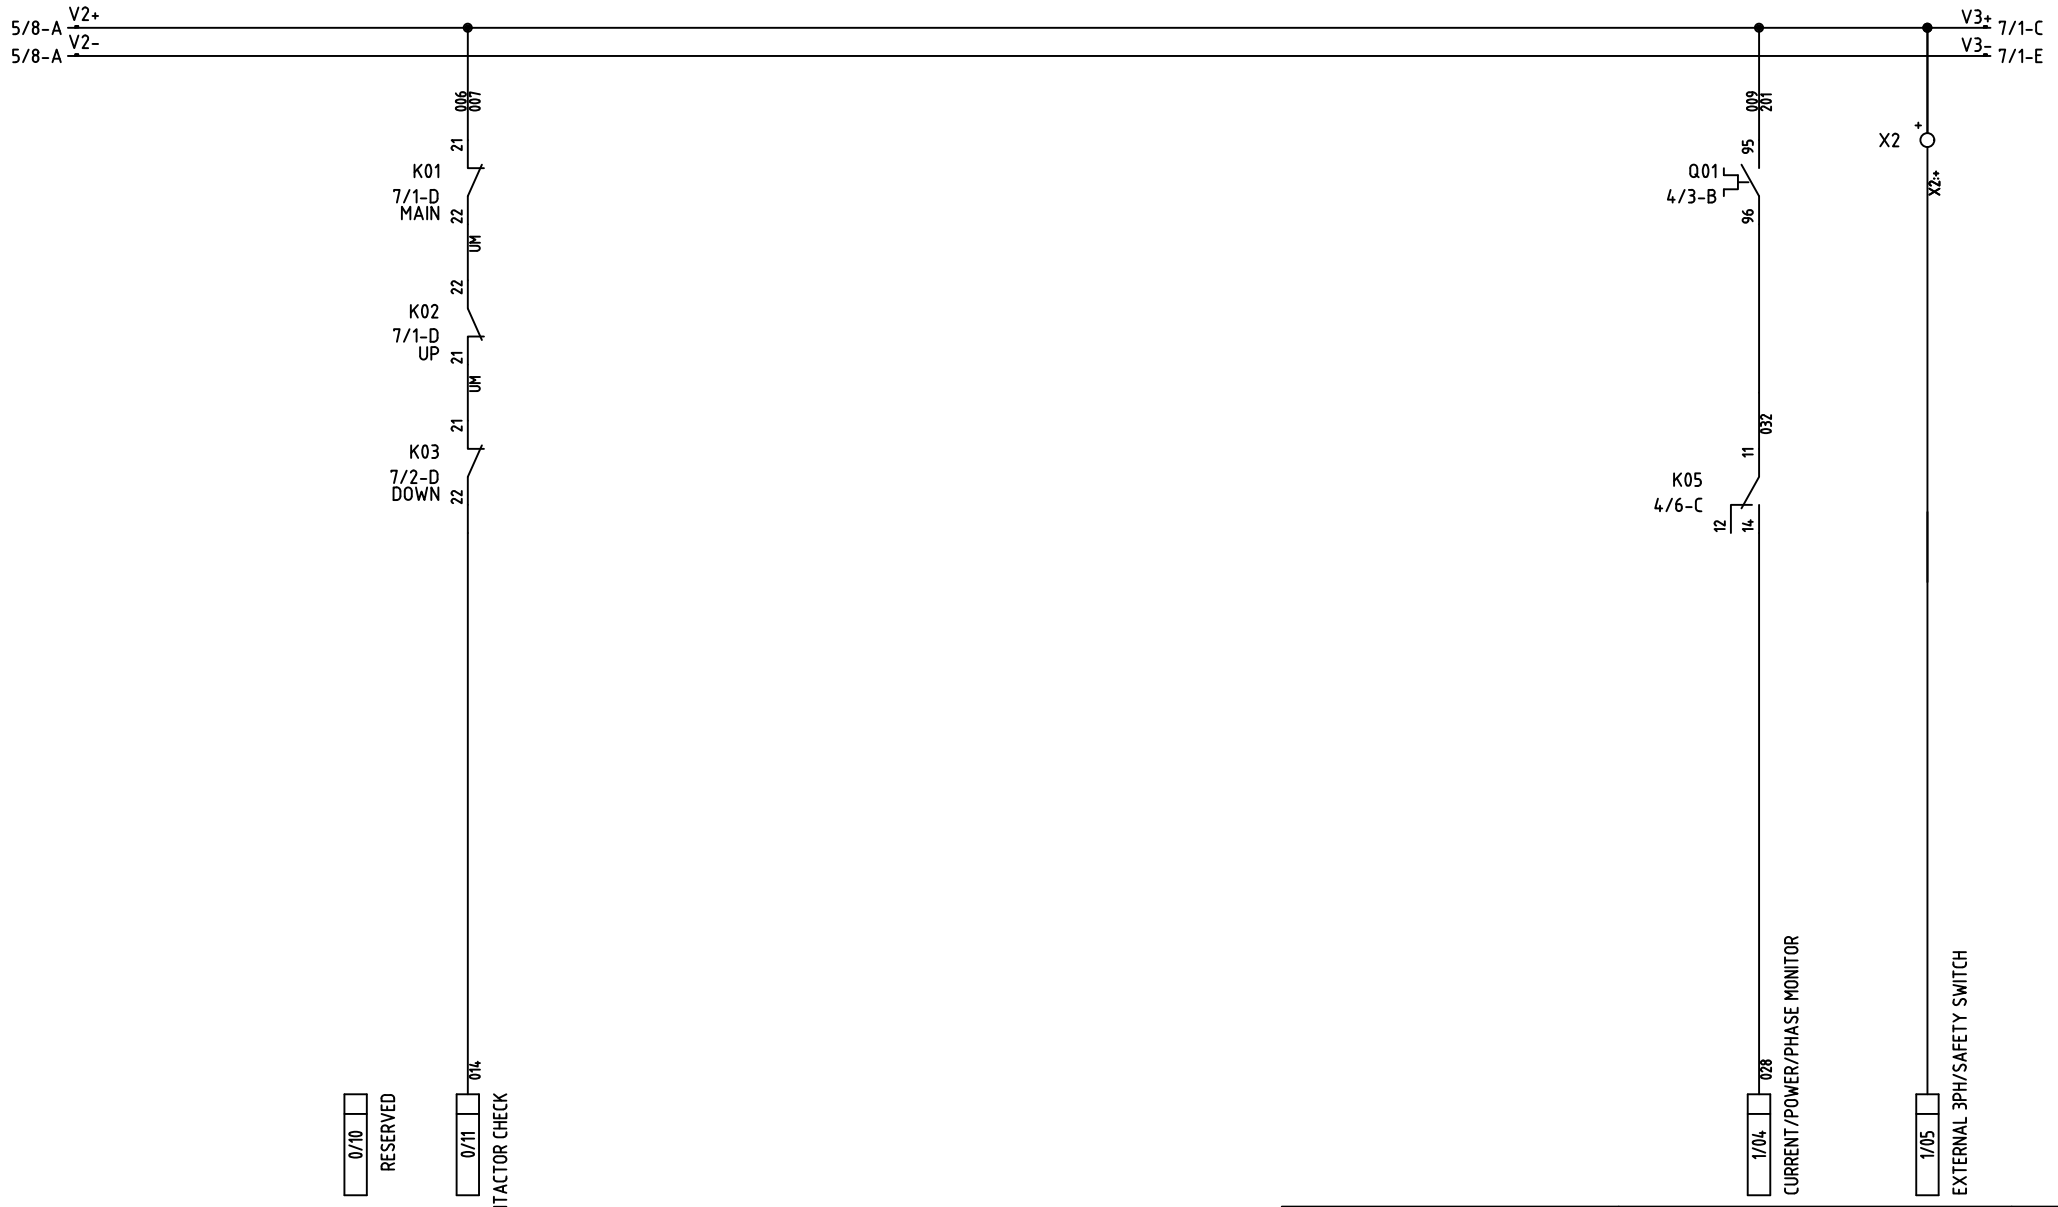

Property of ASSA ABLOY Entrance Systems AB and shall not without our written permission be copied, imparted to a third party or used for any other unauthorized purpose.


ASSA ABLOY

Nihva Poonawalla

Direct drive | Single motor

Wiring diagram

Designed	Approved	Location	Code	Page	Date	Drawing No	Revision
MED	GO	+A1	84470001	6/12	191014	60106	--

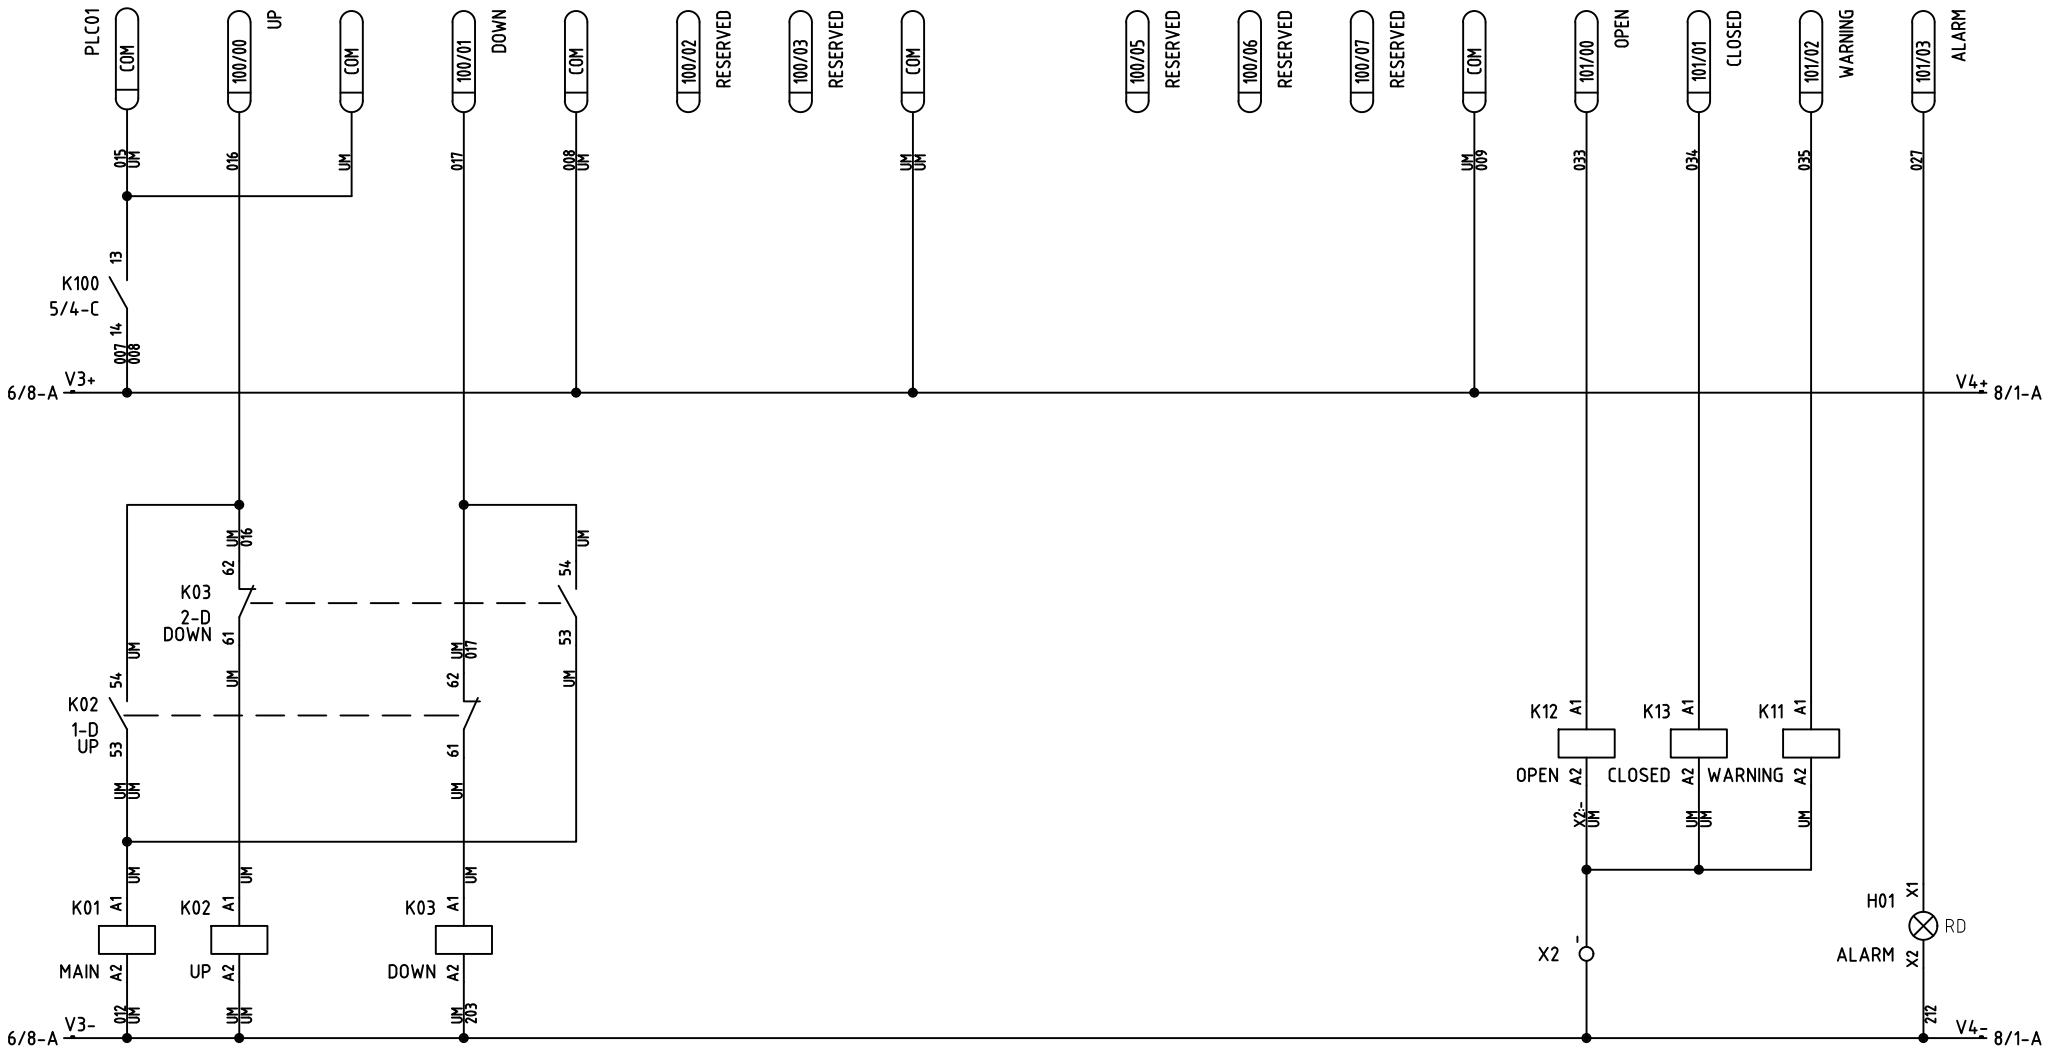

PLC SETTINGS

DIP SETTINGS
PLC01 DIP 4 ON

NO WIRE LABEL -> DBU0,75

ASSA ABLOY


Property of ASSA ABLOY Entrance Systems AB and shall not without our written permission be copied, imparted to a third party or used for any other unauthorized purpose.

Nihva Poonawalla

Direct drive | Single motor

Wiring diagram

Designed	Approved	Location	Code	Page	Date	Drawing No	Revision
MED	GO	+A1	84470001	7/12	191014	60106	--

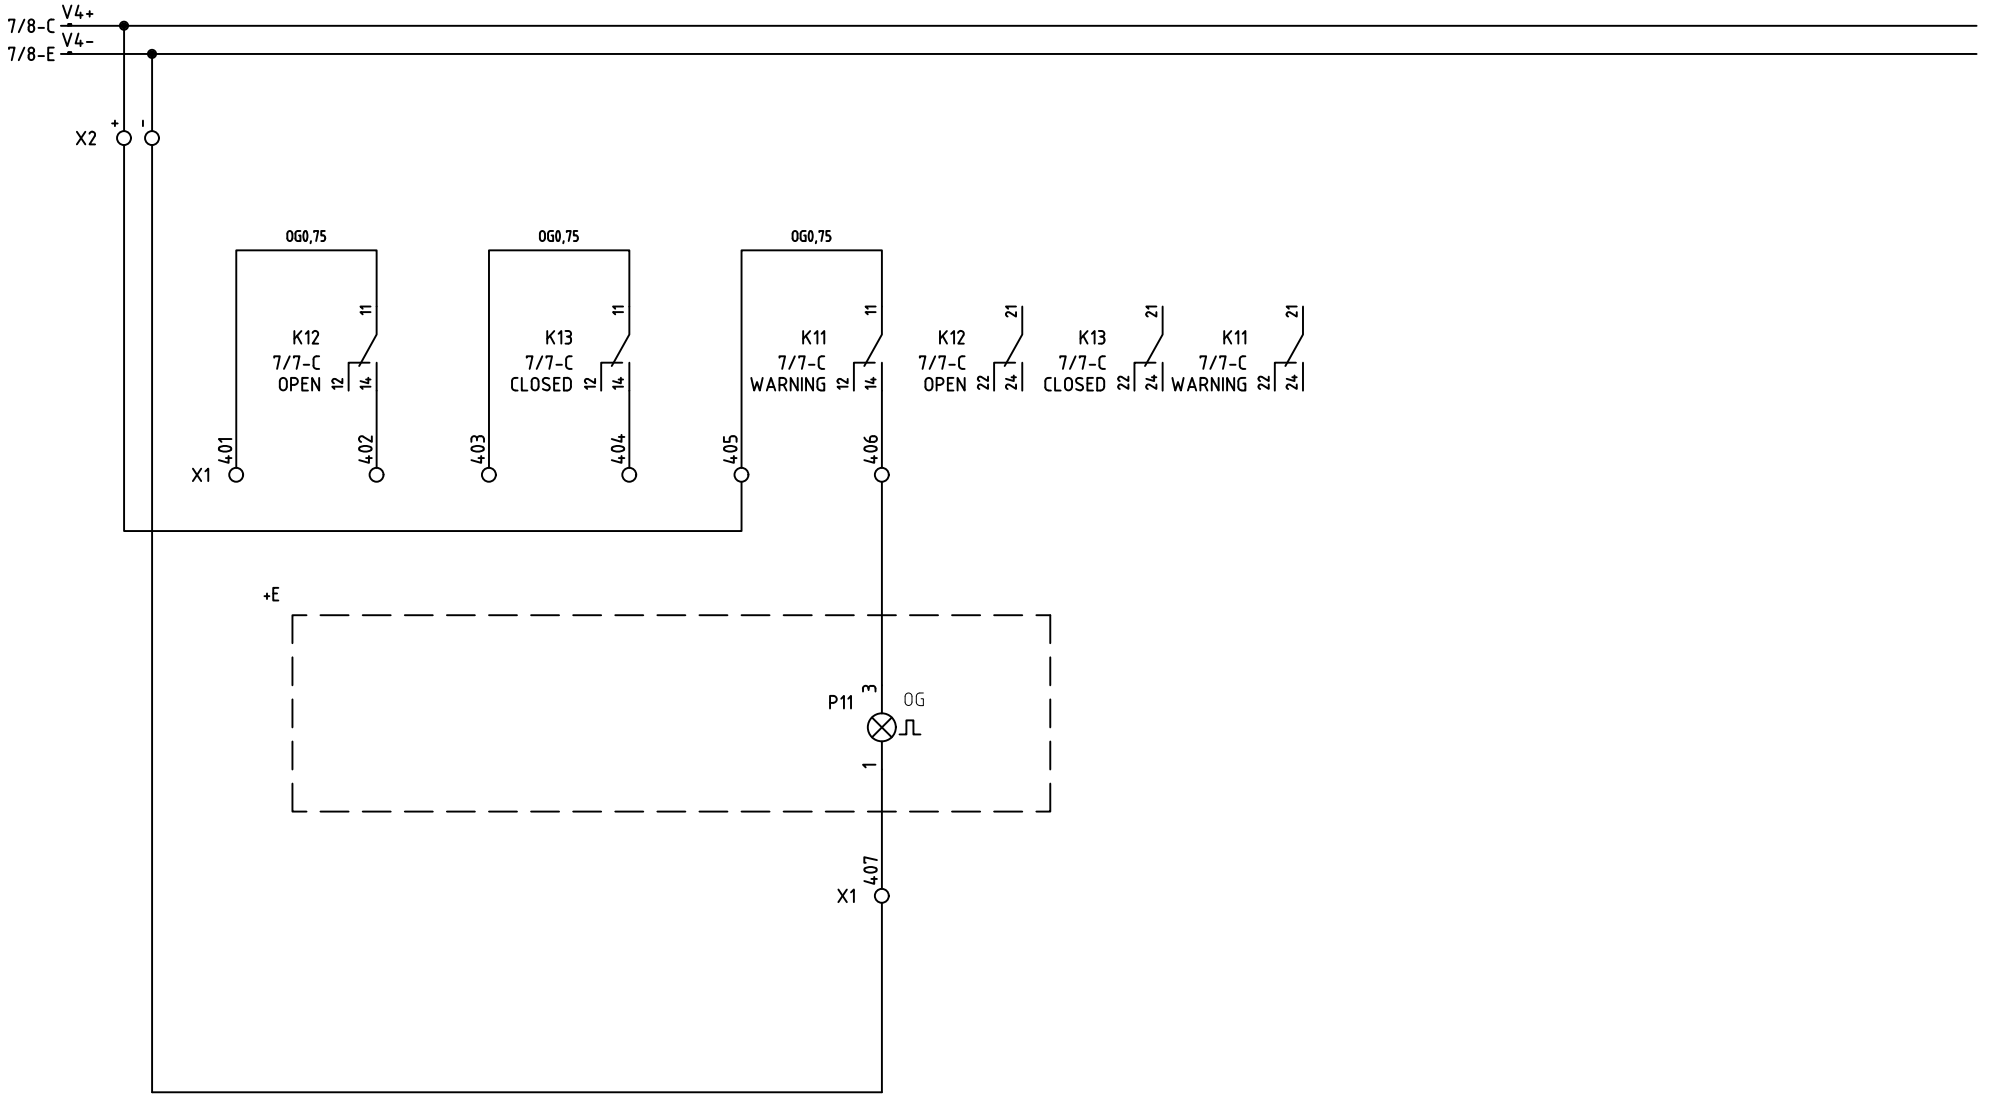

NO WIRE LABEL -> DBU0,75

ASSA ABLOY

Property of ASSA ABLOY Entrance Systems AB and shall not without our written permission be copied, imparted to a third party or used for any other unauthorized purpose.


Nihva Poonawalla


Direct drive | Single motor

Wiring diagram

Designed	Approved	Location	Code
MED	GO	+A1	84470001

Page	Date	Drawing No	Revision
8/12	191014	60106	--

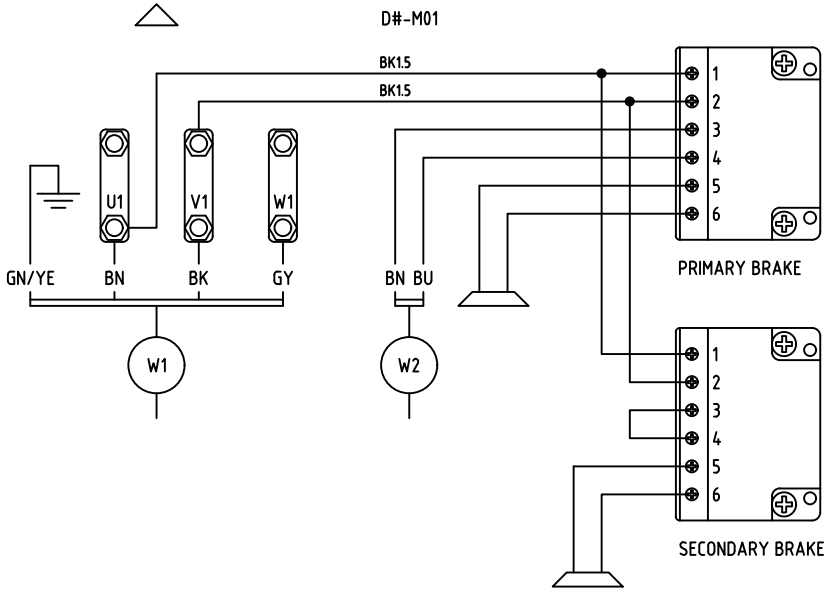

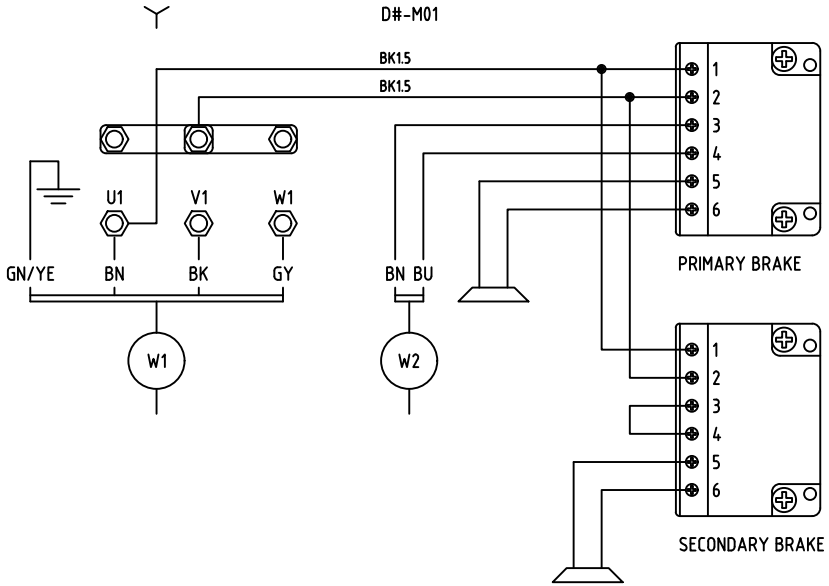

Revision	Date	Revised by	Description
A	16-11-14	MED	W1-W3 type changed


Property of ASSA ABLOY Entrance Systems AB and shall not without our written permission be copied, imparted to a third party or used for any other unauthorized purpose.

Nihva Poonawalla

Direct drive | Single motor

Motor connection

Designed	Approved	Location	Code	Page	Date	Drawing No	Revision
MED	GO	+E	84470001	9/12	191014	60106	A

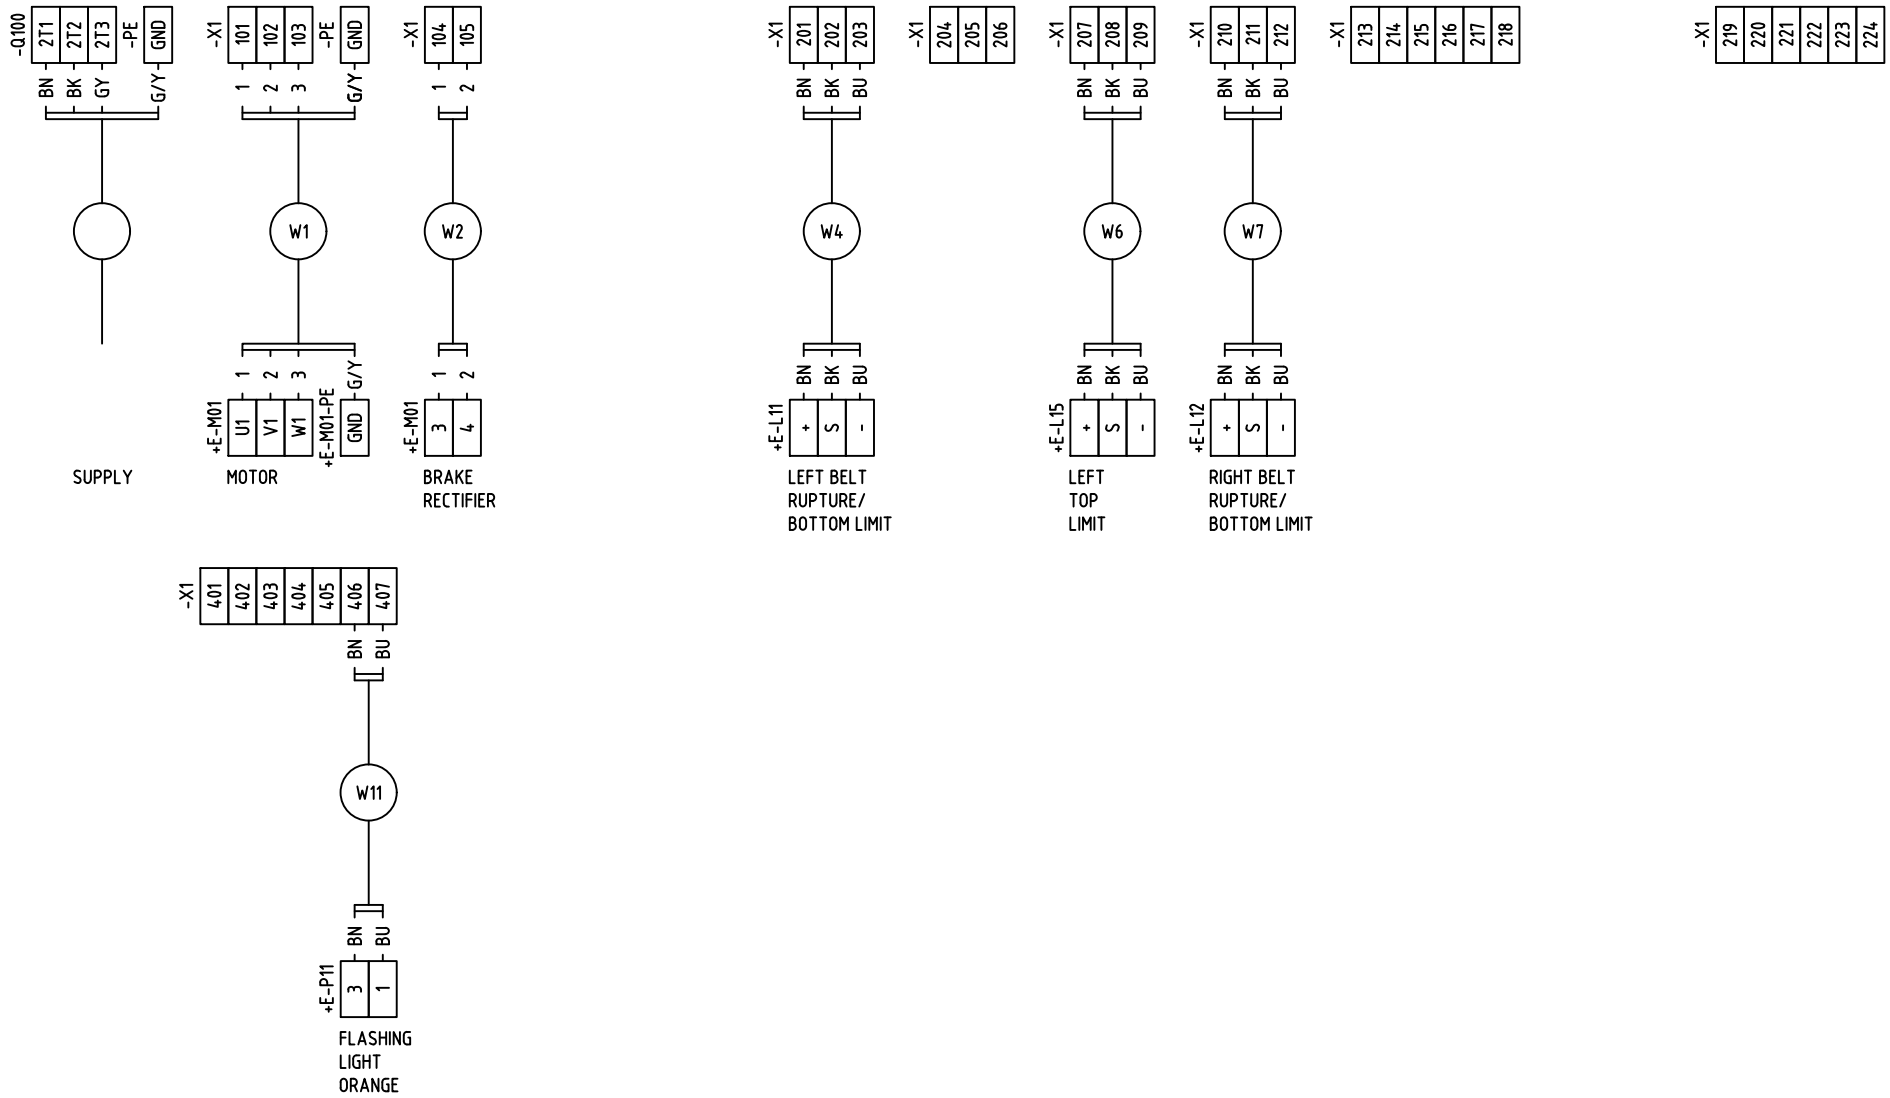

Revision	Date	Revised by	Description
A	16-11-14	MED	W1-W3 type changed

ASSA ABLOY

Property of ASSA ABLOY Entrance Systems AB and shall not without our written permission be copied, imparted to a third party or used for any other unauthorized purpose.

Nihva Poonawalla

Direct drive | Single motor

External connections


Designed	Approved	Location	Code
MED	GO	+A1	84470001

Page 10/12

Date 191014

Drawing No 60106

Revision A

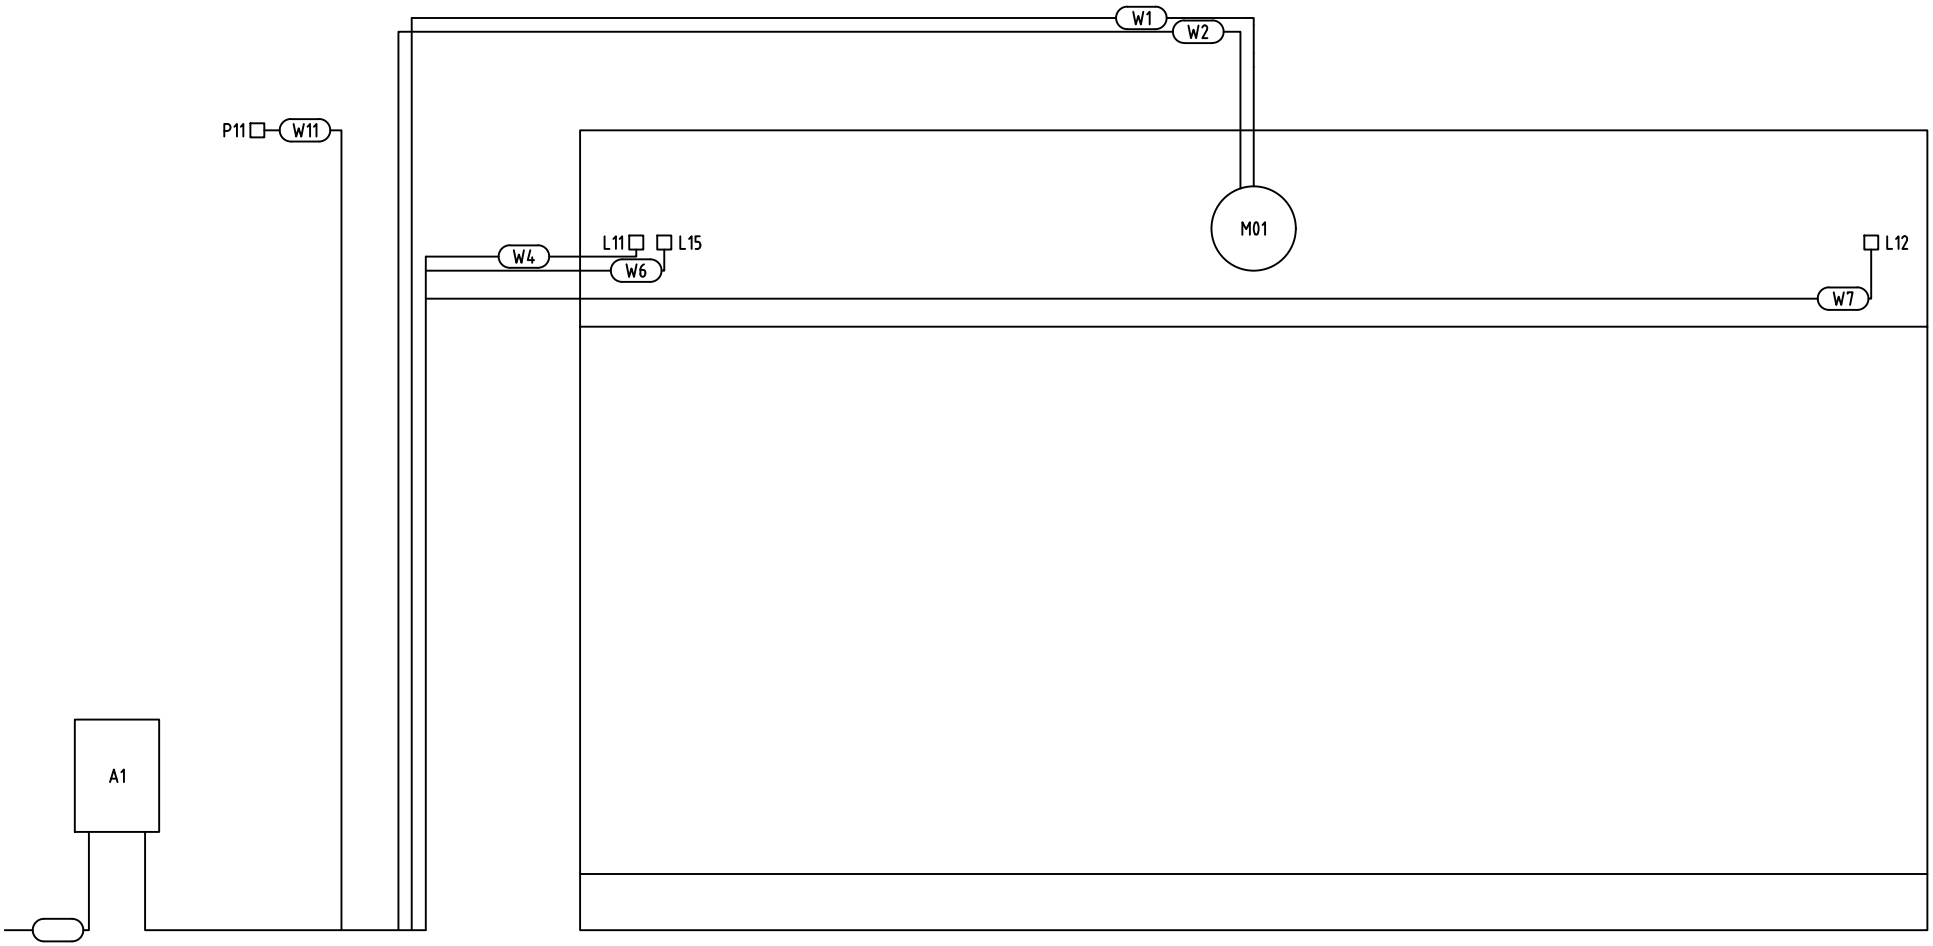

NOMINAL CURRENT:	18.1 A
TOTAL POWER:	8.6 kW
PEAK CURRENT:	79.6 A
VOLTAGE:	400 V/50 Hz

W1 4G6
W2 EXQ 3G1.5 W11 EXQ 3G1.5

W4-7 PUR 4X0.34 w. M12

Revision	Date	Revised by	Description
A	16-11-14	MED	W1-W3 type changed

ASSA ABLOY

Property of ASSA ABLOY Entrance Systems AB and shall not without our written permission be copied, imparted to a third party or used for any other unauthorized purpose.


Nihva Poonawalla


Direct drive | Single motor

Installation overview

Designed	Approved	Location	Code	Revision
MED	GO	+E	84470001	A

Page	11/12
Date	191014
Drawing No	60106

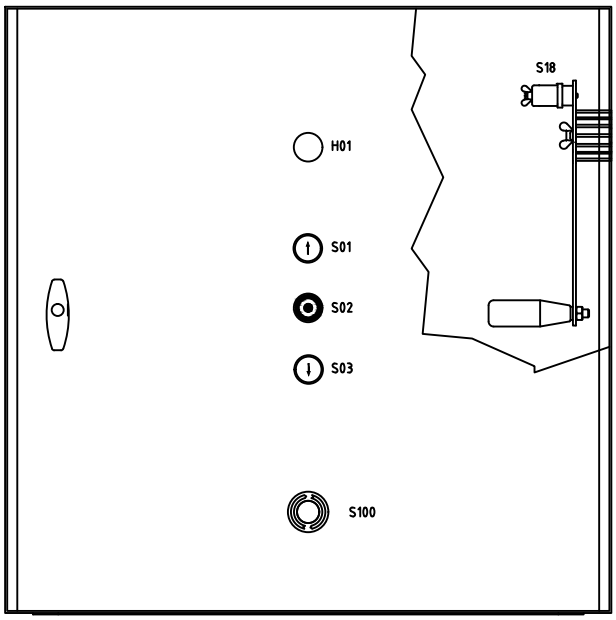

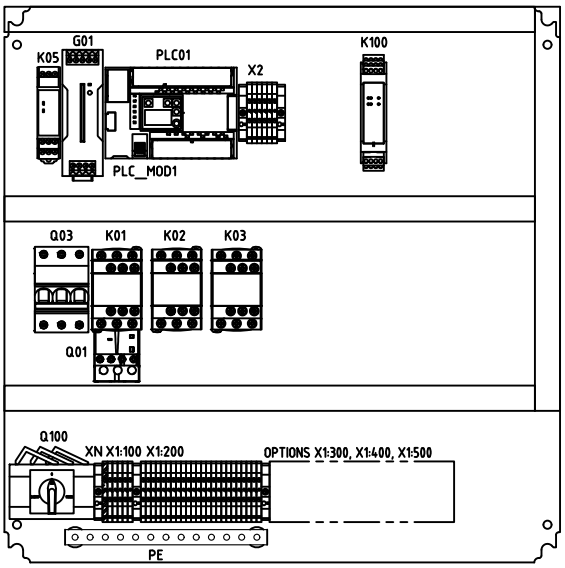

84470001

PLC I/O	
0.00	LEFT WIRE/BELT RUPTURE/BOTTOM LIMIT
0.01	RESERVED
0.02	TOP LIMIT
0.03	RIGHT WIRE/BELT RUPTURE/BOTTOM LIMIT
0.04	SAFETY RELAY
0.05	UP
0.06	STOP
0.07	DOWN N/O
0.08	DOWN N/C
0.09	SAFETY EDGE
0.10	BRAKE
0.11	VFD/CONTACTOR CHECK
1.00	EMERGENCY OPEN
1.01	SENSOR 1
1.02	SENSOR 2
1.03	SENSOR 3
1.04	POWER/PHASE MONITOR
1.05	3-PHASE LIMIT
100.00	FORWARD/UP
100.01	REVERSE/DOWN
100.02	RPM 1
100.03	RPM 2
100.04	RESERVED
100.05	RESET ENCODER
100.06	RESET VFC
100.07	BRAKE
101.00	DOOR OPEN
101.01	DOOR CLOSED
101.02	WARNING
101.03	ALARM LED

Alarm codes	
01	SAFETY RELAY
02	3-PHASE SWITCH
03	ENCODER FAULT
04	ENCODER DIRECTION
05	VFD FAULT
06	TEMP CABINET
07	CONACTOR CONTROL
08	SERVICE ALARM
09	SETUP NOT PERFORMED
10	OVERLOAD
11	LEFT WIRE/BELT RUPTURE
12	RIGHT WIRE/BELT RUPTURE
13	
14	
15	TEMP BRAKE
16	ILLEGAL POSITION LEFT
17	ILLEGAL POSITION RIGHT
18	SKEW ALARM
19	VFD BRAKE ALARM
20	PLC LOW BATTERY

Sensor settings	
1	SAFETY
2	AUT. OPEN (TIME)
3	AUT. CLOSE (TIME)
4	AUT. CLOSE (PASSAGE + TIME)
5	ALT. AUT. OPEN/CLOSE (TIME)
6	ONE BUTTON FUNCTION
7	INTERLOCK
8	AUT. OPEN/CLOSE ON/OFF
9	REDUCED OPENING ON/OFF

Page 12/12 | Date 191014 | Drawing No 60106 | Revision –

Nihva Poonawalla

Direct drive | Single motor

Panel layout

Designed MED | Approved GO | Location +A1 | Code 84470001

ASSA ABLOY

Property of ASSA ABLOY Entrance Systems AB and shall not without our written permission be copied, imparted to a third party or used for any other unauthorized purpose.

Hall & Kapell

Protects assets & equipment all over the world

MEGADOOR


Megadoor
Folding instruction pre-lined door fabrics

1. 5 cm mark in the middle of the centre line (A)
2. Folds right side up, towards centre line. (like a warehouse)
   Fold approx. 700 mm - 1000 mm on both sides towards the centre line.
3. After the last fold the back side are supposed to point upwards.

   If possible fold one side over the other (B)
4. Roll towards the centre

   The core, on which the fabric are rolled up on to (for fabrics over 140 sqm) are supposed to point out approx 5 cm outside the fabric.

   A small PVC-sign on the folded fabric shows on which side the logo is placed.

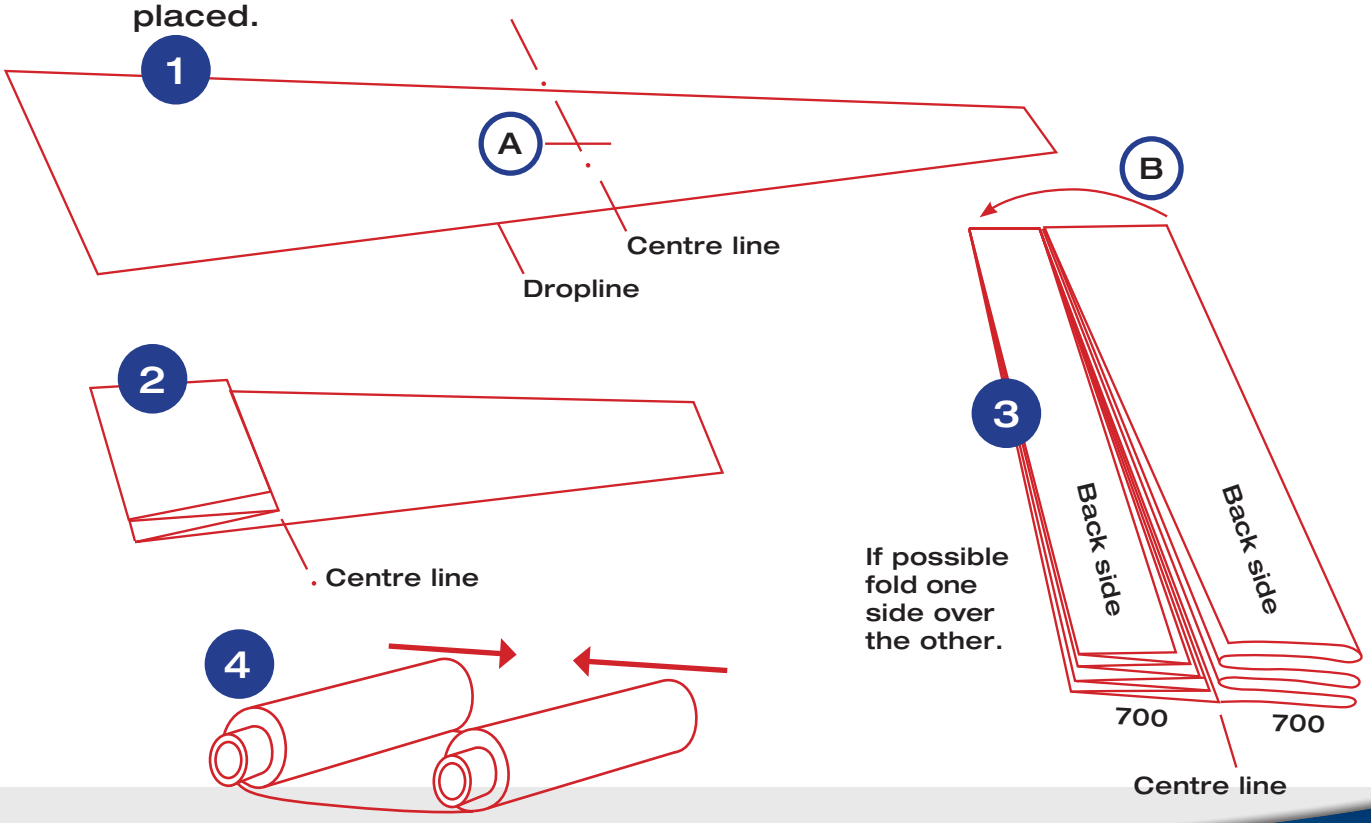

Norrlands Hall & Kapell AB
Kabelvägen 14 | 861 36 Timrå, Sweden | www.nhk.se | Phone: +46 60 - 606 20 00