


13/01/2015

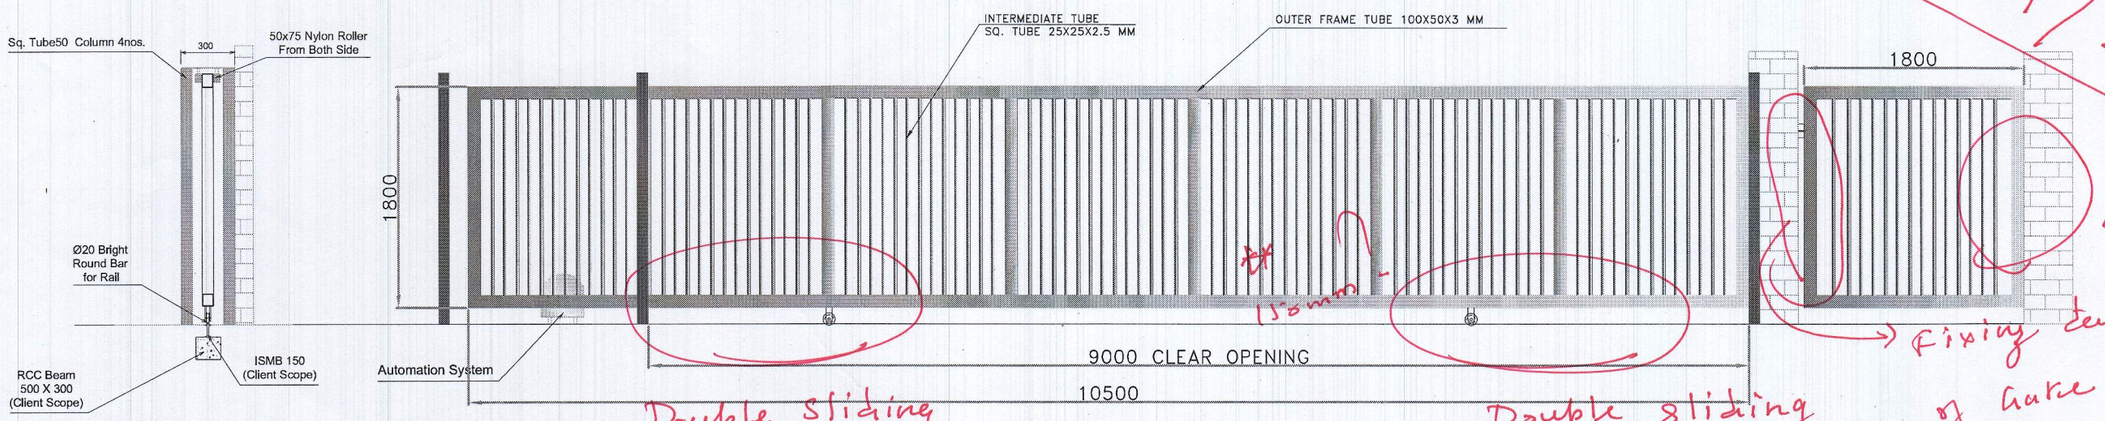

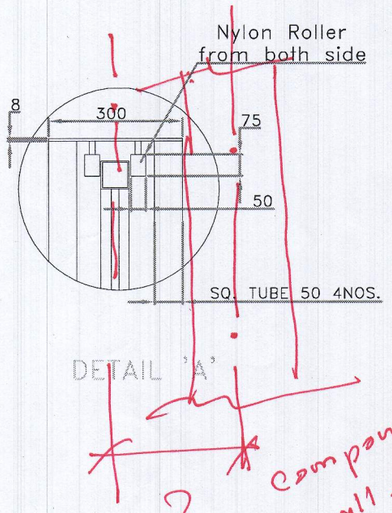

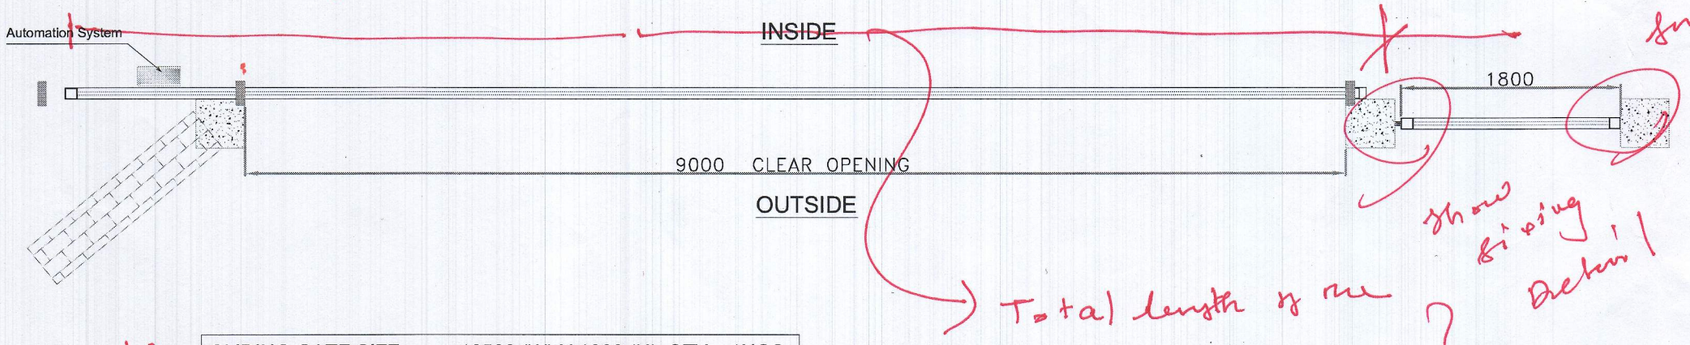


SLIDING GATE SIZE	= 10500 (W) X 1800 (H), QTY = 1NOS.
CLEAR OPENING	= 9,000 (W) X 1800 (H)
WICKET GATE SIZE	= 1800(W) X 1800 (H), QTY = 1NOS.
OUTER FRAME	= 100 X 50 X 3 mm
INNER FRAME	= 25 X 25 X 2.5 mm
GAP B/W FRAME	= 100 c/c
C\COLUMN(V) SUPPORT= 4 NOS.	(Size of the supporting column)
Total weight of sliding gate= 625 kg (APPORX).	

Please mark the column location with respect to the supporting column

Note #1

Show wiring diagram for the operation of the door & any Security Risk

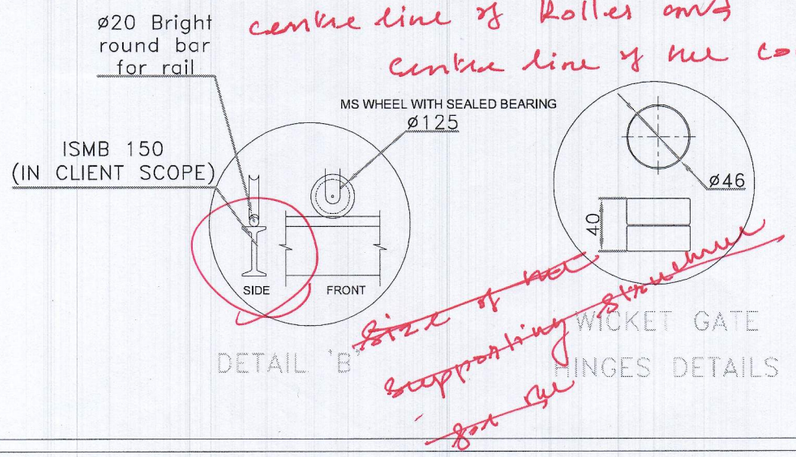

This drawing & designing is the property of NIHVA TECHNOLOGIES. Not be sold or copy to any other concern.

TITLE	ALL DIMENSION ARE IN mm		NIHVA TECHNOLOGIES PVT. LTD.	NIHVA TECHNOLOGY PVT. LTD. PUNE Tel : 020 66304033 Email:- info@nihva.com Website:- www.nihva.com
SLIDING GATE		SIGN	DATE	
	DRAWN	ABHIJIT	10/01/14	CLIENT - REWARD CONSTRUCTION
CLIENT APPROVAL	CHECK	ANIL	10/01/14	PROJECT -INGRERSOLL RAND
	REV.	04		SITE -NARODA , GUJRAT
	APPRD.			DWG. NO. - NVA/REWARD/D1/R2
	MFG			SCALE: 01 | WT: | SHEET: 01
	Ref. No.			If any queries contact : projects@nihva.com