




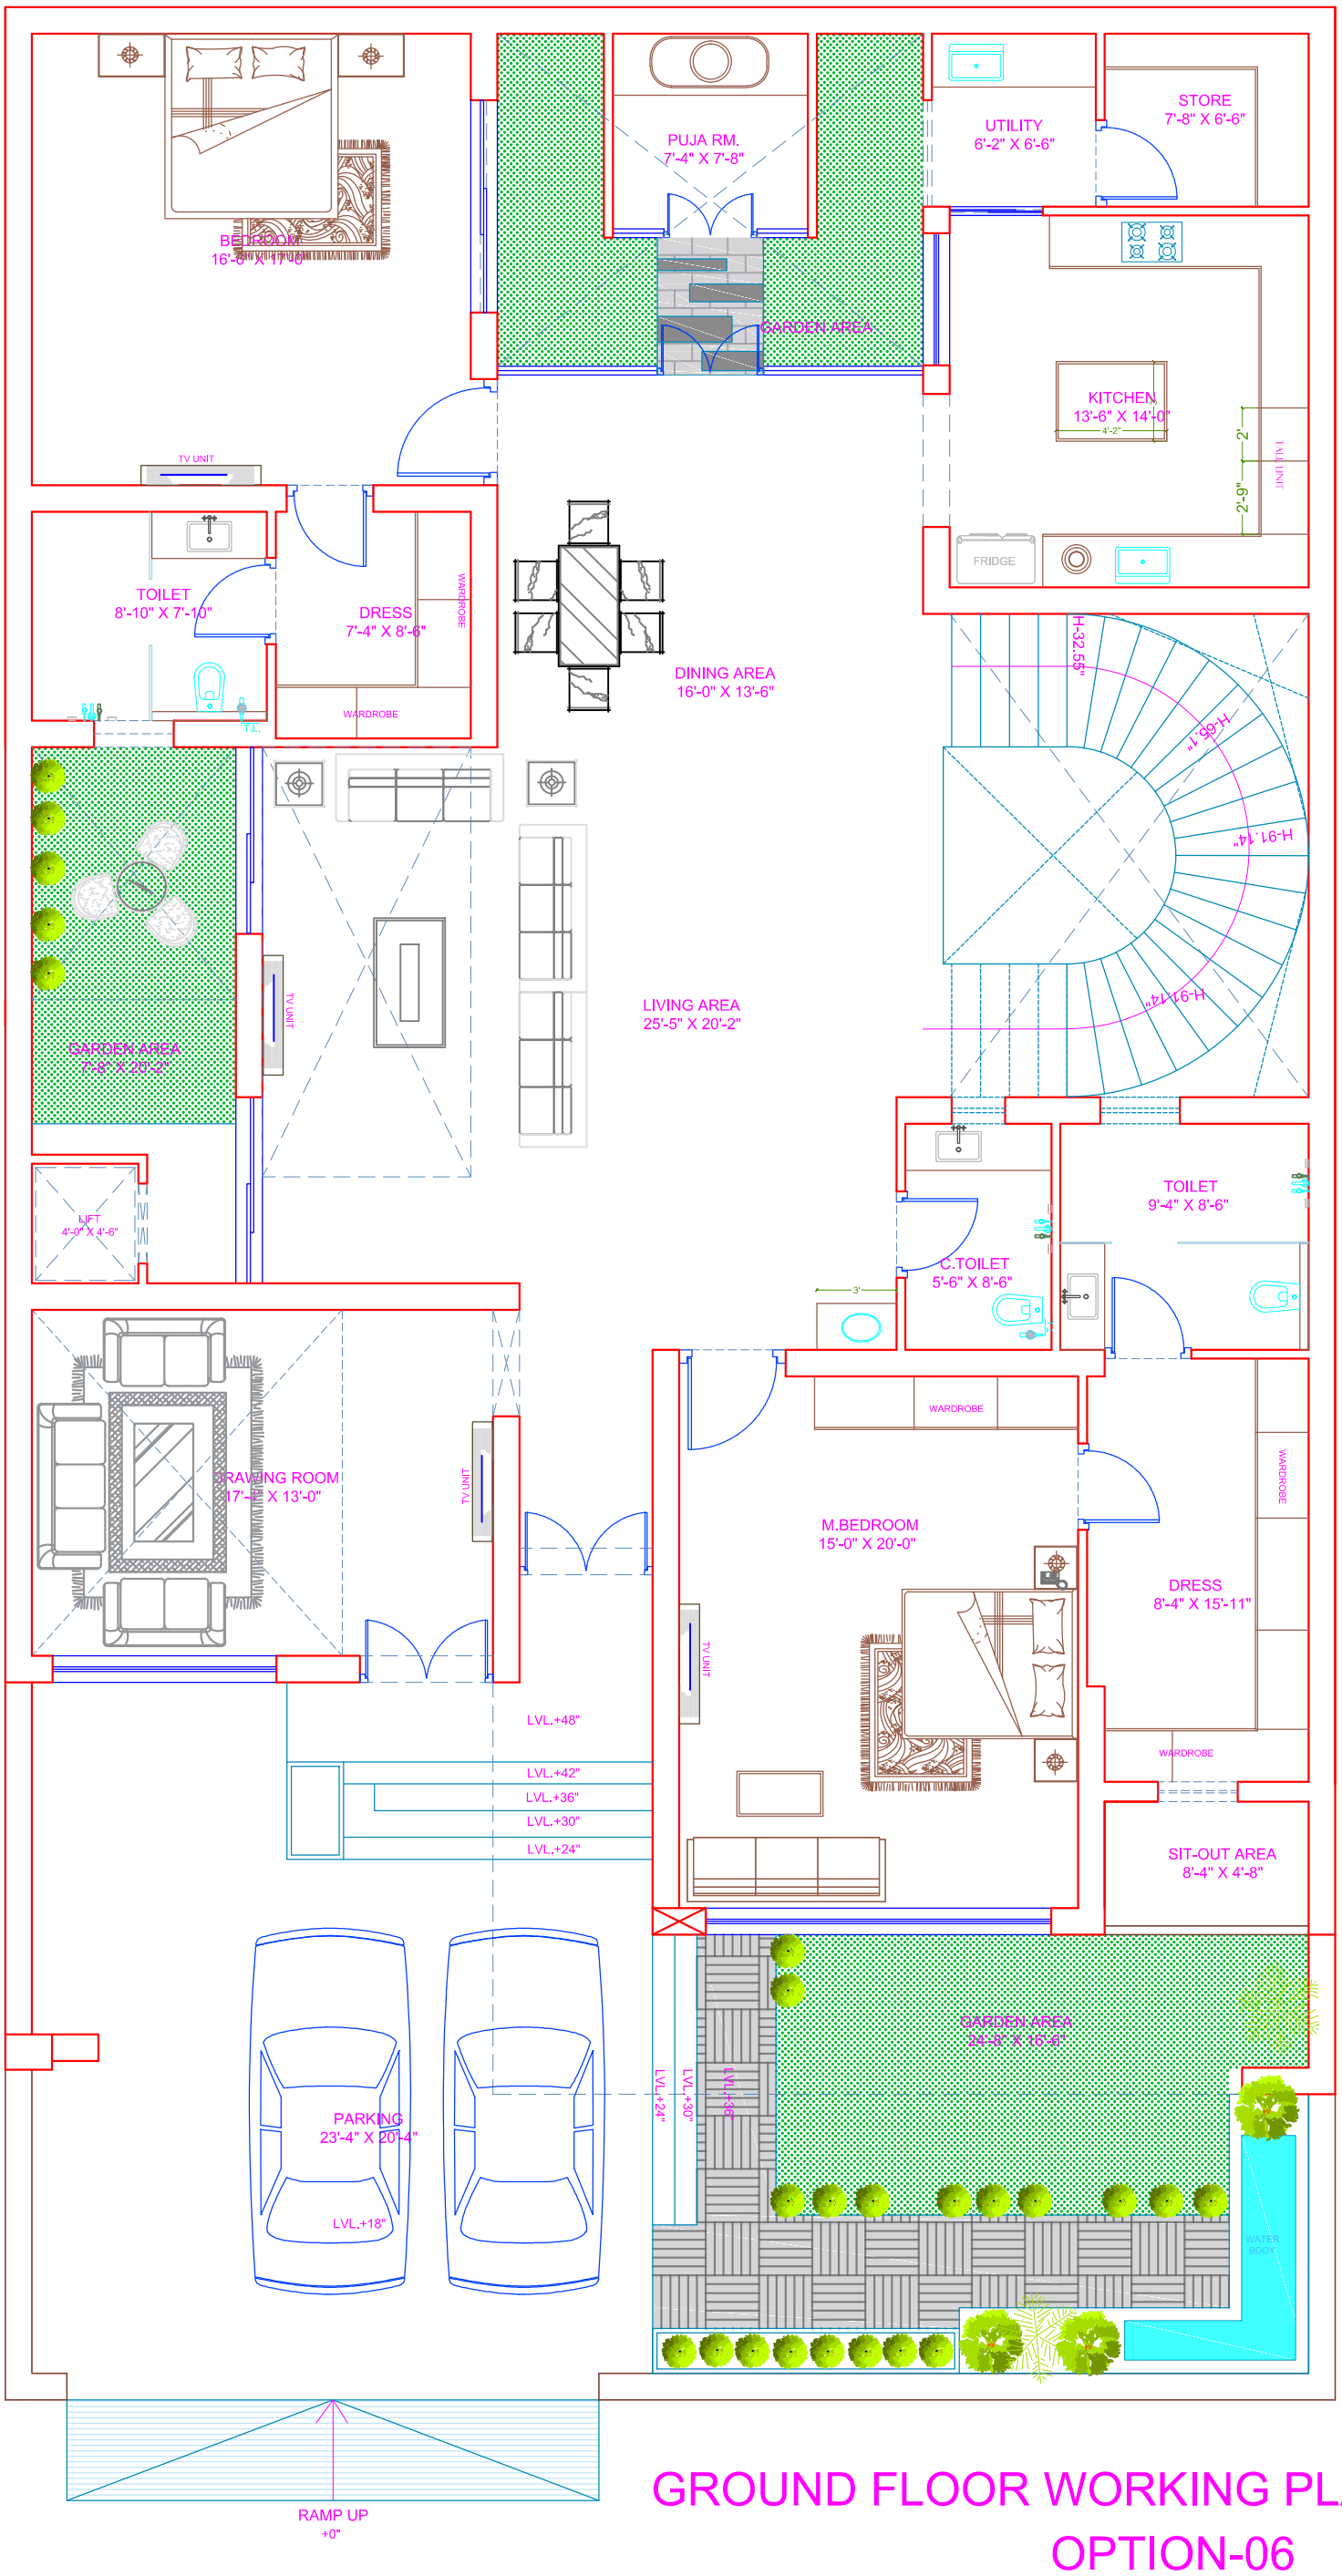


PUJA ROOM IN OPEN SPACE

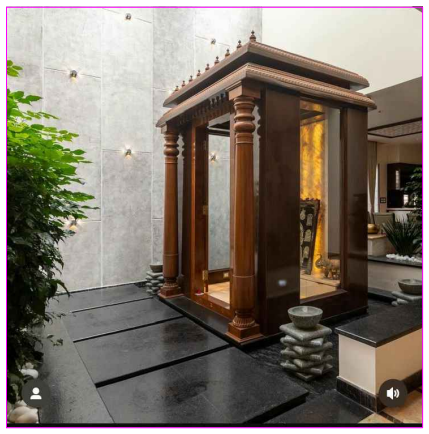


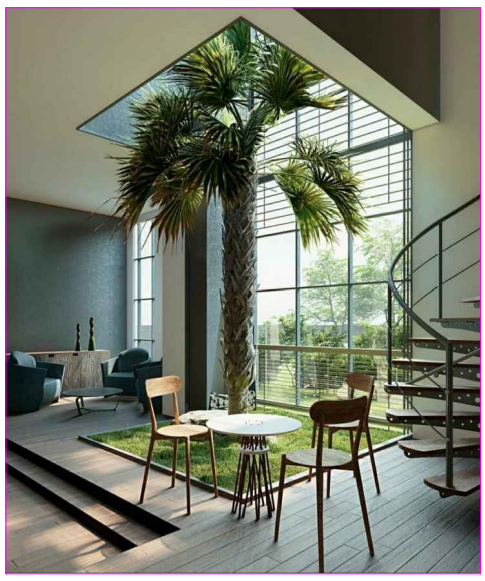

DUPLEX STAIRS WITH INDOOR GARDEN

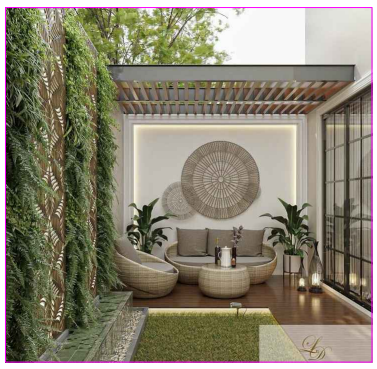

SIT-OUT GARDEN SPACE FROM LIVING AREA

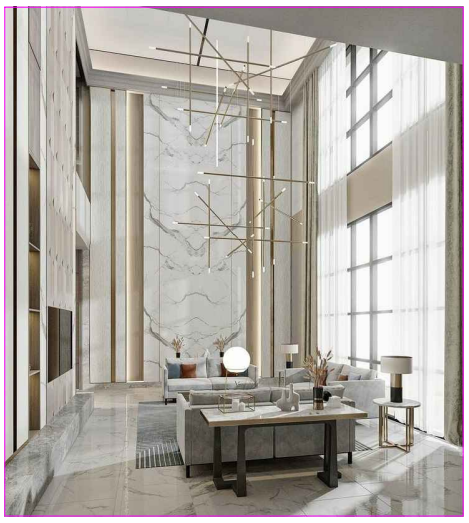

DUPLEX LIVING AREA

GROUND FLOOR WORKING PLAN
OPTION-06

NOTES :

1. THIS DRAWING IS PROPERTY OF ARCHITECT VIPUL BHARTI AND MAY NOT BE COPIED OR USED FOR ANY OTHER PROPOSE THAN FOR WHICH IT IS ISSUE ,WITHOUT PERMISSION OF ITS PRINCIPLES.
2. ALL DIMENSIONS MUST BE CHECKED AND CORRELATED WITH THE STRUCTURAL DRAWINGS AND ANY AMBIGUITY SHALL IMMEDIATELY BROUGHT TO THE NOTICE OF THE ARCHITECTS.
3. ALL DIMENSIONS ARE TO BE READ NOT TO BE MEASURED.
4. ALL DIMENSIONS ARE IN FEET AND INCHES.

REVISIONS

REMARKS	NO	DATE	ZONE

OPTION-06

SCALE : SCALED TO FIT | DEALT : ER.O.P.KUMAWAT

DATE : 17.03.2025 | CHECKED : AR.VIPUL BHARTI

PROJECT : RESIDENCE OF KULDEEP JI

DRAWING TITLE : GROUND FLOOR WORKING DRAWING

MAA ARCHITECTS & INTERIORS :
AR.VIPUL BHARTI
B-95,VINAYAK VIHAR
PF OFFICE ROAD
JODHPUR 342008
MOBILE: 9314522568

DRG.No:-

