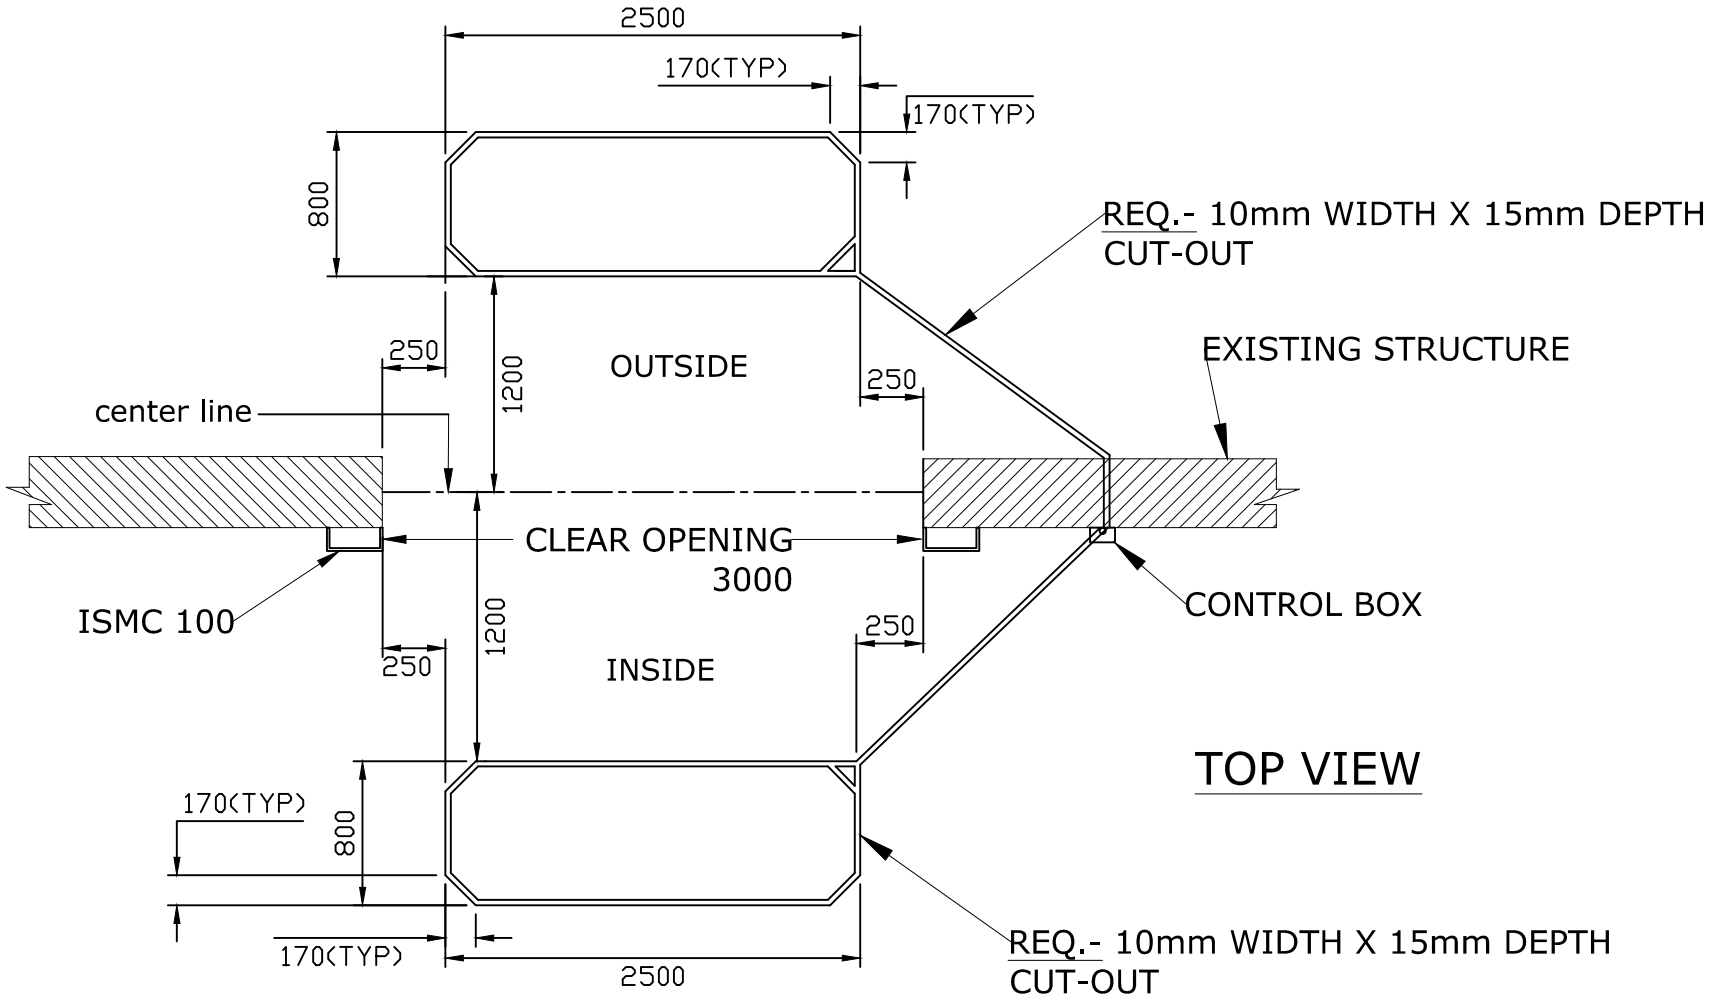


CLEAR WIDTH (CW)	CLEAR HEIGHT (CH)	QUANTITY
3000	3000	1

REV 1 - DISTANCE OF LOOP DETECTOR FROM CENTERLINE WILL BE 1200mm BOTH SIDE.

This drawing & designing is the property of NIHVA TECHNOLOGIES. Not be sold or copy to any other concern.

TITLE

FLOOR CUT-OUT FOR LOOP DETECTOR FOR HIGH SPEED DOOR (RR300)

CLIENT APPROVAL

ALL DIMENSION ARE IN mm

NIHVA TECHNOLOGIES PVT. LTD.

NIHVA TECHNOLOGY PVT. LTD. PUNE
Tel : 020 66304033
Email:- info@nihva.com
Website:- www.nihva.com

	SIGN	DATE	
DRAWN	SURAJ	18/01/17	CLIENT -GE INDIA INDUSTRIAL PVT. LTD
CHECK	OMKAR	18/01/17	PROJECT-
ENG			SITE - MIDC PHASE 2, CHAKAN
APPRD.	R.K	18/01/17	DWG. NO. - NIHVA/16-17/126/R01
MFG			SCALE: NTS | WT: | SHEET: 01
Ref. No.			If any queries contact : projects@nihva.com