
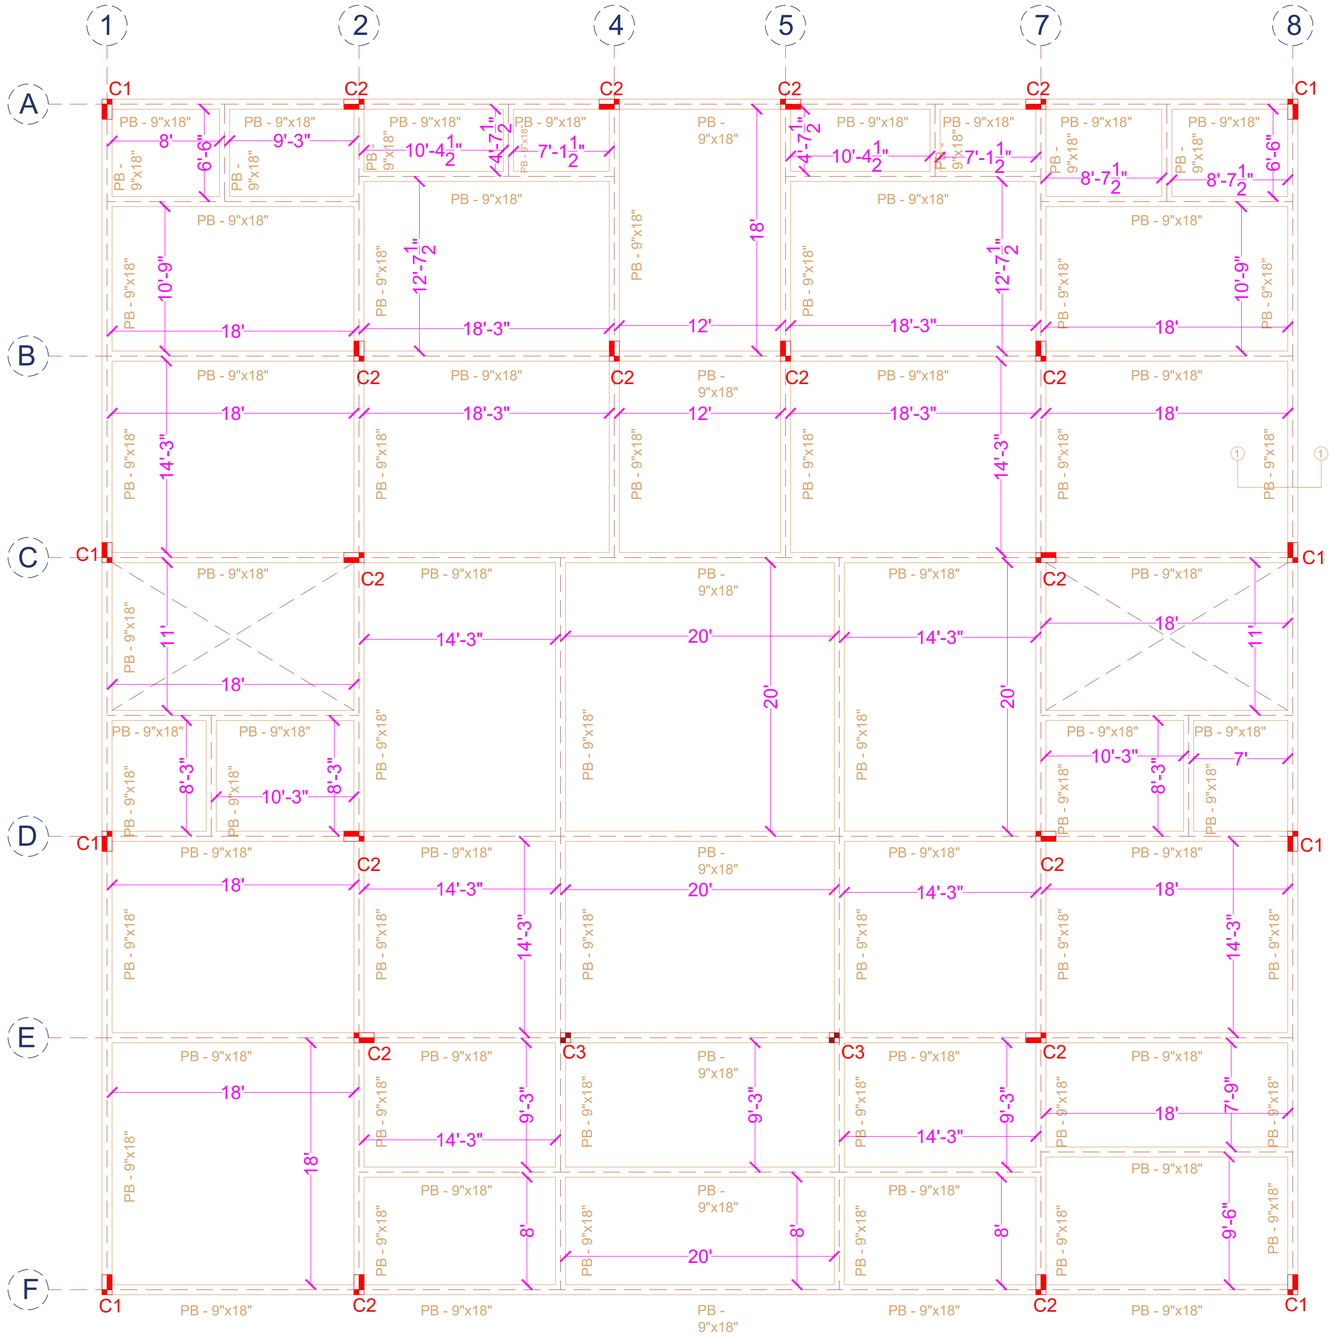



## PLINTH BEAM (PB)

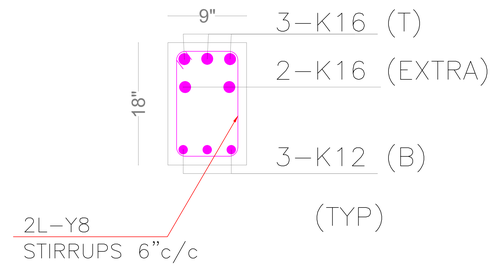


## Section 1–1

NOTES:

1. Grade of concrete :M25
2. Grade of steel : Fe415
3. Lap length


| Ø of bar | 8mm | 10mm | 12mm | 16mm | 20mm |
|---|---|---|---|---|---|
| Lap | 40 cm | 50cm | 60cm | 80cm | 100cm |

4. Do not scale this drawing, Only written dimensions are to be followed.
5. All dimensions are in feet and inches.
6. Clear cover:

| Footings | Columns | Beams | Slab |
|---|---|---|---|
| 5cm | 4 cm | 2.5cm | 2cm |

7. The structure is designed for Stilt+5 floors.
8. SBC of soil is taken as 300 kN/Sq. M.
9. These drawings ,details Specifications,Quantities are based on the information supplied by the Owner, Builder,promoter etc.

**LEGEND :**

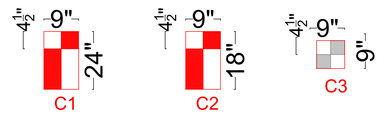


CLIENT : **Sri. Dr G.Venkata Prasad Garu @ Perupalem.**

PLINTH BEAM DIAGRAM

| | | |
|---|---|---|
| DRG NO. :C/1/2. | REV: 01. | SHT.NO. 1 |
| SCALE : NOT TO SCALE | DATE: 04-03-2022 | |

**Architect:** SARADHI ASSOCIATES — Consulting Architects, Engineers & Interiors