



Tolerance ±3 mm (for all dimensions)

Dimensions in [ ] ==> clearance for installation

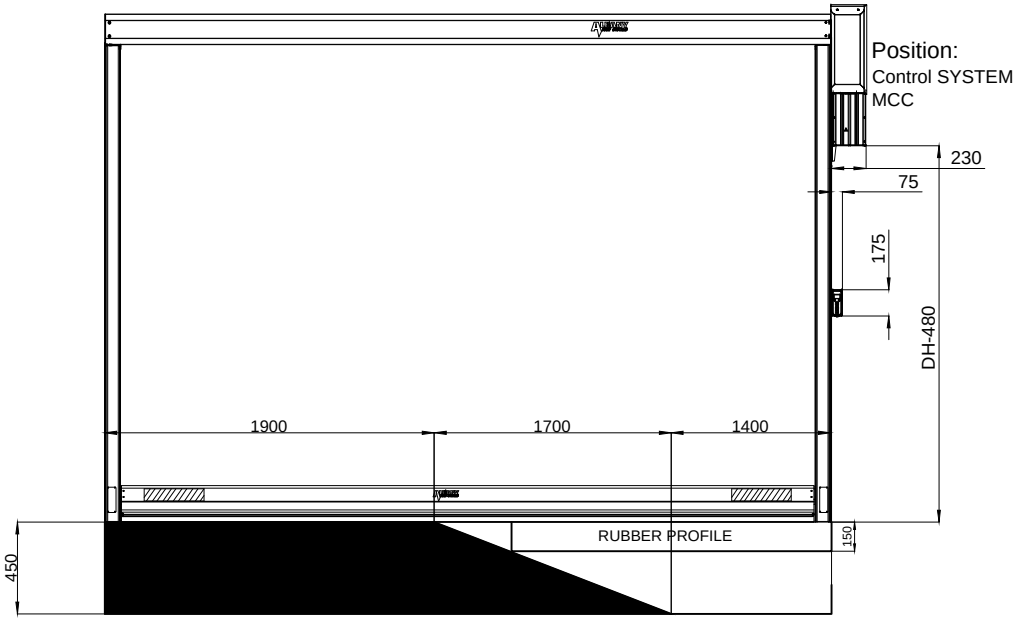

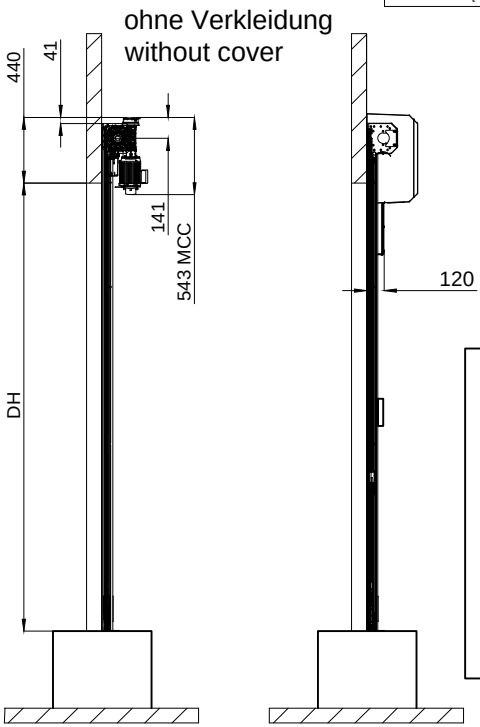

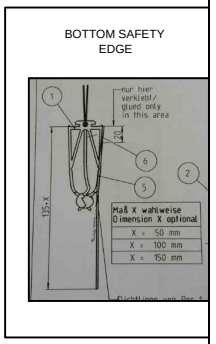

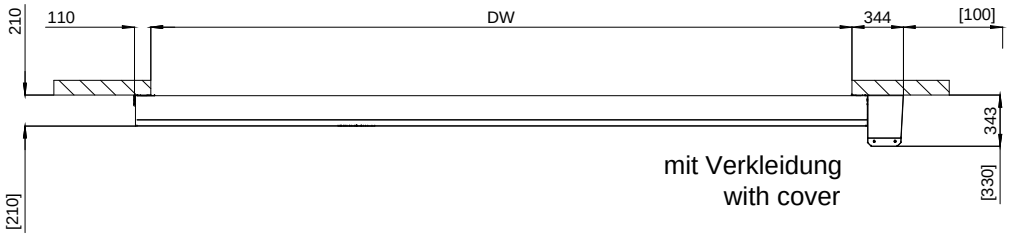

NOTE : ALL CIVIL & STRUCTURAL WORK WILL BE IN CLIENT SCOPE.

CLEAR WIDTH(DW)	CLEAR HEIGHT(DH)	QTY
5000 MM	3000 MM	02 NOS

This drawing & design is the property of NIHVA TECHNOLOGIES. Not to be sold or copied to any other concern.

TITLE	NAME	SIGN	DATE	
HIGH SPEED DOOR RP300 WIDE				NIHVA TECHNOLOGIES PVT. LTD. PUNE
DRAWN	P.V.A		07.09.19	CLIENT :- WOOSHIN
CHECK	V.M.T		07.09.19	PROJECT :-
APPV'ED				LOCATION :-

NIHVA TECHNOLOGIES PVT. LTD.
Tel : 020 66304033
Email:- info@nihva.com
Website:- www.nihva.com

If any queries contact : design@nihva.com

DWG. NO. :- NIHVA/19-20/0094 REV.:-00

ALL DIMENSION ARE IN mm

SCALE: NTS WT: SHEET: 01 OF 01