


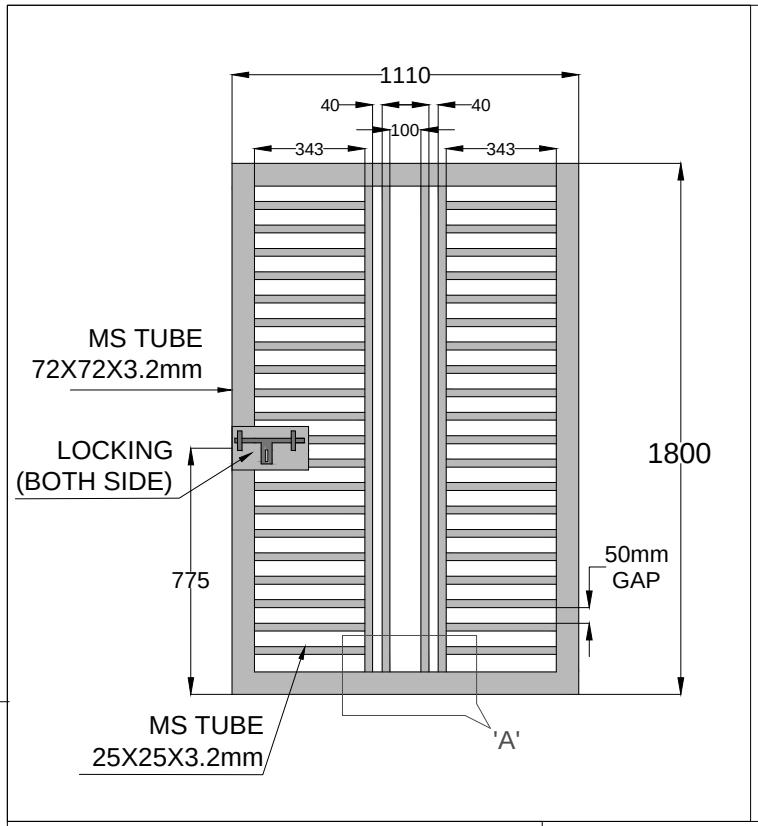


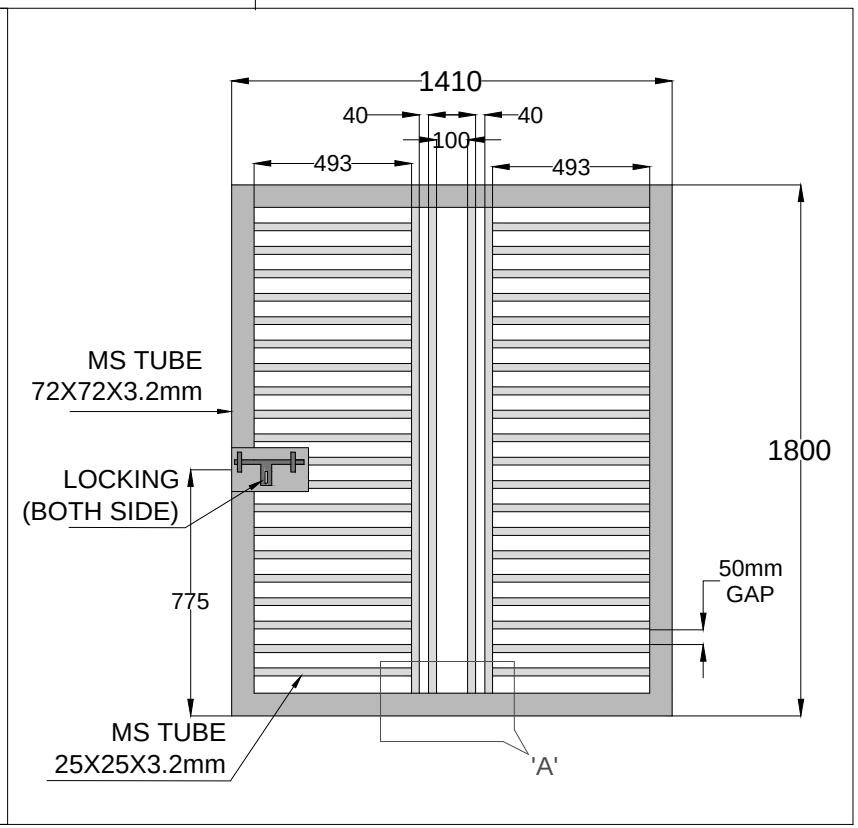

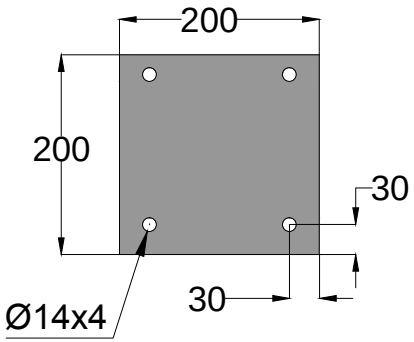

FIXING PLATE

MATERIAL- MILD STEEL
THICKNESS- 10mm
QTY:-04 NOS

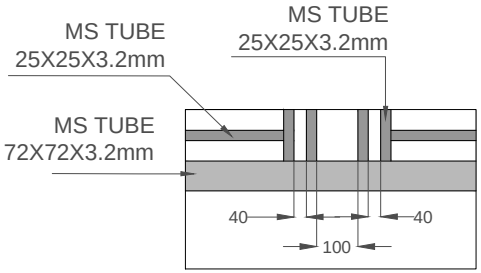

DETAIL VIEW 'A'

REV03:(13/04/2018) -A).HEIGHT REVISED.
REV02:-A).HEIGHT REVISED & LOCKING SYSTEM HEIGHT.
REV01:-A).HEIGHT REVISED.

SR NO	CLEAR WIDTH	CLEAR HEIGHT	QTY.
1	1110mm	1800mm	01NOS
2	1410mm	1800mm	01NOS

This drawing & design is the property of NIHVA TECHNOLOGIES. Not to be sold or copied to any other concern.

TITLE
WICKET GATE LEAF 3 & 4
& FIXING PLAT

NIHVA
NIHVA TECHNOLOGIES PVT. LTD.

NIHVA TECHNOLOGIES
PVT. LTD. PUNE
Tel : 020 66304033
Email:- info@nihva.com
Website:- www.nihva.com

	NAME	SIGN	DATE
DRAWN	SURAJ		03-04-2018
CHECK	OMKAR		03-04-2018
APPRD.	SHEKHAR		03-04-2018

CLIENT -
PROJECT -
SITE LOCATION -

If any queries contact : design@nihva.com
DWG. NO. : NIHVA/17-18/VDR/0274/R03.
REV- 03

ALL DIMENSION ARE IN mm
SCALE: NTS
WT:
SHEET: 01 OF 01