
ALL SIDE
CHA
10 X 45°

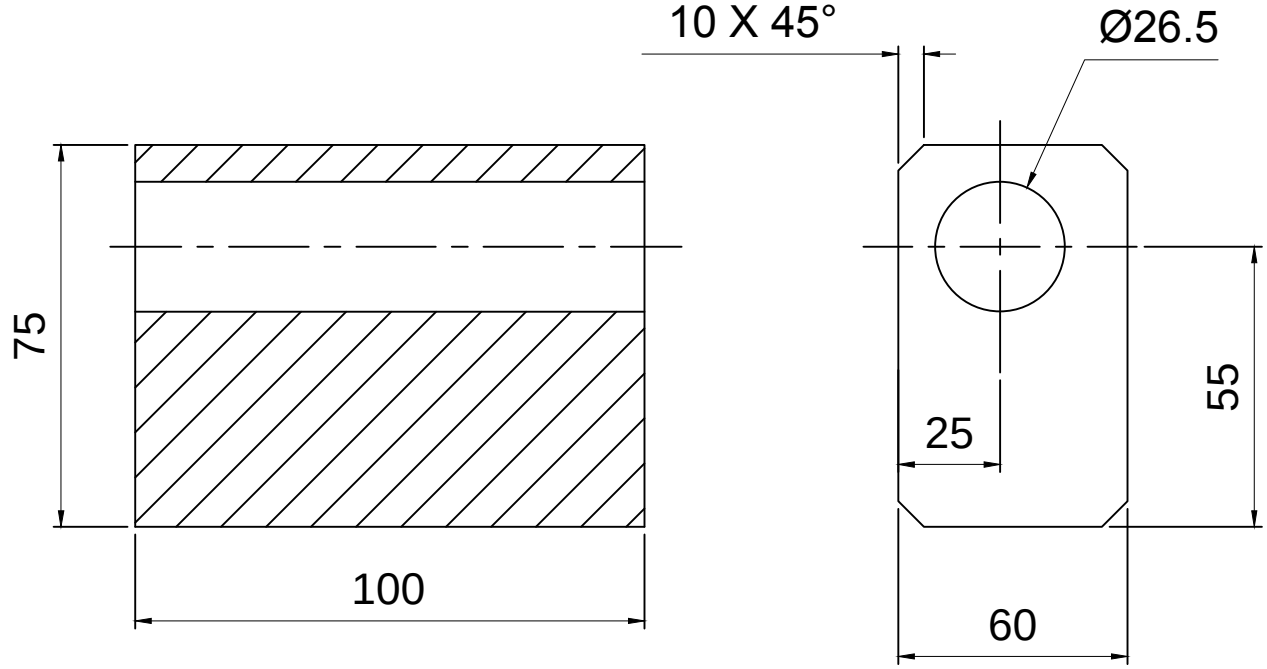


BACK SIDE HINGE BLOCK
MTL = M.S
75 X 60 THK X 103L = 5 NOS

This drawing & design is the property of NIHVA TECHNOLOGIES. Not to be sold or copied to any other concern.

| TITLE: BACK SIDE HINGE BLOCK | | | | NIHVA TECHNOLOGIES PVT. LTD. PUNE<br>Tel : 020 66304033<br>Email:- info@nihva.com<br>Website:- www.nihva.com | | |
|---|---|---|---|---|---|---|
| | NAME | SIGN | DATE | | | |
| DRAWN | P.A | | 20.08.2020 | CLIENT - | | |
| CHECK | G.J | | 20.08.2020 | PROJECT - NDL_630_631 | | |
| APPRD. | | | | SITE LOCATION - | | |
| If any queries contact : design@nihva.com | | | | DWG. NO. : NIHVA/20-21/VDR/0057 | | |
| ALL DIMENSION ARE IN mm | | | | SCALE: NTS | WT: | REV- 00 |