


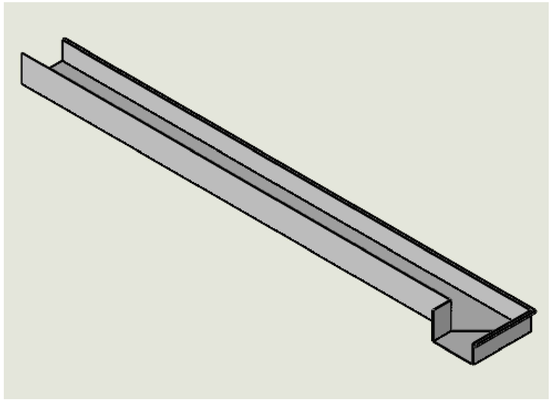


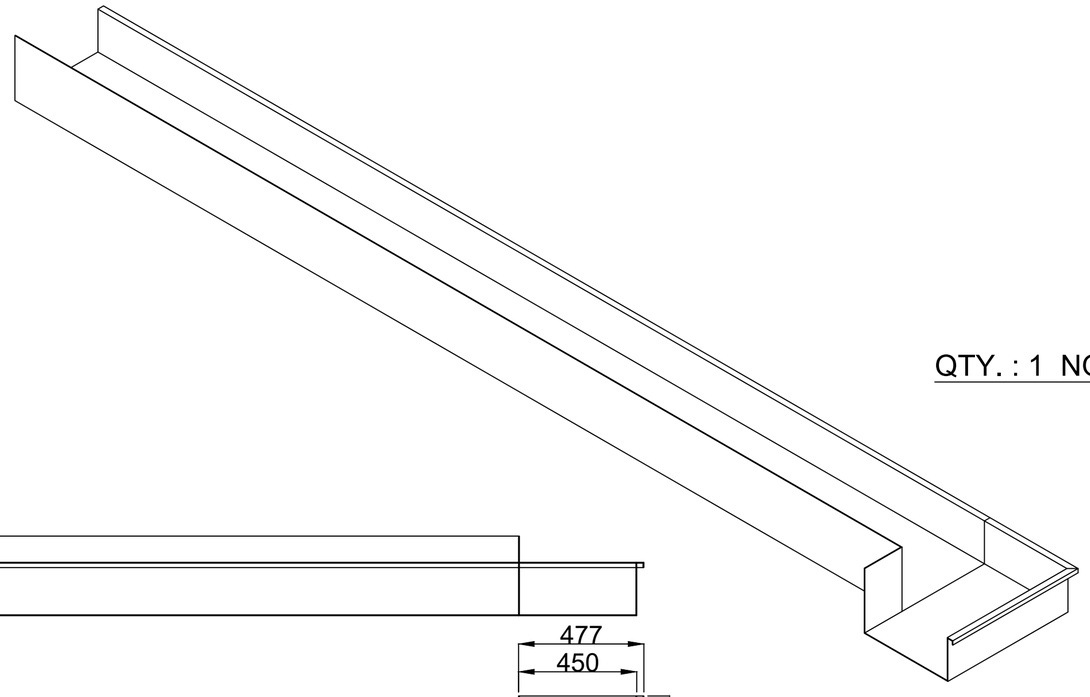


QTY. : 1 NOS.

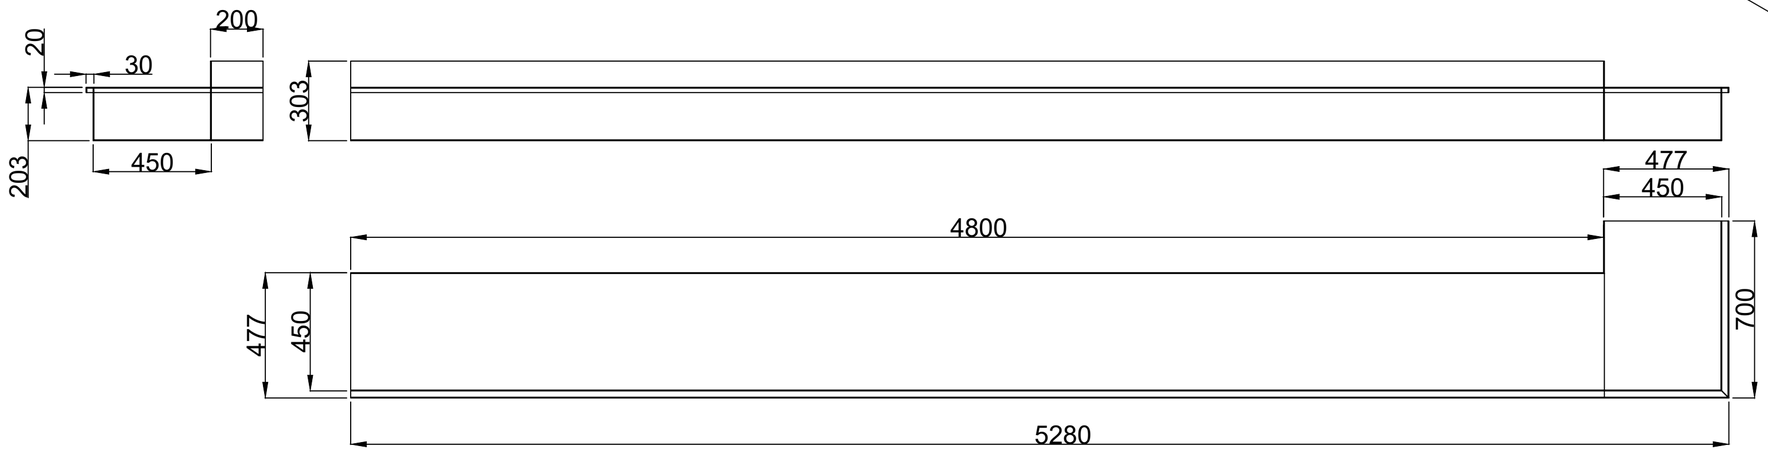

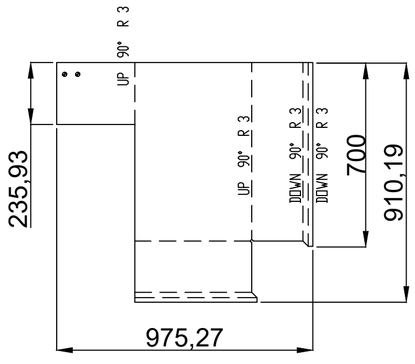

QTY. : 1 NOS.

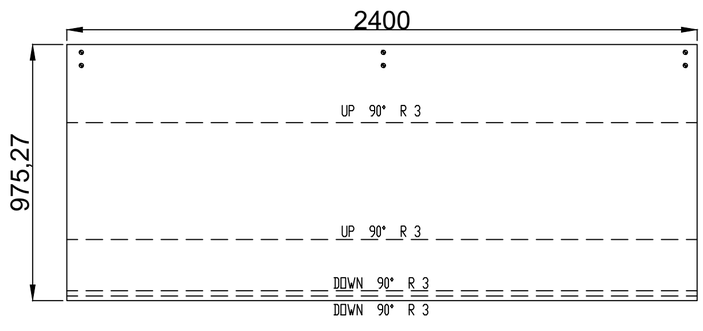

QTY. : 2 NOS.

REV NO.	DESCRIPTION	Date	Revised By

TITLE:- FRONT DRAIN TRAY

	NAME	DATE	SIGN
DRAWN	MAHESH S.	19/10/22	
CHECK	MAHESH S.	19/10/22	
APPRD.	VIJAY T.	19/10/22	

If any queries contact : design@nihva.com

ALL DIMENSION ARE IN mm

NIHVA TECHNOLOGIES PVT. LTD.

NIHVA TECHNOLOGIES PVT. LTD. PUNE
Tel : 020 66304033
Email:- info@nihva.com
Website:- www.nihva.com

CLIENT - NIHVA TECHNOLOGIES PVT.LTD

LOCATION -

PRODUCT: FIX & RETRACTABLE ROOF

DWG NO:-NIHVA/22-23/MFG/0048 | REV- 0

SCALE: NTS | SCALE:-- 1:1 | SHEET: 01 OF 01