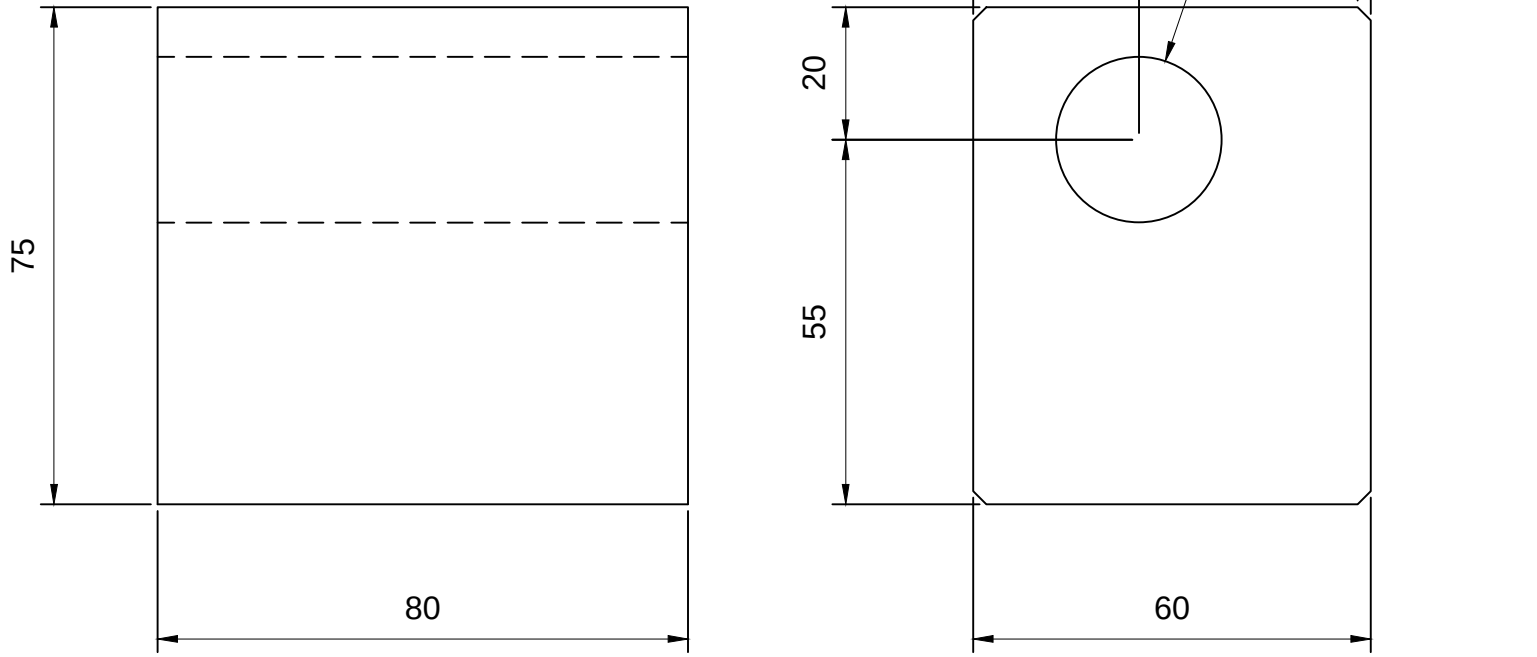


BACK SIDE HINGE BLOCK = 04 NOS
MTL = M.S
75 X 60 THK X 83L = 04 NOS

This drawing & design is the property of NIHVA TECHNOLOGIES. Not to be sold or copied to any other concern.

TITLE			
BACK SIDE HINGE BLOCK			
	NAME	SIGN	DATE
DRAWN	PRADEEP		05.09.2018
CHECK	PRADEEP		05.09.2018
APPRD.	PRADEEP		05.09.2018
If any queries contact : design@nihva.com			
ALL DIMENSION ARE IN mm			

NIHVA TECHNOLOGIES PVT. LTD.
NIHVA TECHNOLOGIES PVT. LTD. PUNE
Tel : 020 66304033
Email:- info@nihva.com
Website:- www.nihva.com

CLIENT -			
PROJECT - DLSD1010			
SITE LOCATION -			
DWG. NO. : NIHVA/18-19/MFG/DLSD1010/017			
SCALE: NTS	WT:	REV- 00	