


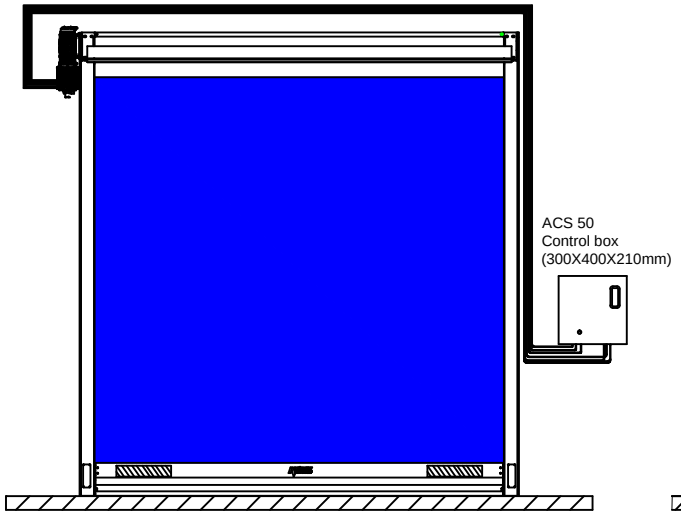


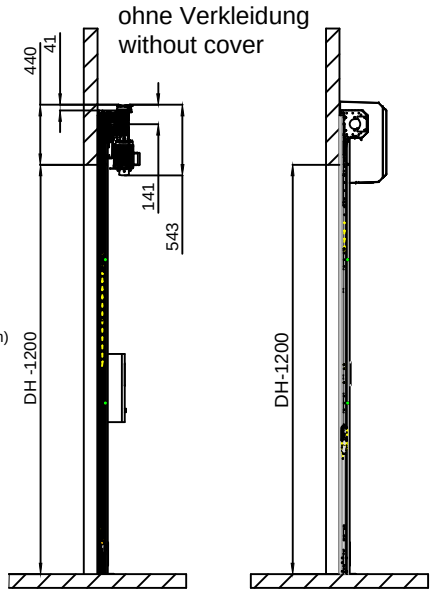


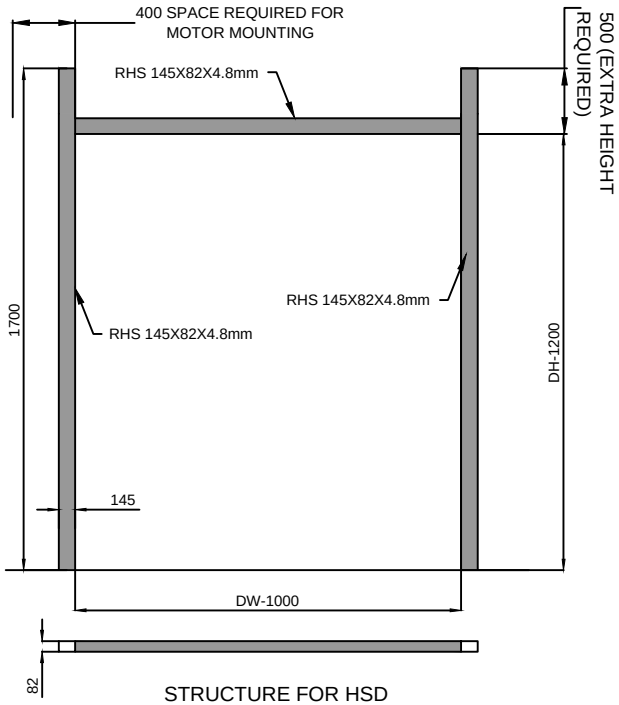

STRUCTURE FOR HSD

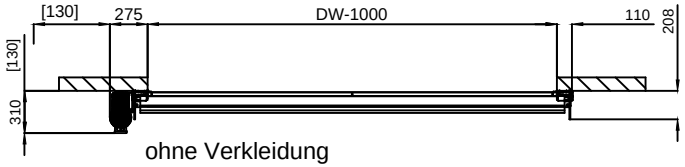

ohne Verkleidung
without cover

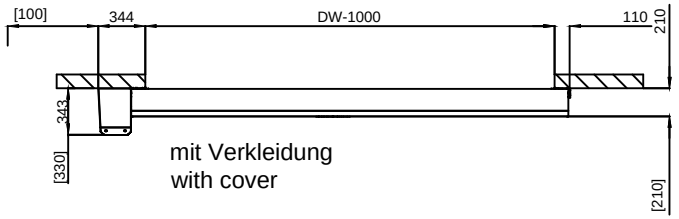

mit Verkleidung
with cover

Tolerance ±3 mm (for all dimensions)
Dimensions in [ ] ==> clearance for installation

COLORS -
1. BLUE (RAL 5002)

CURTAIN TYPE:-ROLLTEX

CLEAR WIDTH(DW)	CLEAR HEIGHT(DH)	MOTOR MOUNTING	QUANTITY
1000mm	1200mm	RIGHT SIDE	01 NO

NOTE -
1.STRUTURE REQUIRED FOR HSD IS IN CLIENT'S SCOPE.

This drawing & design is the property of NIHVA TECHNOLOGIES. Not to be sold or copied to any other concern.

TITLE	HIGH SPEED DOOR RP300 & STRUCTURE			NIHVA TECHNOLOGIES PVT. LTD. PUNE
	NAME	SIGN	DATE	Tel : 020 66304033 Email:- info@nihva.com Website:- www.nihva.com
DRAWN	P.A		17.03.20	CLIENT :-
CHECK	G.J		17.03.20	PROJECT :-
APPV'ED				LOCATION :-
If any queries contact : design@nihva.com				DWG. NO. :- NIHVA/19-20/VDR/374 REV.:- R00
ALL DIMENSION ARE IN mm				SCALE: NTS WT: SHEET: 01 OF 01