

SLIDING DECK LAYOUT

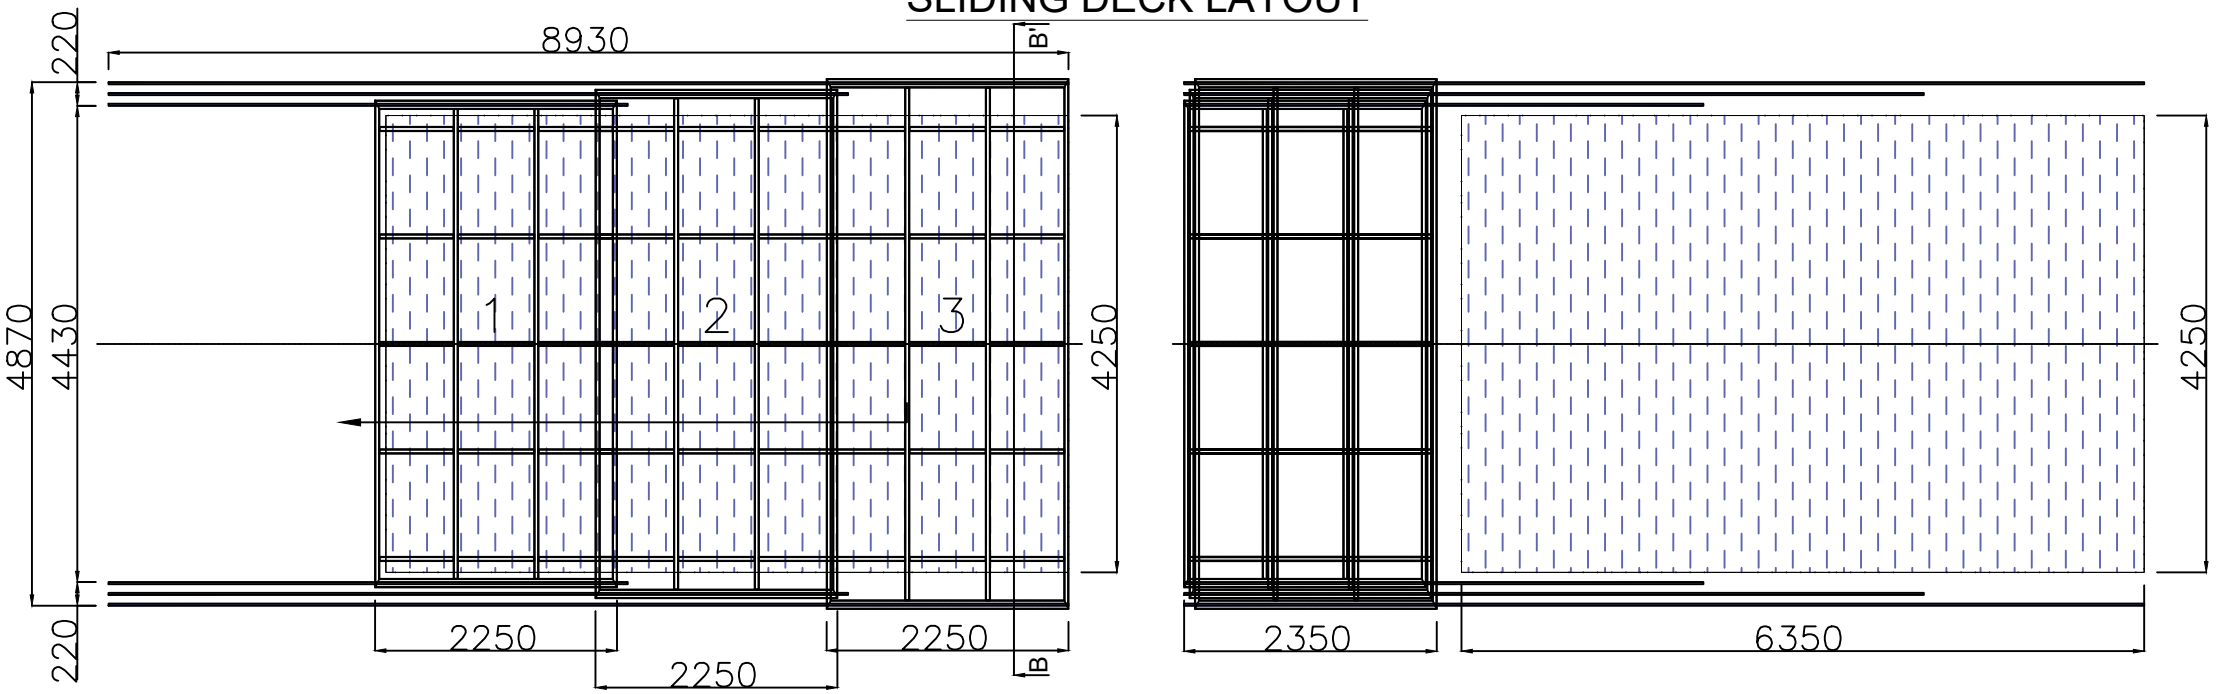

ENCLOSED VIEW

STACKED VIEW

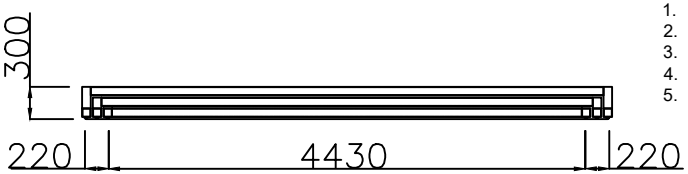

SECTION B-B'

1. SS GRADE - SS 304/SS 316/SS 316L
2. SS SECTION - 80X40 MM/80X80 MM/40X40 MM
3. TOP AL SHEET (OPTIONAL)
4. GASKET - EPDM
5. ALL DIMENSION IN MM.

This drawing & design is the property of NIHVA TECHNOLOGIES. Not to be sold or copied to any other concern.

TITLE				
SLIDING POOL DECK				NIHVA TECHNOLOGIES PVT. LTD. PUNE Tel : 020 66304033 Email:- info@nihva.com Website:- www.nihva.com
	NAME	SIGN	DATE	
DRAWN	G.J.		30.04.22	CLIENT - ATS VILLA
CHECK	A.K.		30.04.22	LOCATION - NEW DELHI_IN
APPRD.	V.T.		30.04.22	PRODUCT - RETRACTABLE ROOF
If any queries contact : projectsautomation@nihva.com				NIHVA\22-23\0026 REV- 0
ALL DIMENSION ARE IN mm				SCALE: NTS SHEET: 01 OF 01