

THIS PRINT IS THE PROPERTY OF NIHVA TECHNOLOGIES PVT LTD
RETURNED UPON REQUSETHIS PART MUST NOT BE SOLD TO ANY OTHER CONCERN

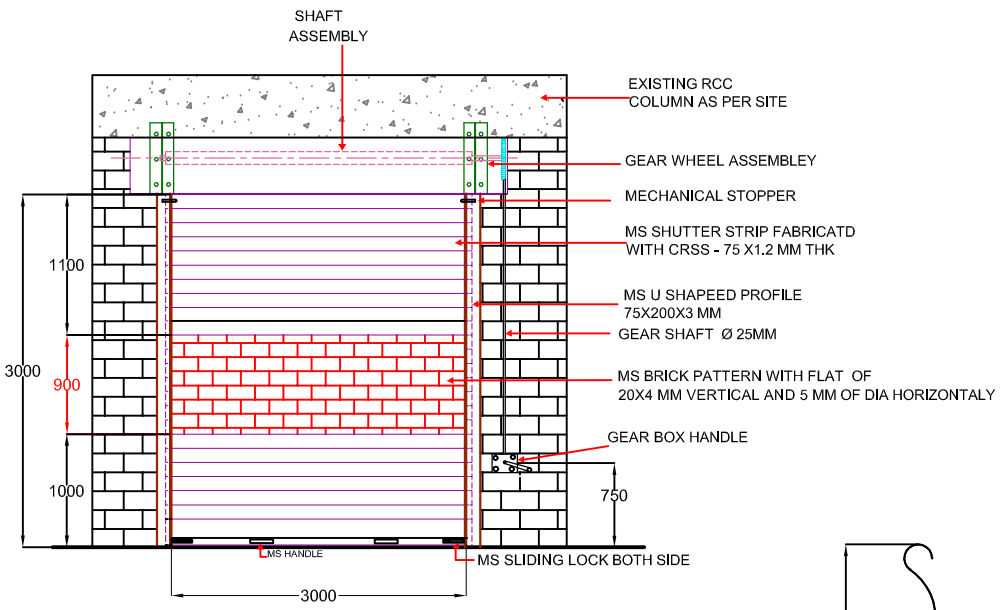


INSIDE ELEVATION


Clear Opening size:-
(W)3.0m x (H)3.0m

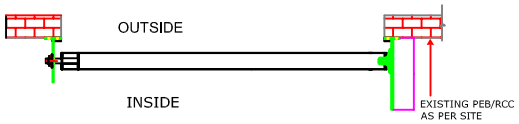


PLAN

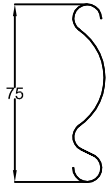


Curve Type MS Shutter lath fabricated with CRS strip 18 gauge

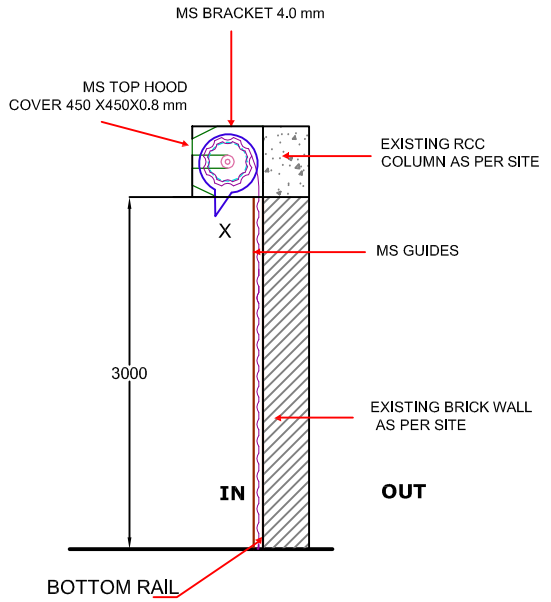

SIDE VIEW

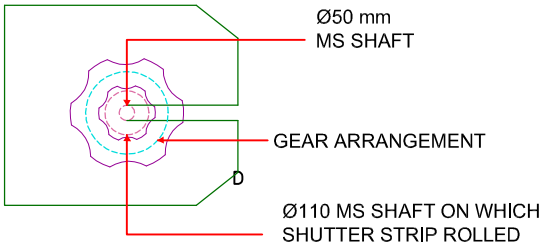

Bracket

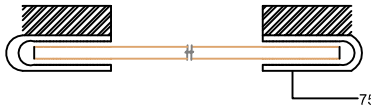

Side guide

Location :- Substation
Size :- 3.0m(W) X 3.0M (H)

TITLE: Grilled Manual Gear Operated Rolling Shutter - GRS 1	DO NOT SCALE DRAWING		NIHVA TECHNOLOGIES PVT. LTD. Pune:-411044 Tel :- 020 66304033 Email :- info@nihva.com
		SIGN	DATE	
CLIENTS APPROVEL:-	DRAWN	Anil		CLIENT:
	CHECK			PROJECT / SITE:
	ENG			PRODUCT NAME:
ALL DIMENSION ARE IN M.M.	APPRD.			DWG. NO.:
	PROD			REV.: 0
	MFG			
	Ref. No.			SCALE: NTS WT: SHEET: 1 OF 1