
PRODUCED BY AN AUTODESK EDUCATIONAL PRODUCT

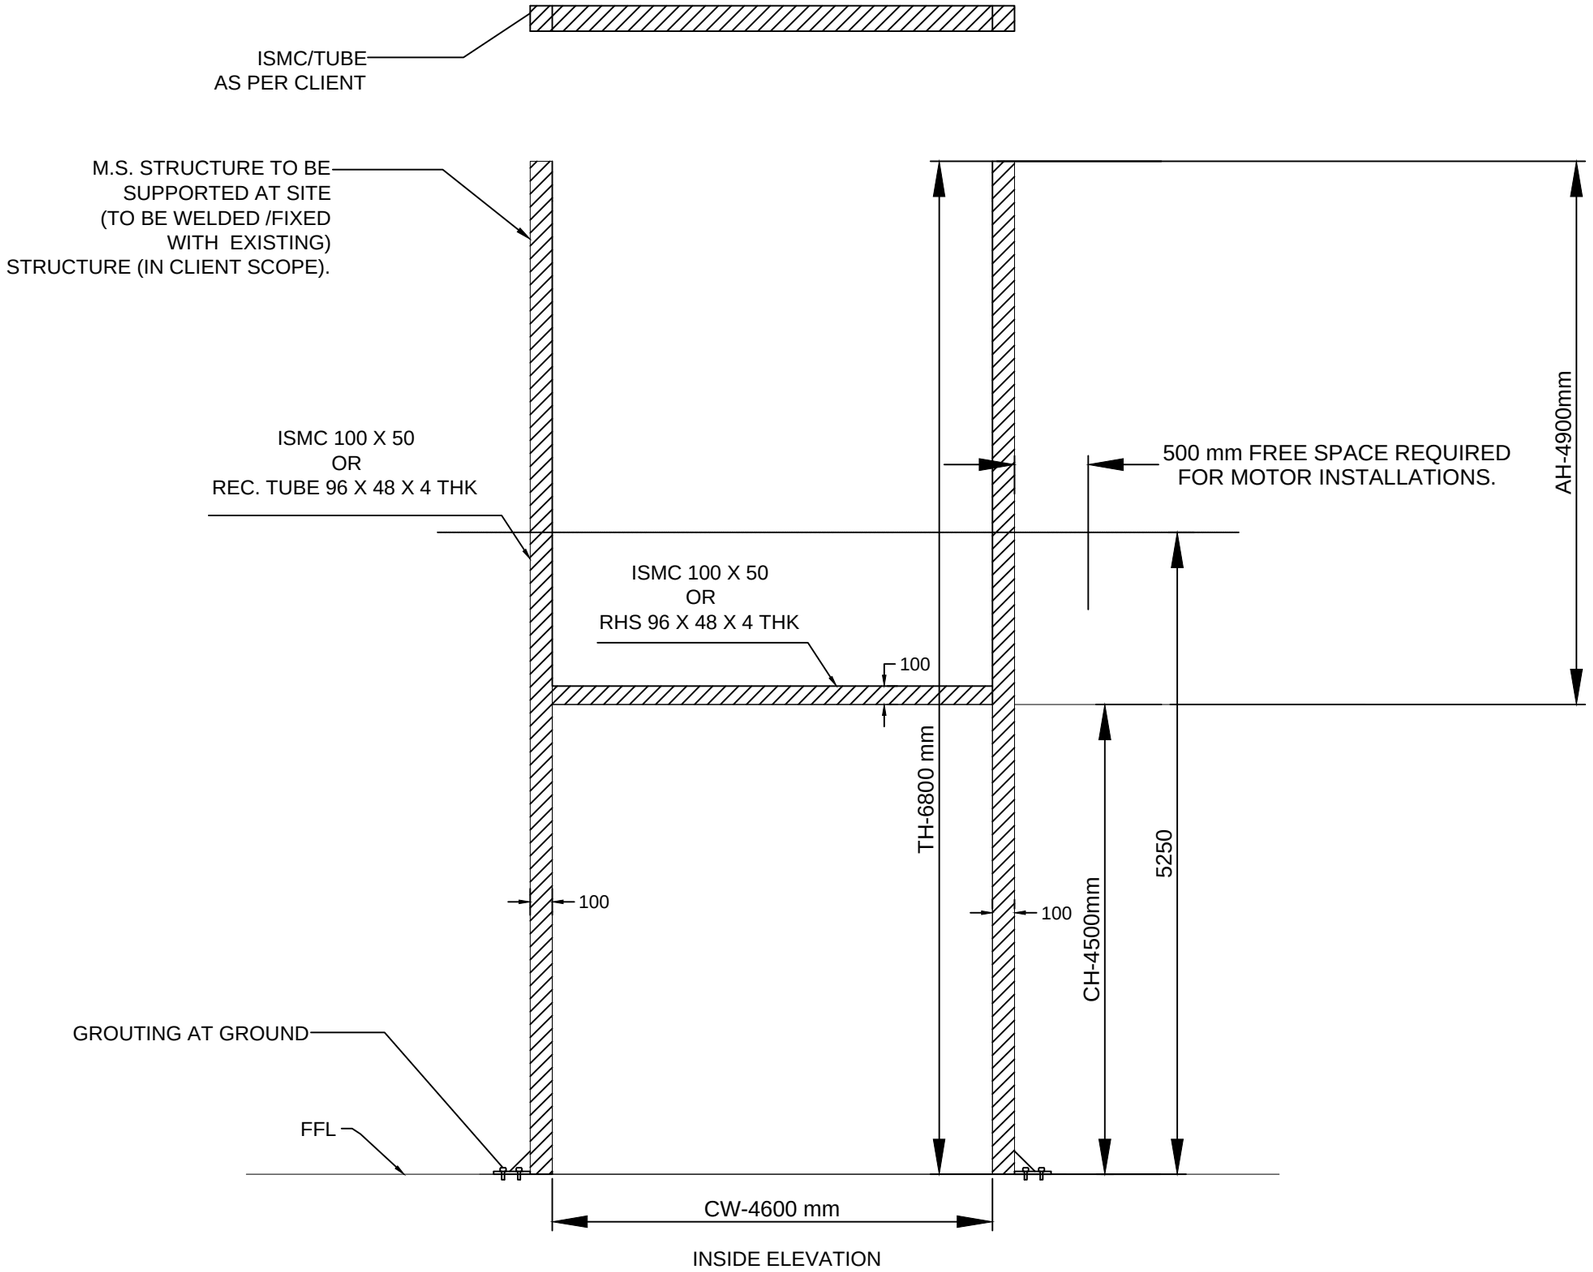

INSIDE ELEVATION

SR NO	CLEAR WIDTH CW	CLEAR HEIGHT CH	AH	QTY
1	4600 mm	4500mm	4900	1 nos

NOTES-
(1) REQUIRED M.S. STRUCTURE , FITTING & ALL CIVIL WORK IN CLIENT SCOPE .
(2) PRODUCT WILL BE INSTALLED AFTER READINESS OF STRUCTURE AS PER DRAWING.

This drawing & design is the property of NIHVA TECHNOLOGIES. Not to be sold or copied to any other concern.

TITLE: STRUCTURE FOR SECTIONAL DOOR

NIHVA TECHNOLOGIES PVT. LTD.
NIHVA TECHNOLOGIES PVT. LTD. PUNE
Tel : 020 66304033
Email:- info@nihva.com
Website:- www.nihva.com

	NAME	SIGN	DATE
DRAWN	G.P.		23.12.2021
CHECK	A.K.		23.12.2021
REV.			
APPROVAL			

CLIENT -AJAY KALE AND ASSOSIATES
PROJECT -
SITE LOCATION -
DWG. NO. : NIHVA/21-22/CLT/285
SCALE: NTS | WT: | SHEET: 02 OF 02

If any queries contact : design@nihva.com

ALL DIMENSION ARE IN mm

PRODUCED BY AN AUTODESK EDUCATIONAL PRODUCT

PRODUCED BY AN AUTODESK EDUCATIONAL PRODUCT