



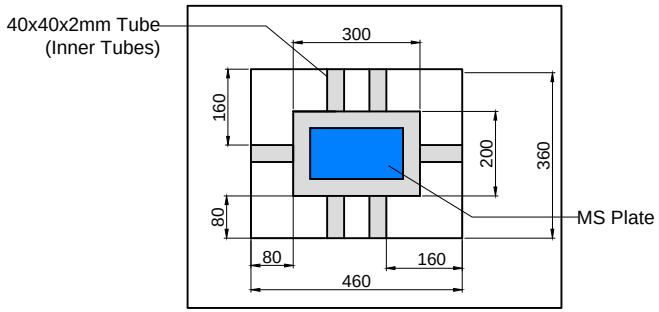

DETAILED VIEW OF A

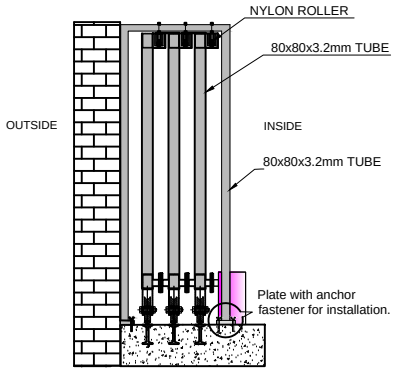

TOLERANCE - ±10mm

Clear Opening size -15000mm x 1500mm
Total No. of Leaf - 6 Leaf
Outer Tube Size-80x80x3.2mm
Inner Tube Size-40x40x2mm
NOTE :- *ALL REQ. CIVIL WORK WILL BE IN CLIENT SCOPE.

SR NO	CLEAR WIDTH	CLEAR HEIGHT	QTY.
1	15000mm	1500mm	1
2	1200mm	1500mm	1

REV 1(30-03-2018)- WICKET GATE HAS BEEN ADDED.

This drawing & design is the property of NIHVA TECHNOLOGIES. Not to be sold or copied to any other concern.

TITLE
TELESCOPIC GATE


NIHVA TECHNOLOGIES PVT. LTD.
NIHVA TECHNOLOGIES PVT. LTD. PUNE
Tel : 020 66304033
Email:- info@nihva.com
Website:- www.nihva.com


	NAME	SIGN	DATE
DRAWN	SURAJ		19-03-2018
CHECK	OMKAR		19-03-2018
APPRD.	PRADEEP		19-03-2018

If any queries contact : design@nihva.com

ALL DIMENSION ARE IN mm

CLIENT - ARA CONSTRUCTION.
PROJECT - AUTOGEN INDIA
SITE LOCATION - KHED CITY,PUNE
DWG. NO. : NIHVA/17-18/0401/R01 | REV- 1
SCALE: NTS | WT: | SHEET: 01 OF 01

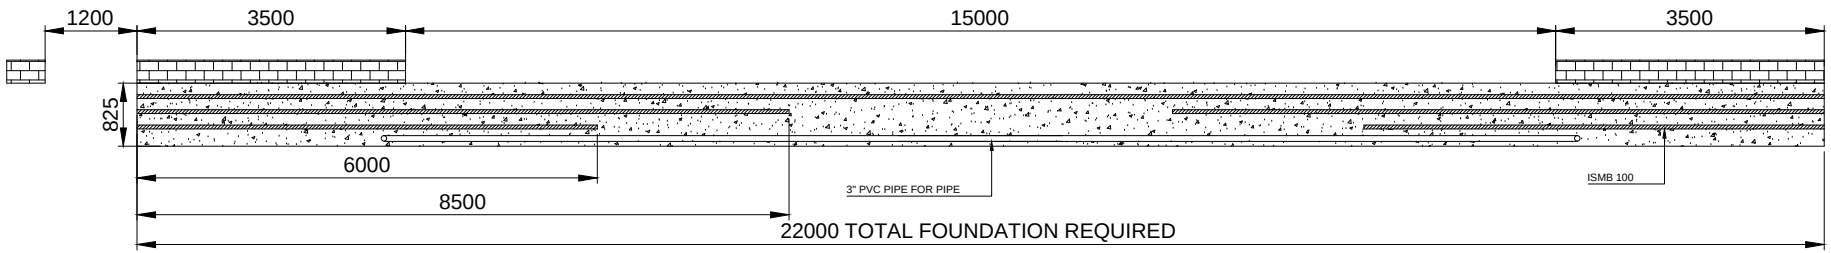

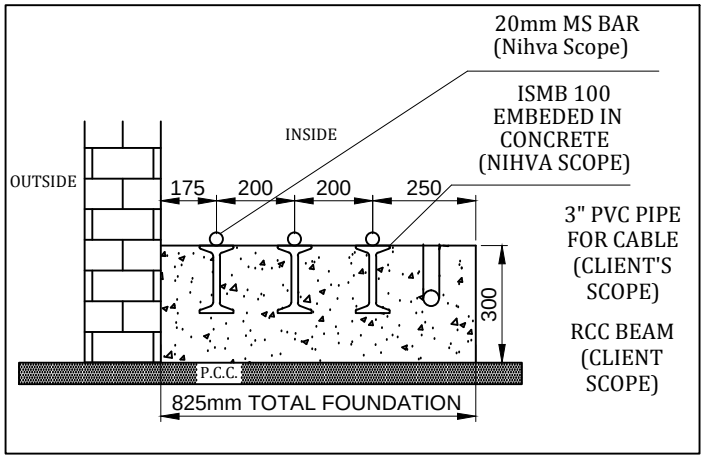

TOLERANCE - ±10mm

This drawing & design is the property of NIHVA TECHNOLOGIES. Not to be sold or copied to any other concern.

TITLE
Telescopic gate 15x1.5m FOUNDATION DRG

NIHVA TECHNOLOGIES PVT. LTD. PUNE
Tel : 020 66304033
Email:- info@nihva.com
Website:- www.nihva.com

	NAME	SIGN	DATE
DRAWN	OMKAR		30-03-2018
CHECK	PRADEEP		30-03-2018
APPRD.	PRADEEP		30-03-2018

CLIENT - ARA CONSTRUCTION
PROJECT - AUTOGEN , INDIA
SITE LOCATION - KHED CITY,PUNE

If any queries contact : design@nihva.com
DWG. NO. : NIHVA/17-18/409
REV- 0
ALL DIMENSION ARE IN mm
SCALE: NTS
WT:
SHEET: 01 OF 01