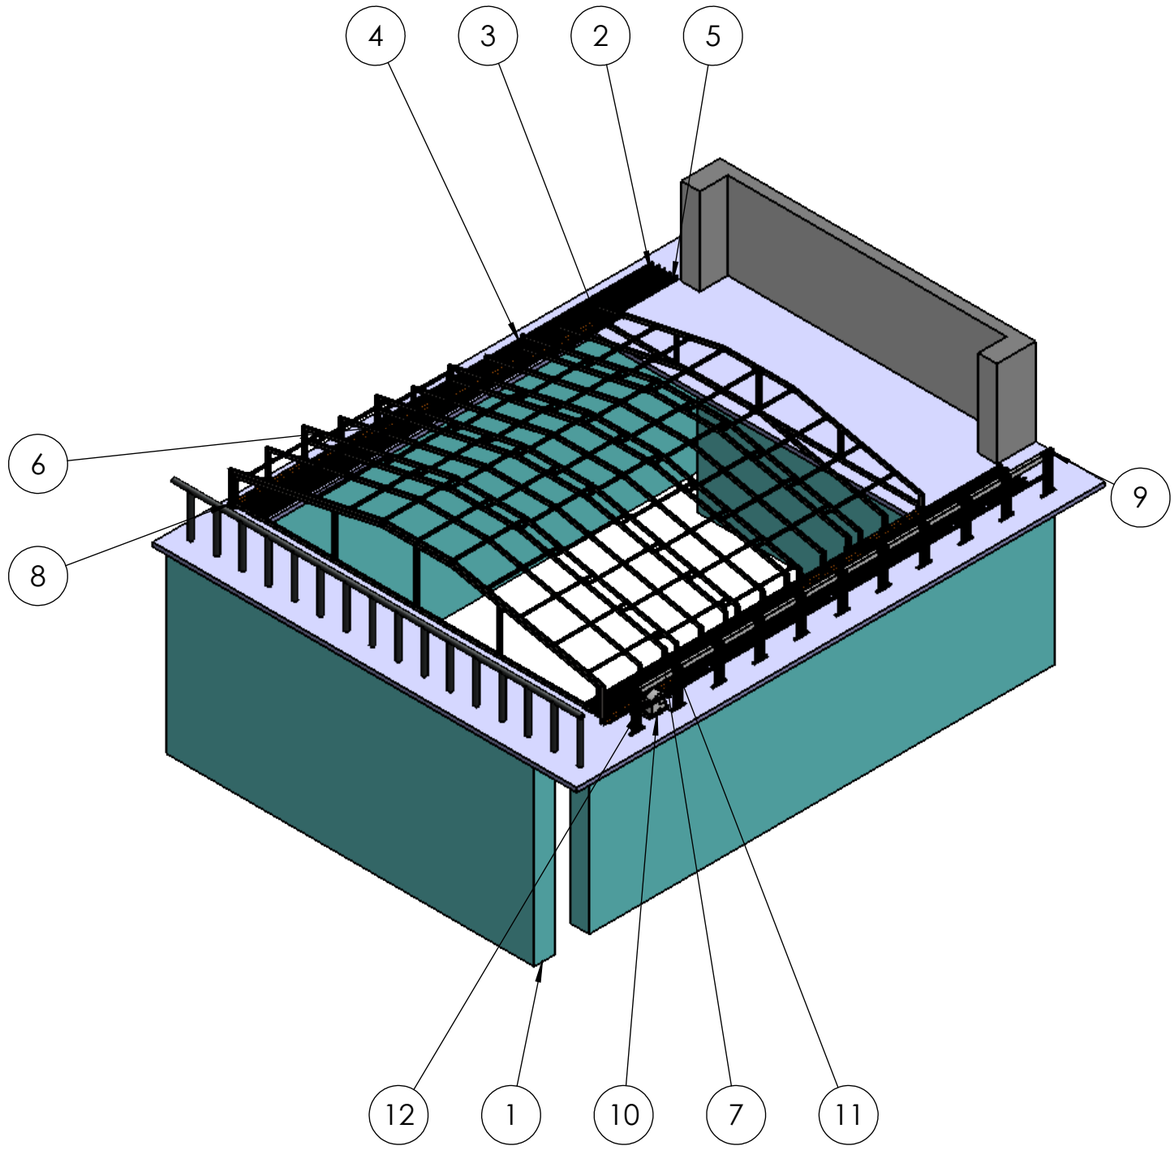


ITEM NO.	PART NUMBER	DESCRIPTION	QTY.
1	CIVIL BASE		1
2	GUIDE RAILS-T89-1B		10
3	PANEL 1		1
4	PANEL 2		1
5	Anchor Bolt M10x75	STD	150
6	PANEL 3		1
7	PANEL 4		1
8	PANEL 5		1
9	rack support		11
10	MOTOR WITH BRACKET		1
11	BUSBAR FLASHER	STD (LOOSE PART)	5
12	RACK	STD (M4 RACK, 30x8x1000 mm, ZINC COATED WITH SPACERS AND SCREWS.)	10

TITLE - RETRACTABLE ROOF

DWG NO - NTPL277-PM-01-00-00-00

NIHVA TECHNOLOGIES PVT.LTD.PUNE

Website - www.nihva.com

	NAME	SIGNATURE	DATE
DRAWN	J.P		19-05-2025
CHK'D	S.W		19-05-2025
APPV'D	V.T.		19-05-2025

PROJECT NO - NTPL277-PM

PRODUCT - RETRACTABLE ROOF

SITE LOCATION - AYODHYA

if any queries contact - supportautomation@nihva.com

REVISION -

QTY - 1


ALL DIMENSION ARE IN mm


A3

SCALE -

SHEET 1 OF 32


ITEM NO.	PART NUMBER	DESCRIPTION	QTY.
1	PANEL 1		1
2	bearing supporting tube	80 x 80 3mm	2
3	NP-PLT04_TP	MS - 100X100X10T	4
4	NP-PLT02_TP	MS - 100X100X10T	4
5	NP-PLT05_TP	MS - 150X100X10T	2
6	NP-PLT03_TP	MS - 150X100X10T	2
7	NP-PLT06_TP	MS - 110X100X10T	4
8	NP-PLT07_TP	MS - 70X50X10T	4
9	NP-PLT08_ TP	MS - 180X100X6T	4
10	SUPPORTING TUBES		18
11	ROLLER BRG HSG	MS ROLLER BRG HSG	4
12	PANEL 1 ENCLOSE R		1

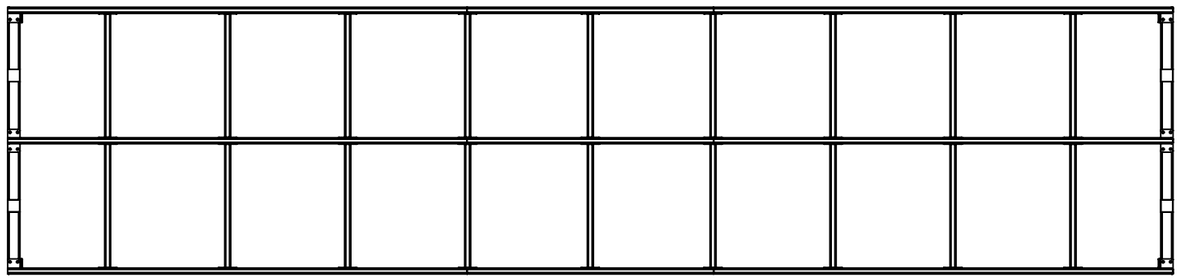


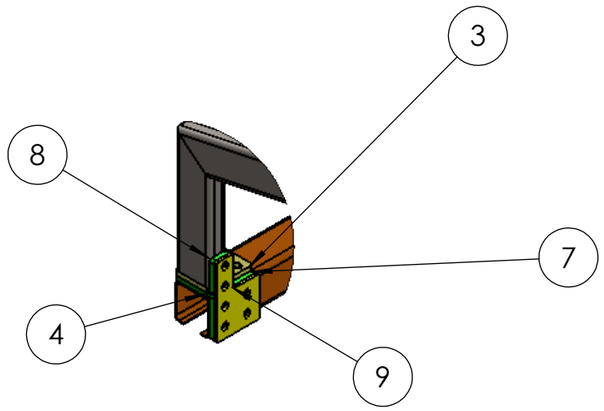

DETAIL E


SCALE 1 : 10

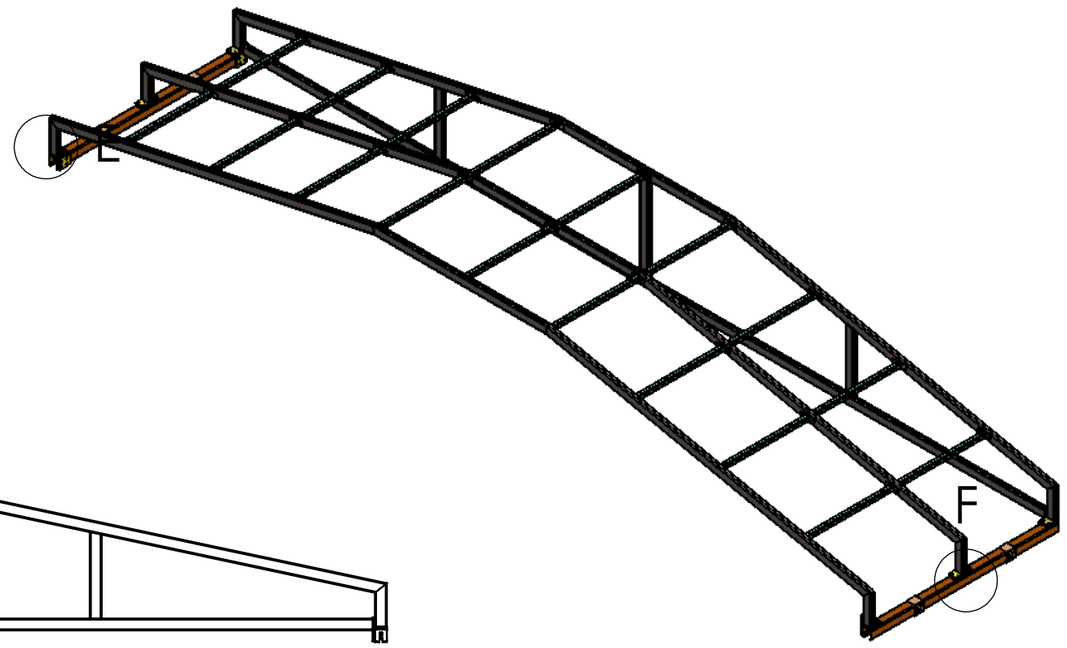

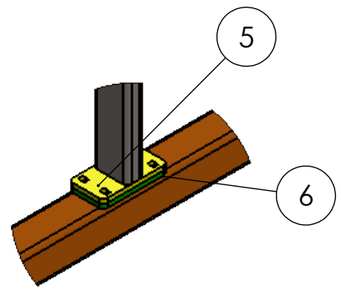

DETAIL F


SCALE 1 : 10

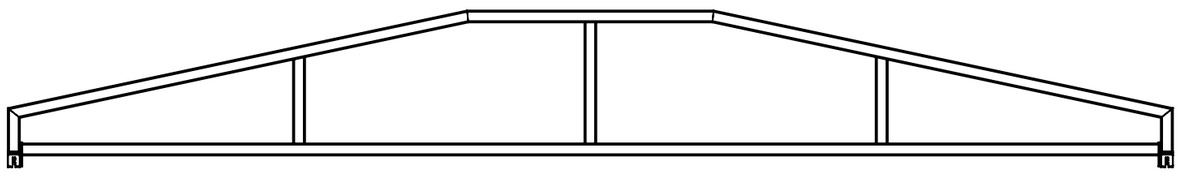


TITLE - RETRACTABLE ROOF				NIHVA TECHNOLOGIES PVT.LTD.PUNE
DWG NO - NTPL277-PM-01-01-00-00				Website - www.nihva.com
	NAME	SIGNATURE	DATE	PROJECT NO - NTPL277-PM
DRAWN	J.P		19-05-2025	PRODUCT - RETRACTABLE ROOF
CHK'D	S.W		19-05-2025	SITE LOCATION - AYODHYA
APPV'D	V.T.		19-05-2025	
if any queries contact - supportautomation@nihva.com				REVISION - QTY - 1
ALL DIMENSION ARE IN mm			A3	SCALE - SHEET 2 OF 32

ITEM NO.	PART NUMBER	DESCRIPTION	QTY.
1	PANEL 1		1




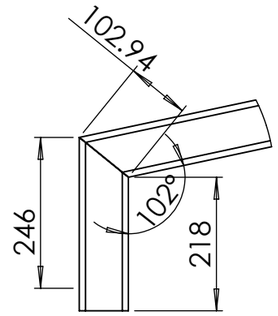

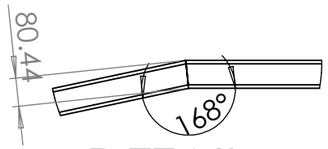


DETAIL G

SCALE 2 : 35

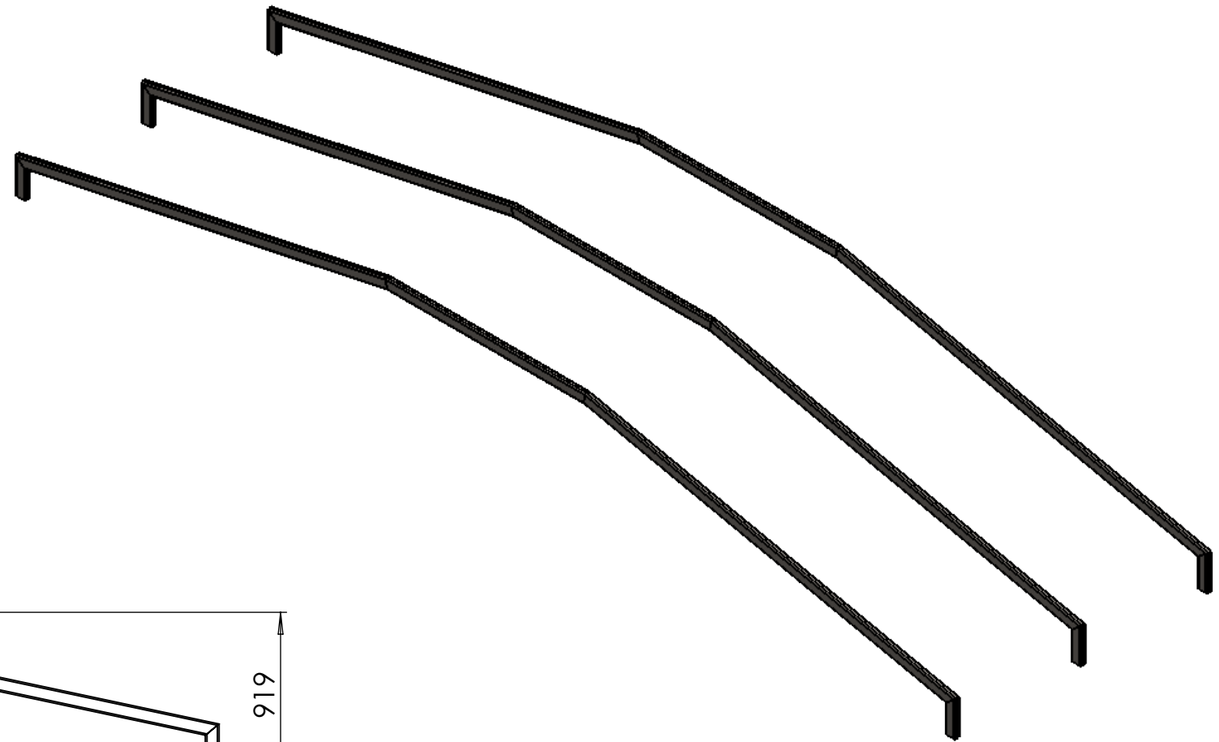


DETAIL A


SCALE 1 : 10

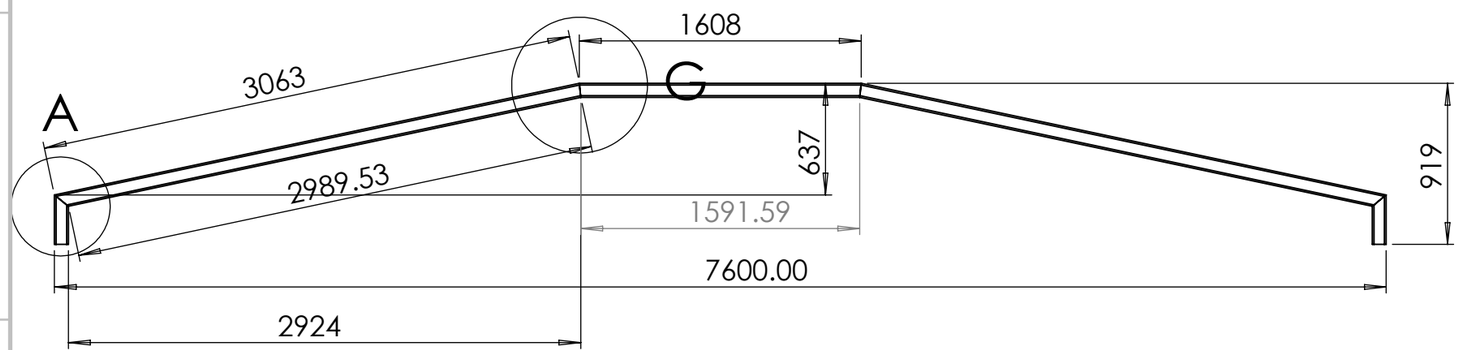


TITLE - RETRACTABLE ROOF				NIHVA TECHNOLOGIES PVT.LTD.PUNE
DWG NO - NTPL277-PM-01-01-00-01				Website - www.nihva.com
	NAME	SIGNATURE	DATE	PROJECT NO - NTPL277-PM
DRAWN	J.P		19-05-2025	PRODUCT - RETRACTABLE ROOF
CHK'D	S.W		19-05-2025	SITE LOCATION - AYODHYA
APPV'D	V.T.		19-05-2025	
if any queries contact - supportautomation@nihva.com				REVISION - QTY - 1
ALL DIMENSION ARE IN mm			A3	SCALE - SHEET 3 OF 32

ITEM NO.	PART NUMBER	DESCRIPTION	QTY.
1	SUPPORTING TUBES	40 x 40 x 2.5	110

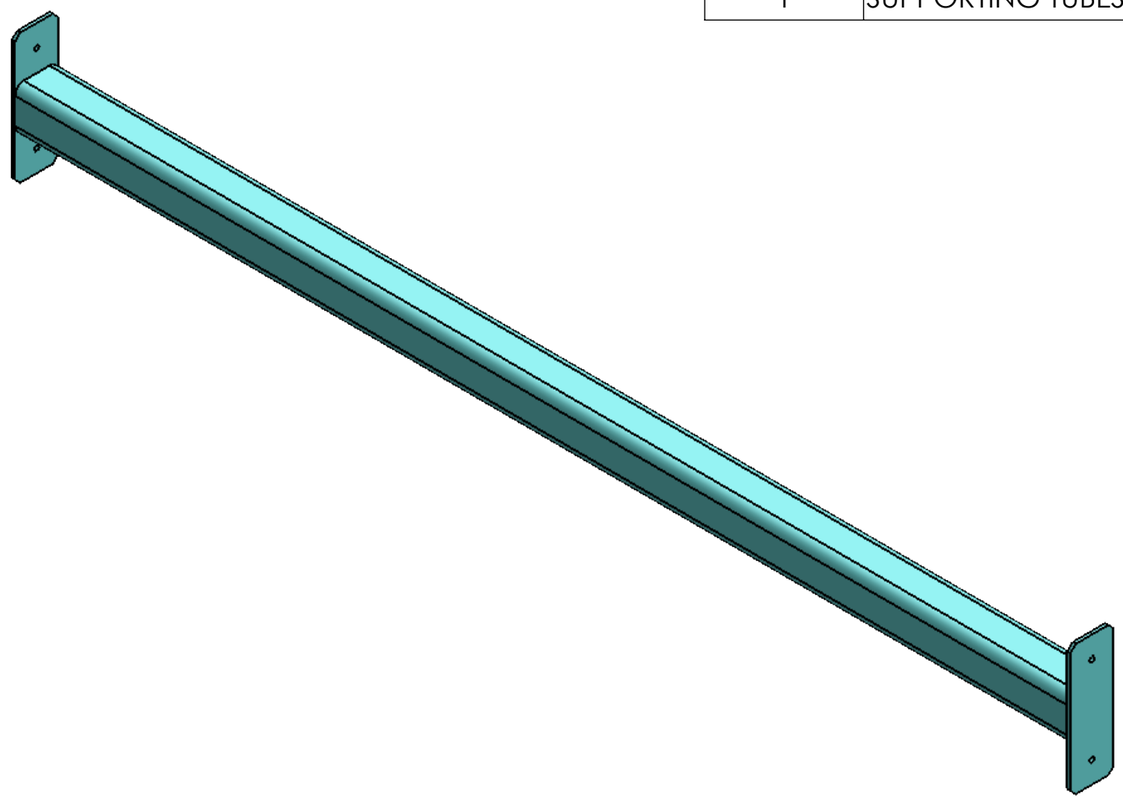


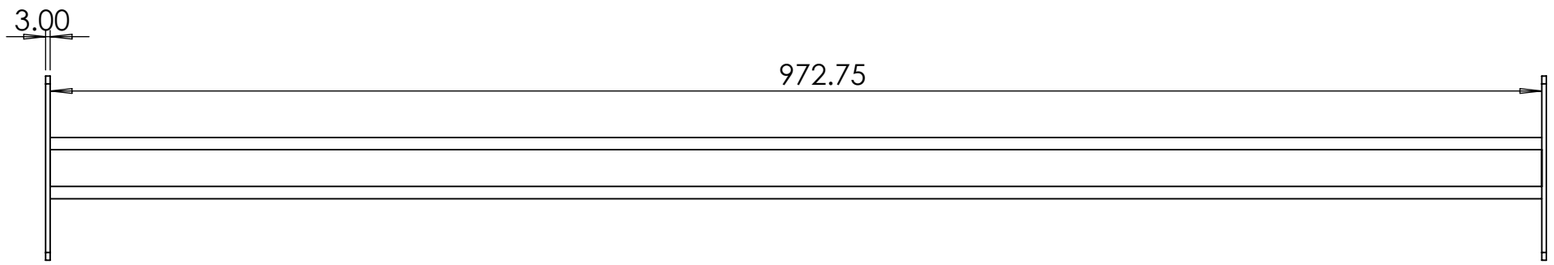

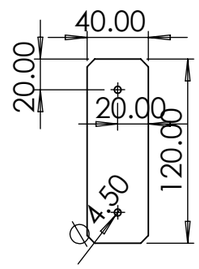


TITLE - RETRACTABLE ROOF				NIHVA TECHNOLOGIES PVT.LTD.PUNE
DWG NO - NTPL277-PM-01-01-00-02				Website - www.nihva.com
	NAME	SIGNATURE	DATE	PROJECT NO - NTPL277-PM
DRAWN	J.P		19-05-2025	PRODUCT - RETRACTABLE ROOF
CHK'D	S.W		19-05-2025	SITE LOCATION - AYODHYA
APPV'D	V.T.		19-05-2025	
if any queries contact - supportautomation@nihva.com				REVISION - QTY - 1
ALL DIMENSION ARE IN mm		A3		SCALE - SHEET 4 OF 32


ITEM NO.	PART NUMBER	DESCRIPTION	QTY.
1	PANEL 1 ENCLOSE R		1

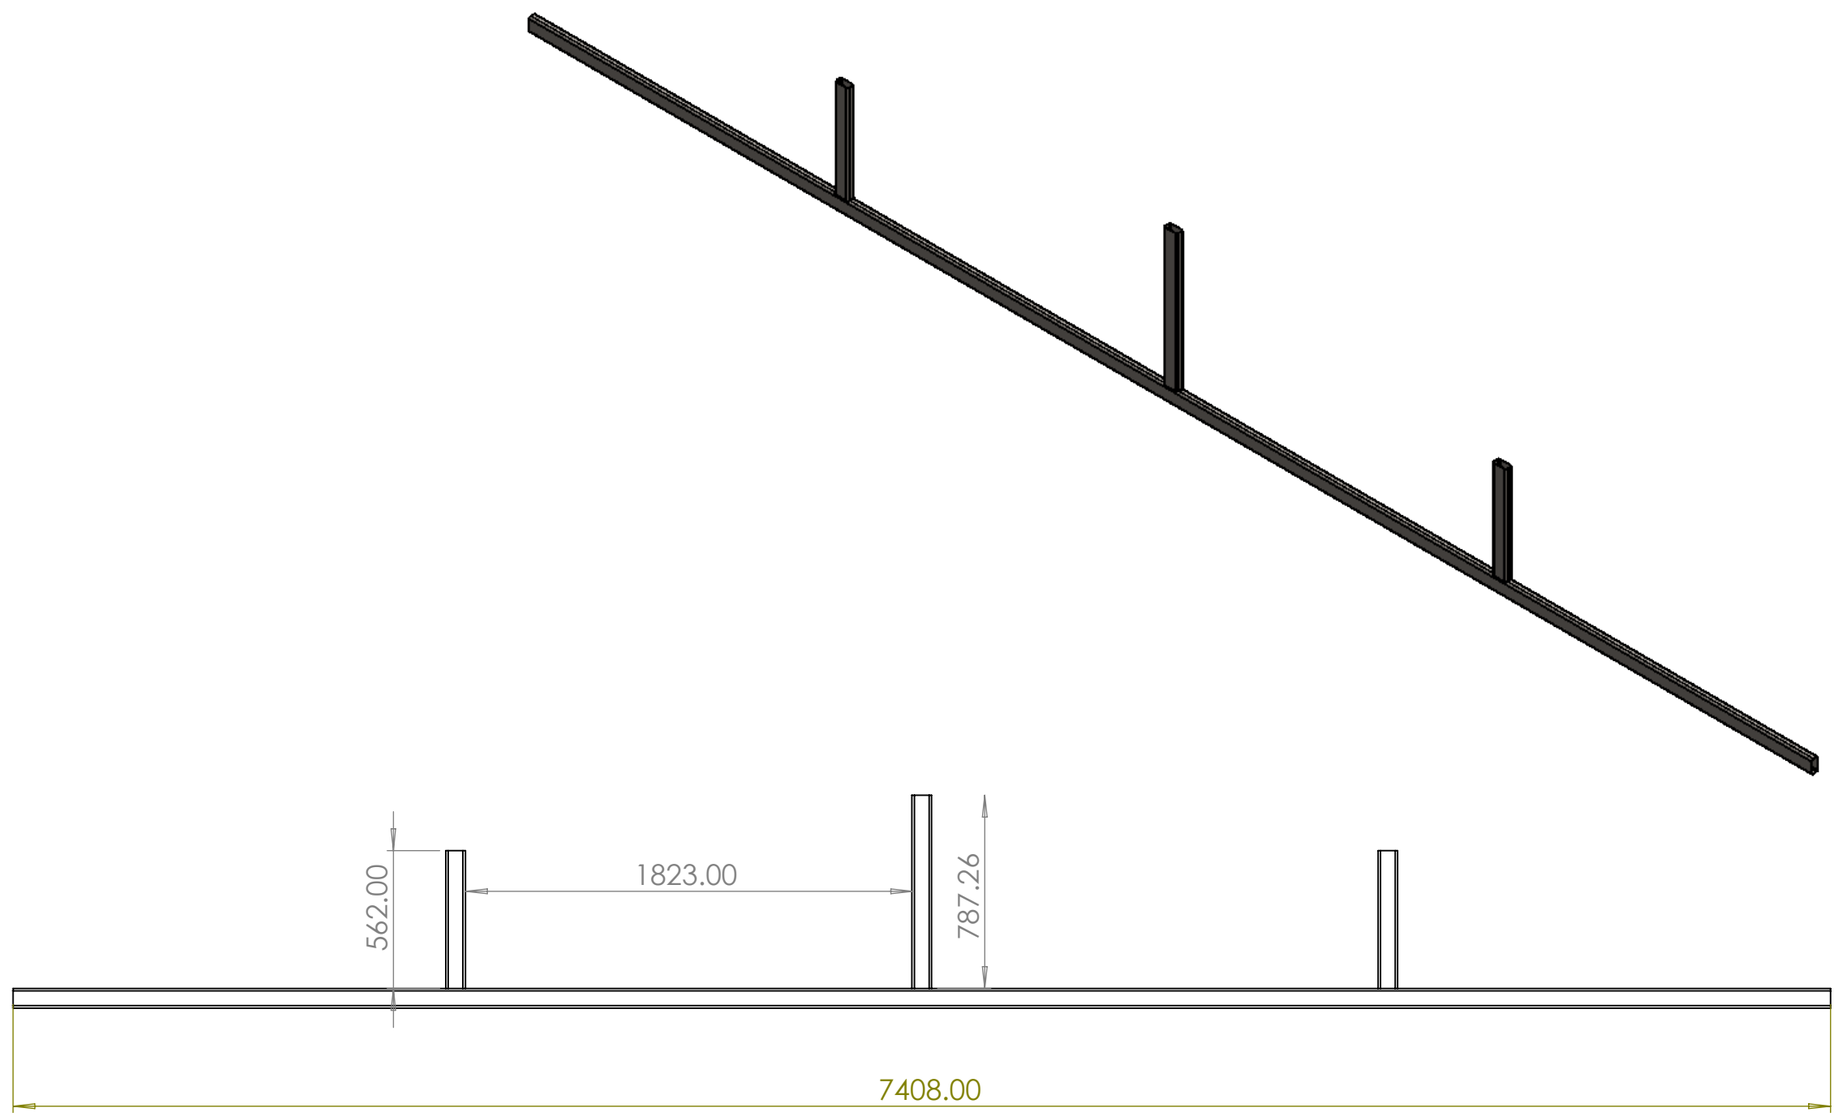


TITLE - RETRACTABLE ROOF				NIHVA TECHNOLOGIES PVT.LTD.PUNE
DWG NO - NTPL277-PM-01-01-00-03				Website - www.nihva.com
	NAME	SIGNATURE	DATE	PROJECT NO - NTPL277-PM
DRAWN	J.P		19-05-2025	PRODUCT - RETRACTABLE ROOF
CHK'D	S.W		19-05-2025	SITE LOCATION - AYODHYA
APPV'D	V.T.		19-05-2025	
if any queries contact - supportautomation@nihva.com				REVISION - QTY - 1
ALL DIMENSION ARE IN mm			A3	SCALE - SHEET 5 OF 32

ITEM NO.	PART NUMBER	DESCRIPTION	QTY.
1	bearing supporting tube	80 x 80 x 3mm	10

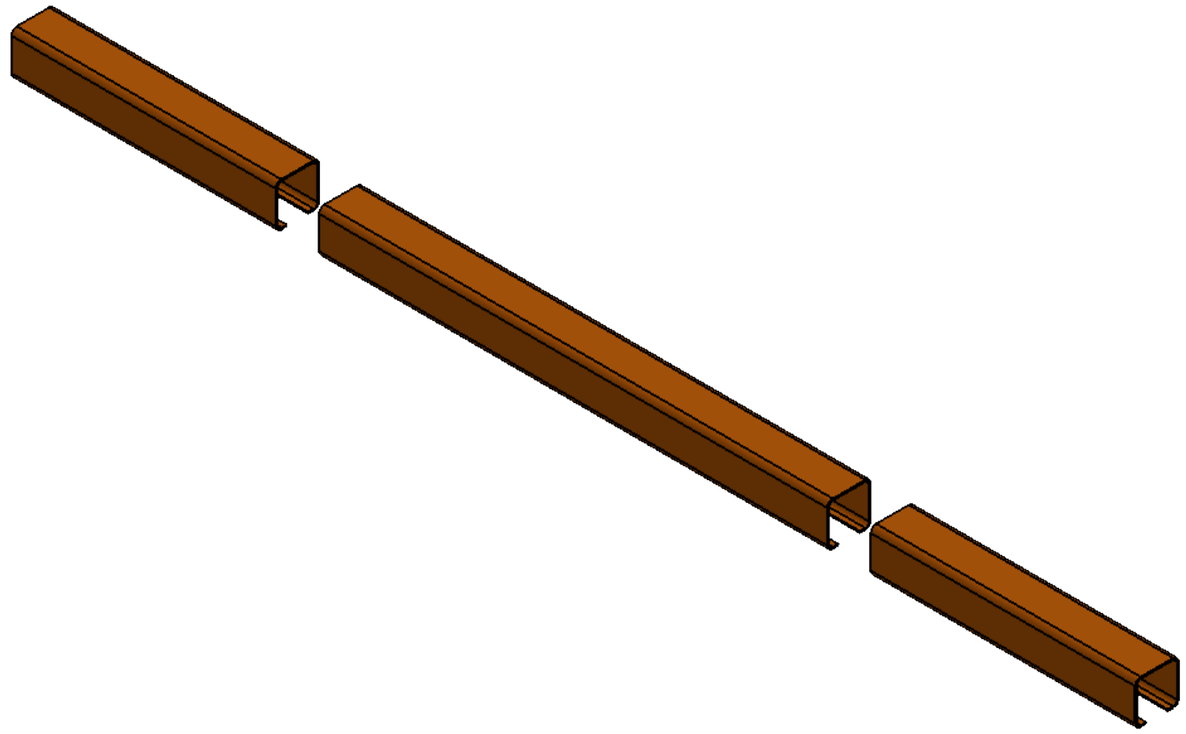


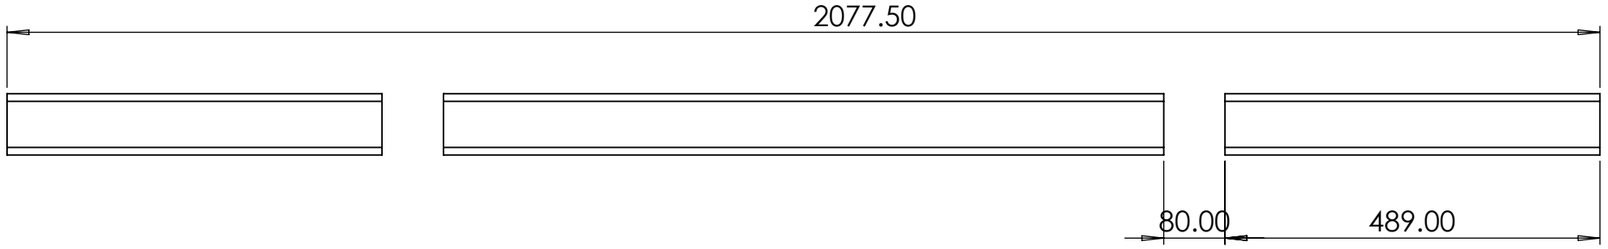


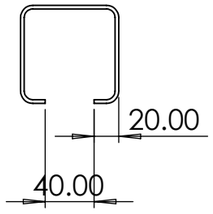


TITLE - RETRACTABLE ROOF				NIHVA TECHNOLOGIES PVT.LTD.PUNE
DWG NO - NTPL277-PM-01-01-00-04				Website - www.nihva.com
	NAME	SIGNATURE	DATE	PROJECT NO - NTPL277-PM
DRAWN	J.P		19-05-2025	PRODUCT - RETRACTABLE ROOF
CHK'D	S.W		19-05-2025	SITE LOCATION - AYODHYA
APPV'D	V.T.		19-05-2025	
if any queries contact - supportautomation@nihva.com				REVISION - / QTY - 1
ALL DIMENSION ARE IN mm			A3	SCALE - / SHEET 6 OF 32


ITEM NO.	PART NUMBER	DESCRIPTION	QTY.
1	ROLLER BRG HSG	100X80X80 MM	22

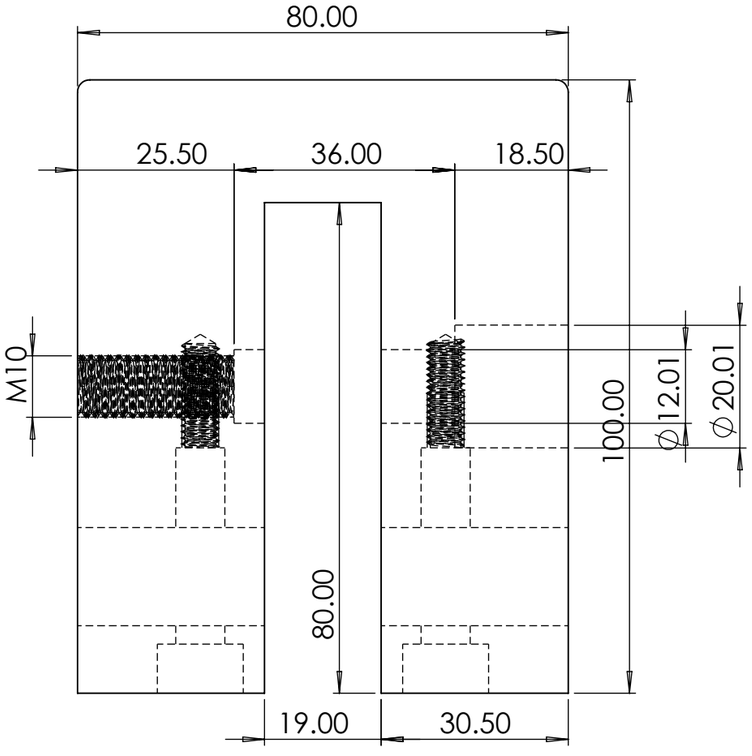

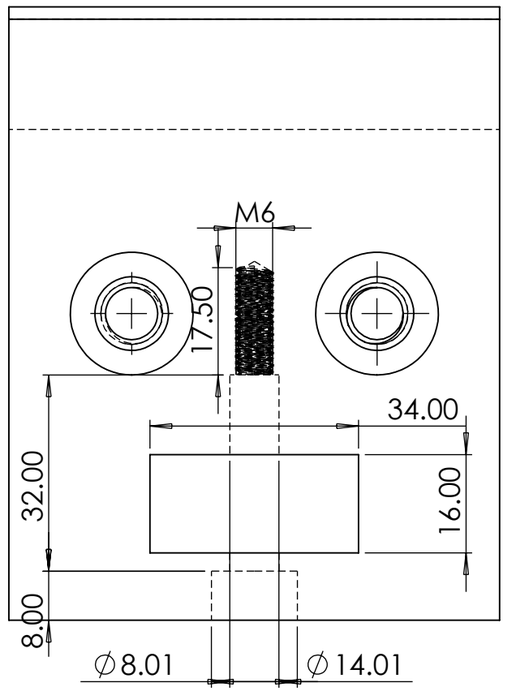


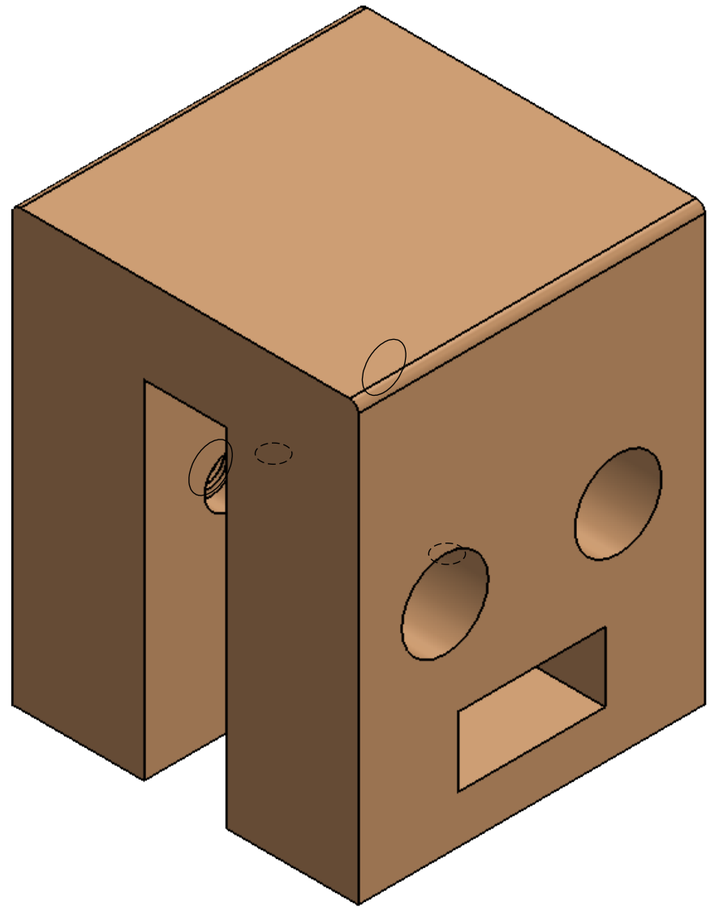


TITLE - RETRACTABLE ROOF				NIHVA TECHNOLOGIES PVT.LTD.PUNE
DWG NO - NTPL277-PM-01-00-01-01				Website - www.nihva.com
	NAME	SIGNATURE	DATE	PROJECT NO - NTPL277-PM
DRAWN	J.P		19-05-2025	PRODUCT - RETRACTABLE ROOF
CHK'D	S.W		19-05-2025	SITE LOCATION - AYODHYA
APPV'D	V.T.		19-05-2025	
if any queries contact - supportautomation@nihva.com				REVISION - QTY - 1
ALL DIMENSION ARE IN mm			A3	SCALE - SHEET 7 OF 32

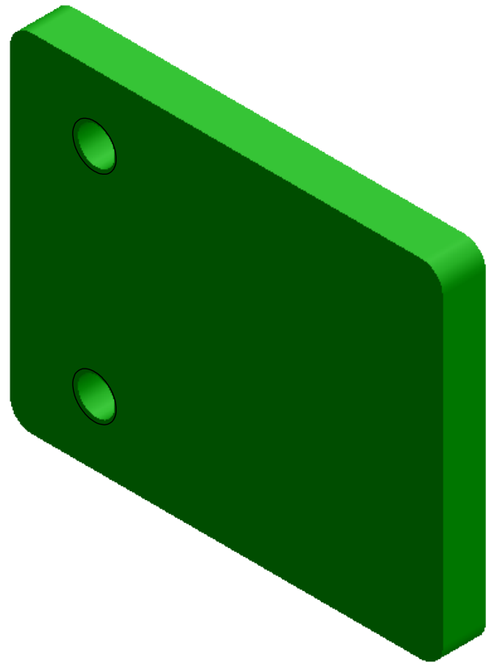


ITEM NO.	PART NUMBER	DESCRIPTION	QTY.
1	NP-PLT02_TP	MS - 100X100X10T	24

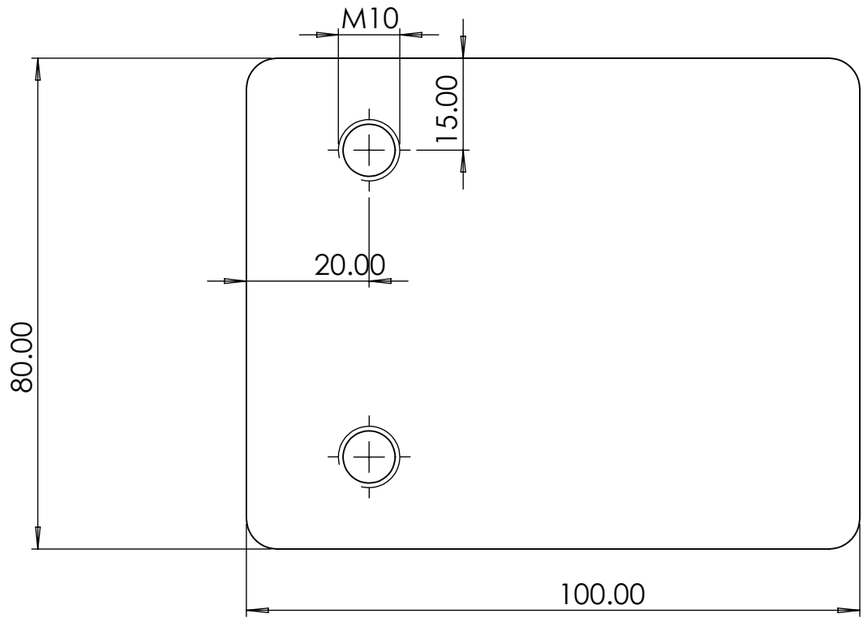


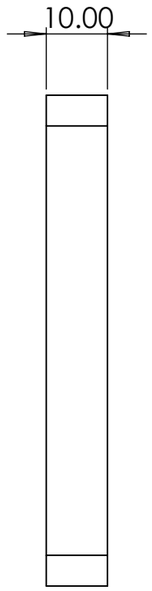

TITLE - RETRACTABLE ROOF				NIHVA TECHNOLOGIES PVT.LTD.PUNE
DWG NO - NTPL277-PM-01-01-00-05				Website - www.nihva.com
	NAME	SIGNATURE	DATE	PROJECT NO - NTPL277-PM
DRAWN	J.P		19-05-2025	PRODUCT - RETRACTABLE ROOF
CHK'D	S.W		19-05-2025	SITE LOCATION - AYODHYA
APPV'D	V.T.		19-05-2025	
if any queries contact - supportautomation@nihva.com				REVISION - QTY - 1
ALL DIMENSION ARE IN mm			A3	SCALE - SHEET 8 OF 32


ITEM NO.	PART NUMBER	DESCRIPTION	QTY.
1	NP-PLT03_TP	MS - 150X100X10T	14

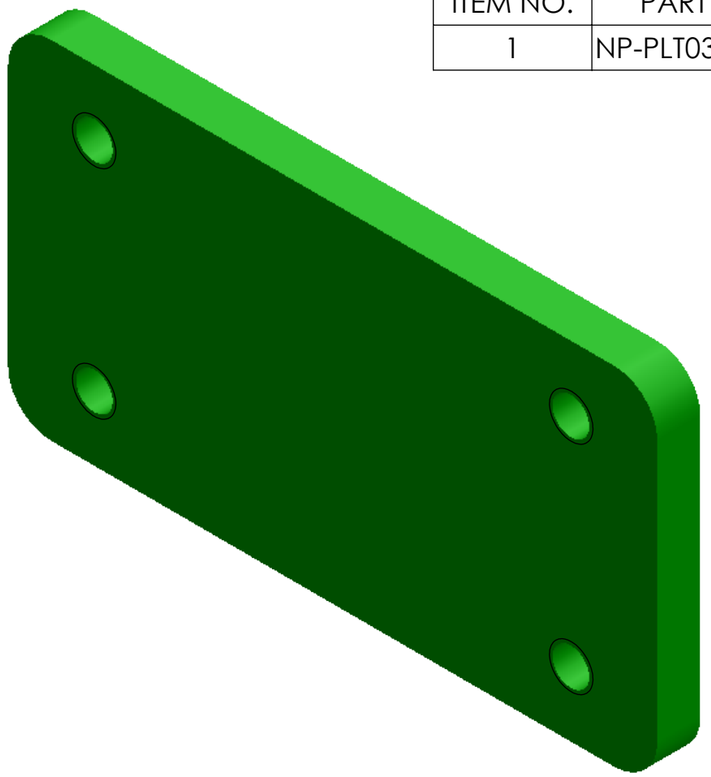


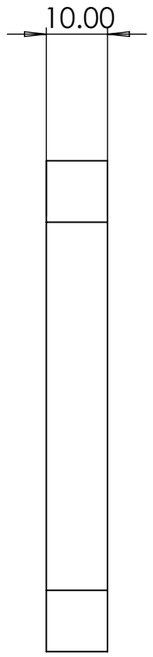


TITLE - RETRACTABLE ROOF				NIHVA TECHNOLOGIES PVT.LTD.PUNE
DWG NO - NTPL277-PM-01-01-00-06				Website - www.nihva.com
	NAME	SIGNATURE	DATE	PROJECT NO - NTPL277-PM
DRAWN	J.P		19-05-2025	PRODUCT - RETRACTABLE ROOF
CHK'D	S.W		19-05-2025	SITE LOCATION - AYODHYA
APPV'D	V.T.		19-05-2025	
if any queries contact - supportautomation@nihva.com				REVISION - QTY - 1
ALL DIMENSION ARE IN mm			A3	SCALE - SHEET 9 OF 32

ITEM NO.	PART NUMBER	DESCRIPTION	QTY.
1	NP-PLT04_TP	MS - 100X100X10T	24

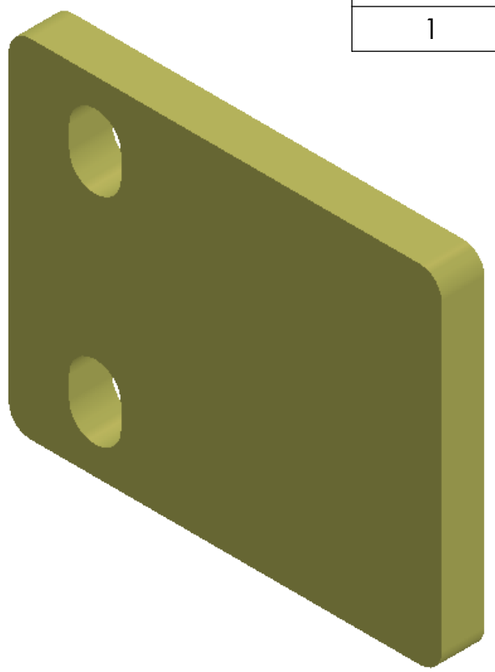


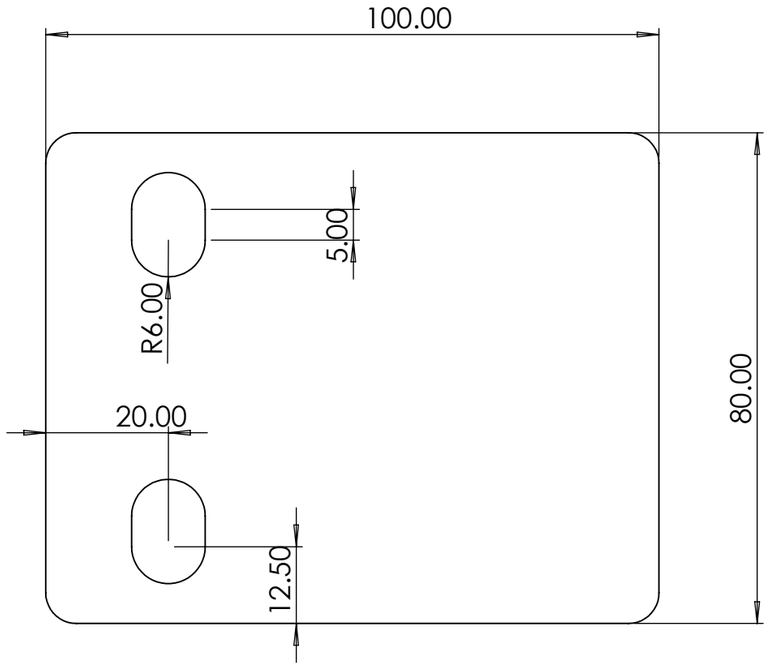


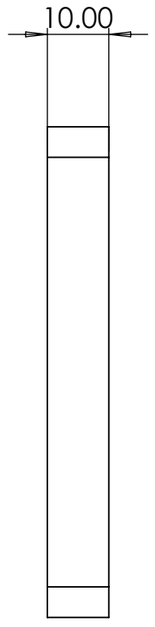


TITLE - RETRACTABLE ROOF				NIHVA TECHNOLOGIES PVT.LTD.PUNE Website - www.nihva.com
DWG NO - NTPL277-PM-01-01-00-07				
	NAME	SIGNATURE	DATE	PROJECT NO - NTPL277-PM
DRAWN	J.P		19-05-2025	PRODUCT - RETRACTABLE ROOF
CHK'D	S.W		19-05-2025	SITE LOCATION - AYODHYA
APPV'D	V.T.		19-05-2025	
if any queries contact - supportautomation@nihva.com				REVISION - / QTY - 1
ALL DIMENSION ARE IN mm			A3	SCALE - / SHEET 10 OF 32

ITEM NO.	PART NUMBER	DESCRIPTION	QTY.
1	NP-PLT05_TP	MS - 150X100X10T	14

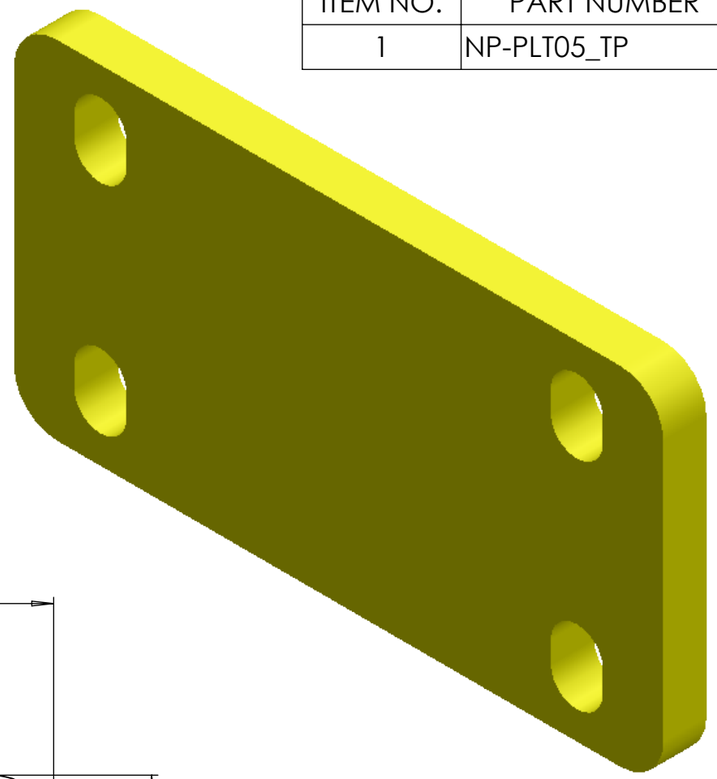


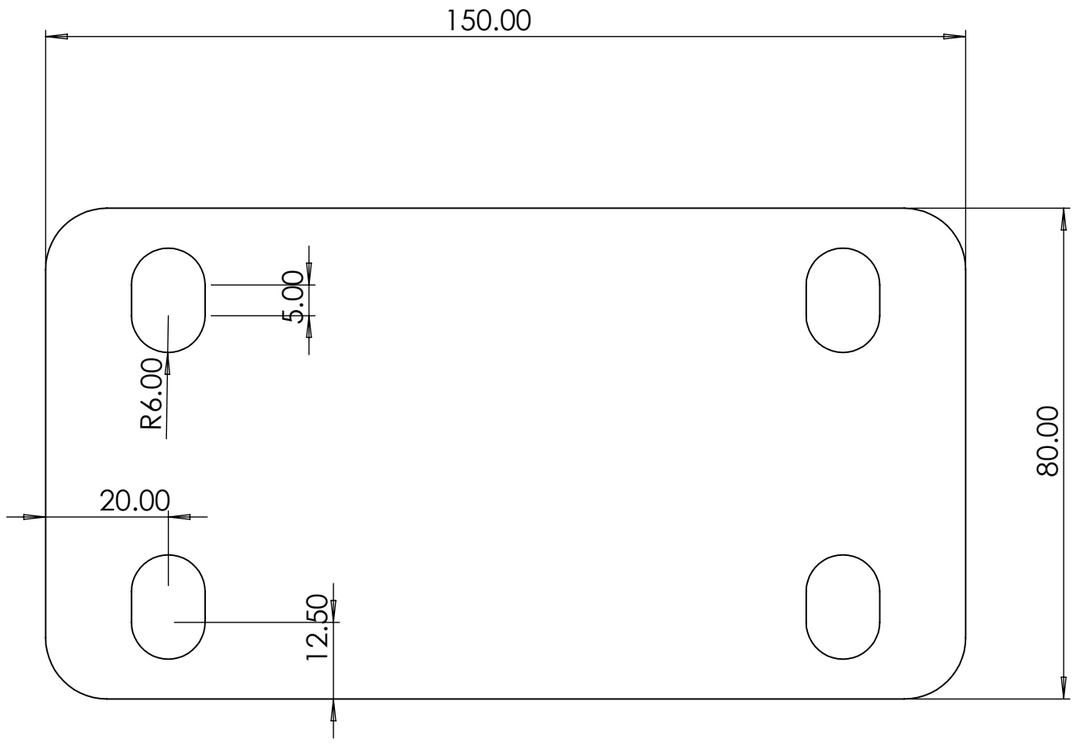


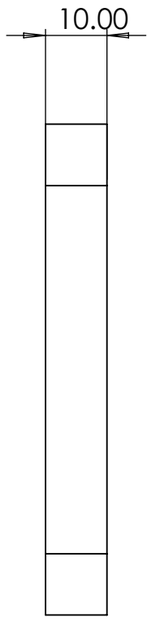


TITLE - RETRACTABLE ROOF				NIHVA TECHNOLOGIES PVT.LTD.PUNE
DWG NO - NTPL277-PM-01-01-00-08				Website - www.nihva.com
	NAME	SIGNATURE	DATE	PROJECT NO - NTPL277-PM
DRAWN	J.P		19-05-2025	PRODUCT - RETRACTABLE ROOF
CHK'D	S.W		19-05-2025	SITE LOCATION - AYODHYA
APPV'D	V.T.		19-05-2025	
if any queries contact - supportautomation@nihva.com				REVISION - QTY - 1
ALL DIMENSION ARE IN mm			A3	SCALE - SHEET 11 OF 32

ITEM NO.	PART NUMBER	DESCRIPTION	QTY.
1	NP-PLT06_TP	MS - 110X100X10T	24

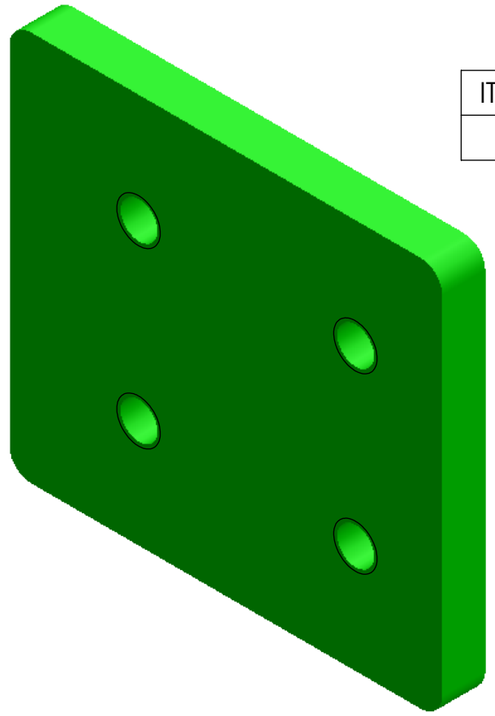


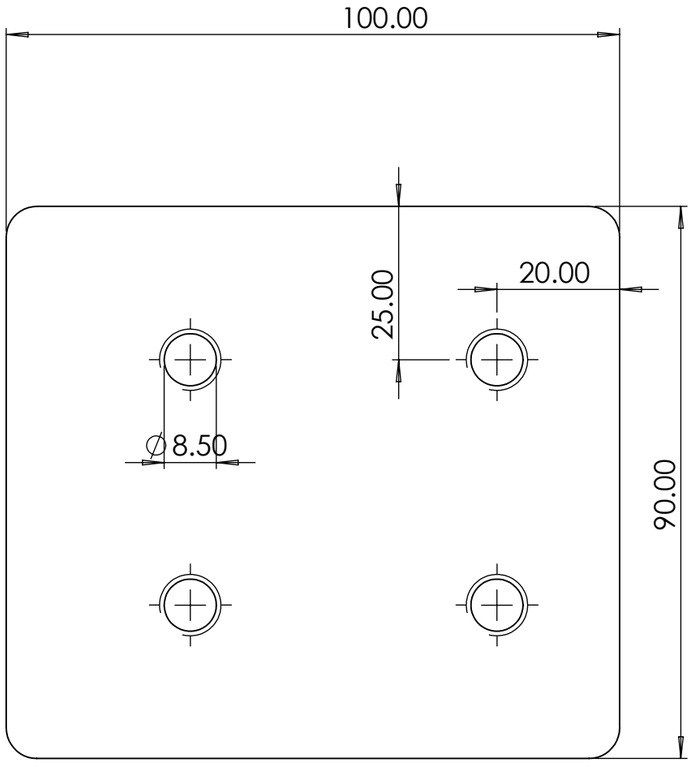


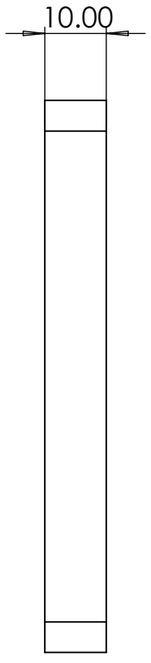


TITLE - RETRACTABLE ROOF				NIHVA TECHNOLOGIES PVT.LTD.PUNE
DWG NO - NTPL277-PM-01-01-00-09				Website - www.nihva.com
	NAME	SIGNATURE	DATE	PROJECT NO - NTPL277-PM
DRAWN	J.P		19-05-2025	PRODUCT - RETRACTABLE ROOF
CHK'D	S.W		19-05-2025	SITE LOCATION - AYODHYA
APPV'D	V.T.		19-05-2025	
if any queries contact - supportautomation@nihva.com				REVISION - QTY - 1
ALL DIMENSION ARE IN mm		A3		SCALE - SHEET 12 OF 32

ITEM NO.	PART NUMBER	DESCRIPTION	QTY.
1	NP-PLT07_TP	MS - 70X50X10T	24

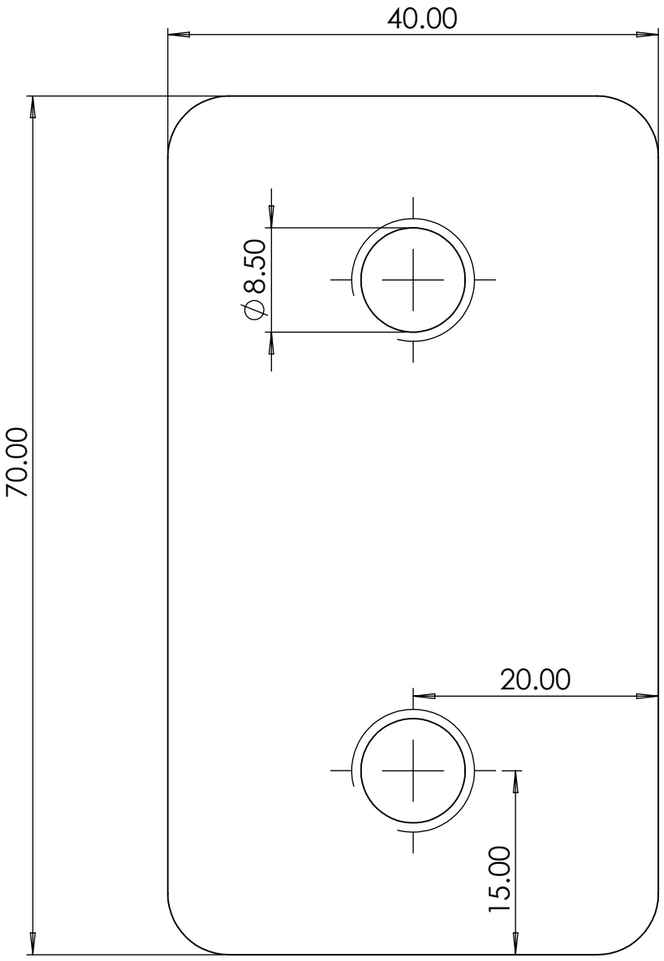


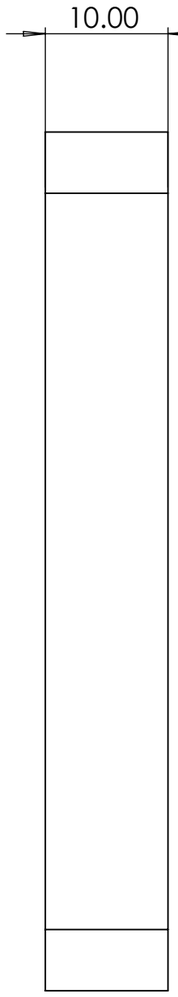


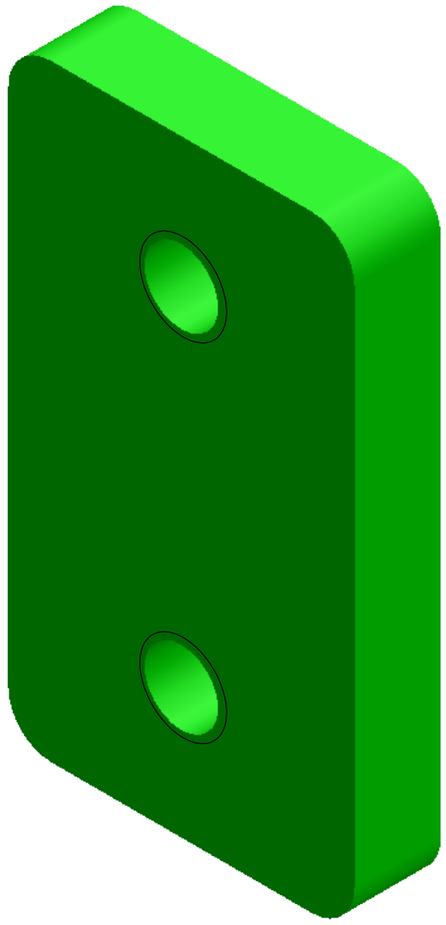


TITLE - RETRACTABLE ROOF				NIHVA TECHNOLOGIES PVT.LTD.PUNE
DWG NO - NTPL277-PM-01-01-00-010				Website - www.nihva.com
	NAME	SIGNATURE	DATE	PROJECT NO - NTPL277-PM
DRAWN	J.P		19-05-2025	PRODUCT - RETRACTABLE ROOF
CHK'D	S.W		19-05-2025	SITE LOCATION - AYODHYA
APPV'D	V.T.		19-05-2025	
if any queries contact - supportautomation@nihva.com				REVISION - QTY - 1
ALL DIMENSION ARE IN mm			A3	SCALE - SHEET 13 OF 32


ITEM NO.	PART NUMBER	DESCRIPTION	QTY.
1	NP-PLT08_ TP	MS - 180X100X6T	24

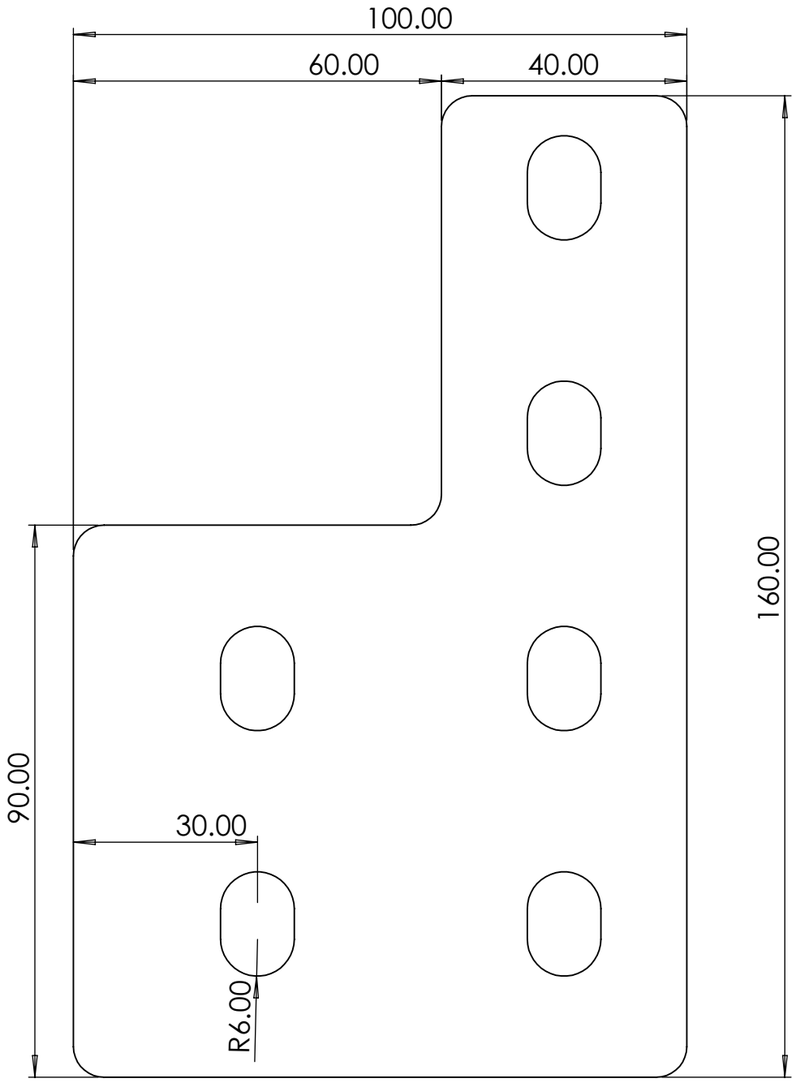

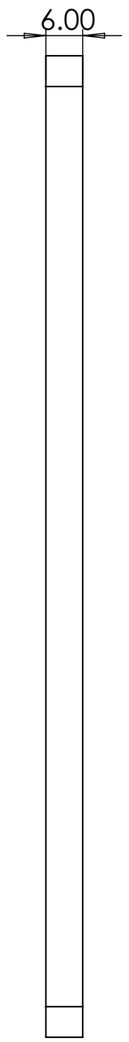


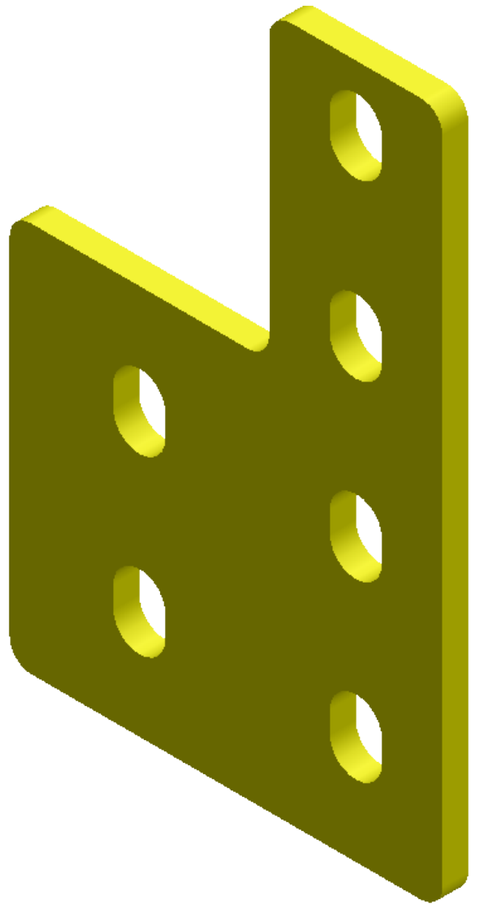


TITLE - RETRACTABLE ROOF				NIHVA TECHNOLOGIES PVT.LTD.PUNE
DWG NO - NTPL277-PM-01-00-00-00				Website - www.nihva.com
	NAME	SIGNATURE	DATE	PROJECT NO - NTPL277-PM
DRAWN	J.P		19-05-2025	PRODUCT - RETRACTABLE ROOF
CHK'D	S.W		19-05-2025	SITE LOCATION - AYODHYA
APPV'D	V.T.		19-05-2025	
if any queries contact - supportautomation@nihva.com				REVISION - QTY - 1
ALL DIMENSION ARE IN mm			A3	SCALE - SHEET 14 OF 32

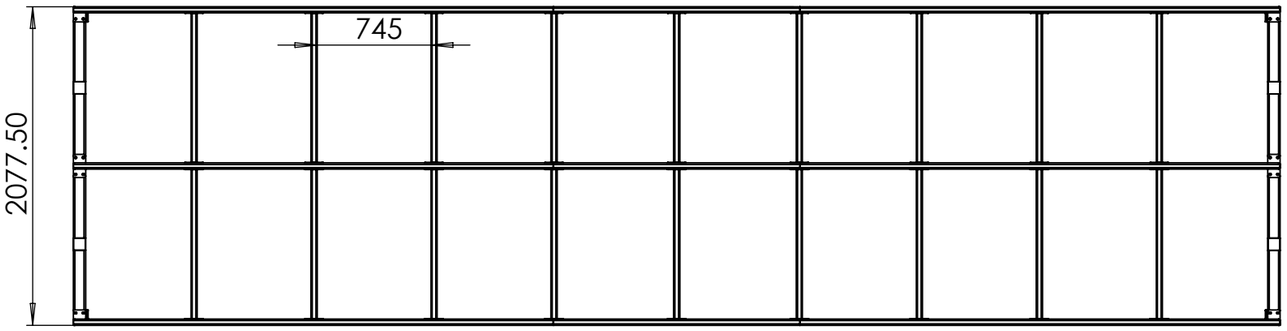

ITEM NO.	PART NUMBER	DESCRIPTION	QTY.
1	PANEL 2		1
2	bearing supporting tube		2
3	NP-PLT04_TP	MS - 100X100X10T	4
4	NP-PLT02_TP	MS - 100X100X10T	4
5	NP-PLT05_TP	MS - 150X100X10T	2
6	NP-PLT03_TP	MS - 150X100X10T	2
7	NP-PLT06_TP	MS - 110X100X10T	4
8	NP-PLT07_TP	MS - 70X50X10T	4
9	NP-PLT08_ TP	MS - 180X100X6T	4
10	SUPPORTING TUBES		18
11	ROLLER BRG HSG	MS ROLLER BRG HSG	4

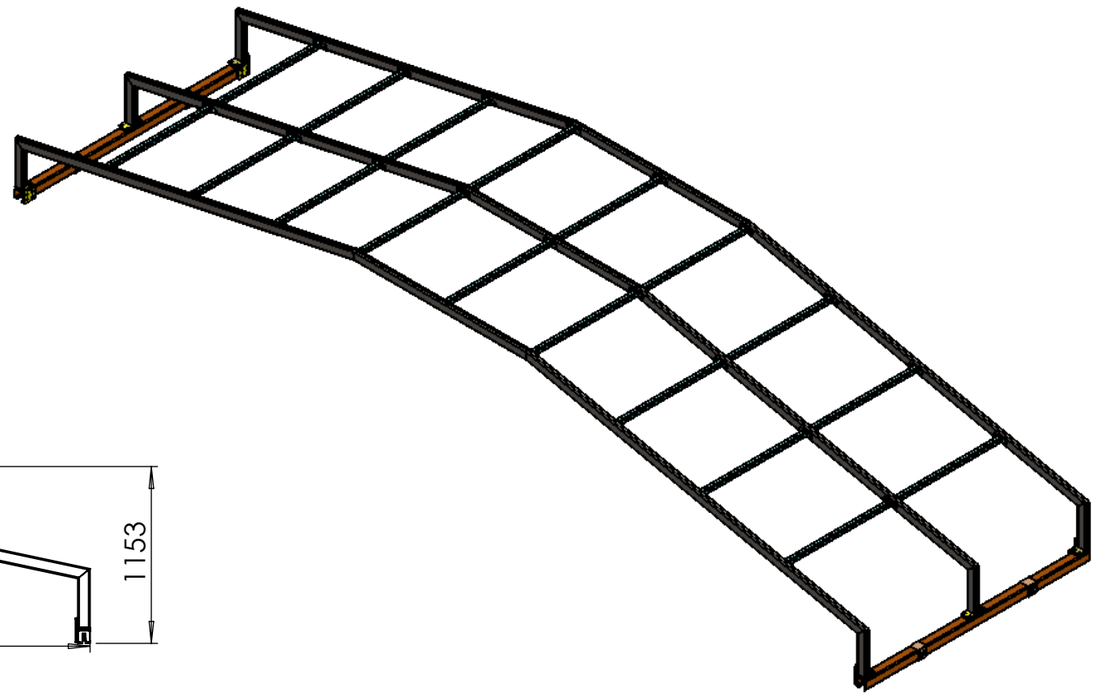


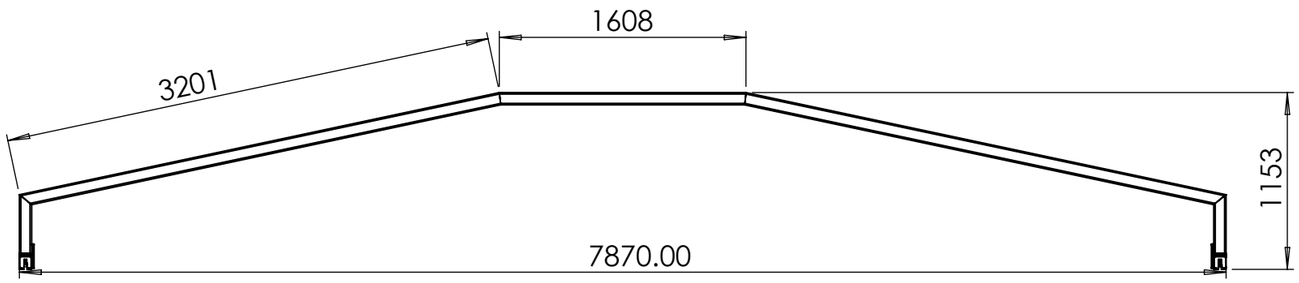

TITLE - RETRACTABLE ROOF				NIHVA TECHNOLOGIES PVT.LTD.PUNE
DWG NO - NTPL277-PM-01-02-00-00				Website - www.nihva.com
	NAME	SIGNATURE	DATE	PROJECT NO - NTPL277-PM
DRAWN	J.P		19-05-2025	PRODUCT - RETRACTABLE ROOF
CHK'D	S.W		19-05-2025	SITE LOCATION - AYODHYA
APPV'D	V.T.		19-05-2025	
if any queries contact - supportautomation@nihva.com				REVISION - QTY - 1
ALL DIMENSION ARE IN mm			A3	SCALE - SHEET 15 OF 32


ITEM NO.	PART NUMBER	DESCRIPTION	QTY.
1	PANEL 2		1



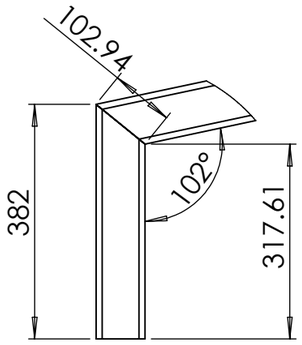


DETAIL C


SCALE 1 : 10

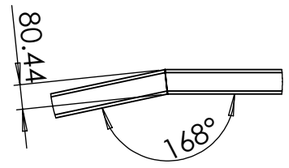


DETAIL M

SCALE 1 : 20

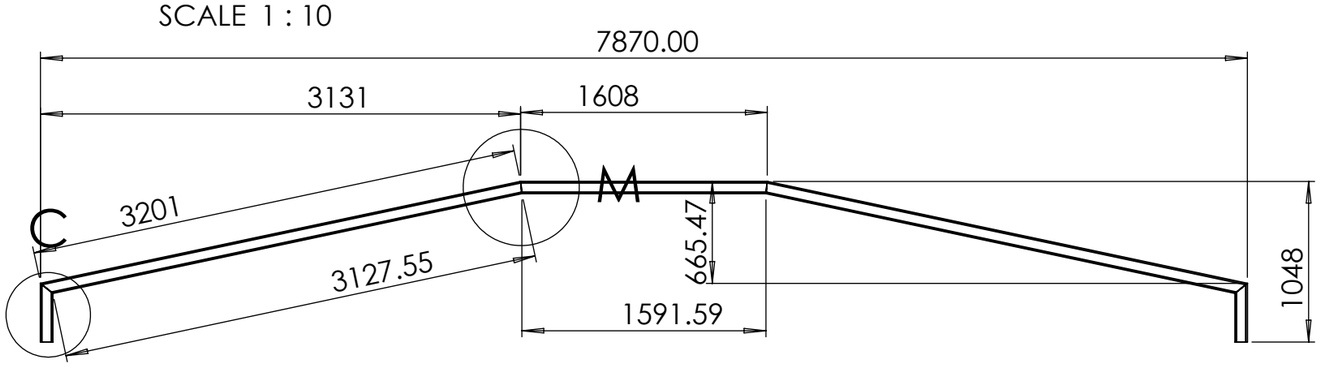


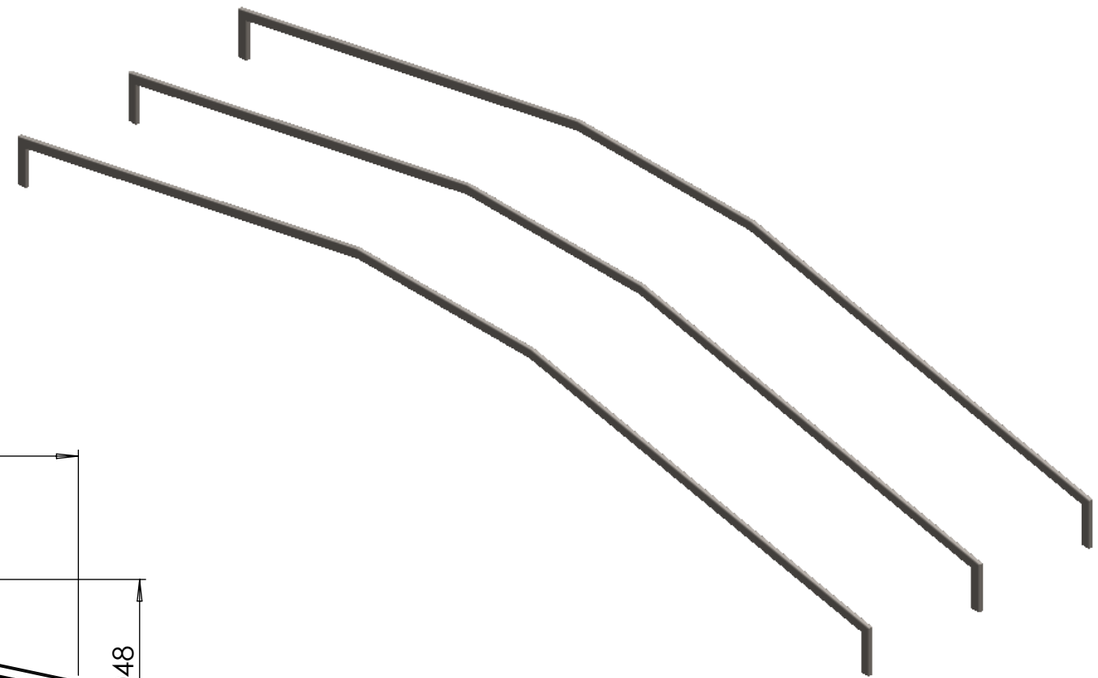


TITLE - RETRACTABLE ROOF				NIHVA TECHNOLOGIES PVT.LTD.PUNE
DWG NO - NTPL277-PM-01-02-00-01				Website - www.nihva.com
	NAME	SIGNATURE	DATE	PROJECT NO - NTPL277-PM
DRAWN	J.P		19-05-2025	PRODUCT - RETRACTABLE ROOF
CHK'D	S.W		19-05-2025	SITE LOCATION - AYODHYA
APPV'D	V.T.		19-05-2025	
if any queries contact - supportautomation@nihva.com				REVISION - QTY - 1
ALL DIMENSION ARE IN mm			A3	SCALE - SHEET 16 OF 32

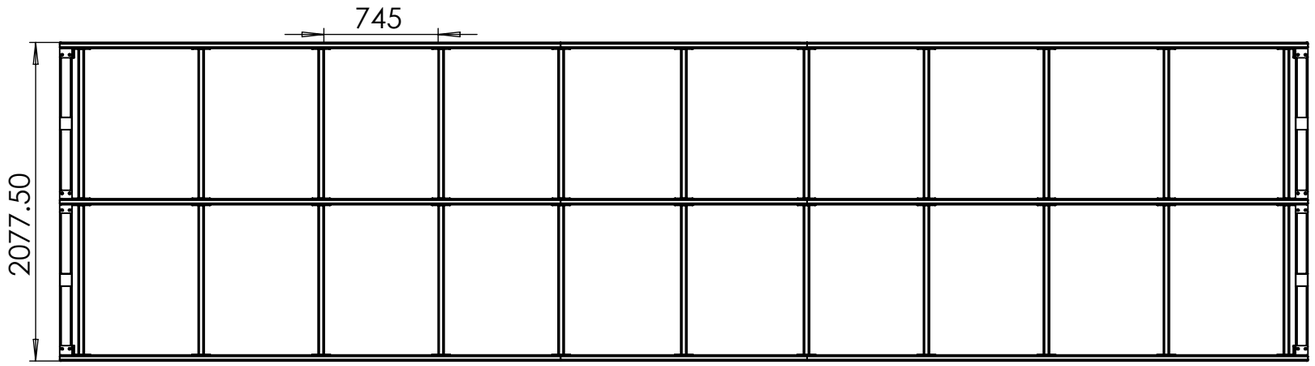


ITEM NO.	PART NUMBER	DESCRIPTION	QTY.
1	PANEL 3		1
2	bearing supporting tube	80 x 80 x 3mm	2
3	NP-PLT04_TP	MS - 100X100X10T	4
4	NP-PLT02_TP	MS - 100X100X10T	4
5	NP-PLT05_TP	MS - 150X100X10T	2
6	NP-PLT03_TP	MS - 150X100X10T	2
7	NP-PLT06_TP	MS - 110X100X10T	4
8	NP-PLT07_TP	MS - 70X50X10T	4
9	NP-PLT08_ TP	MS - 180X100X6T	4
10	SUPPORTING TUBES		22
11	ROLLER BRG HSG	MS ROLLER BRG HSG	4

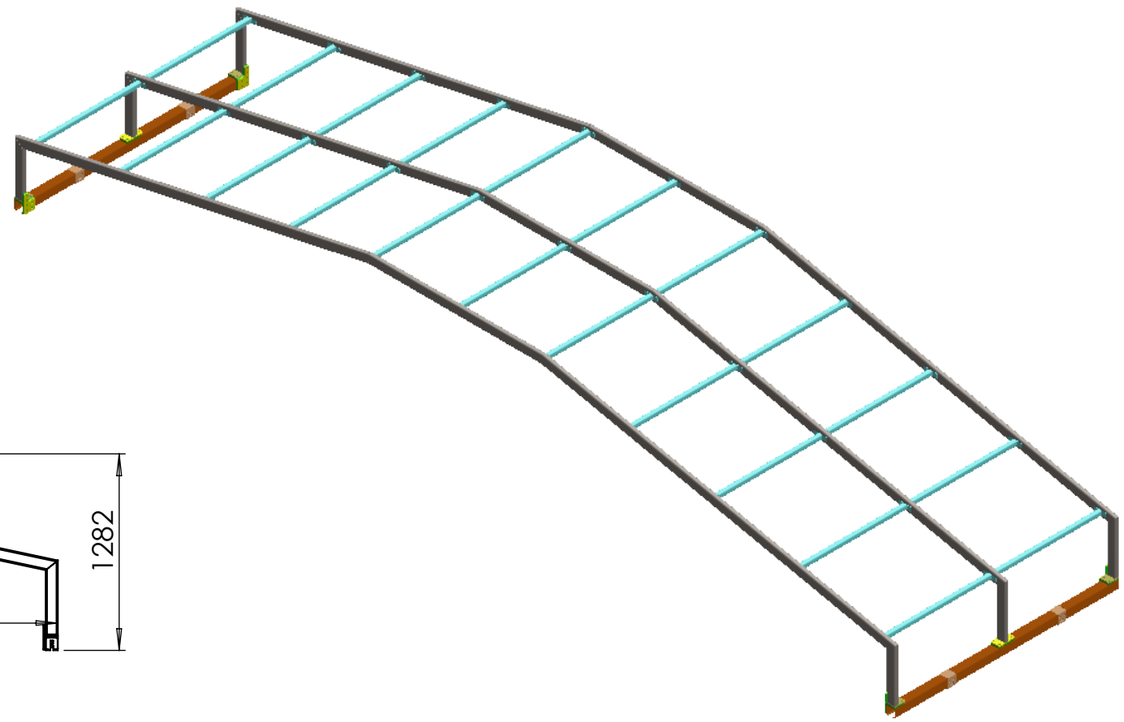


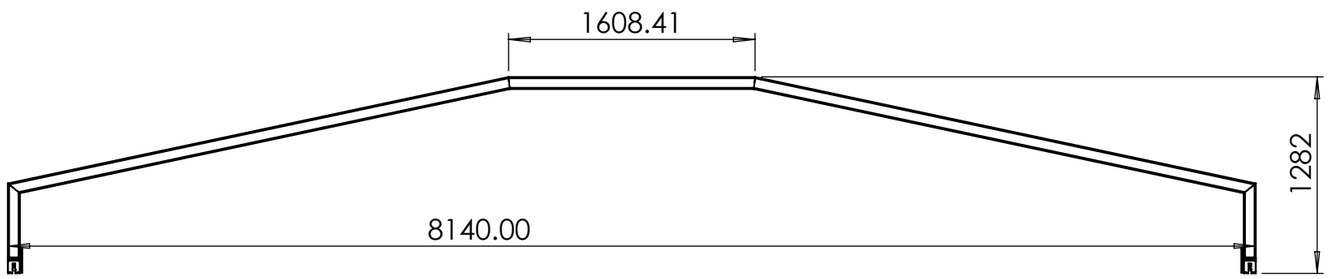


TITLE - RETRACTABLE ROOF				NIHVA TECHNOLOGIES PVT.LTD.PUNE
DWG NO - NTPL277-PM-01-03-00-00				Website - www.nihva.com
	NAME	SIGNATURE	DATE	PROJECT NO - NTPL277-PM
DRAWN	J.P		19-05-2025	PRODUCT - RETRACTABLE ROOF
CHK'D	S.W		19-05-2025	SITE LOCATION - AYODHYA
APPV'D	V.T.		19-05-2025	
if any queries contact - supportautomation@nihva.com				REVISION - QTY - 1
ALL DIMENSION ARE IN mm			A3	SCALE - SHEET 17 OF 32

ITEM NO.	PART NUMBER	DESCRIPTION	QTY.
1	PANEL 3		1

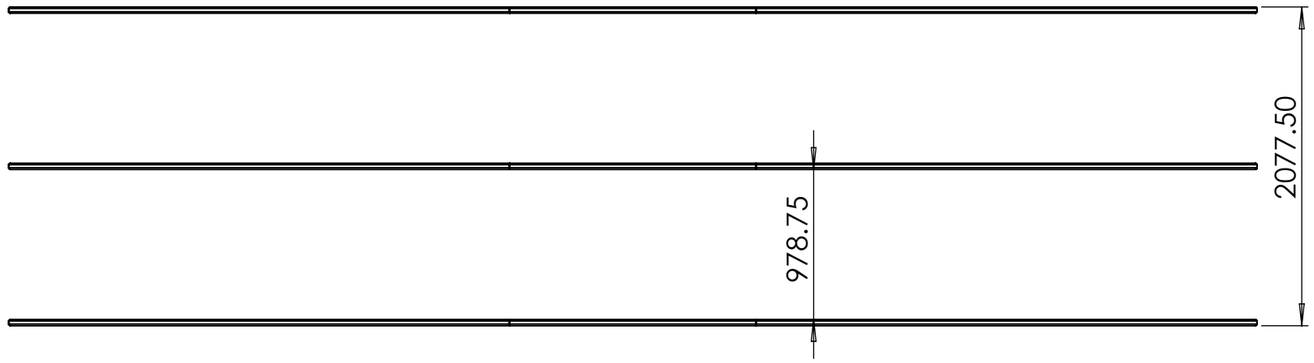


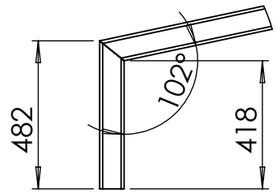


DETAIL H
SCALE 1 : 20

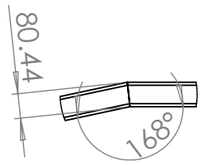


DETAIL N
SCALE 1 : 20

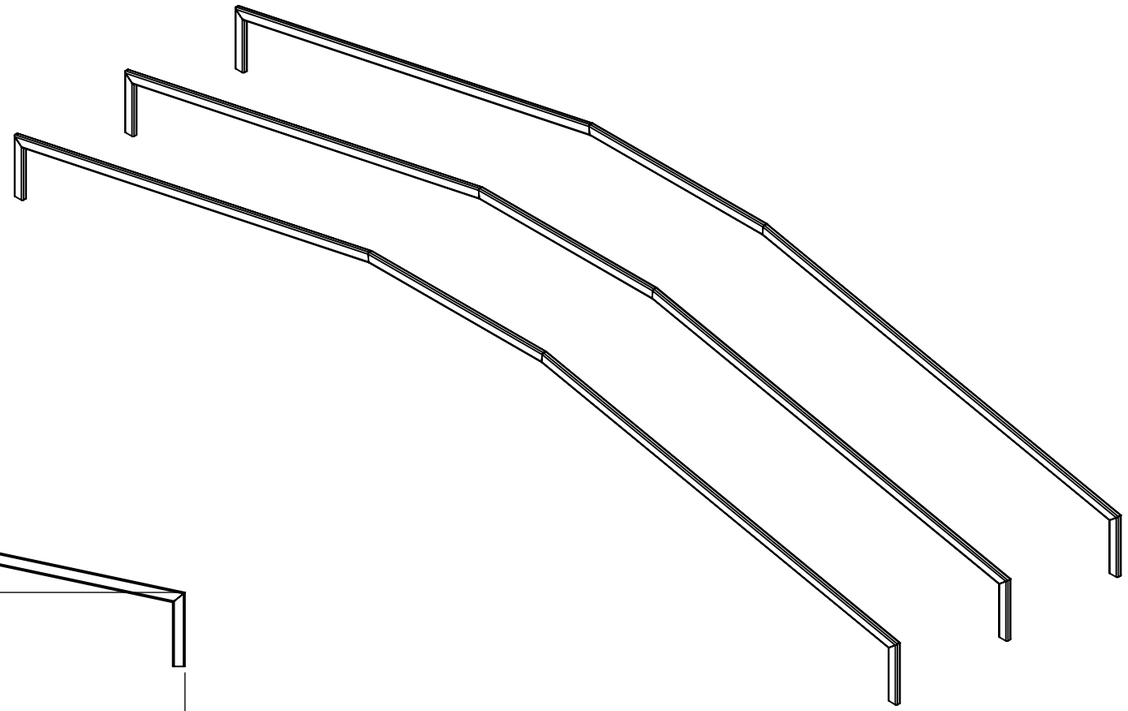


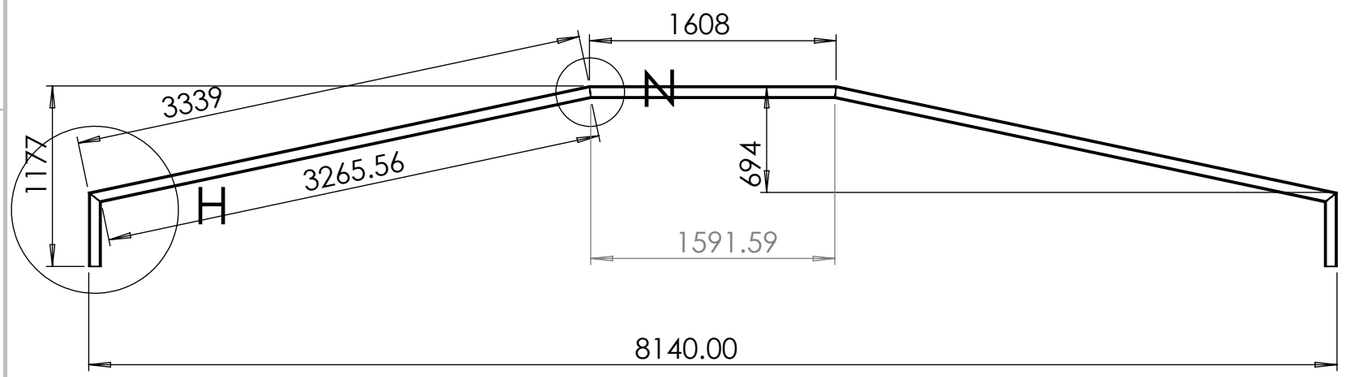


TITLE - RETRACTABLE ROOF				NIHVA TECHNOLOGIES PVT.LTD.PUNE
DWG NO - NTPL277-PM-01-03-00-01				Website - www.nihva.com
	NAME	SIGNATURE	DATE	PROJECT NO - NTPL277-PM
DRAWN	J.P		19-05-2025	PRODUCT - RETRACTABLE ROOF
CHK'D	S.W		19-05-2025	SITE LOCATION - AYODHYA
APPV'D	V.T.		19-05-2025	
if any queries contact - supportautomation@nihva.com				REVISION - QTY - 1
ALL DIMENSION ARE IN mm			A3	SCALE - SHEET 18 OF 32

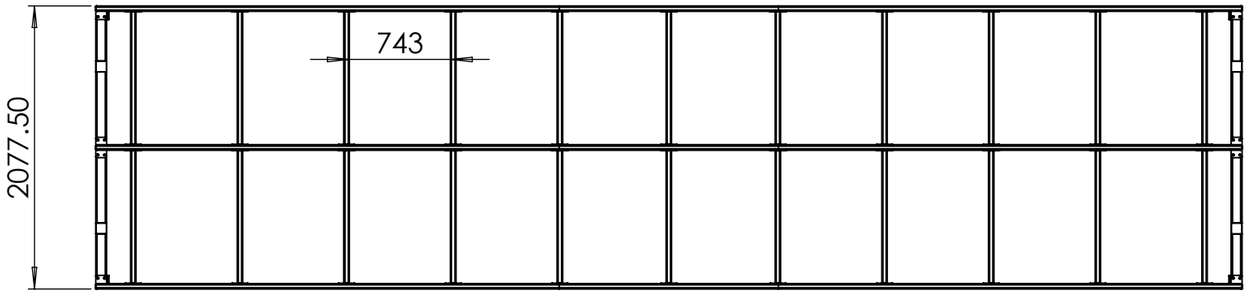

ITEM NO.	PART NUMBER	DESCRIPTION	QTY.
1	PANEL 4		1
2	4bearing supporting tube	80 x 80 x 3mm	2
3	NP-PLT04_TP	MS - 100X100X10T	4
4	NP-PLT02_TP	MS - 100X100X10T	4
5	NP-PLT05_TP	MS - 150X100X10T	2
6	NP-PLT03_TP	MS - 150X100X10T	2
7	NP-PLT06_TP	MS - 110X100X10T	4
8	NP-PLT07_TP	MS - 70X50X10T	4
9	NP-PLT08_ TP	MS - 180X100X6T	4
10	SUPPORTING TUBES		22
11	ROLLER BRG HSG	MS ROLLER BRG HSG	4

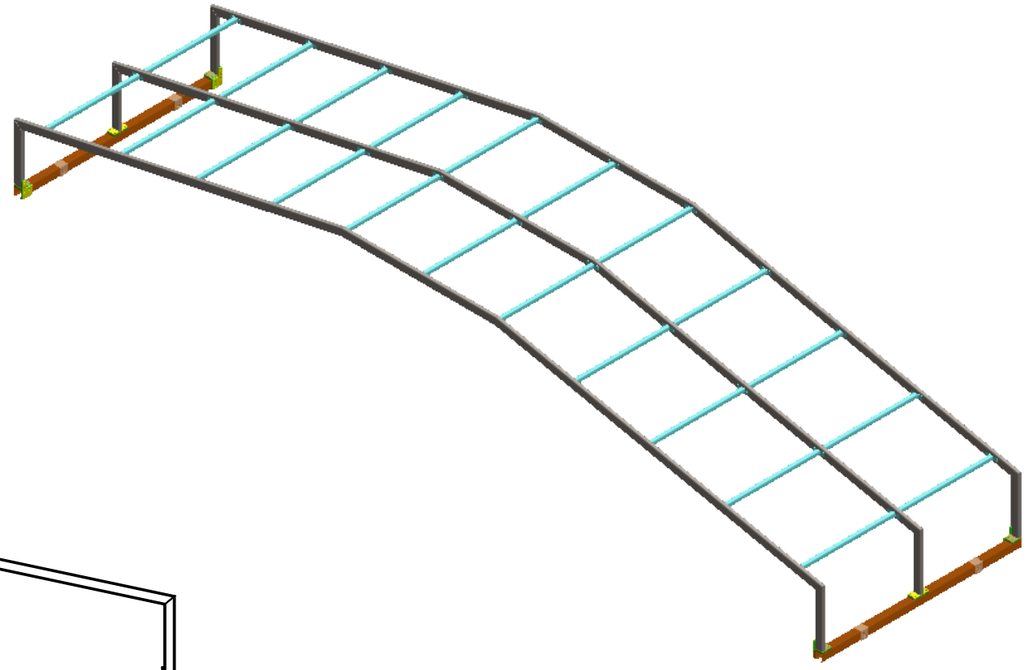


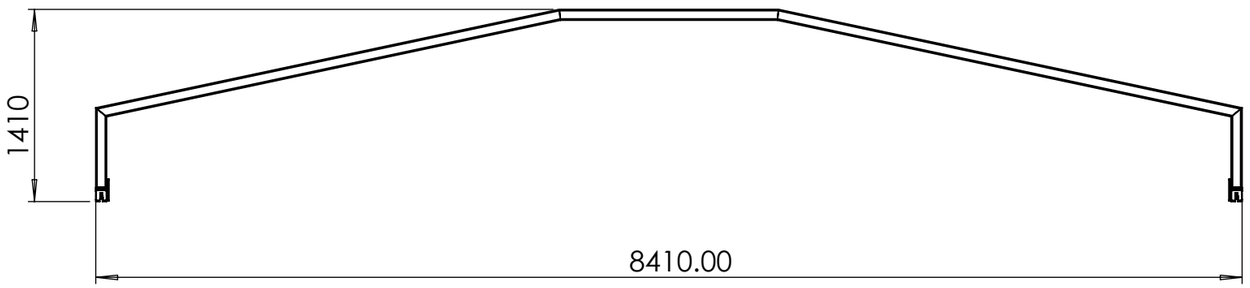

TITLE - RETRACTABLE ROOF				NIHVA TECHNOLOGIES PVT.LTD.PUNE
DWG NO - NTPL277-PM-01-04-00-00				Website - www.nihva.com
	NAME	SIGNATURE	DATE	PROJECT NO - NTPL277-PM
DRAWN	J.P		19-05-2025	PRODUCT - RETRACTABLE ROOF
CHK'D	S.W		19-05-2025	SITE LOCATION - AYODHYA
APPV'D	V.T.		19-05-2025	
if any queries contact - supportautomation@nihva.com				REVISION - QTY - 1
ALL DIMENSION ARE IN mm			A3	SCALE - SHEET 19 OF 32


ITEM NO.	PART NUMBER	DESCRIPTION	QTY.
1	PANEL 4		1



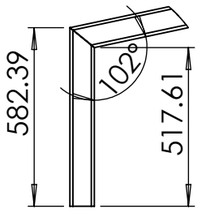


DETAIL K


SCALE 1 : 20

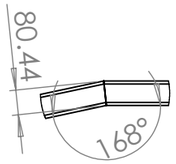


DETAIL O

SCALE 1 : 20

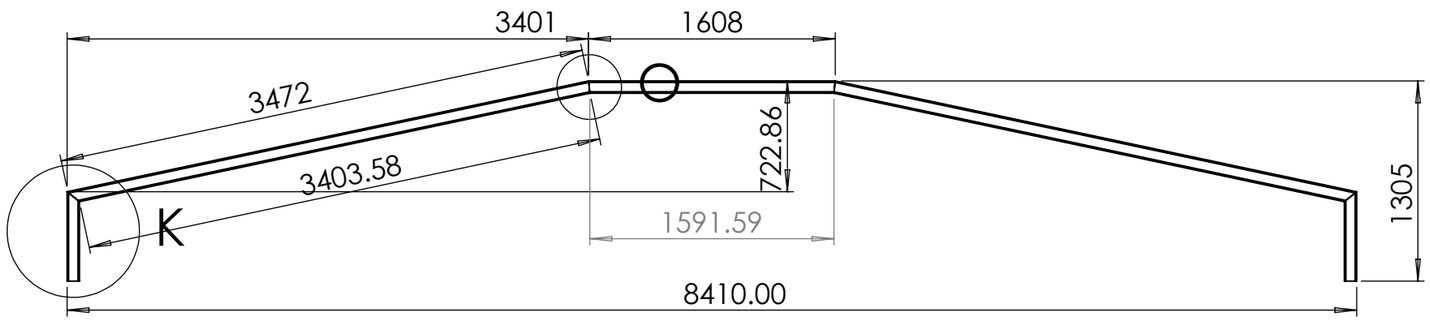


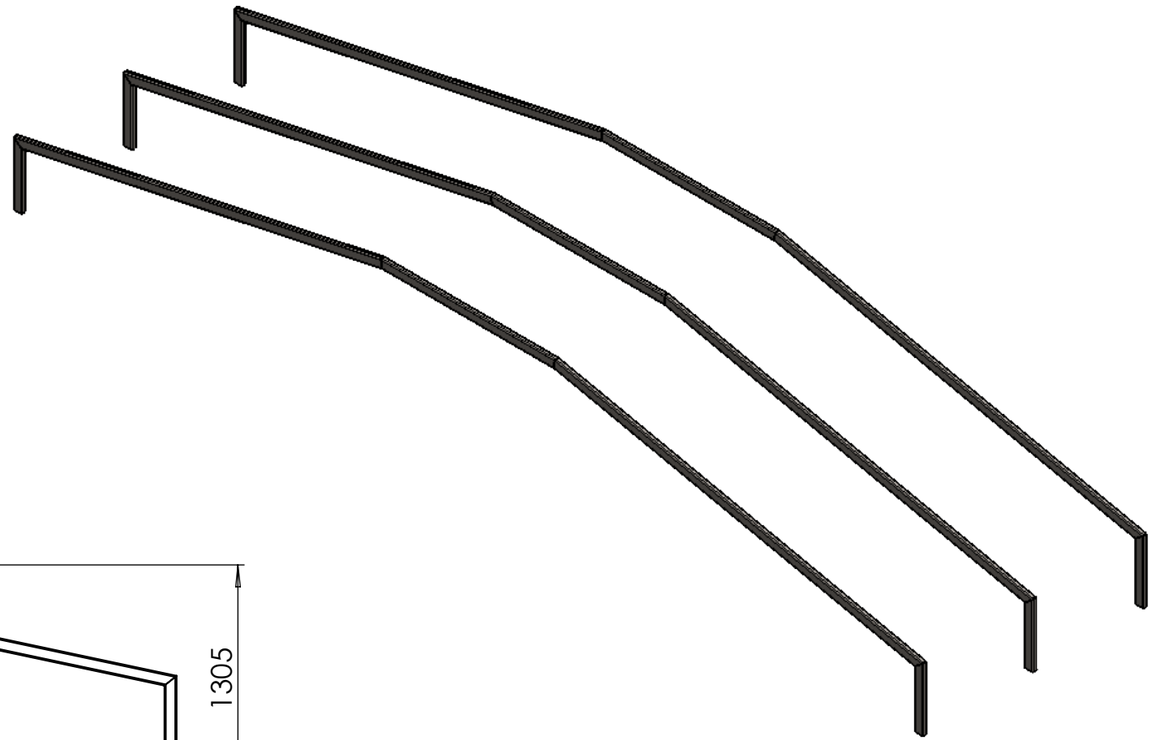


TITLE - RETRACTABLE ROOF				NIHVA TECHNOLOGIES PVT.LTD.PUNE
DWG NO - NTPL277-PM-01-04-00-01				Website - www.nihva.com
	NAME	SIGNATURE	DATE	PROJECT NO - NTPL277-PM
DRAWN	J.P		19-05-2025	PRODUCT - RETRACTABLE ROOF
CHK'D	S.W		19-05-2025	SITE LOCATION - AYODHYA
APPV'D	V.T.		19-05-2025	
if any queries contact - supportautomation@nihva.com				REVISION - / QTY - 1
ALL DIMENSION ARE IN mm			A3	SCALE - / SHEET 20 OF 32

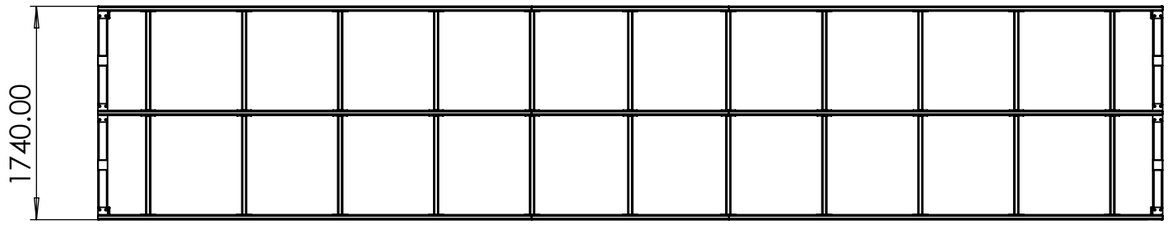

ITEM NO.	PART NUMBER	DESCRIPTION	QTY.
1	PANEL 5		1
2	bearing supporting tube	80 x 80 x 3mm	2
3	NP-PLT04_TP	MS - 100X100X10T	4
4	NP-PLT02_TP	MS - 100X100X10T	4
5	NP-PLT05_TP	MS - 150X100X10T	2
6	NP-PLT03_TP	MS - 150X100X10T	2
7	NP-PLT06_TP	MS - 110X100X10T	4
8	NP-PLT07_TP	MS - 70X50X10T	4
9	NP-PLT08_ TP	MS - 180X100X6T	4
10	SUPPORTING TUBES		22
11	ROLLER BRG HSG	MS ROLLER BRG HSG	4
12	PANEL 5 ENCLOSER		1

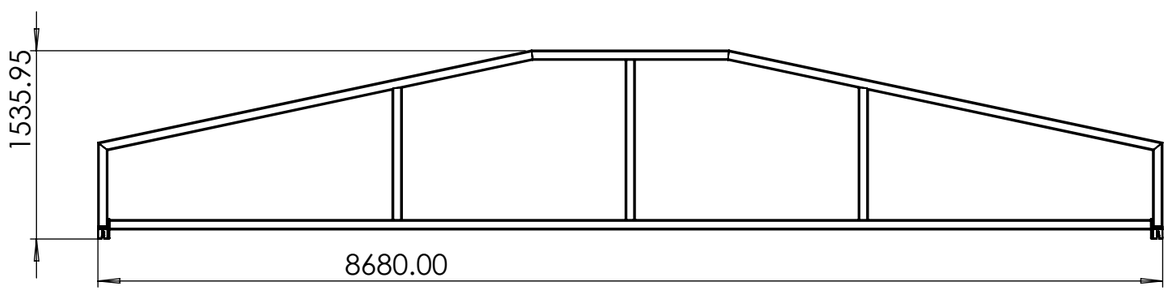

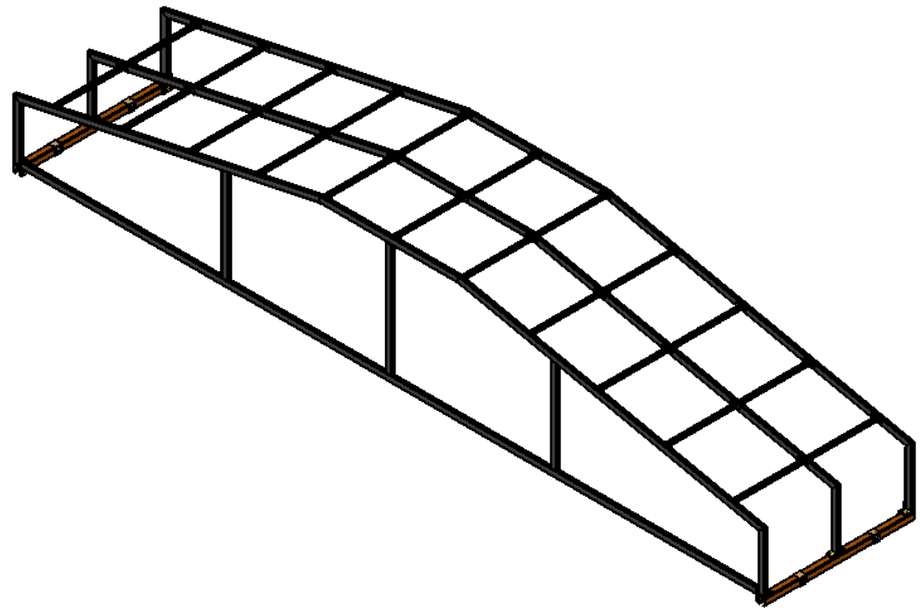

TITLE - RETRACTABLE ROOF

DWG NO - NTPL277-PM-01-00-00-00

NIHVA TECHNOLOGIES PVT.LTD.PUNE

Website - www.nihva.com

	NAME	SIGNATURE	DATE
DRAWN	J.P		19-05-2025
CHK'D	S.W		19-05-2025
APPV'D	V.T.		19-05-2025

PROJECT NO - NTPL277-PM

PRODUCT - RETRACTABLE ROOF

SITE LOCATION - AYODHYA

if any queries contact - supportautomation@nihva.com

REVISION -

QTY - 1


ALL DIMENSION ARE IN mm


A3

SCALE -

SHEET 21 OF 32

ITEM NO.	PART NUMBER	DESCRIPTION	QTY.
1	PANEL 5 ENCLOSER		1

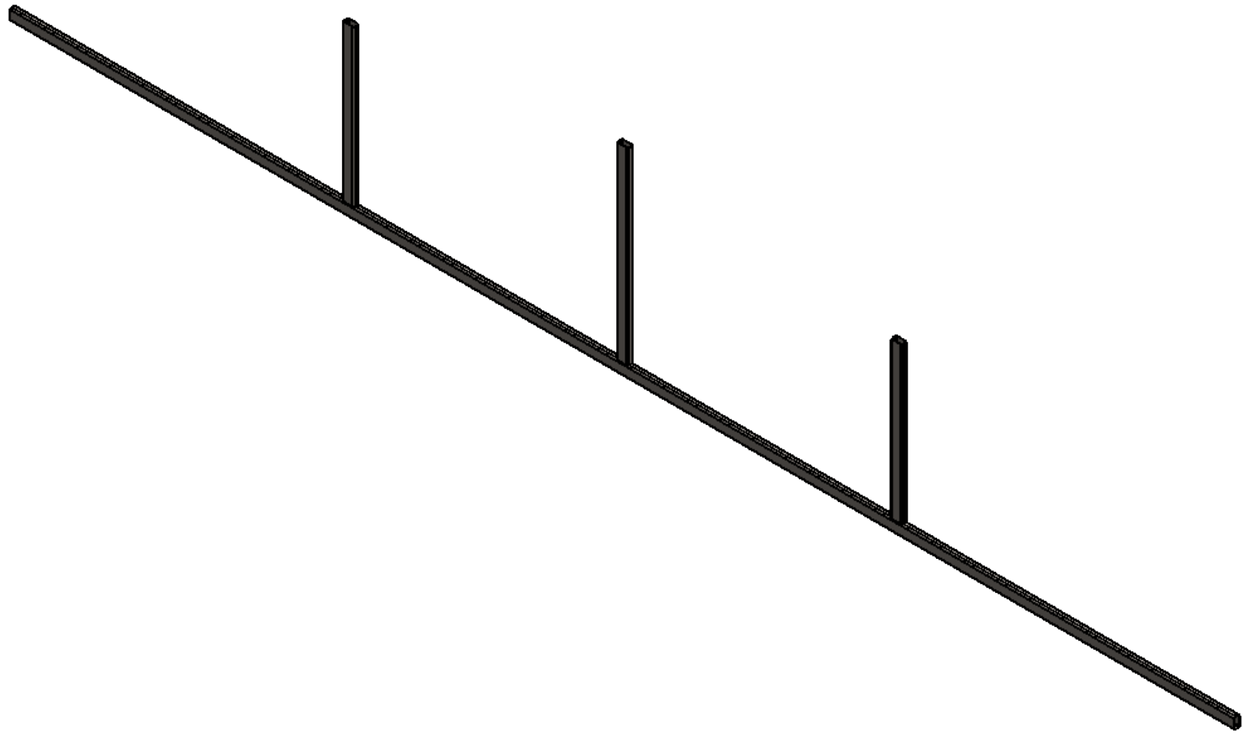


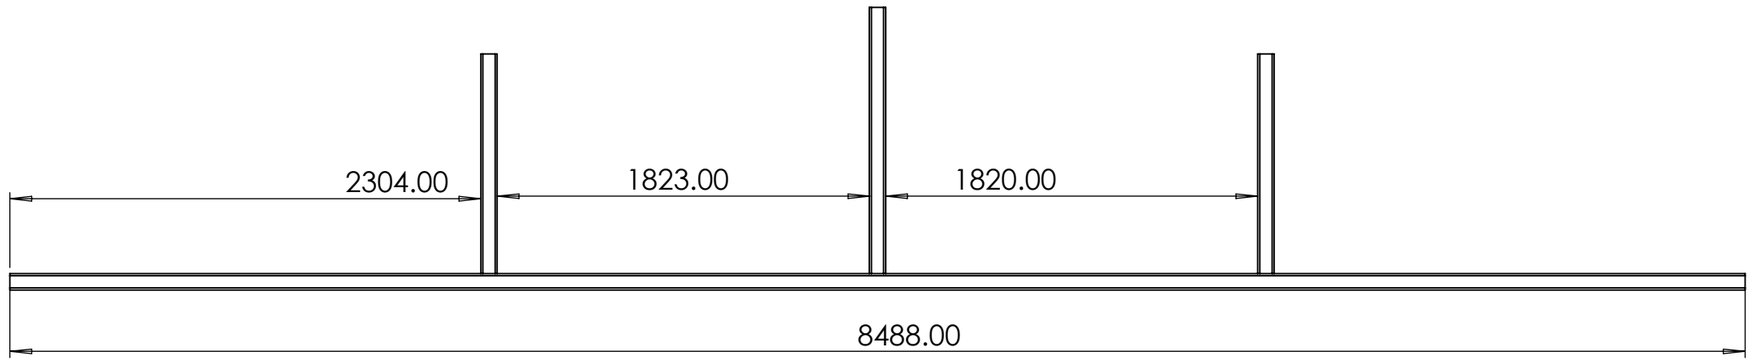

TITLE - RETRACTABLE ROOF				NIHVA TECHNOLOGIES PVT.LTD.PUNE
DWG NO - NTPL277-PM-01-05-00-01				Website - www.nihva.com
	NAME	SIGNATURE	DATE	PROJECT NO - NTPL277-PM
DRAWN	J.P		19-05-2025	PRODUCT - RETRACTABLE ROOF
CHK'D	S.W		19-05-2025	SITE LOCATION - AYODHYA
APPV'D	V.T.		19-05-2025	
if any queries contact - supportautomation@nihva.com				REVISION - QTY - 1
ALL DIMENSION ARE IN mm		A3		SCALE - SHEET 22 OF 32


ITEM NO.	PART NUMBER	DESCRIPTION	QTY.
1	PANEL 5		1



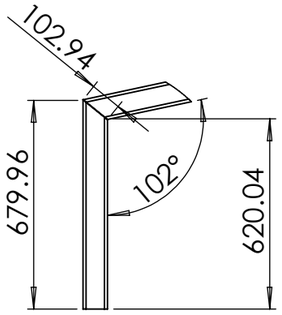


DETAIL L


SCALE 1 : 20

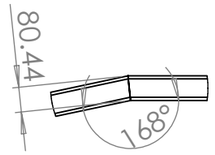

DETAIL P


SCALE 1 : 20

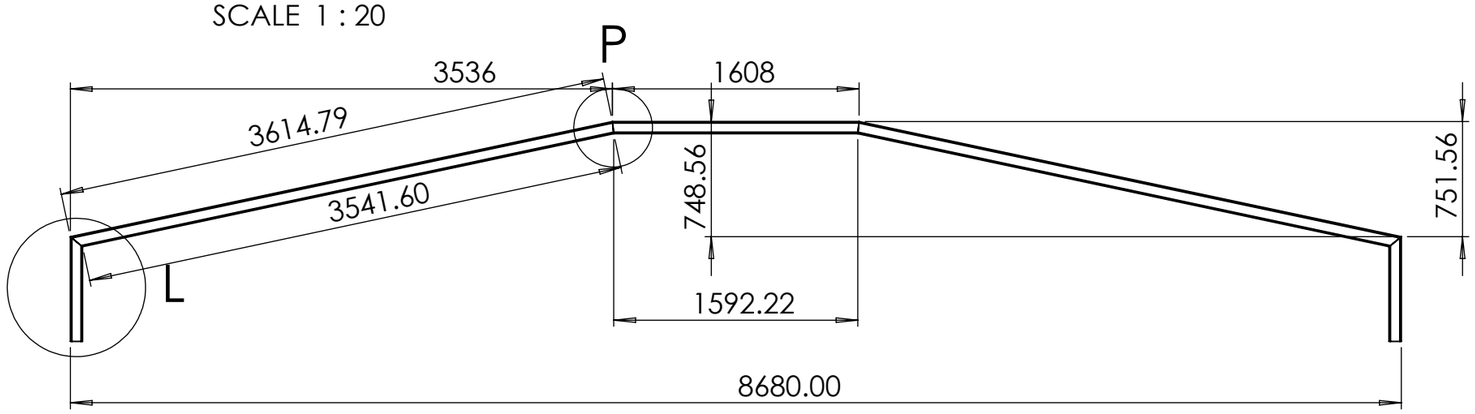

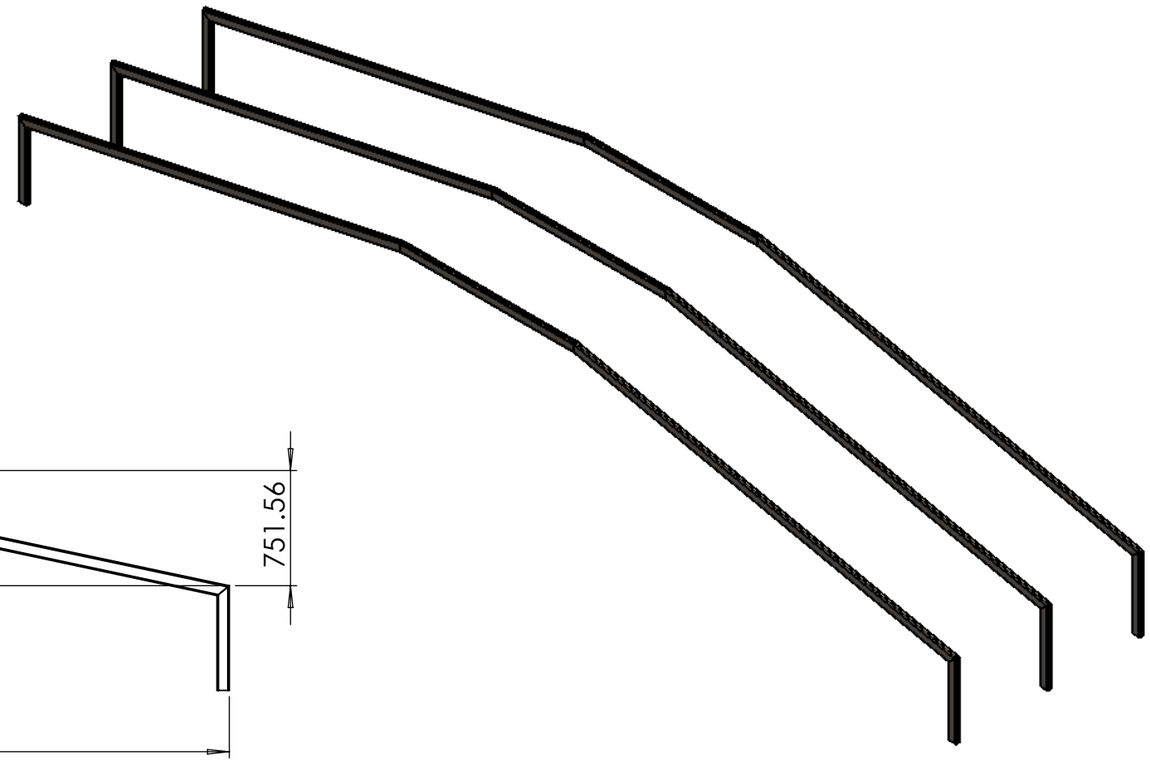

TITLE - RETRACTABLE ROOF				NIHVA TECHNOLOGIES PVT.LTD.PUNE
DWG NO - NTPL277-PM-01-05-00-02				Website - www.nihva.com
	NAME	SIGNATURE	DATE	PROJECT NO - NTPL277-PM
DRAWN	J.P		19-05-2025	PRODUCT - RETRACTABLE ROOF
CHK'D	S.W		19-05-2025	SITE LOCATION - AYODHYA
APPV'D	V.T.		19-05-2025	
if any queries contact - supportautomation@nihva.com				REVISION - QTY - 1
ALL DIMENSION ARE IN mm			A3	SCALE - SHEET 23 OF 32


ITEM NO.	PART NUMBER	DESCRIPTION	QTY.
1	T 89 STANDARD track		10

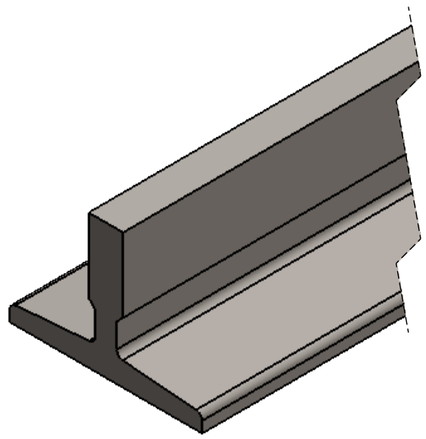

track length = 9400mm


TITLE - RETRACTABLE ROOF				NIHVA TECHNOLOGIES PVT.LTD.PUNE
DWG NO - NTPL277-PM-01-00-00-01				Website - www.nihva.com
	NAME	SIGNATURE	DATE	PROJECT NO - NTPL277-PM
DRAWN	J.P		19-05-2025	PRODUCT - RETRACTABLE ROOF
CHK'D	S.W		19-05-2025	SITE LOCATION - AYODHYA
APPV'D	V.T.		19-05-2025	
if any queries contact - supportautomation@nihva.com				REVISION - QTY - 1
ALL DIMENSION ARE IN mm			A3	SCALE - SHEET 24 OF 32


ITEM NO.	PART NUMBER	DESCRIPTION	QTY.
1	RACK	STD (M4 RACK, 30x8x1000 mm, ZINC COATED WITH SPACERS AND SCREWS.)	11

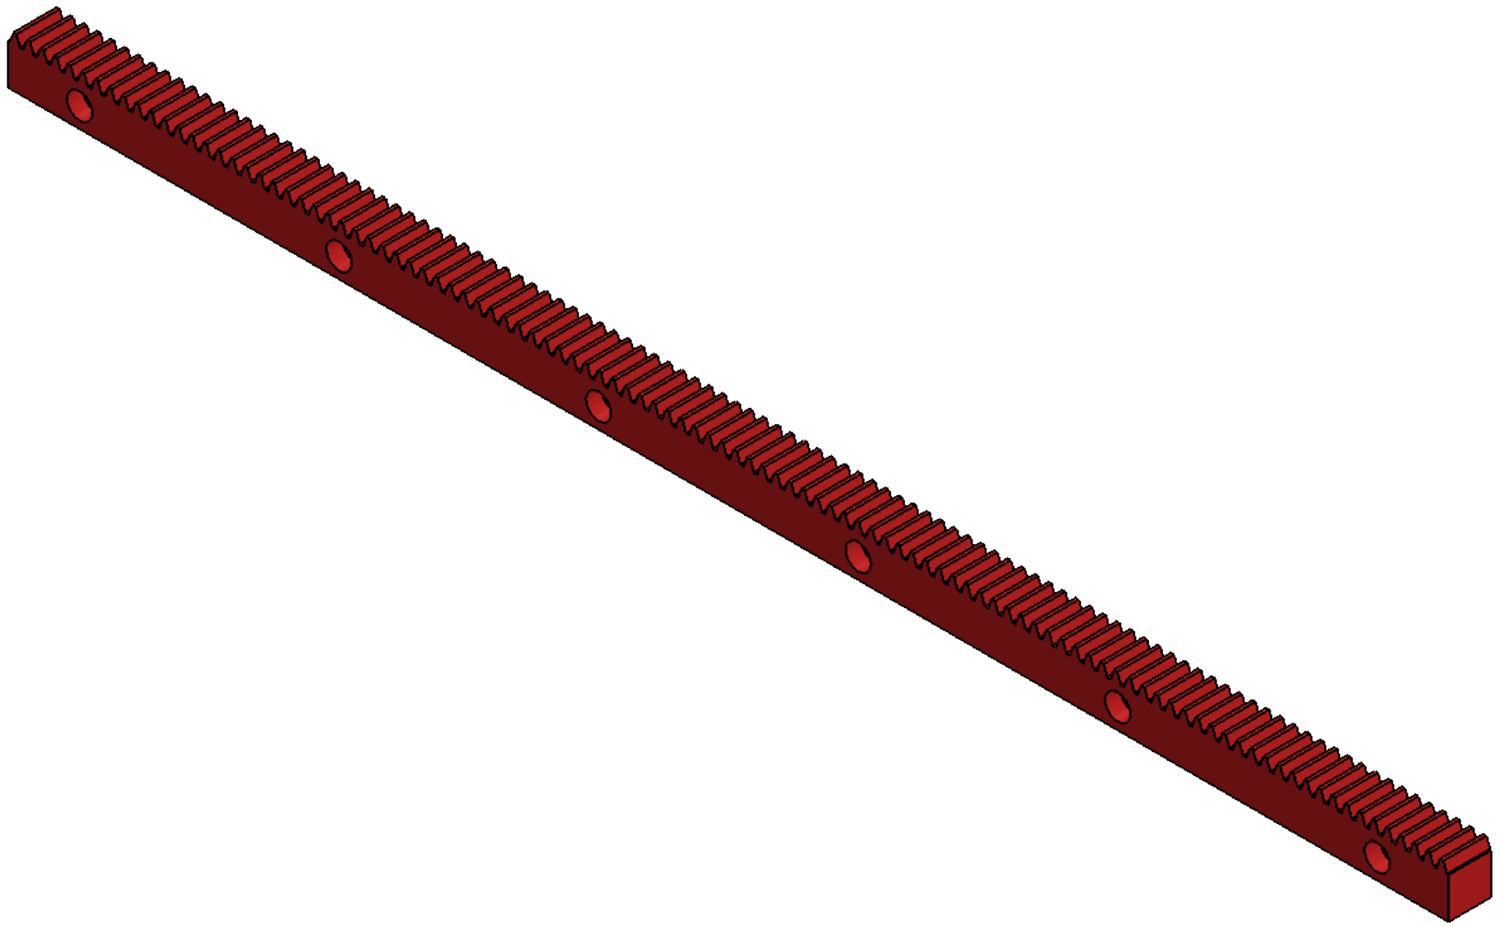


TITLE - RETRACTABLE ROOF				NIHVA TECHNOLOGIES PVT.LTD.PUNE
DWG NO - NTPL277-PM-01-00-00-02				Website - www.nihva.com
	NAME	SIGNATURE	DATE	PROJECT NO - NTPL277-PM
DRAWN	J.P		19-05-2025	PRODUCT - RETRACTABLE ROOF
CHK'D	S.W		19-05-2025	SITE LOCATION - AYODHYA
APPV'D	V.T.		19-05-2025	
if any queries contact - supportautomation@nihva.com				REVISION - QTY - 1
ALL DIMENSION ARE IN mm		A3		SCALE - SHEET 25 OF 32

ITEM NO.	PART NUMBER	DESCRIPTION	QTY.
1	C- CHANEL MTG BASE PLATE (leser cutting)	320X50X10MM THK	1
2	C - CHANEL	70X30X780	2
3	C- CHANEL JOINING PLATE	35X40X10MM THK	1
4	BUSBAR MTG PLATE		2

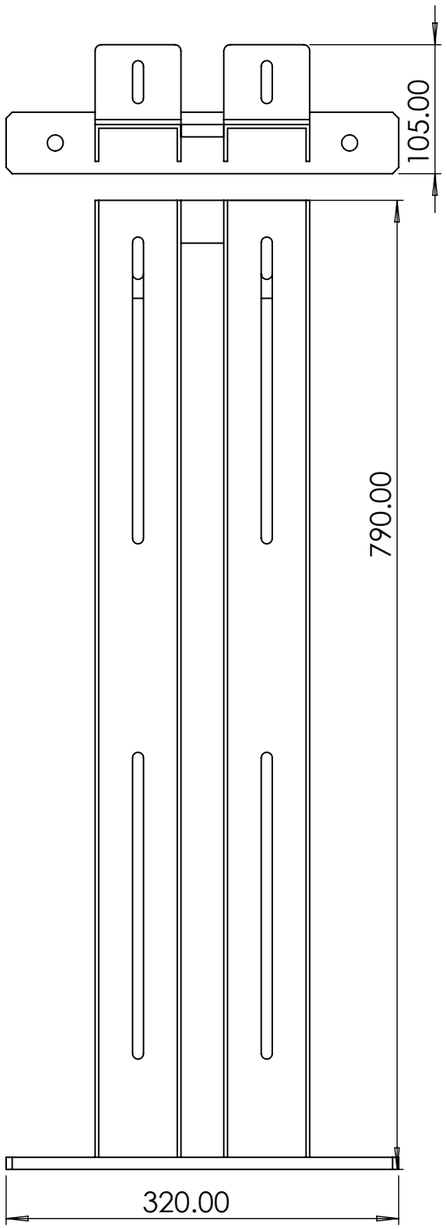


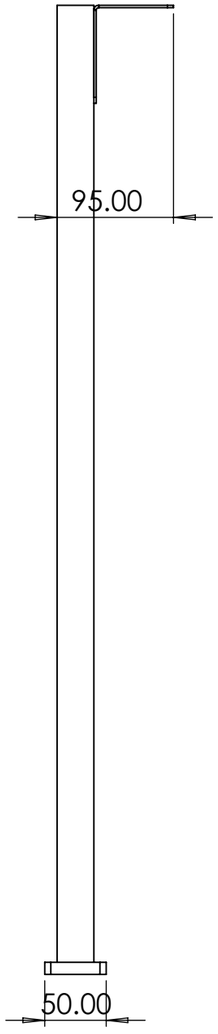


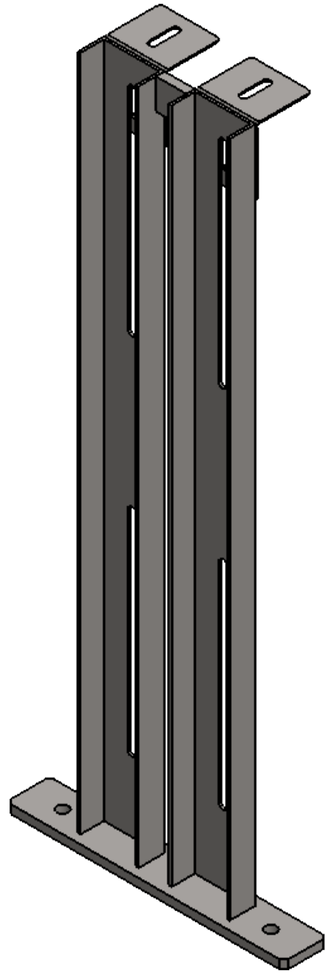


TITLE - RETRACTABLE ROOF				NIHVA TECHNOLOGIES PVT.LTD.PUNE
DWG NO - NTPL277-PM-01-06-00-00				Website - www.nihva.com
	NAME	SIGNATURE	DATE	PROJECT NO - NTPL277-PM
DRAWN	J.P		19-05-2025	PRODUCT - RETRACTABLE ROOF
CHK'D	S.W		19-05-2025	SITE LOCATION - AYODHYA
APPV'D	V.T.		19-05-2025	
if any queries contact - supportautomation@nihva.com				REVISION - / QTY - 1
ALL DIMENSION ARE IN mm		A3		SCALE - / SHEET 26 OF 32


ITEM NO.	PART NUMBER	DESCRIPTION	QTY.
1	C- CHANEL MTG BASE PLATE (leser cutting)	320X50X10MM THK	11

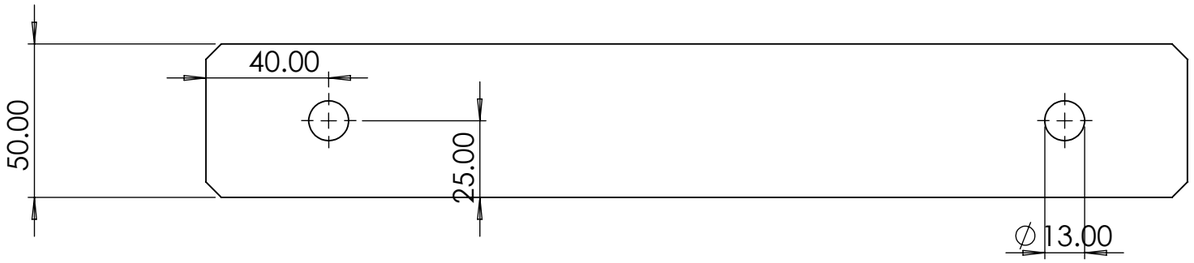


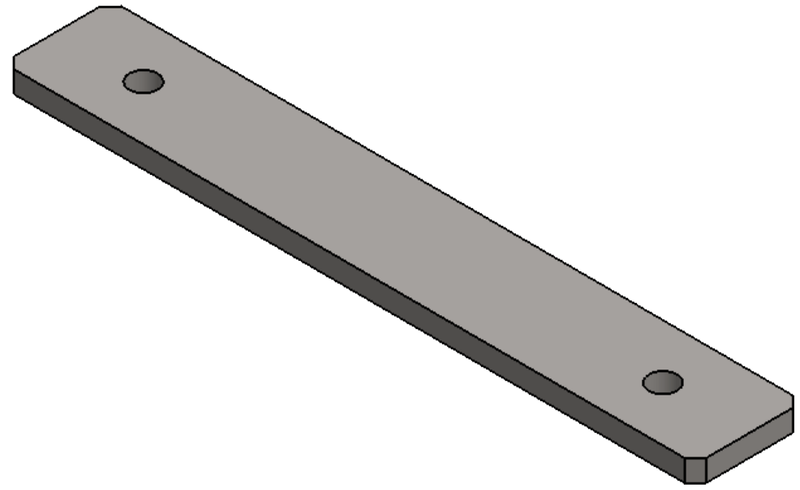

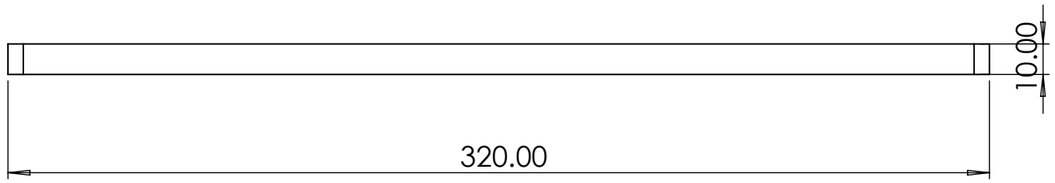

TITLE - RETRACTABLE ROOF				NIHVA TECHNOLOGIES PVT.LTD.PUNE
DWG NO - NTPL277-PM-01-06-00-01				Website - www.nihva.com
	NAME	SIGNATURE	DATE	PROJECT NO - NTPL277-PM
DRAWN	J.P		19-05-2025	PRODUCT - RETRACTABLE ROOF
CHK'D	S.W		19-05-2025	SITE LOCATION - AYODHYA
APPV'D	V.T.		19-05-2025	
if any queries contact - supportautomation@nihva.com				REVISION - QTY - 1
ALL DIMENSION ARE IN mm		A3		SCALE - SHEET 27 OF 32

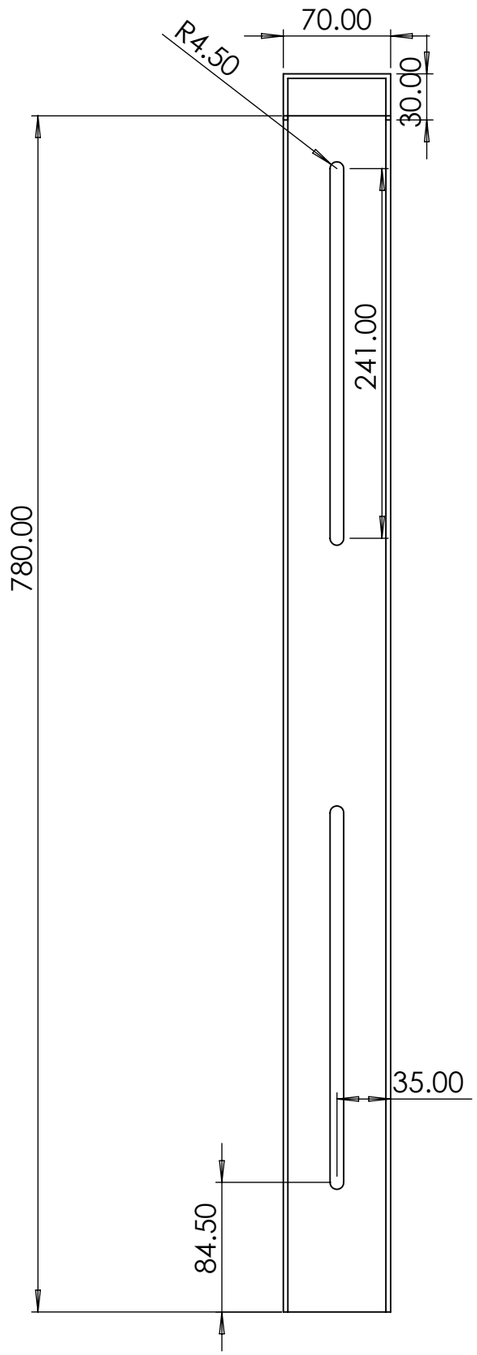


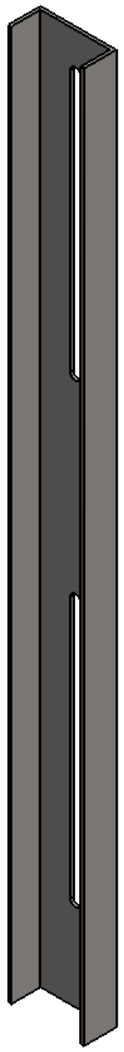


ITEM NO.	PART NUMBER	DESCRIPTION	QTY.
1	C - CHANEL	70X30X780	22

TITLE - RETRACTABLE ROOF				NIHVA TECHNOLOGIES PVT.LTD.PUNE
DWG NO - NTPL277-PM-01-06-00-02				Website - www.nihva.com
	NAME	SIGNATURE	DATE	PROJECT NO - NTPL277-PM
DRAWN	J.P		19-05-2025	PRODUCT - RETRACTABLE ROOF
CHK'D	S.W		19-05-2025	SITE LOCATION - AYODHYA
APPV'D	V.T.		19-05-2025	
if any queries contact - supportautomation@nihva.com				REVISION - QTY - 1
ALL DIMENSION ARE IN mm			A3	SCALE - SHEET 28 OF 32


ITEM NO.	PART NUMBER	DESCRIPTION	QTY.
1	BUSBAR MTG PLATE		22

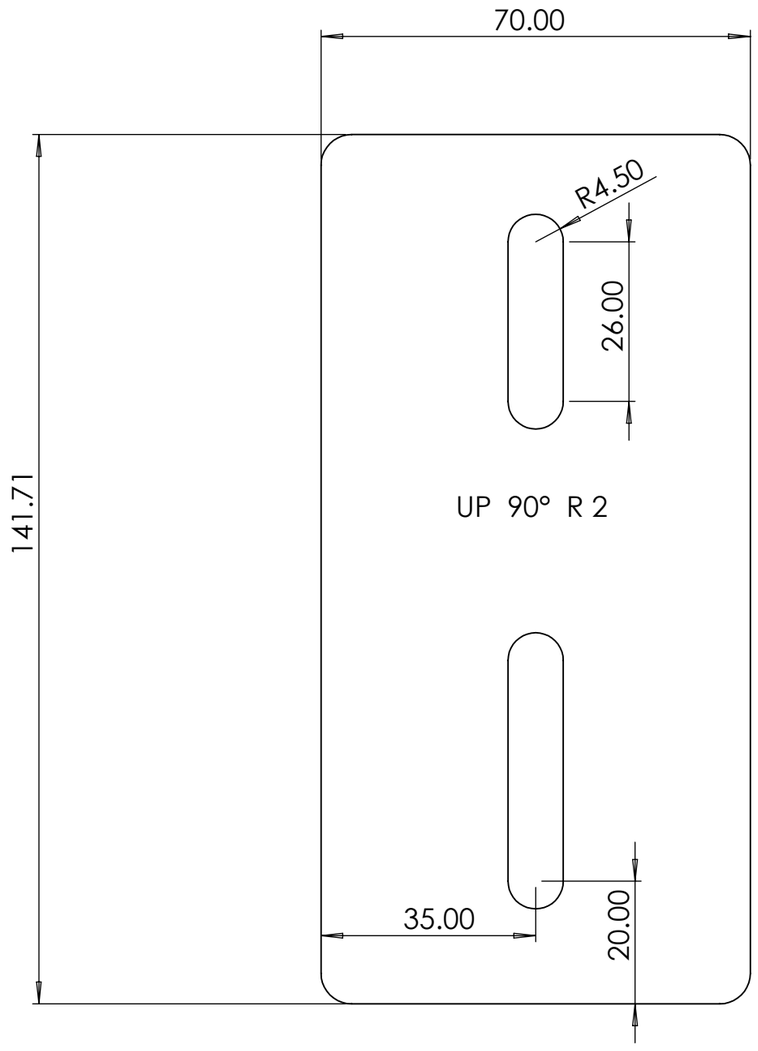


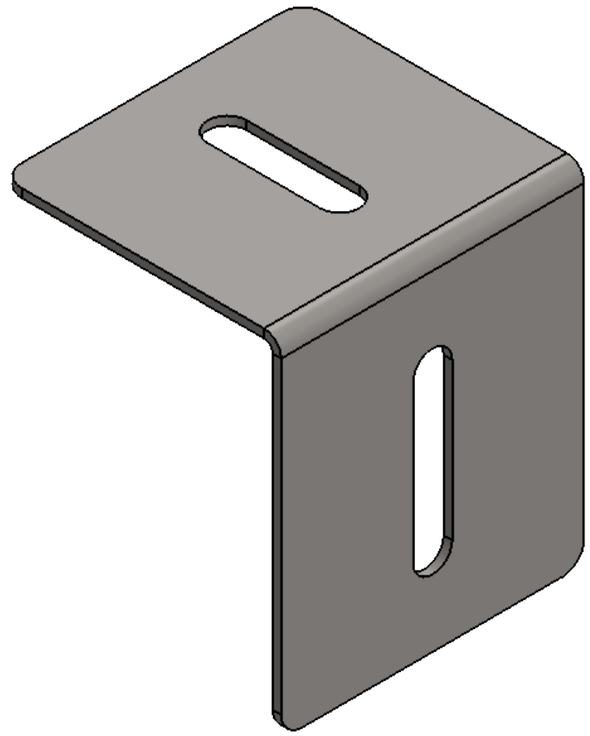

TITLE - RETRACTABLE ROOF				NIHVA TECHNOLOGIES PVT.LTD.PUNE
DWG NO - NTPL277-PM-01-06-00-03				Website - www.nihva.com
	NAME	SIGNATURE	DATE	PROJECT NO - NTPL277-PM
DRAWN	J.P		19-05-2025	PRODUCT - RETRACTABLE ROOF
CHK'D	S.W		19-05-2025	SITE LOCATION - AYODHYA
APPV'D	V.T.		19-05-2025	
if any queries contact - supportautomation@nihva.com				REVISION - QTY - 1
ALL DIMENSION ARE IN mm			A3	SCALE - SHEET 29 OF 32


ITEM NO.	PART NUMBER	DESCRIPTION	QTY.
1	C- CHANEL JOINING PLATE	35X40X10MM THK	22

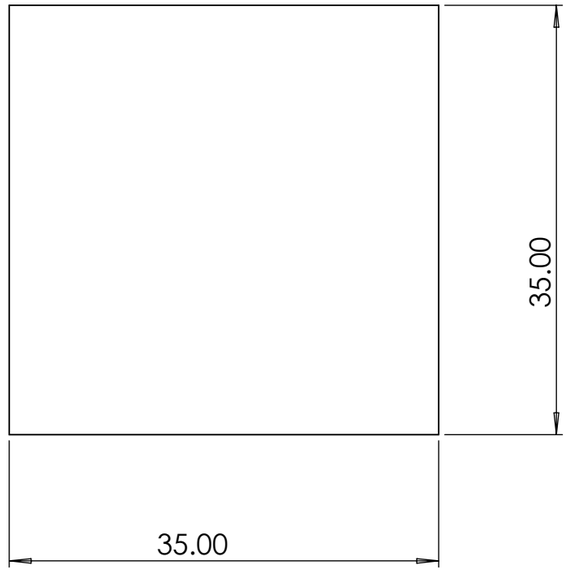


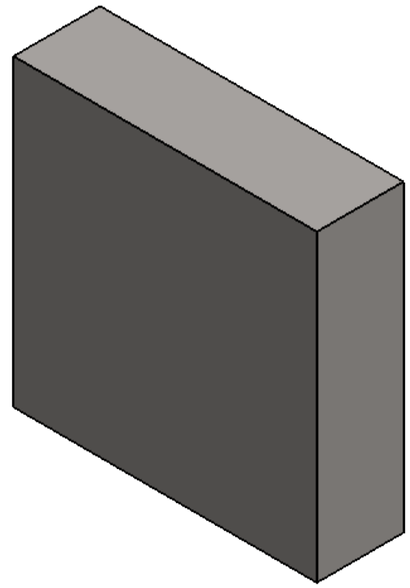

TITLE - RETRACTABLE ROOF				NIHVA TECHNOLOGIES PVT.LTD.PUNE
4DWG NO - NTPL277-PM-01-06-00-04				Website - www.nihva.com
	NAME	SIGNATURE	DATE	PROJECT NO - NTPL277-PM
DRAWN	J.P		19-05-2025	PRODUCT - RETRACTABLE ROOF
CHK'D	S.W		19-05-2025	SITE LOCATION - AYODHYA
APPV'D	V.T.		19-05-2025	
if any queries contact - supportautomation@nihva.com				REVISION - QTY - 1
ALL DIMENSION ARE IN mm		A3		SCALE - SHEET 30 OF 32

ITEM NO.	PART NUMBER	DESCRIPTION	QTY.
1	MOTOR MTG BRT PLATE 1_NICE_1.8T	514X681X5MM THK	1

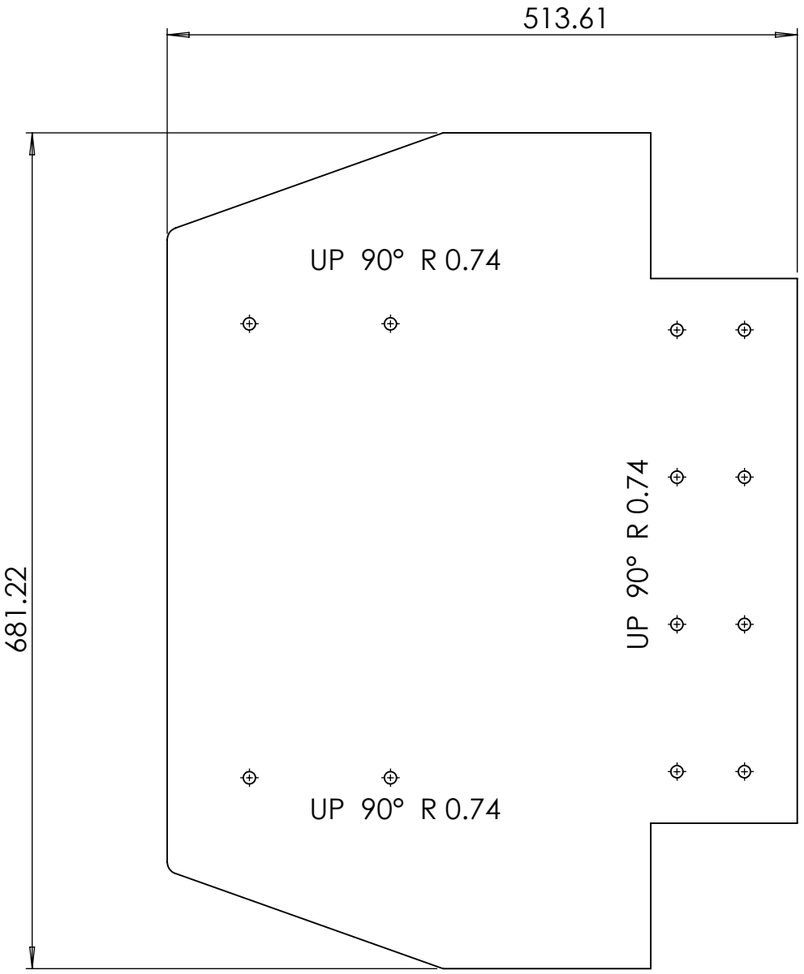

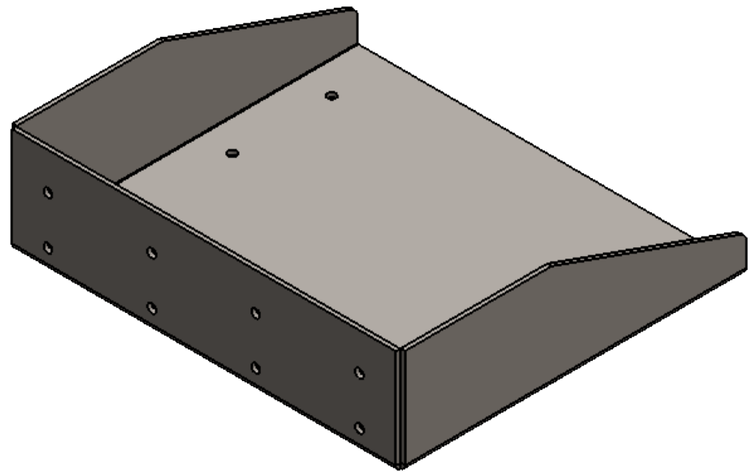

TITLE - RETRACTABLE ROOF				NIHVA TECHNOLOGIES PVT.LTD.PUNE
DWG NO - NTPL277-PM-01-00-00-00				Website - www.nihva.com
	NAME	SIGNATURE	DATE	PROJECT NO - NTPL277-PM
DRAWN	J.P		19-05-2025	PRODUCT - RETRACTABLE ROOF
CHK'D	S.W		19-05-2025	SITE LOCATION - AYODHYA
APPV'D	V.T.		19-05-2025	
if any queries contact - supportautomation@nihva.com				REVISION - QTY - 1
ALL DIMENSION ARE IN mm		A3		SCALE - SHEET 31 OF 32

TITLE - RETRACTABLE ROOF				NIHVA TECHNOLOGIES PVT.LTD.PUNE
DWG NO - NTPL277-PM-01-00-00-00				Website - www.nihva.com
	NAME	SIGNATURE	DATE	PROJECT NO - NTPL277-PM
DRAWN	J.P		19-05-2025	PRODUCT - RETRACTABLE ROOF
CHK'D	S.W		19-05-2025	SITE LOCATION - AYODHYA
APPV'D	V.T.		19-05-2025	
if any queries contact - supportautomation@nihva.com				REVISION - QTY - 1
ALL DIMENSION ARE IN mm			A3	SCALE - SHEET 32 OF 32