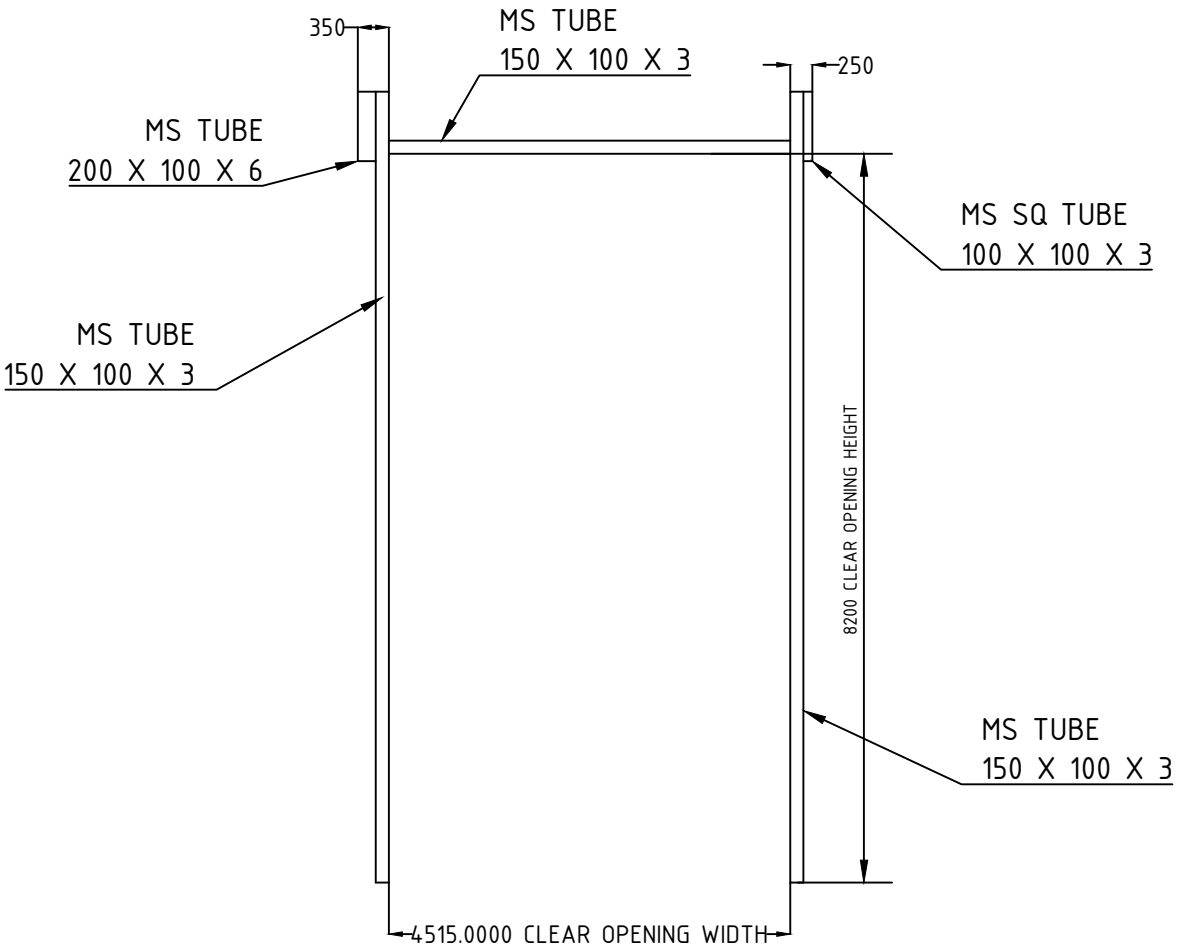

DIMENSION :

CLEAR WIDTH	CLEAR HEIGHT	QUANTITY
4515 mm	8200 mm	

MATERIAL :

THICKNESS :

NOTE:-

NIHVA
NIHVA TECHNOLOGIES PVT. LTD.
NIHVA TECHNOLOGIES PVT. LTD. PUNE
Email:- info@nihva.com
Website:- www.nihva.com

TITLE:

DOUBLE WALL ROLLING SHUTTER STRUCTURE

CLIENT'S APPROVAL :

CLIENT - SEZ BIOTECH

PROJECT -

SITE LOCATION - PUNE

DWG. NO. : NIHVA/20-21/0205

SCALE: NTS	WT:	SHEET:1 OF 1

DRAWN BY: G.P.	DATE: 12-08-2021
CHECKED BY: A.K.	DATE: 12-08-2021
APPROVED BY : V.T.	DATE: 12-08-2021

If any queries contact : design@nihva.com

NOTE: ALL DIMENSIONS ARE IN mm

THIS DRAWING & DESIGN IS THE PROPERTY OF NIHVA TECHNOLOGIES. NOT TO BE SOLD OR COPIED TO ANY OTHER CONCERN.