



PRODUCED BY AN AUTODESK EDUCATIONAL PRODUCT

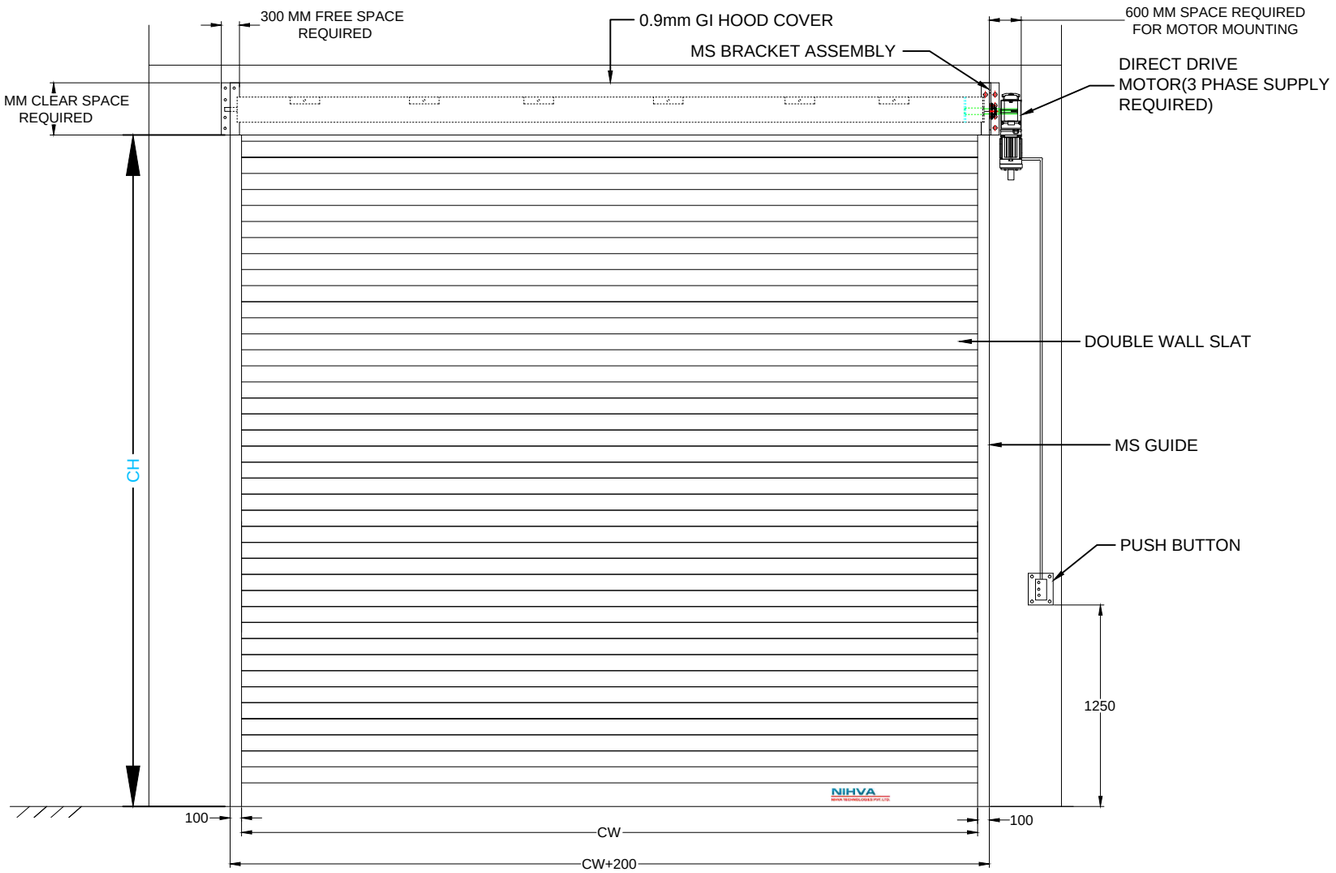

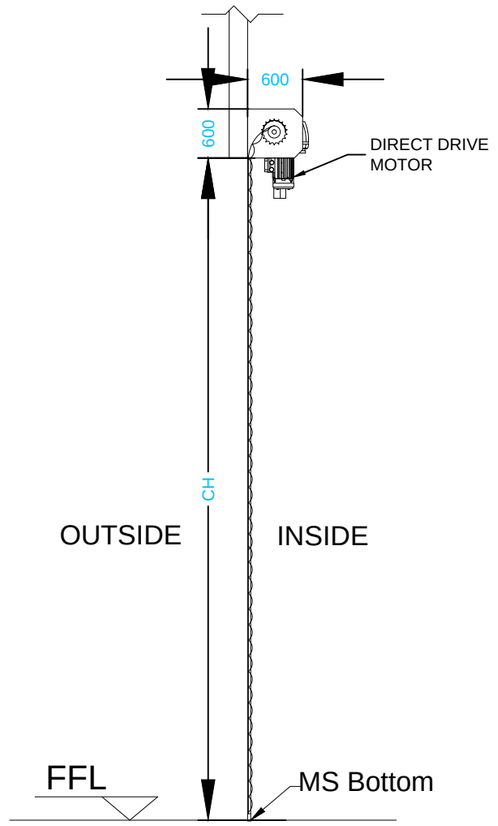


Section A-A

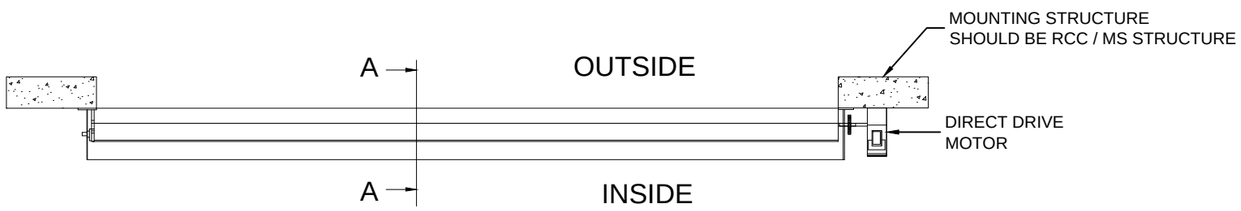

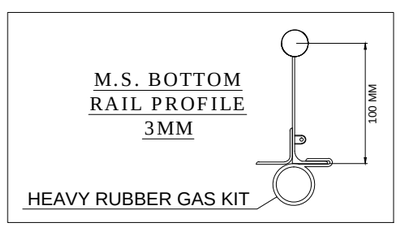

Main Slats
Double Wall Rolling Shutter

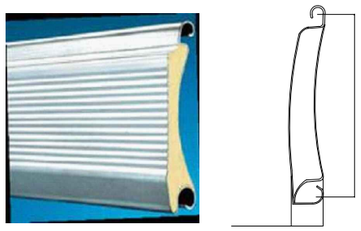

COLOR OF SLATS & SHUTTER -RAL9002 (GRAY WHITE)

DIMENSION :

CLEAR WIDTH	CLEAR HEIGHT	QUANTITY
3600 mm	3800 mm	1 NOS

NOTE:-

1.STRUCTURE FOR SHUTTER WILL BE IN CLIENT'S SCOPE.
2. 3 PHASE SUPPLY SHOULD BE PROVIDED.

NIHVA TECHNOLOGIES PVT. LTD.
NIHVA TECHNOLOGIES PVT. LTD. PUNE
Email:- info@nihva.com
Website:- www.nihva.com

TITLE:

DOUBLE WALL ROLLING SHUTTER
03. LGF East side

CLIENT'S APPROVAL :

CLIENT - AJAY KALE AND ASSOSIATE

PROJECT -

SITE LOCATION - PIRANGUT

DWG. NO. : NIHVA/21-22/CLT/294

SCALE: NTS	WT:	SHEET:01 OF 02
DRAWN BY: G.P.		DATE: 23-12-2021
CHECKED BY: A.K.		DATE: 23-12-2021
APPROVED BY :		

If any queries contact : design@nihva.com


NOTE: ALL DIMENSIONS ARE IN mm


THIS DRAWING & DESIGN IS THE PROPERTY OF NIHVA TECHNOLOGIES, NOT TO BE SOLD OR COPIED TO ANY OTHER CONCERN.


PRODUCED BY AN AUTODESK EDUCATIONAL PRODUCT

PRODUCED BY AN AUTODESK EDUCATIONAL PRODUCT

PRODUCED BY AN AUTODESK EDUCATIONAL PRODUCT

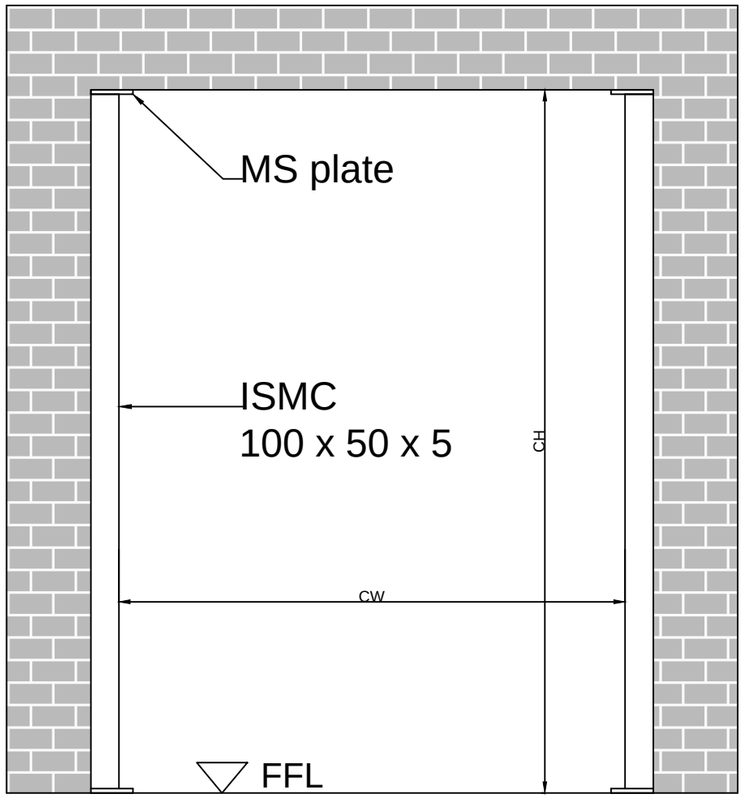

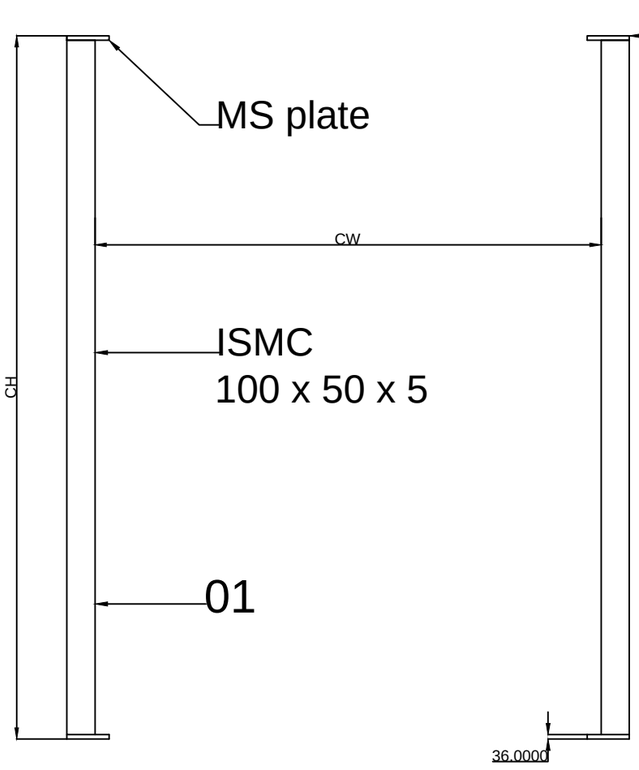

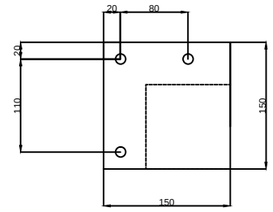

MS plate
Scale: 3:1

Door
Structure

CLEAR WIDTH	CLEAR HEIGHT	Qty
3600	3800	1 nos

This drawing & design is the property of NIHVA TECHNOLOGIES. Not to be sold or copied to any other concern.

TITLE	STRUCTURE			NIHVA TECHNOLOGIES PVT. LTD.	NIHVA TECHNOLOGIES PVT. LTD. PUNE Tel : 020 66304033 Email:- info@nihva.com Website:- www.nihva.com
	NAME	SIGN	DATE		
DRAWN	G.P.		23.12.21	CLIENT :- AJAY KALE AND ASSOSIATE	
CHECK	A.K.		23.12.21	PROJECT :-	
APPV'ED	V.T		23.12.21	LOCATION :-	
If any queries contact : design@nihva.com				DWG. NO. :- NIHVA/21-22/CLT/294	REV :- R00
ALL DIMENSION ARE IN mm				SCALE: NTS	WT: / SHEET: 02 OF 02

PRODUCED BY AN AUTODESK EDUCATIONAL PRODUCT