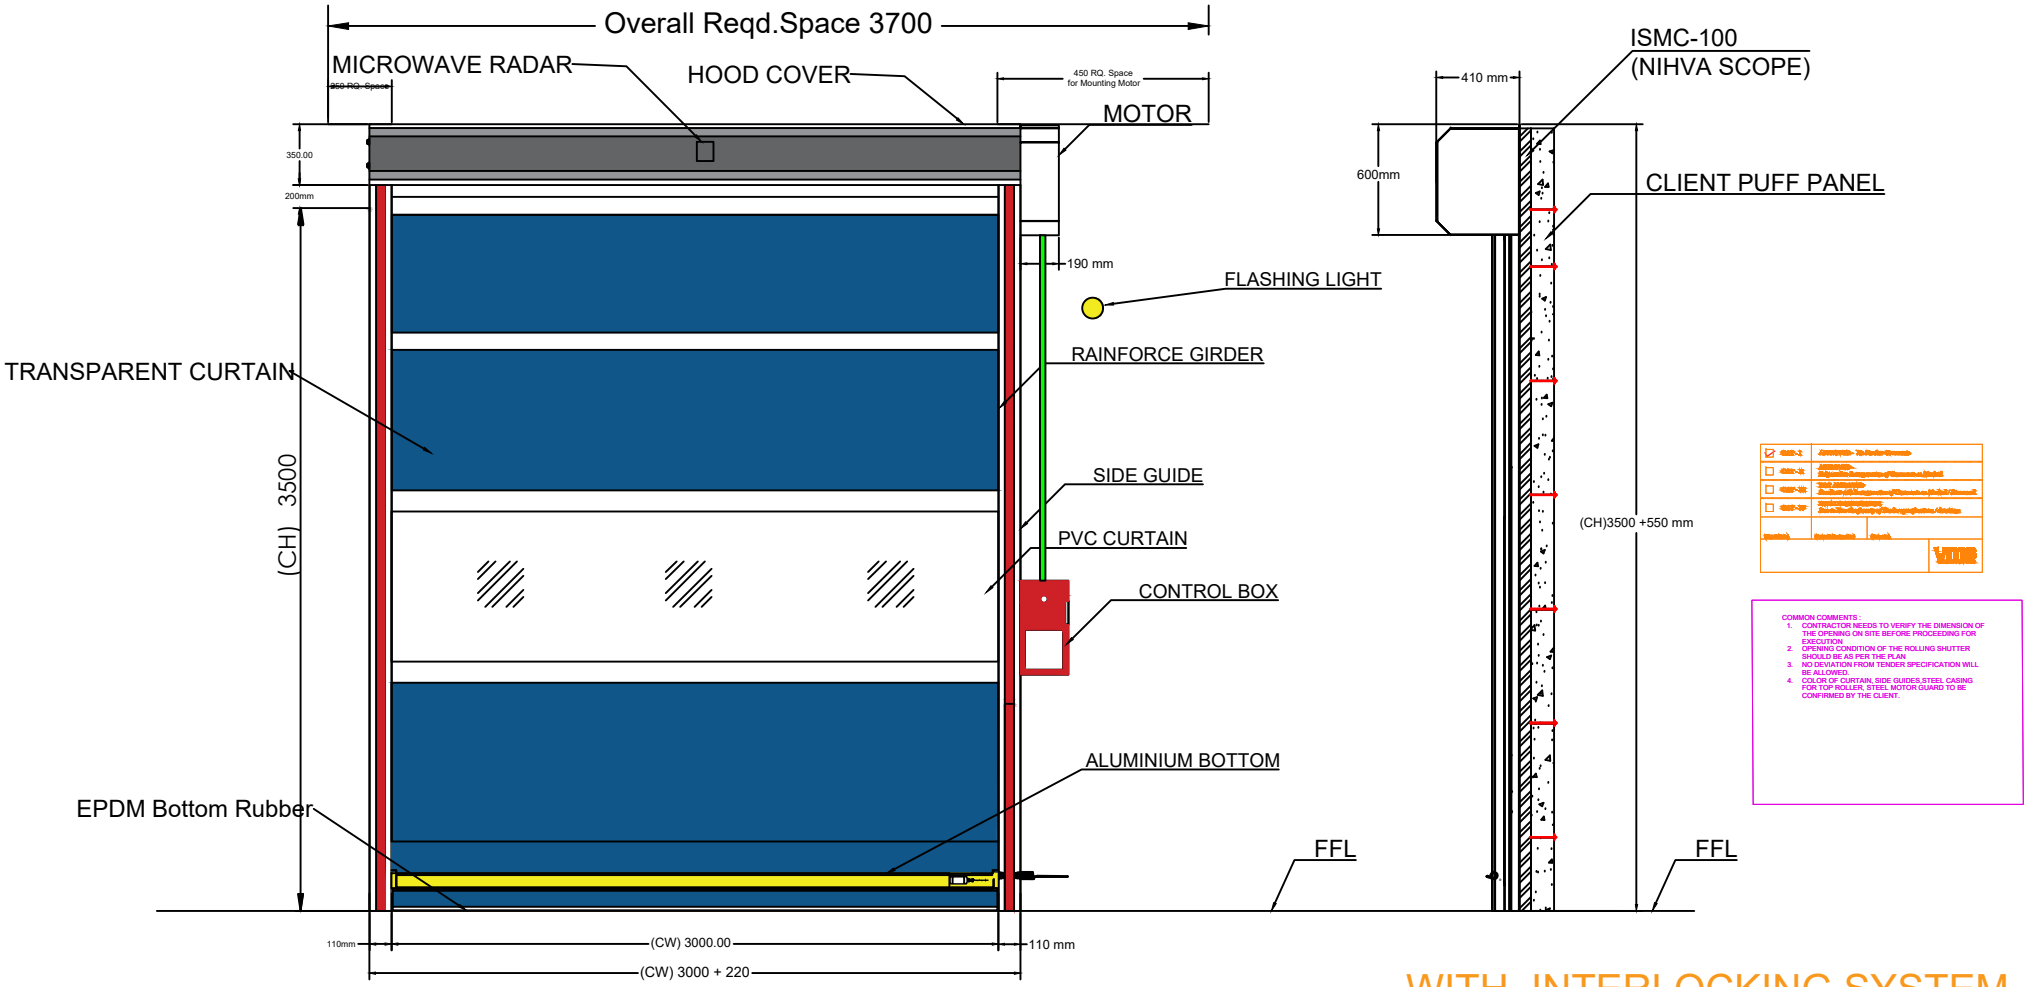


COMMON COMMENTS :
1. CONTRACTOR NEEDS TO VERIFY THE DIMENSION OF THE OPENING ON SITE BEFORE PROCEEDING FOR EXECUTION.
2. OPENING CONDITION OF THE ROLLING SHUTTER SHOULD BE AS PER THE PLAN.
3. NO DEVIATION FROM TENDER SPECIFICATION WILL BE ALLOWED.
4. COLOR OF CURTAIN, SIDE GUIDES,STEEL CASING FOR TOP ROLLER, STEEL MOTOR GUARD TO BE CONFIRMED BY THE CLIENT.

WITH INTERLOCKING SYSTEM

TECHNICAL SPECIFICATION :

SR.	SPECIFICATIONS	DETAILS
1	Control Panel	LED Display Servo Controller : - Operating Speed (Adjustable) : 1.4~2.5 min/ Working Temperature : -35 degree to 65 degree - Water Resistant : IP65 Make IDER, manufactured under European Standards
2	Drive	IDER Make ,CE Certified
3	Motor Power ,Torque	Power : 1.1 kW Torque : 65 Nm
4	Door Travel Speed	Opening: 2 m/Sec & Closing:0.9m/Sec
5	Safety Device	Safety Photocell Pair & Safety Edges
6	Surface Finish	As Per Client Requirement
7	Accessories	Radar Sensor ,Magnetic Loop Detector ,Flashing Light Buzzer

NOTE:

All Cables & Ele.Conduits to be provided by NIHVA
(1) All Civil Work in Client Scope
(2) Required M.S.Structure & Fittings at NIHVA Scope

Sr	Clear Width (CW)	Clear Height (CH)	QTY
1	3000	3500	2

This drawing & design is the property of NIHVA TECHNOLOGIES. Not to be sold or copied to any other concern.

TITLE HIGH SPEED DOOR WITH SENSOR GA DRAWING


	NAME	SIGN	DATE
DRAWN	S.J		18.01.2024
CHECK	A.K		18.01.2024
APPRD.	V.T		18.01.2024


If any queries contact : projectsupport@nihva.com


ALL DIMENSION ARE IN mm


NIHVA TECHNOLOGIES PVT. LTD.
NIHVA TECHNOLOGIES PVT. LTD. PUNE
Tel : 020 66304033
Email:- info@nihva.com
Website:- www.nihva.com

CLIENT - RINAC
PROJECT - HIGH SPEED DOOR
FORMAT NO - NIHVA-DD-F-03
DWG. NO. : NIHVA/23-24/00XX
REV- R00
SCALE: NTS
WT:
SHEET:

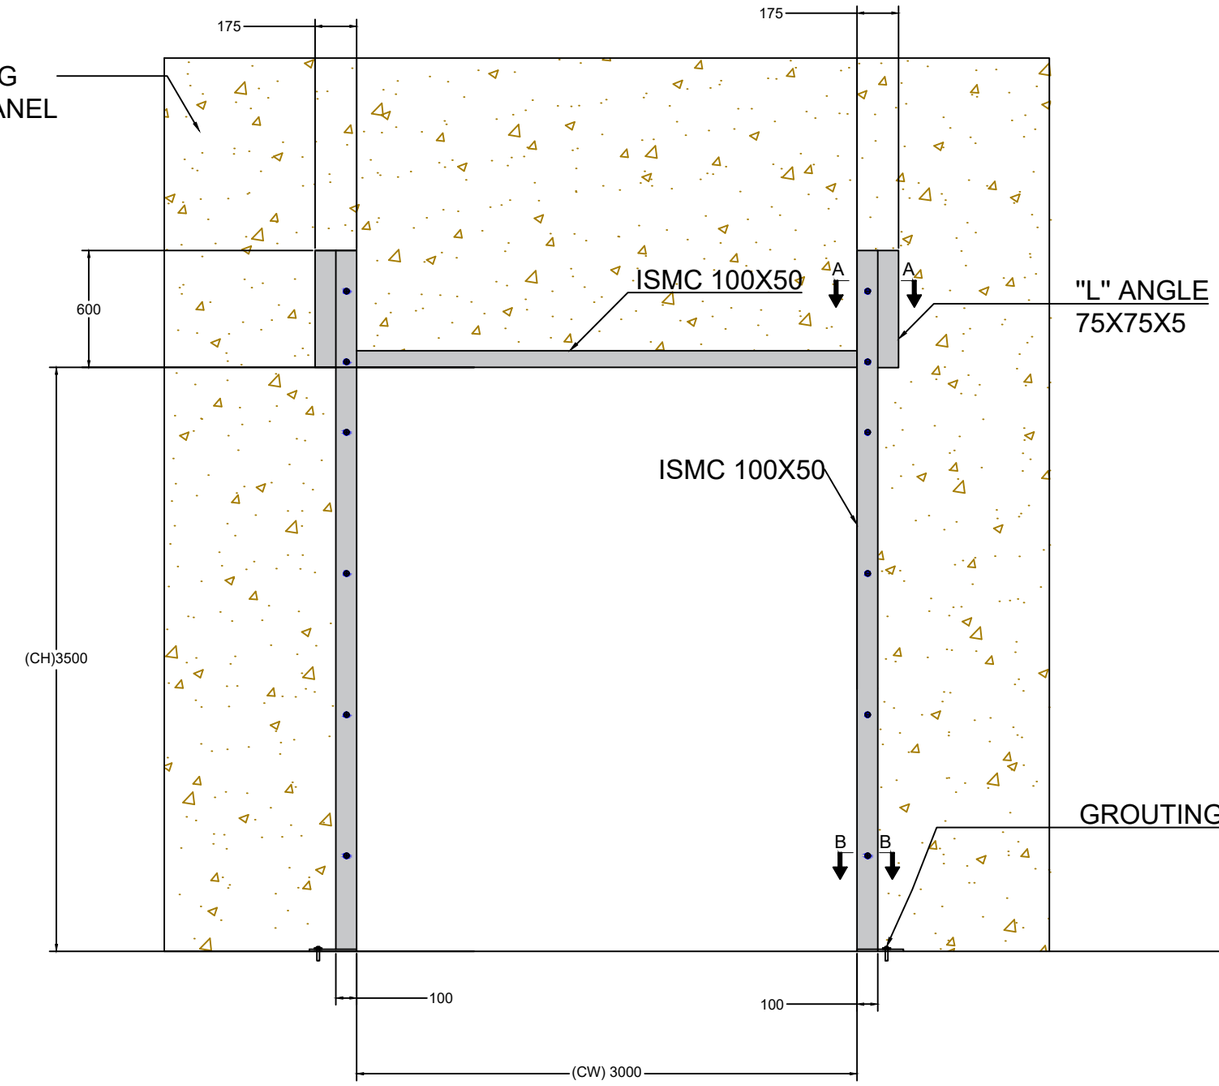

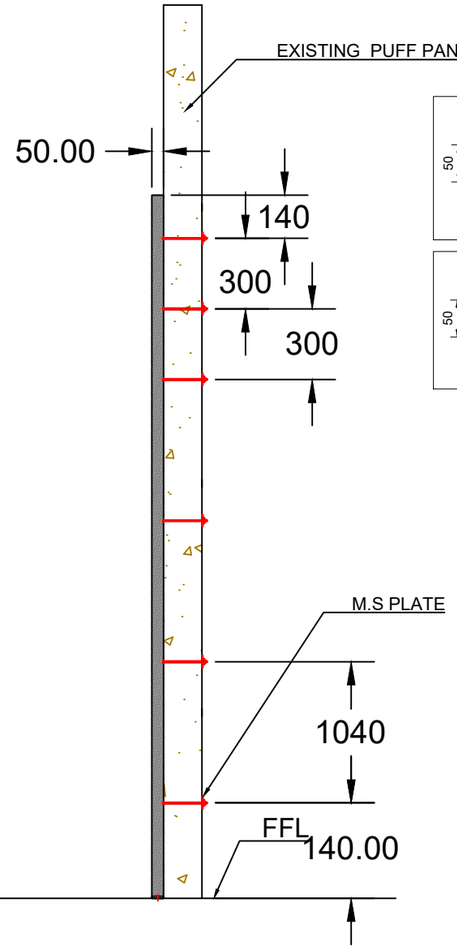

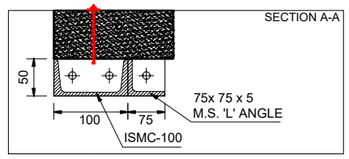

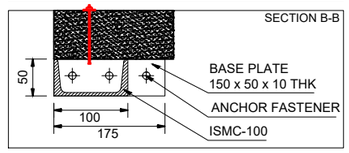


M.S. STRUCTURE DETAILS

Sr	Description	Clear Width (CW)	Clear Height (CH)	QTY
1	HSD With Sensor	**3000**	**3500**	2

This drawing & design is the property of NIHVA TECHNOLOGIES. Not to be sold or copied to any other concern.

TITLE	HIGH SPEED DOOR STRUCTURE DRAWING			NIHVA TECHNOLOGIES PVT. LTD. PUNE Tel : 020 66304033 Email:- info@nihva.com Website:- www.nihva.com
	NAME	SIGN	DATE	
DRAWN	S.J		18.01.2024	CLIENT - RINAC
CHECK	A.K		18.01.2024	PROJECT - HIGH SPEED DOOR ST.
APPRD.	V.T		18.01.2024	FORMAT NO - NIHVA-DD-F-03
If any queries contact : projectsupport@nihva.com				DWG. NO. : NIHVA/23-24/00XX / REV- R00
ALL DIMENSION ARE IN mm				SCALE: NTS / WT: / SHEET:

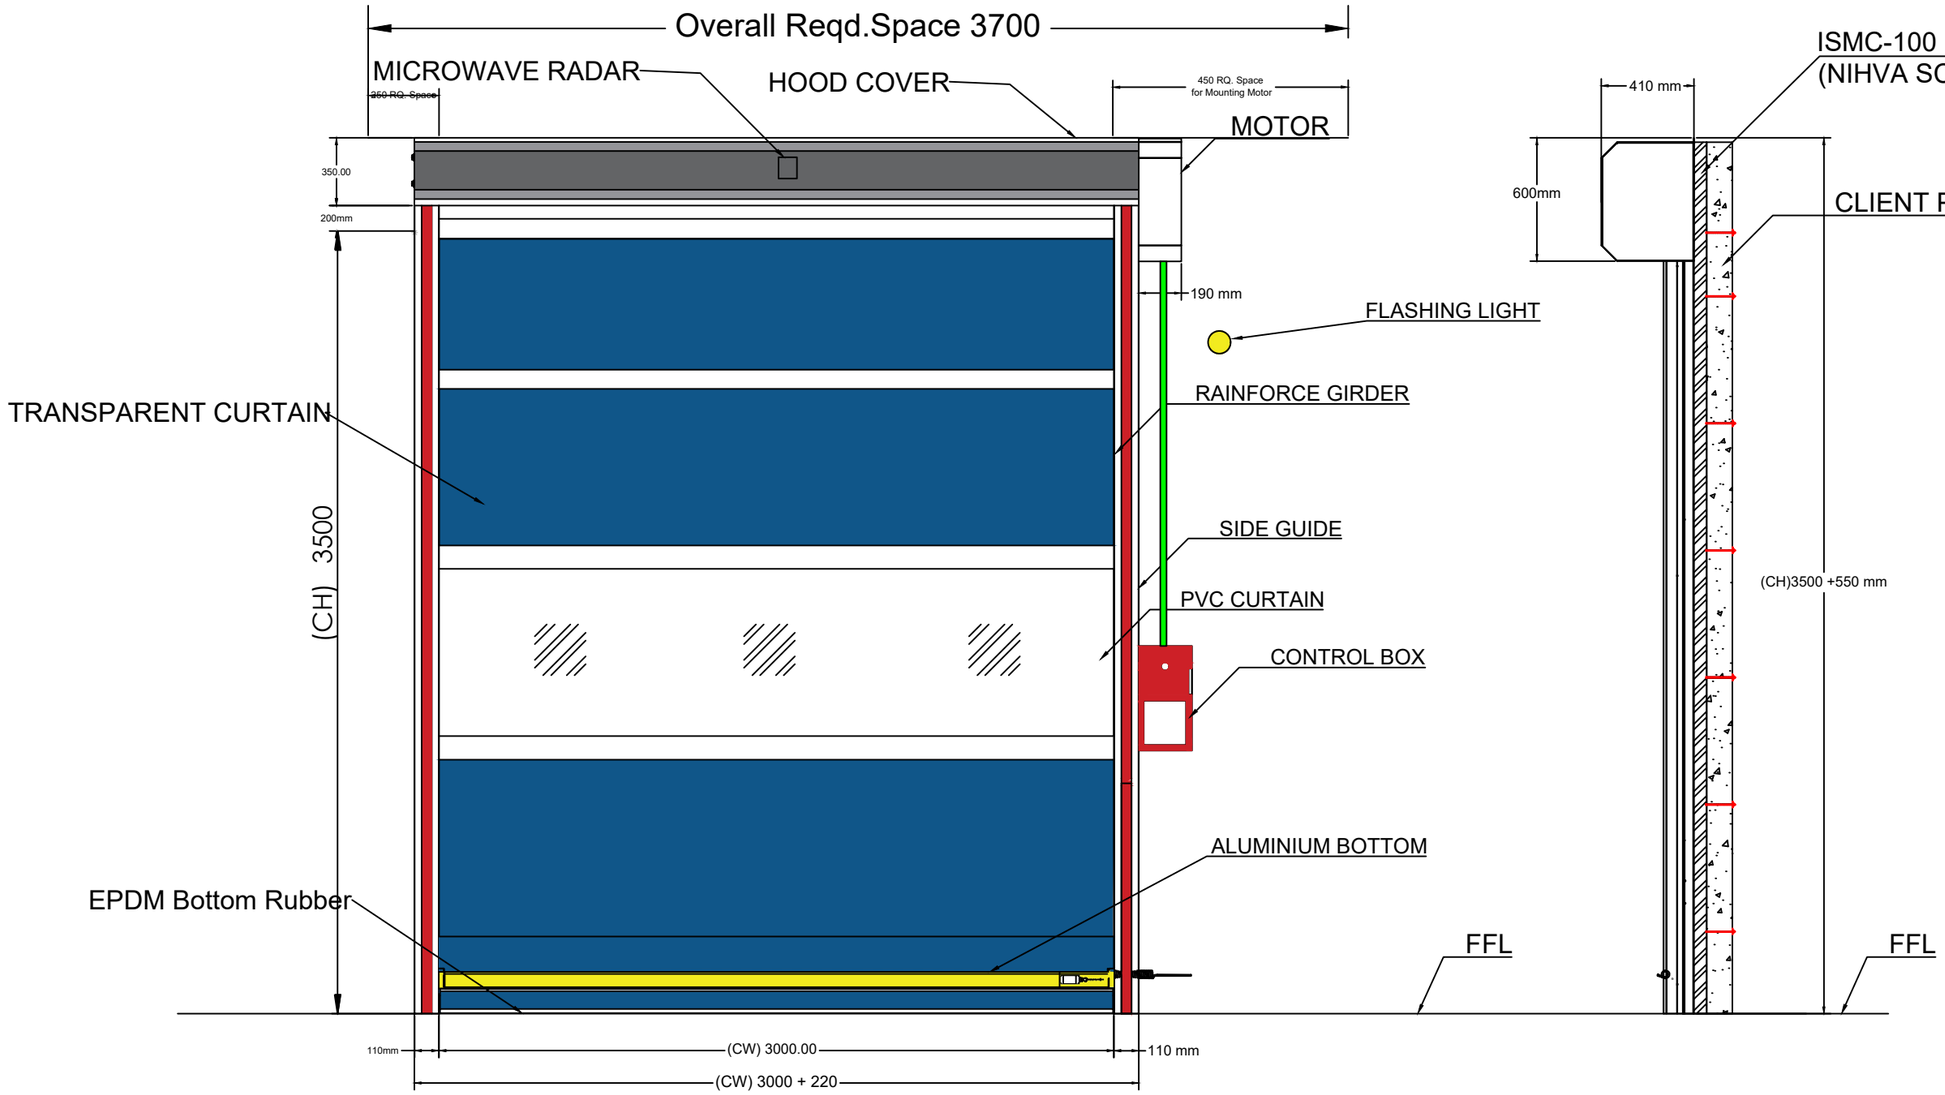

TECHNICAL SPECIFICATION :

SR.	SPECIFICATIONS	DETAILS
1	Control Panel	LED Display Servo Controller : - Operating Speed (Adjustable) : 1.4~2.5 min/ Working Temperature : -35 degree to 65 degree - Water Resistant : IP65 Make IDER, manufactured under European Standards
2	Drive	IDER Make ,CE Certified
3	Motor Power ,Torque	Power : 1.1 kW Torque : 65 Nm
4	Door Travel Speed	Opening: 2 m/Sec & Closing:0.9m/Sec
5	Safety Device	Safety Photocell Pair & Safety Edges
6	Surface Finish	As Per Client Requirement
7	Accessories	Radar Sensor ,Magnetic Loop Detector ,Flashing Light Buzzer

NOTE:

All Cables & Ele.Conduits to be provided by NIHVA
(1) All Civil Work in Client Scope
(2) Required M.S.Structure & Fittings at NIHVA Scope

Sr	Clear Width (CW)	Clear Height (CH)	QTY
1	3000	3500	1

COMMON COMMENTS :
1. CONTRACTOR NEEDS TO VERIFY THE DIMENSION OF THE OPENING ON SITE BEFORE PROCEEDING FOR EXECUTION.
2. OPENING CONDITION OF THE ROLLING SHUTTER SHOULD BE AS PER THE PLAN
3. NO DEVIATION FROM TENDER SPECIFICATION WILL BE ALLOWED.
4. COLOR OF CURTAIN, SIDE GUIDES,STEEL CASING FOR TOP ROLLER, STEEL MOTOR GUARD TO BE CONFIRMED BY THE CLIENT.

This drawing & design is the property of NIHVA TECHNOLOGIES. Not to be sold or copied to any other concern.

TITLE: HIGH SPEED DOOR WITH SENSOR GA DRAWING


	NAME	SIGN	DATE
DRAWN	S.J		18.01.2024
CHECK	A.K		18.01.2024
APPRD.	V.T		18.01.2024


If any queries contact : projectsupport@nihva.com


ALL DIMENSION ARE IN mm


NIHVA TECHNOLOGIES PVT. LTD.
NIHVA TECHNOLOGIES PVT. PUNE
Tel : 020 66304033
Email:- info@nihva.com
Website:- www.nihva.com

CLIENT - RINAC
PROJECT - HIGH SPEED DOOR
FORMAT NO - NIHVA-DD-F-03
DWG. NO. : NIHVA/23-24/00XX
REV- R00
SCALE: NTS
WT:
SHEET:

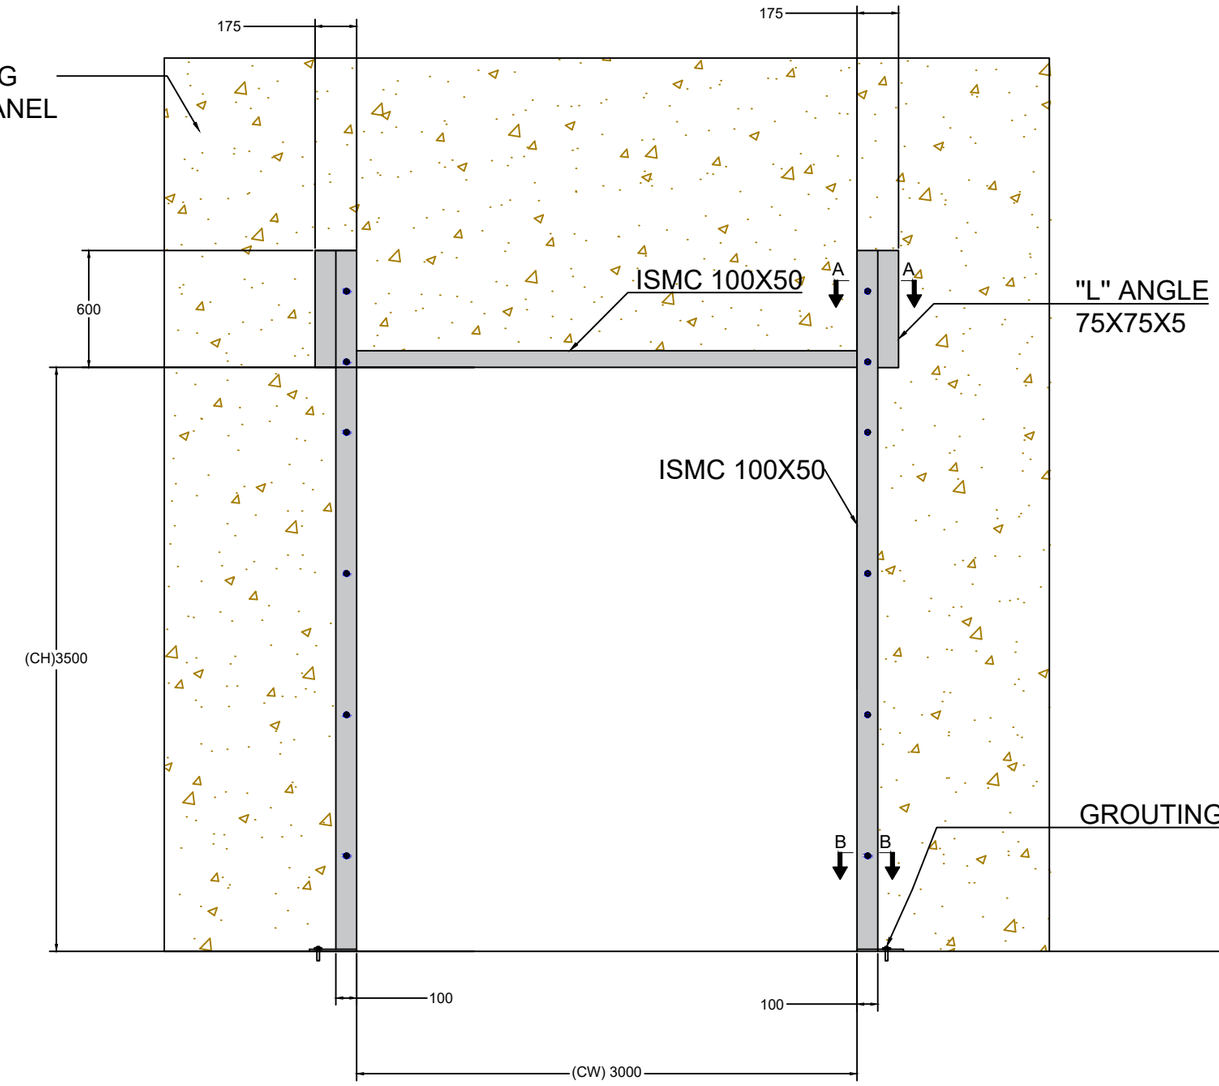

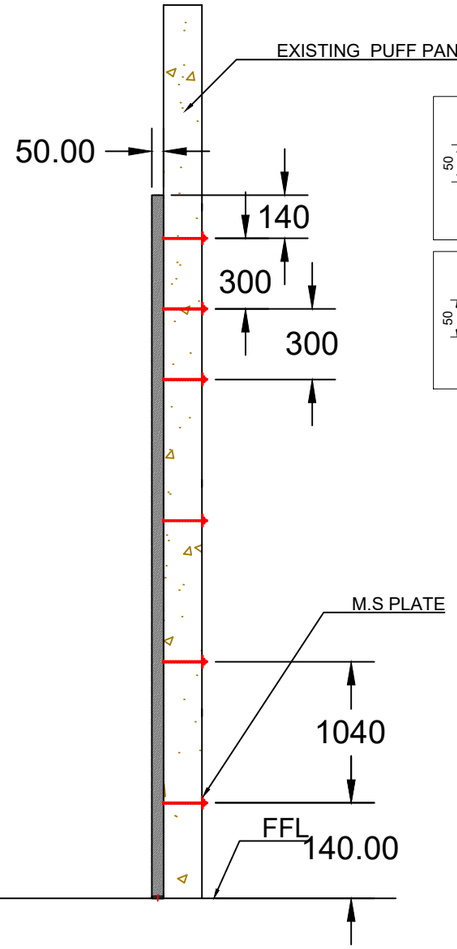

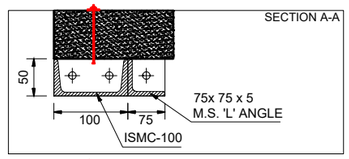

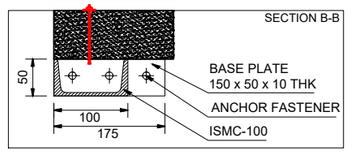

M.S. STRUCTURE DETAILS

Sr	Description	Clear Width (CW)	Clear Height (CH)	QTY
1	HSD With Sensor	**3000**	**3500**	1

This drawing & design is the property of NIHVA TECHNOLOGIES. Not to be sold or copied to any other concern.

TITLE HIGH SPEED DOOR STRUCTURE DRAWING

NIHVA TECHNOLOGIES PVT. LTD.

NIHVA TECHNOLOGIES PVT. LTD. PUNE
Tel : 020 66304033
Email:- info@nihva.com
Website:- www.nihva.com

	NAME	SIGN	DATE
DRAWN	S.J		18.01.2024
CHECK	A.K		18.01.2024
APPRD.	V.T		18.01.2024

CLIENT - RINAC

PROJECT - HIGH SPEED DOOR ST.

FORMAT NO - NIHVA-DD-F-03

If any queries contact : projectsupport@nihva.com

DWG. NO. : NIHVA/23-24/00XX


REV- R00

ALL DIMENSION ARE IN mm

SCALE: NTS

WT:

SHEET:

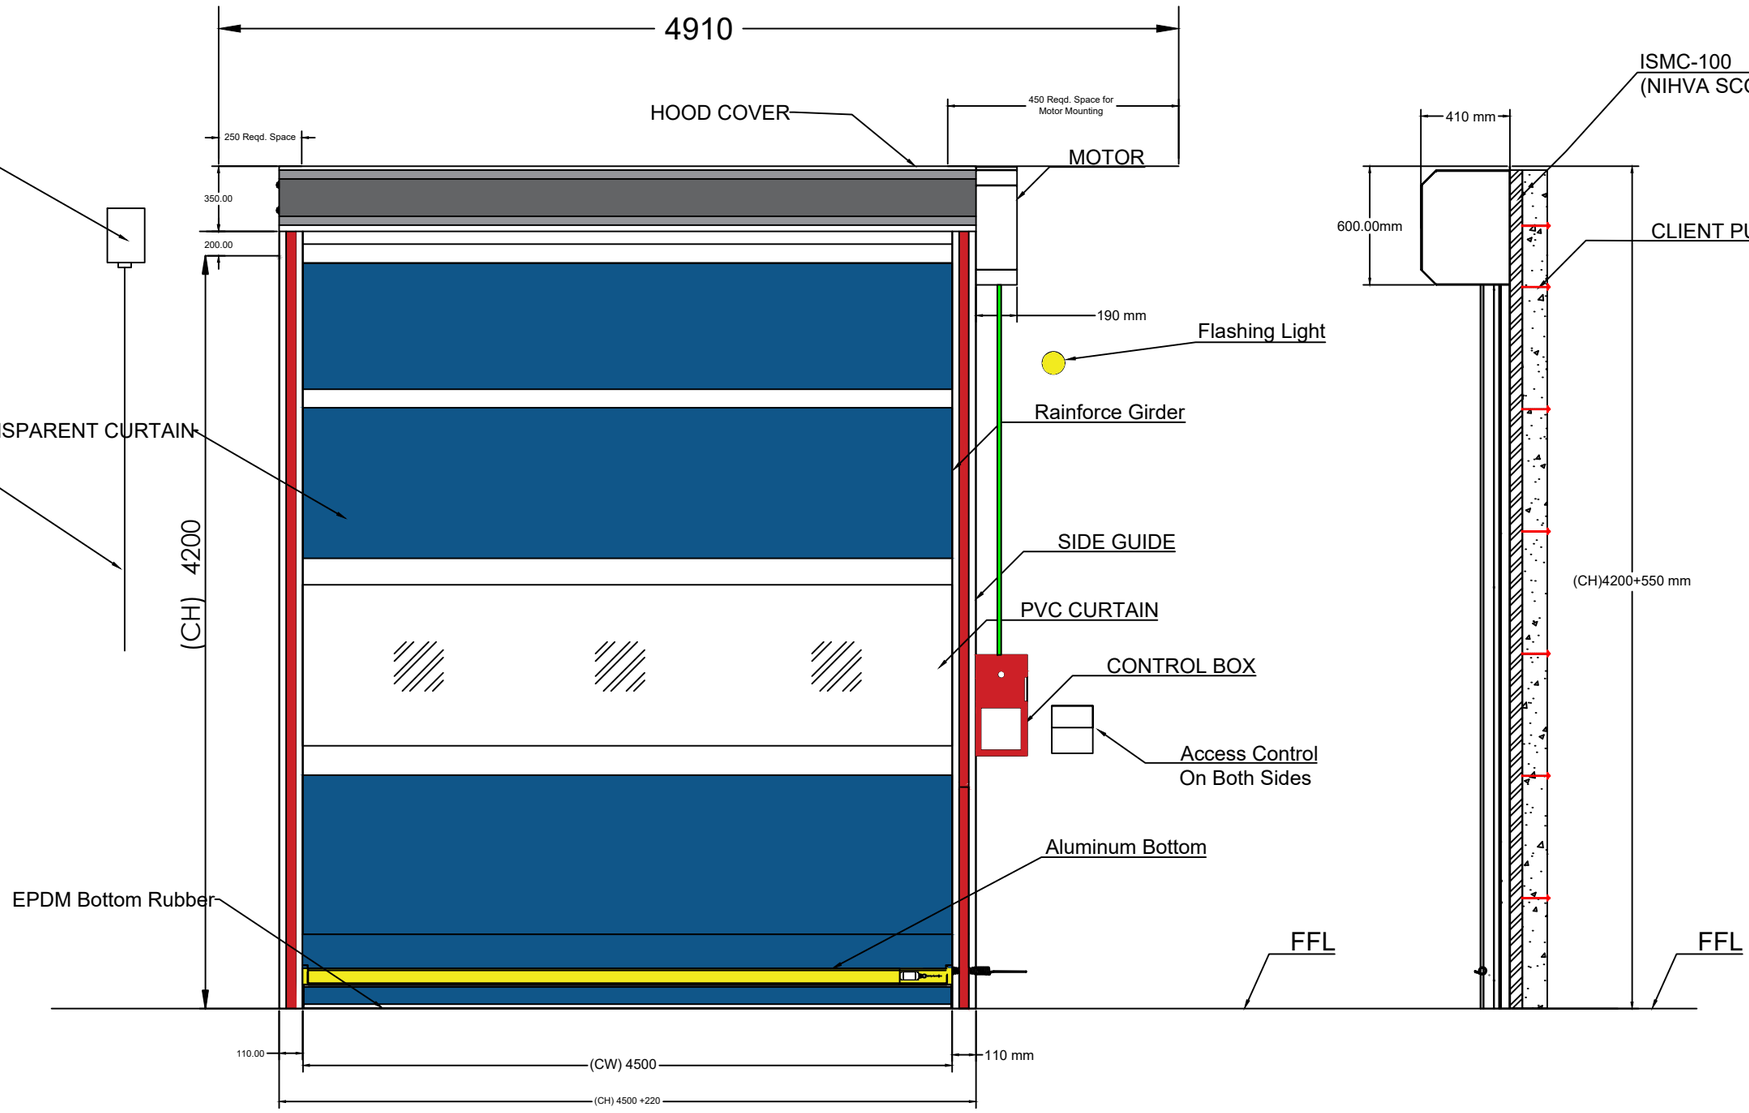

COMMON COMMENTS :

1. CONTRACTOR NEEDS TO VERIFY THE DIMENSION OF THE OPENING ON SITE BEFORE PROCEEDING FOR EXECUTION
2. OPENING CONDITION OF THE ROLLING SHUTTER SHOULD BE AS PER THE PLAN
3. NO DEVIATION FROM TENDER SPECIFICATION WILL BE ALLOWED.
4. COLOR OF CURTAIN, SIDE GUIDES,STEEL CASING FOR TOP ROLLER, STEEL MOTOR GUARD TO BE CONFIRMED BY THE CLIENT.

TECHNICAL SPECIFICATION :

SR.	SPECIFICATIONS	DETAILS
1	Control Panel	LED Display Servo Controller : - Operating Speed (Adjustable) : 1.4~2.5 min/ Working Temperature : -35 degree to 65 degree - Water Resistant : IP65 Make IDER, manufactured under European Standards
2	Drive	IDER Make ,CE Certified
3	Motor Power ,Torque	Power : 1.1 kW Torque : 65 Nm
4	Door Travel Speed	Opening: 2 m/Sec & Closing:0.9m/Sec
5	Safety Device	Safety Photocell Pair & Safety Edges
6	Surface Finish	As Per Client Requirement
7	Accessories	Flashing Light with Buzzer , Pull Chord

NOTE:

(1) All Cables & Ele.Conduits to be provided by NIHVA
(2) All Civil Work in Client Scope
(3) Required M.S.Structure & Fittings at NIHVA Scope

Sr	Clear Width (CW)	Clear Height (CH)	QTY
1	4500	4200	1

This drawing & design is the property of NIHVA TECHNOLOGIES. Not to be sold or copied to any other concern.

TITLE HIGH SPEED DOOR WITH ACCESS CONTROL GA DRAWING

	NAME	SIGN	DATE
DRAWN	S.J		19.01.2024
CHECK	A.K		19.01.2024
APPRD.	V.T		19.01.2024

If any queries contact : projectsupport@nihva.com

ALL DIMENSION ARE IN mm

NIHVA TECHNOLOGIES PVT. LTD.
NIHVA TECHNOLOGIES PVT. LTD. PUNE
Tel : 020 66304033
Email:- info@nihva.com
Website:- www.nihva.com


CLIENT - RINAC


PROJECT - HIGH SPEED DOOR

FORMAT NO - NIHVA-DD-F-03

DWG. NO. : NIHVA/23-24/00XX | REV- R00

SCALE: NTS | WT: | SHEET:

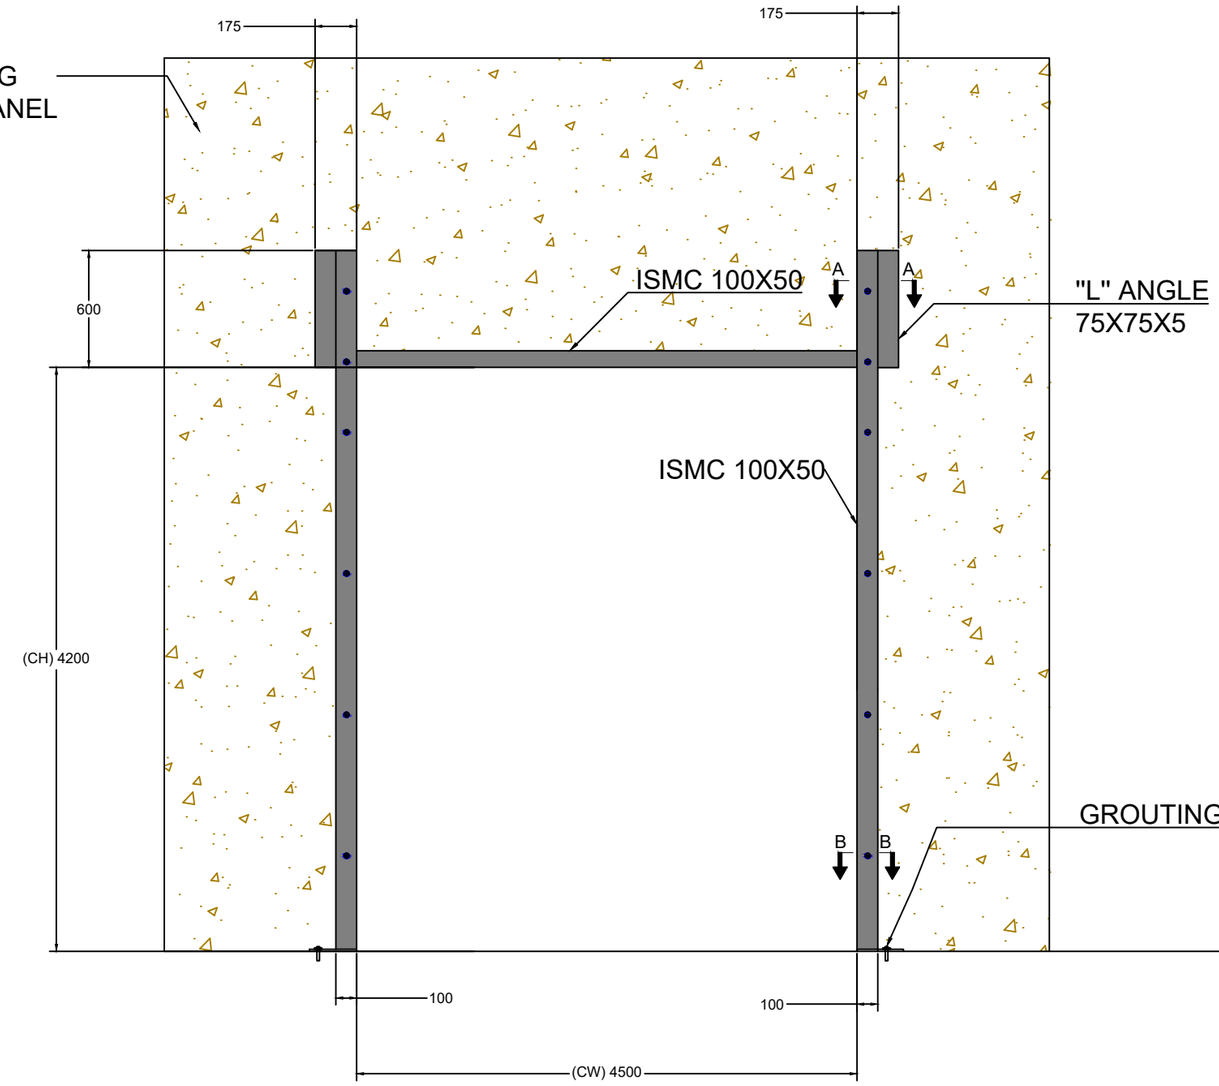

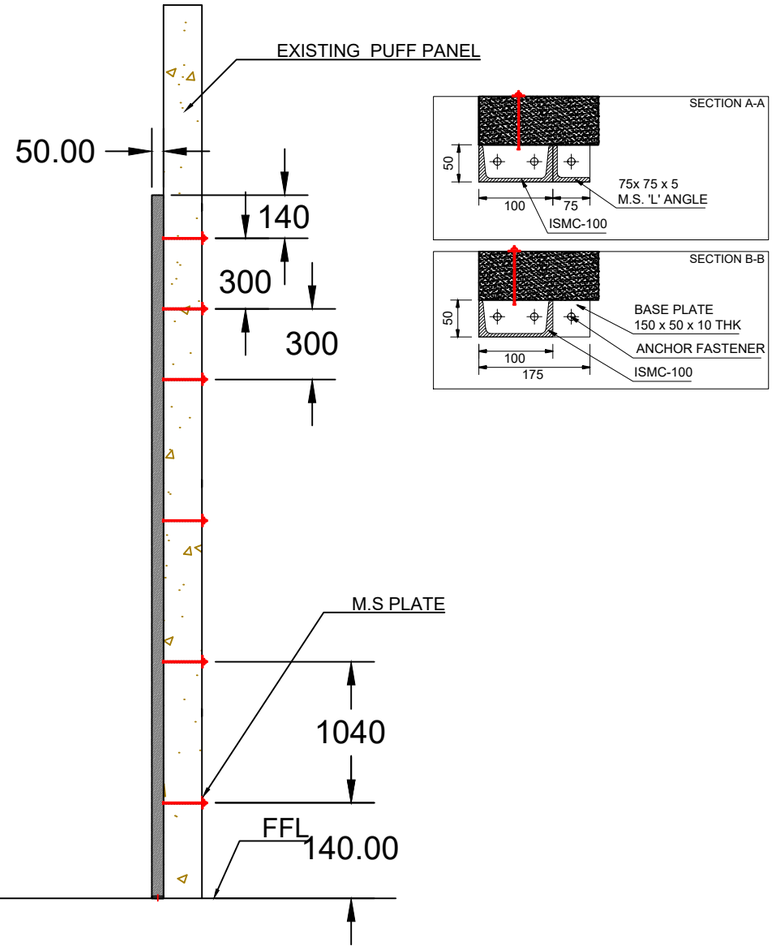


M.S. STRUCTURE DETAILS

Sr	Description	Clear Width (CW)	Clear Height (CH)	QTY
1	HSD Without Sensor With Access Control	**4500**	**4200**	1

This drawing & design is the property of NIHVA TECHNOLOGIES. Not to be sold or copied to any other concern.

TITLE	HIGH SPEED DOOR STRUCTURE DRAWING			NIHVA TECHNOLOGIES PVT. LTD. PUNE Tel : 020 66304033 Email:- info@nihva.com Website:- www.nihva.com	
	NAME	SIGN	DATE	CLIENT - RINAC	
DRAWN	S.J		18.01.2024		
CHECK	A.K		18.01.2024	PROJECT - HIGH SPEED DOOR ST.	
APPRD.	V.T		18.01.2024	FORMAT NO - NIHVA-DD-F-03	
If any queries contact : projectsupport@nihva.com				DWG. NO. : NIHVA/23-24/00XX	REV- R00
ALL DIMENSION ARE IN mm				SCALE: NTS	WT: SHEET:

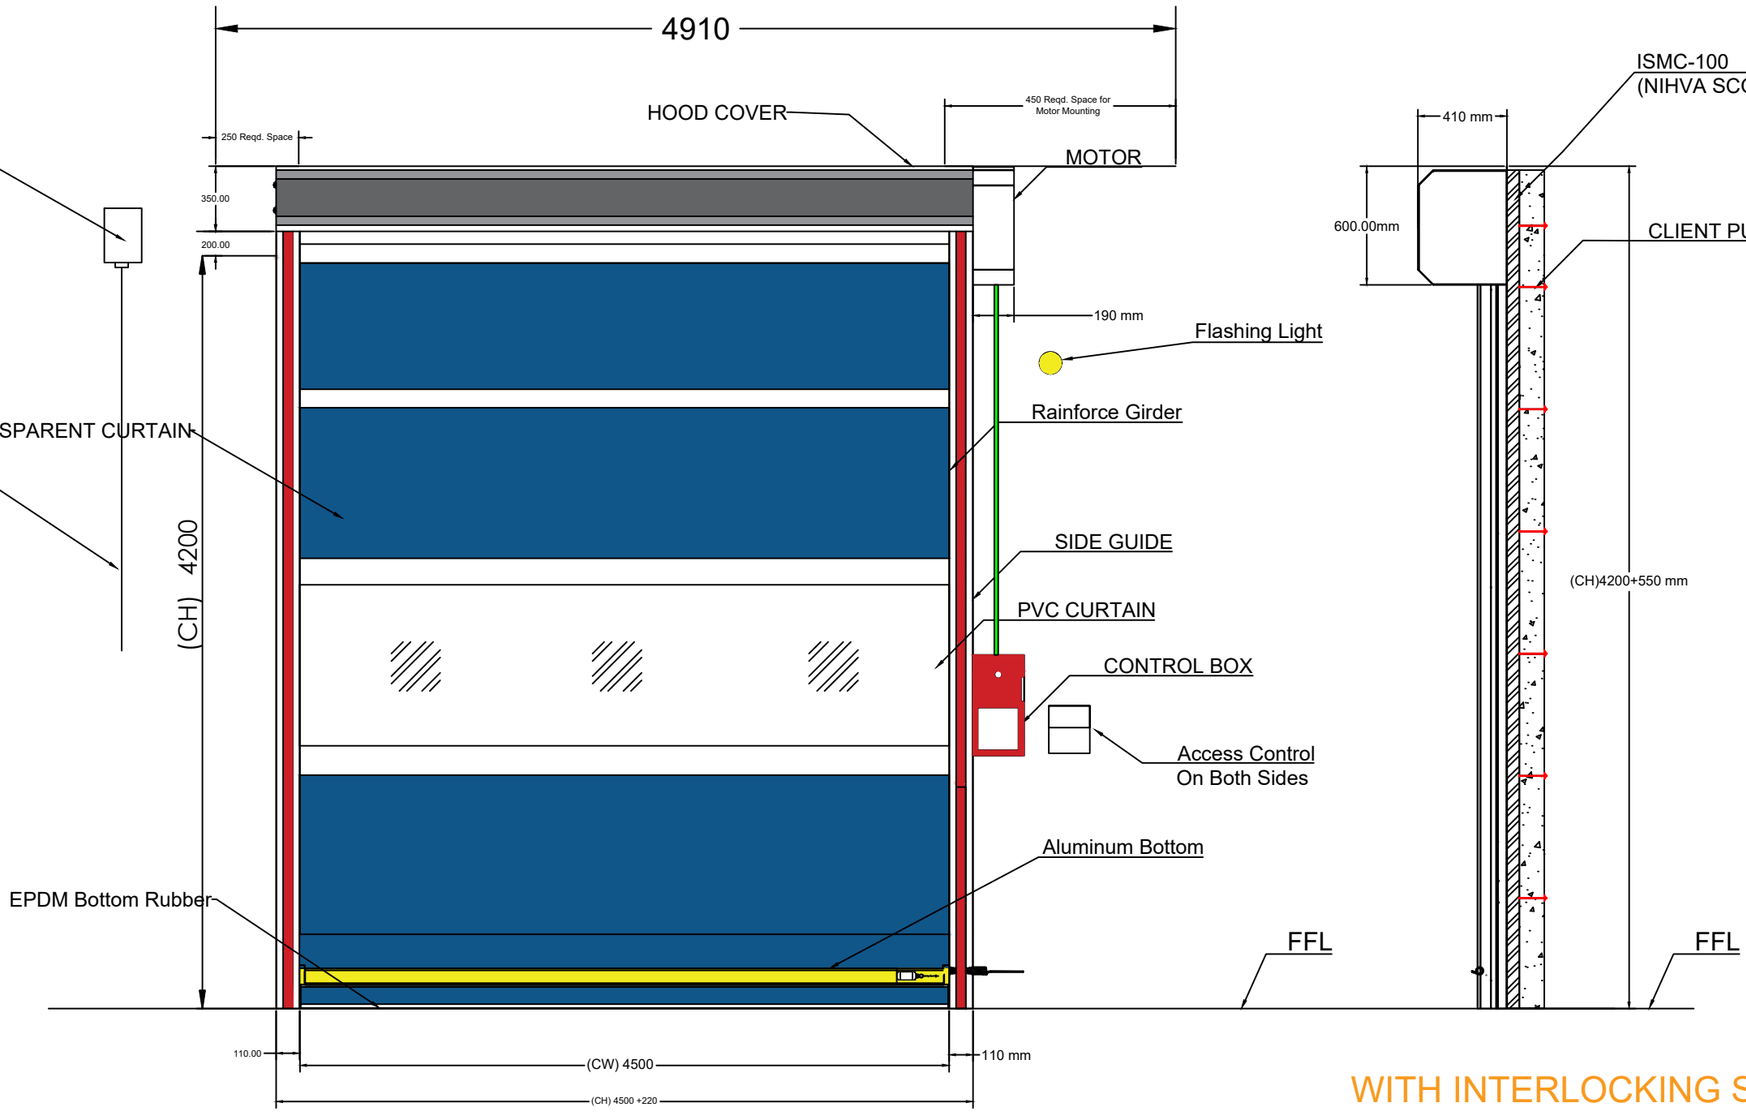

COMMON COMMENTS :

1. CONTRACTOR NEEDS TO VERIFY THE DIMENSION OF THE OPENING ON SITE BEFORE PROCEEDING FOR EXECUTION
2. OPENING CONDITION OF THE ROLLING SHUTTER SHOULD BE AS PER THE PLAN
3. NO DEVIATION FROM TENDER SPECIFICATION WILL BE ALLOWED.
4. COLOR OF CURTAIN, SIDE GUIDES,STEEL CASING FOR TOP ROLLER, STEEL MOTOR GUARD TO BE CONFIRMED BY THE CLIENT.

WITH INTERLOCKING SYSTEM

TECHNICAL SPECIFICATION :

SR.	SPECIFICATIONS	DETAILS
1	Control Panel	LED Display Servo Controller : - Operating Speed (Adjustable) : 1.4~2.5 min/ Working Temperature : -35 degree to 65 degree - Water Resistant : IP65 Make IDER, manufactured under European Standards
2	Drive	IDER Make ,CE Certified
3	Motor Power ,Torque	Power : 1.1 kW Torque : 65 Nm
4	Door Travel Speed	Opening: 2 m/Sec & Closing:0.9m/Sec
5	Safety Device	Safety Photocell Pair & Safety Edges
6	Surface Finish	As Per Client Requirement
7	Accessories	Flashing Light with Buzzer , Pull Chord

NOTE:

(1) All Cables & Ele.Conduits to be provided by NIHVA
(2) All Civil Work in Client Scope
(3) Required M.S.Structure & Fittings at NIHVA Scope

Sr	Clear Width (CW)	Clear Height (CH)	QTY
1	4500	4200	2

This drawing & design is the property of NIHVA TECHNOLOGIES. Not to be sold or copied to any other concern.

TITLE HIGH SPEED DOOR WITH ACCESS CONTROL GA DRAWING

	NAME	SIGN	DATE
DRAWN	S.J		19.01.2024
CHECK	A.K		19.01.2024
APPRD.	V.T		19.01.2024

If any queries contact : projectsupport@nihva.com

ALL DIMENSION ARE IN mm

NIHVA TECHNOLOGIES PVT. LTD.
NIHVA TECHNOLOGIES PVT. LTD. PUNE
Tel : 020 66304033
Email:- info@nihva.com
Website:- www.nihva.com


CLIENT - RINAC


PROJECT - HIGH SPEED DOOR

FORMAT NO - NIHVA-DD-F-03

DWG. NO. : NIHVA/23-24/00XX | REV- R00

SCALE: NTS | WT: | SHEET:

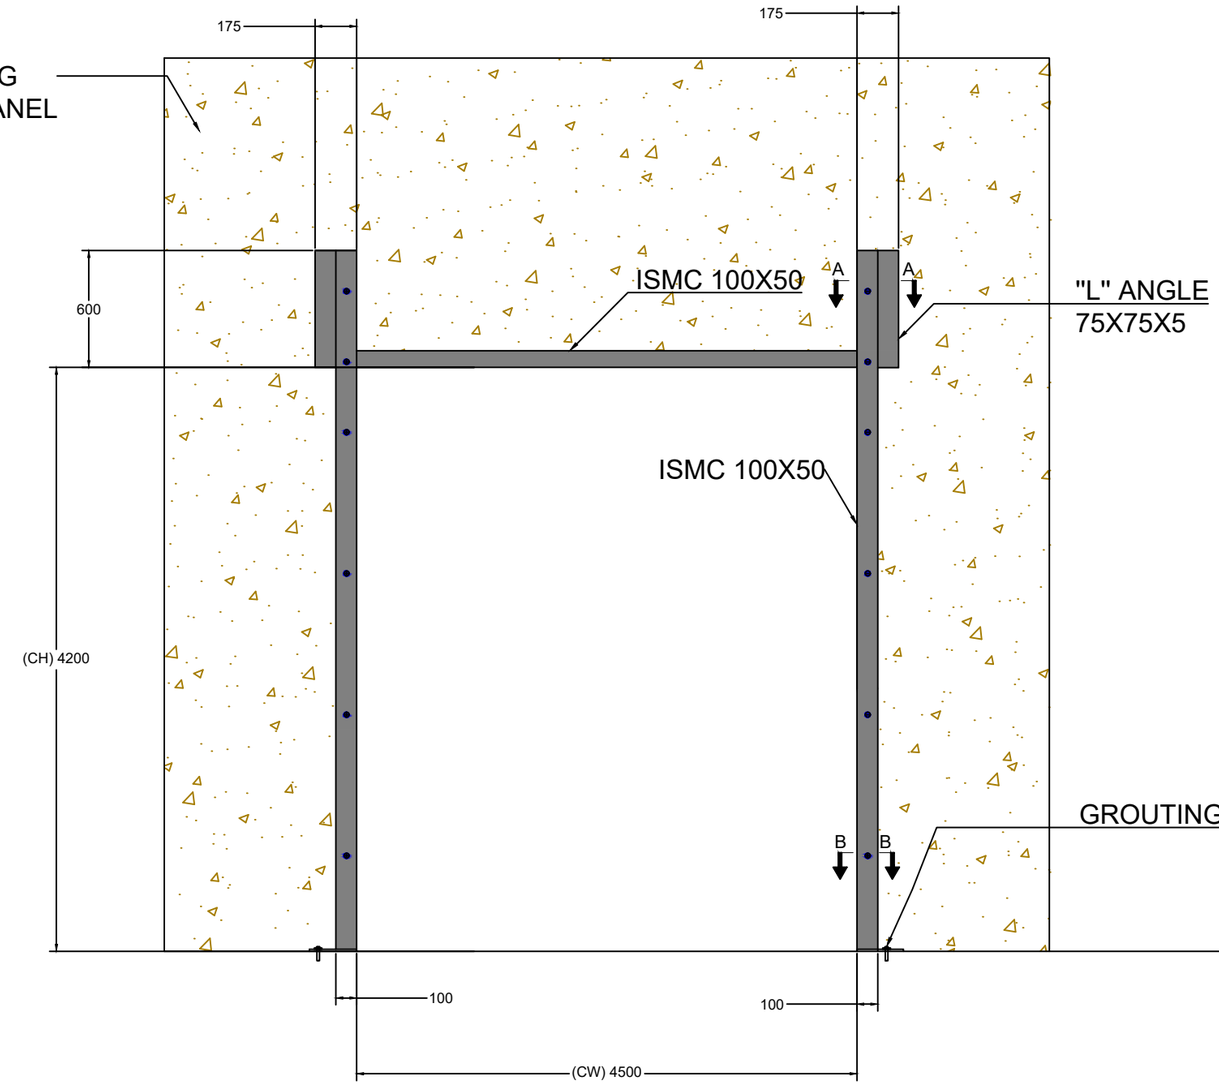

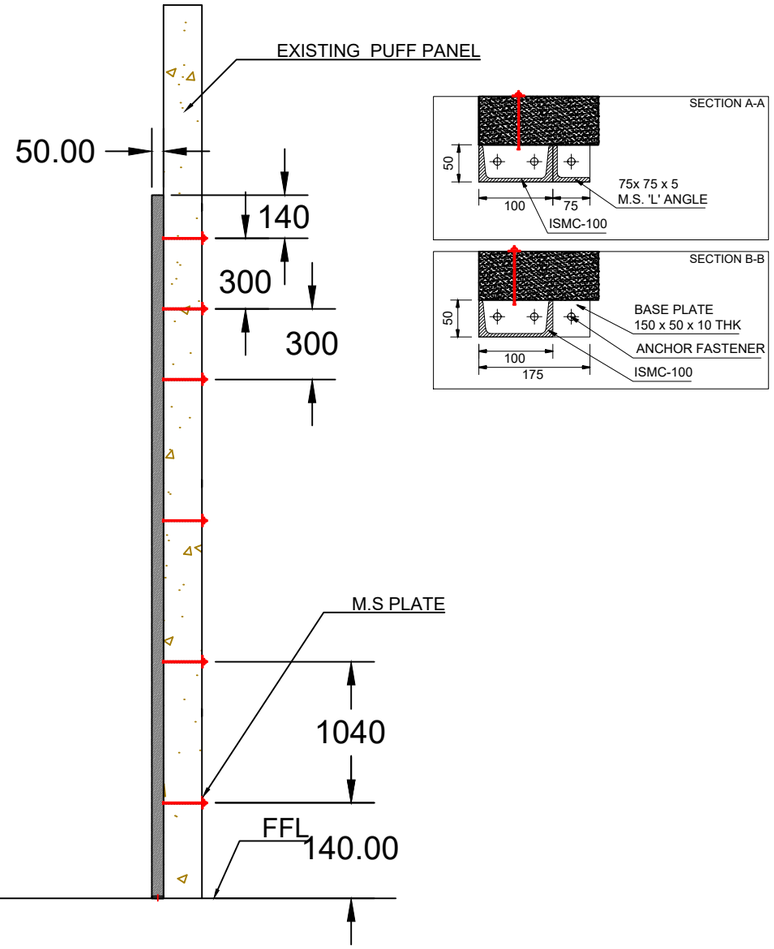

M.S. STRUCTURE DETAILS

Sr	Description	Clear Width (CW)	Clear Height (CH)	QTY
1	HSD Without Sensor With Access Control	**4500**	**4200**	2

This drawing & design is the property of NIHVA TECHNOLOGIES. Not to be sold or copied to any other concern.

TITLE	HIGH SPEED DOOR STRUCTURE DRAWING			NIHVA TECHNOLOGIES PVT. LTD. PUNE Tel : 020 66304033 Email:- info@nihva.com Website:- www.nihva.com
	NAME	SIGN	DATE	
DRAWN	S.J		18.01.2024	CLIENT - RINAC
CHECK	A.K		18.01.2024	PROJECT - HIGH SPEED DOOR ST.
APPRD.	V.T		18.01.2024	FORMAT NO - NIHVA-DD-F-03
If any queries contact : projectsupport@nihva.com				DWG. NO. : NIHVA/23-24/00XX / REV- R00
ALL DIMENSION ARE IN mm				SCALE: NTS / WT: / SHEET: