



PLAN
(SCALE 1:50)

*ACCESS CONTROL DOOR


D9 - 2500 x 2400 MM
- NEAR COLUMN C28

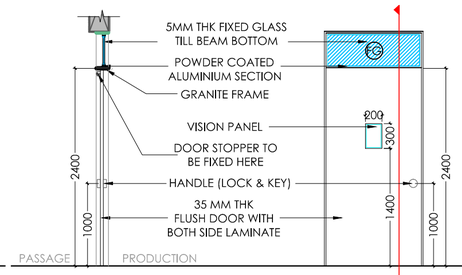


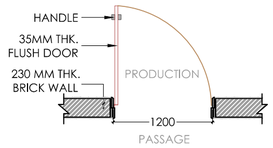

PLAN
(SCALE 1:50)

D1 - 1200 x 2400 MM
- NEAR COLUMN C30

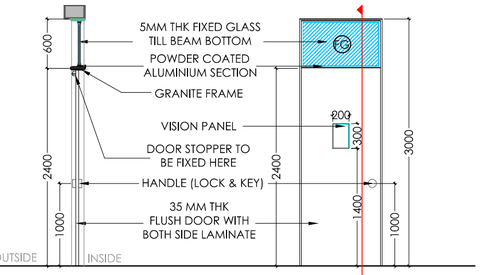


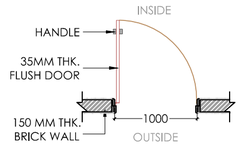


*HEIGHT OF FG NEED TO CHECK ON SITE BEFORE EXECUTION

PLAN
(SCALE 1:50)


D2 - 1000 x 3000 MM
- NEAR GENTS CHANGING ROOM & DISABLED TOILET

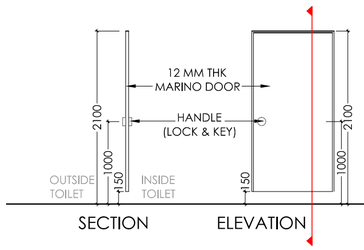

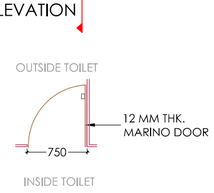

PLAN
(SCALE 1:50)

D3 - 750 x 2100 MM

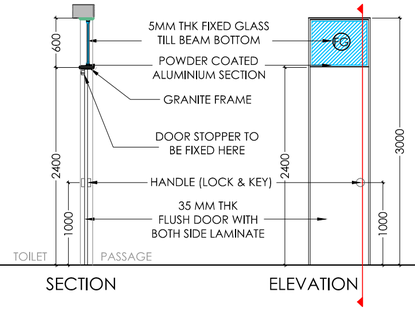





*HEIGHT OF FG NEED TO CHECK ON SITE BEFORE EXECUTION

PLAN
(SCALE 1:50)


D4 - 750 x 3075 MM
- AT JANITOR, VISITOR'S TOILET

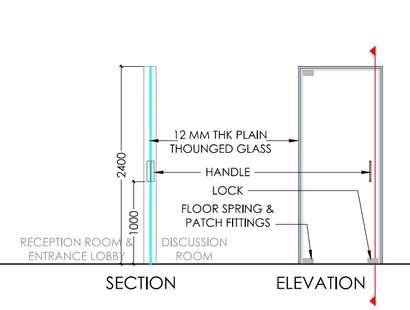


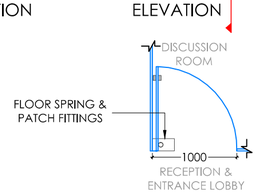

PLAN
(SCALE 1:50)


D5 - 1000 x 2400 MM AT
DISCUSSION ROOM

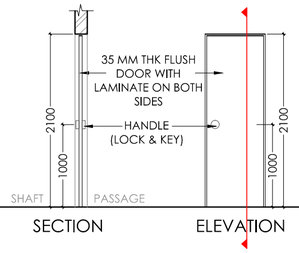


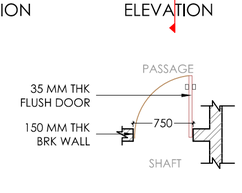

PLAN
(SCALE 1:50)


D6 - 750 x 2100 MM
AT LIFT SHAFT

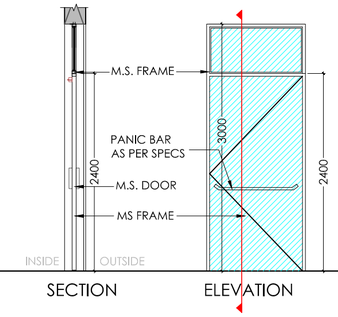


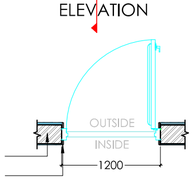

PLAN
(SCALE 1:50)

D7 - 1200 x 2400 MM
- AT PANEL ROOM

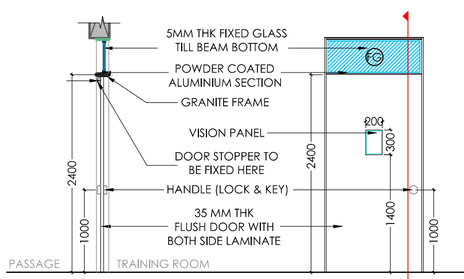


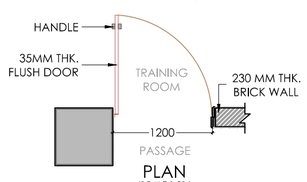


PLAN
(SCALE 1:50)

*ACCESS CONTROL DOOR


D8 - 1200 x 2400 MM
- AT TRAINING ROOM

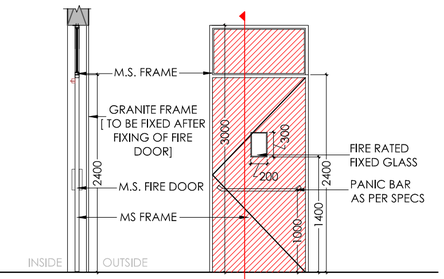


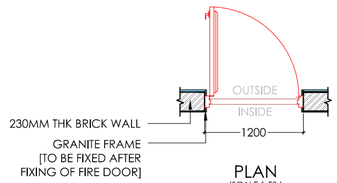

PLAN
(SCALE 1:50)

FD - 1200 x 2400 MM
- NEAR STAIRCASE & PRECISION SHOP

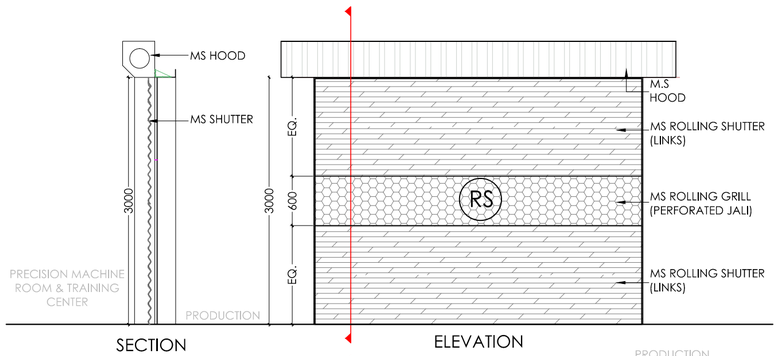

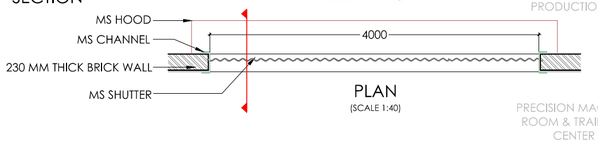


PLAN
(SCALE 1:40)

RS - 4000 x 3000 MM
- PRECISION MACHINE ROOM & TRAINING CENTER

DWG. NO- PDA/724/AR/WD/OB/DOOR AND WINDOW DETAILS/010

SHEET NO - 04/04 | R1

KEYPLAN

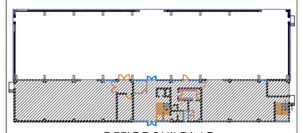

OFFICE BUILDING

OFFICE BUILDING
DOOR SCHEDULE

DOOR SCHEDULE

SR. [NO.]	NAME	SIZE [MM]	NO.	DESCRIPTION
1.	FD	1200X2400	3	NIVHA MAKE FIRE DOOR 2 HRS FIRE RATING SPEC. AS DIRECTED BY ENGINEER IN CHARGE.
2.	GD HOLD	2000X2400	1	12 MM THK TOUGHENED GLASS DOOR
3.	GD1	2000X2400	1	12 MM THK TOUGHENED GLASS DOOR *ACCESS COTROL DOOR
4.	RS	4000X3000	2	ROLLING SHUTTER
5.	D	CANCELLED		
6.	D1	1200X2400	1	35 MM THK FLUSH DOOR WITH LAMINATE ON BOTH SIDES WITH VISION PANEL
7.	D2	1000X3000	2	35 MM THK FLUSH DOOR WITH LAMINATE ON BOTH SIDES WITH VISION PANEL
8.	D3	750X2100	4	12 MM THICK MARINO DOOR
9.	D4	750X3075	2	35 MM THK FLUSH DOOR WITH LAMINATE ON BOTH SIDES
10.	D5	1000X2400	2	12 MM THK TOUGHENED GLASS DOOR
11.	D6	750X2100	1	35 MM THK FLUSH DOOR WITH LAMINATE ON BOTH SIDES
12.	D7	1200X3000	1	METAL DOOR
13.	D8	1200X2400	1	35 MM THK FLUSH DOOR WITH LAMINATE ON BOTH SIDES WITH VISION PANEL *ACCESS CONTROL DOOR
14.	D9	2500X2400	1	
16.	OP	1000X2100	1	OPENING
17.	OP1	900X2100	1	OPENING

NOTE:-
***DOORS AND WINDOWS ACCESSORIES TO BE GET IT DONE BY CONTRACTORS/VENDORS.**
***ALL ACCESSORIES ARE NOT SHOWN IN DRAWING, THAT SHOULD E PROVIDED BY CONTRACTORS/VENDORS.**

***** NOTES:**
1. PLEASE DO NOT SCALE THE DRAWING. FOLLOW WRITTEN DIMENSIONS.
2. ALL DIMENSIONS GIVEN ARE IN MM.
3. IN CASE OF CONTROVERSIES CONTACT THE ARCHITECT IMMEDIATELY.
4. FOR STRUCTURAL DETAILS PLEASE REFER R.C.C. DRAWINGS.
5. DO NOT REFER PREVIOUS DRAWINGS.
6. CONSIDER VITRIFIED FLOOR AS FLOOR FINISH UNLESS NOTED OTHERWISE.

REVISION NO.

REV. NO	DATE	DESCRIPTION
R0	05/05/2017	FIRST ISSUE TO SITE - AFC
R1	11/05/2017	REVISED DOOR D4 & ROLLING SHUTTER

PRASHANT DESHMUKH & ASSOCIATES
ARCHITECTURAL & ENGINEERING CONSULTANTS

OFFICE BUILDING DOOR/WINDOW DETAILS - GROUND FLOOR

N
NORTH

PRASHANT DESHMUKH AND ASSOCIATES
ARCHITECTURAL & ENGINEERING CONSULTANTS
1/62-B, PADMADARSHAN SOC.,
PUNE - SATARA ROAD, PUNE - 411 009.
TELEFAX :- 2422 78 96 32907142 24218714

CLIENT	TAGMA CENTRE OF EXCELLENCE & TRAINING
PROJECT	PROPOSED CENTRE OF EXCELLENCE & TRAINING FOR TAGMA, INDIA

SCALE	DEALT BY	DATE	DWG NO
AM	PAYAL	11/05/2017	PDA/724/AR/WD/OB/DOOR AND WINDOW DETAILS/010
CHK. BY	SHRIDEVI	DWG PATH	F:\Projects\Tagma\01 Architectural\04 Working\office Buildings\DETAILS\GROUND FLOOR - DOOR & WINDOW DETAILS 12.04.17 R0.dwg