





SIDE VIEW

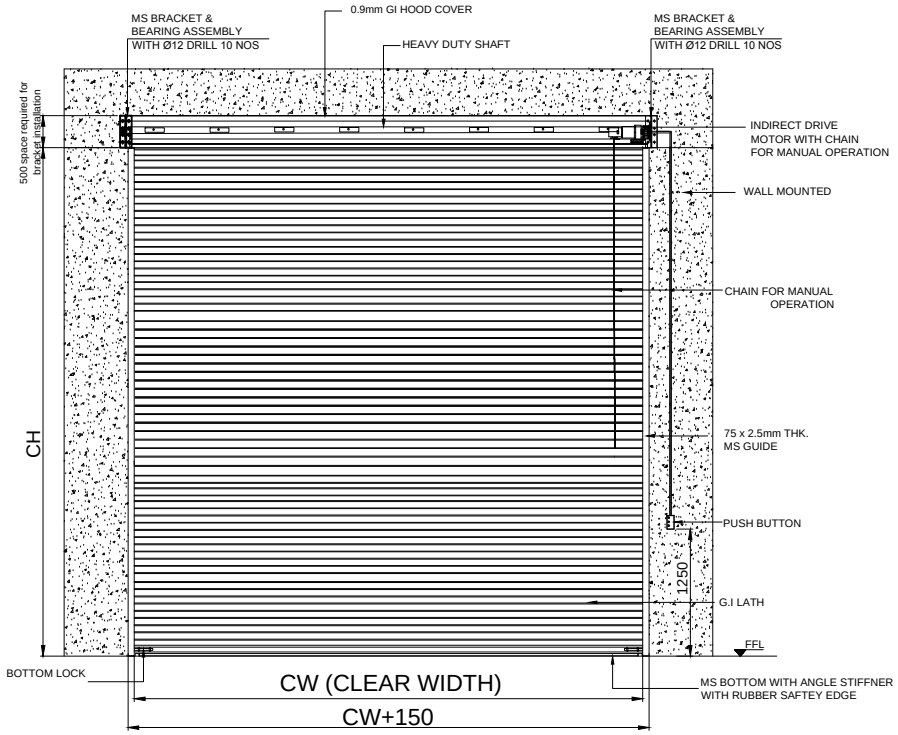



ELEVATION

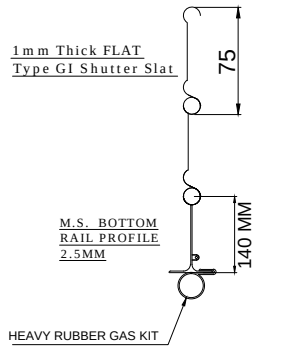


M.S. BOTTOM RAIL PROFILE 2.5MM

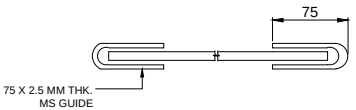

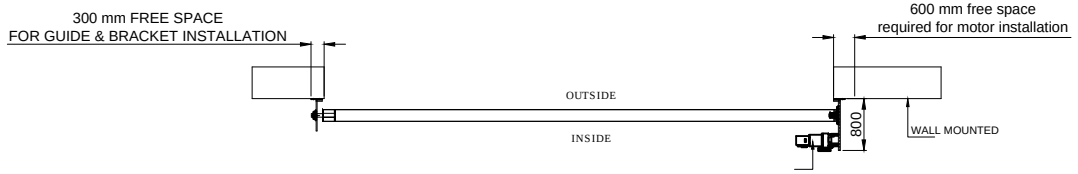
PLAN

TOLERANCE - ±5mm

NOTE-
1. ALL CIVIL WORK WILL BE CLIENT'S SCOPE.

NOTE FOR MANUFACTURING :

1. PLEASE SUPPLY SHUTTER WITHOUT SLATS & GUIDE REMAINING MATERIAL AS PER STANDARD PROCEDURE.

| S.NO | RAL CODE | COLOR | CLEAR WIDTH | CLEAR HEIGHT | QTY. | MOUNTING |
|---|---|---|---|---|---|---|
| 01 | RAL 9002 | WHITE GRAY | 2500mm | 3000mm | 6 NOS | WALL |

This drawing & design is the property of NIHVA TECHNOLOGIES. Not to be sold or copied to any other concern.

TITLE
MOTORISED ROLLING SHUTTER

| | NAME | SIGN | DATE |
|---|---|---|---|
| DRAWN | P.A | | 08.01.2020 |
| CHECK | G.J | | 08.01.2020 |
| APPRD. | | | |

If any queries contact : design@nihva.com

ALL DIMENSION ARE IN mm

NIHVA
NIHVA TECHNOLOGIES PVT. LTD.
Website:- www.nihva.com
NIHVA TECHNOLOGIES PVT. LTD. PUNE
Tel : 020 66304033
Email:- info@nihva.com

CLIENT -

PROJECT -

SITE LOCATION -

DWG. NO. : NIHVA/19-20/VDR/276 | REV- R00

SCALE: NTS | WT: | SHEET: 01 OF 01