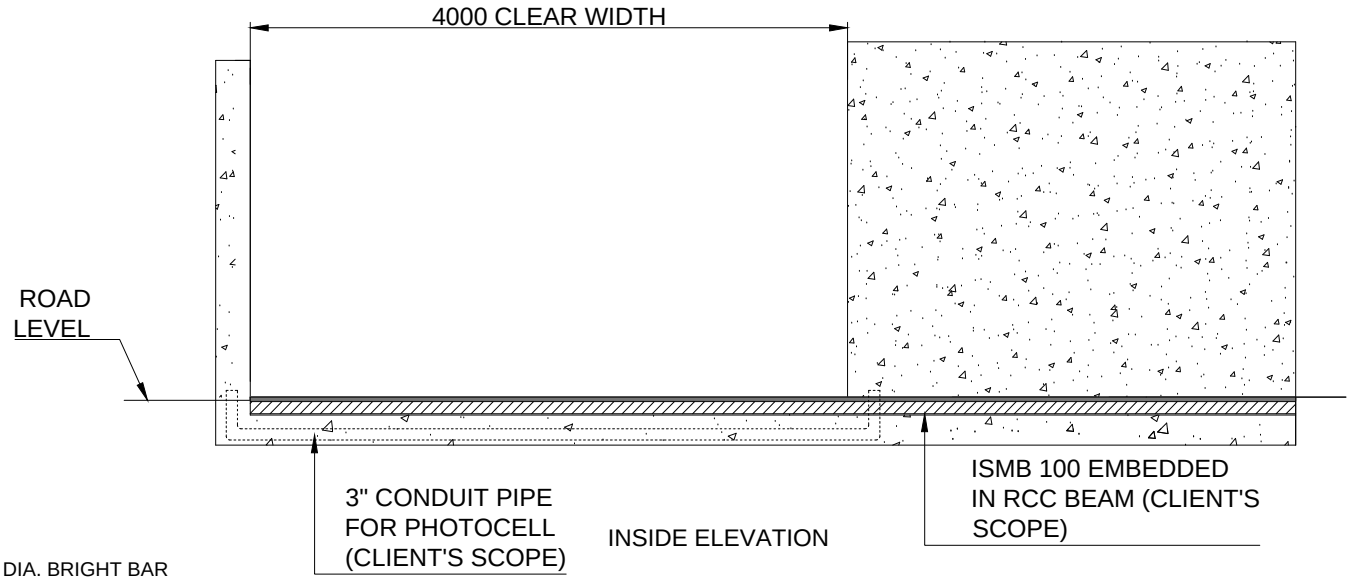

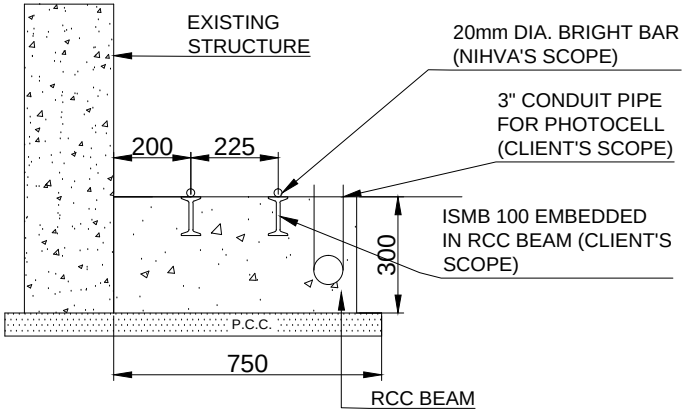

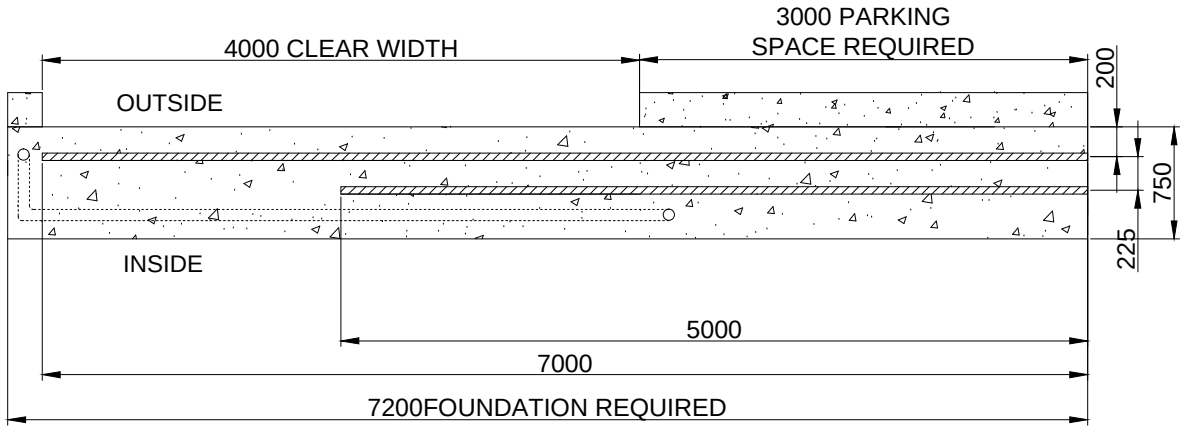

PLAN

REV 1- A. FOUNDATION WIDTH REVISED FROM 675 TO 750mm.

NOTE-
1. ALL REQUIRED CIVIL WORK WILL BE IN CLIENTS SCOPE.

GATE WIDTH	GATE HEIGHT	QUANTITY	LOCATION
4000 mm	1800mm	1 NOS	FRISKING BLOCK

This drawing & design is the property of NIHVA TECHNOLOGIES. Not to be sold or copied to any other concern.

TITLE: AUTOMATIC TWO LEAF TELESCOPIC GATE 3 FOUNDATION DRAWING

	NAME	DATE
DRAWN	OMKAR	30/10/17
CHECK	SHEKHAR	30/10/17
REV.		
APPROVAL	SHEKHAR	30/10/17

If any queries contact : projects@nihva.com

ALL DIMENSION ARE IN mm

NIHVA TECHNOLOGIES PVT. LTD.
NIHVA TECHNOLOGIES PVT. LTD. PUNE
Tel : 020 66304033
Email:- info@nihva.com
Website:- www.nihva.com

CLIENT - LUPIN LIMITED

PROJECT -

SITE LOCATION - MIHAN, NAGPUR

DWG. NO. : NIHVA/17-18/0253/R01 | REV- 1

SCALE: NTS | WT: | SHEET: 01 OF 01