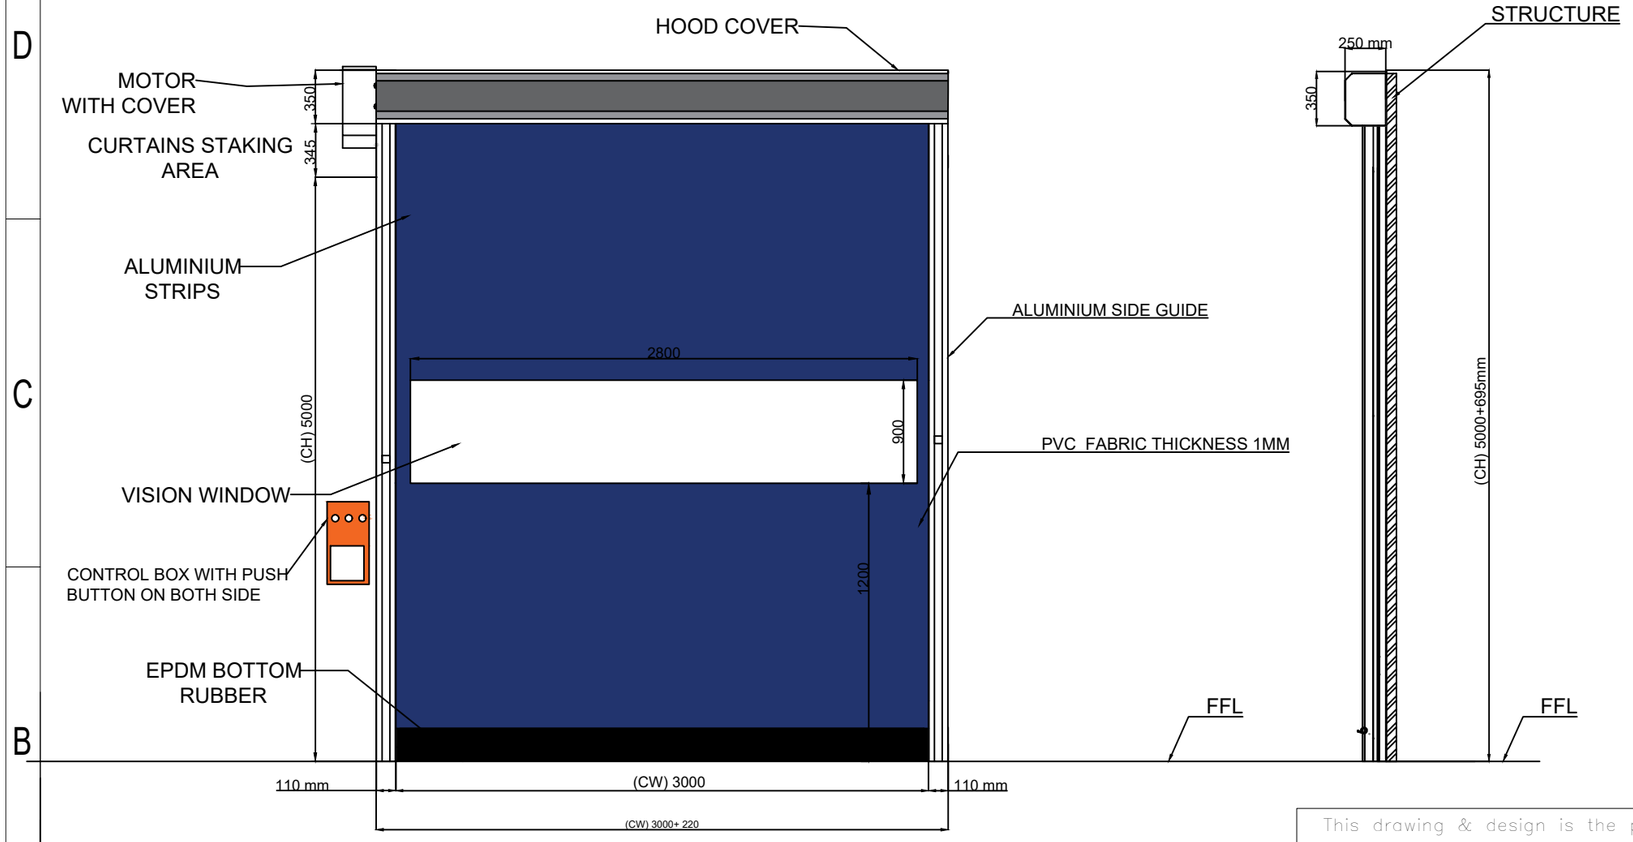


TECHNICAL SPECIFICATION :

SR.	SPECIFICATIONS	DETAILS
1	USE	INTERNAL DOOR
2	MOUNTING	ON STRUCTURE: INSIDE / OUTSIDE
3	CURTAIN PANEL	PVC FABRIC THICKNESS 1 MM
4	MANUAL RELEASE	CRANK HANDLE
5	DOOR TRAVEL SPEED	OPENING: UPTO 1.5M/SEC & CLOSING: 0.8 M/SEC
6	SAFETY DEVICE	SAFETY PHOTOCELL PAIR & SAFETY EDGES
7	ACCESSORIES	REMOTE,REVOLVING LIGHT, MAGNETIC LOOP DETECTOR,GUARD PROTECTION,THREE WAY PUSH BUTTON, FLOOR SENSOR FOR FORKLIFT
8	RAL CODE	RAL 5010

HIGH SPEED ROLL UP DOOR SIZES :-

SR	CLEAR WIDTH (CW)	CLEAR HEIGHT (CH)	QTY
1	**3000**	**5000**	01

NOTE :-

1. All DIMENSIONS ARE IN MM.

REV- R01

REV-01: AS PER CLEINT REQUIREMENT VISION WINDOW SIZE CHANGES.

This drawing & design is the property of NIHVA TECHNOLOGIES. Not to be sold or copied to any other concern.

TITLE	HIGH SPEED DOOR			NIHVA TECHNOLOGIES PVT. LTD. PUNE Tel : 020 66304033 Email:- info@nihva.com Website:- www.nihva.com	
	NAME	SIGN	DATE		
DRAWN	B.S		29.08.2025	CLIENT - MARS PETCARE IND PVT LTD	
CHECK	V.T		29.08.2025	PROJECT - HIGH SPEED DOOR	
APPRD.	V.T		29.08.2025	FORMAT NO - NIHVA-DD-F-03	
If any queries contact : Design@nihva.com				DWG. NO. : NIHVA/24-25/MP/1308001	REV- R01
ALL DIMENSION ARE IN mm				SCALE: NTS	WT: SHEET: