

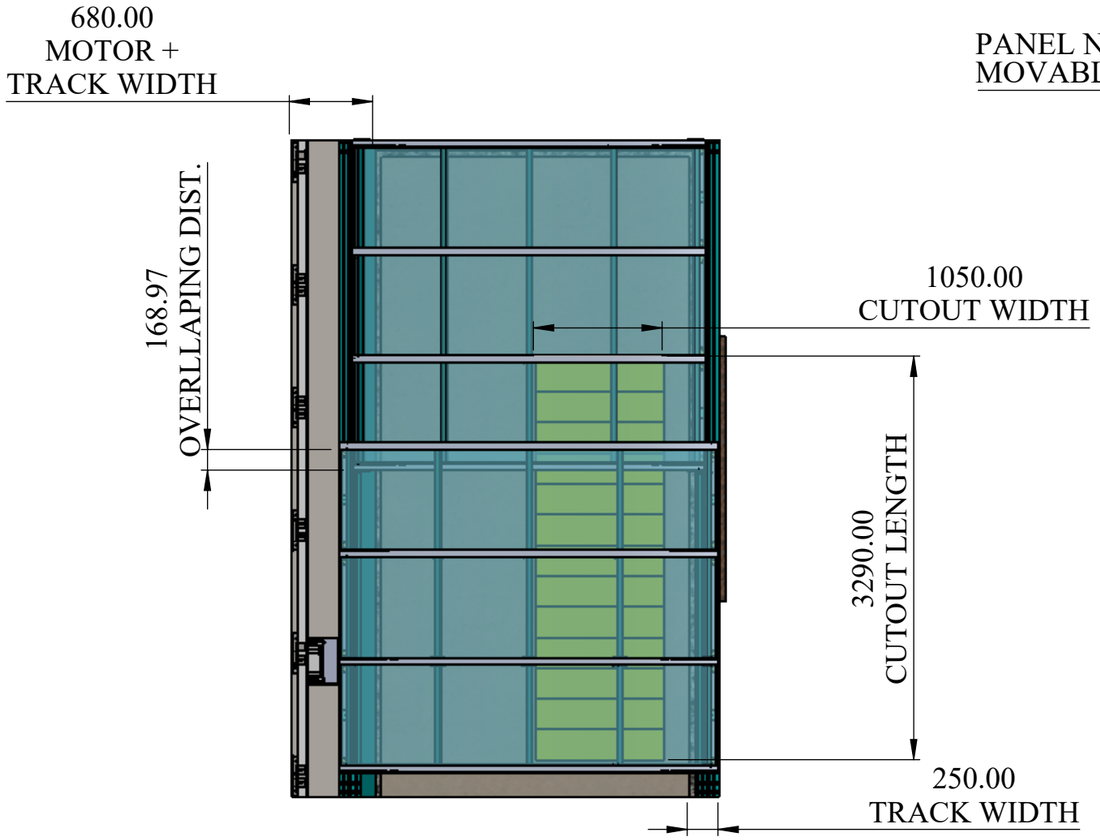


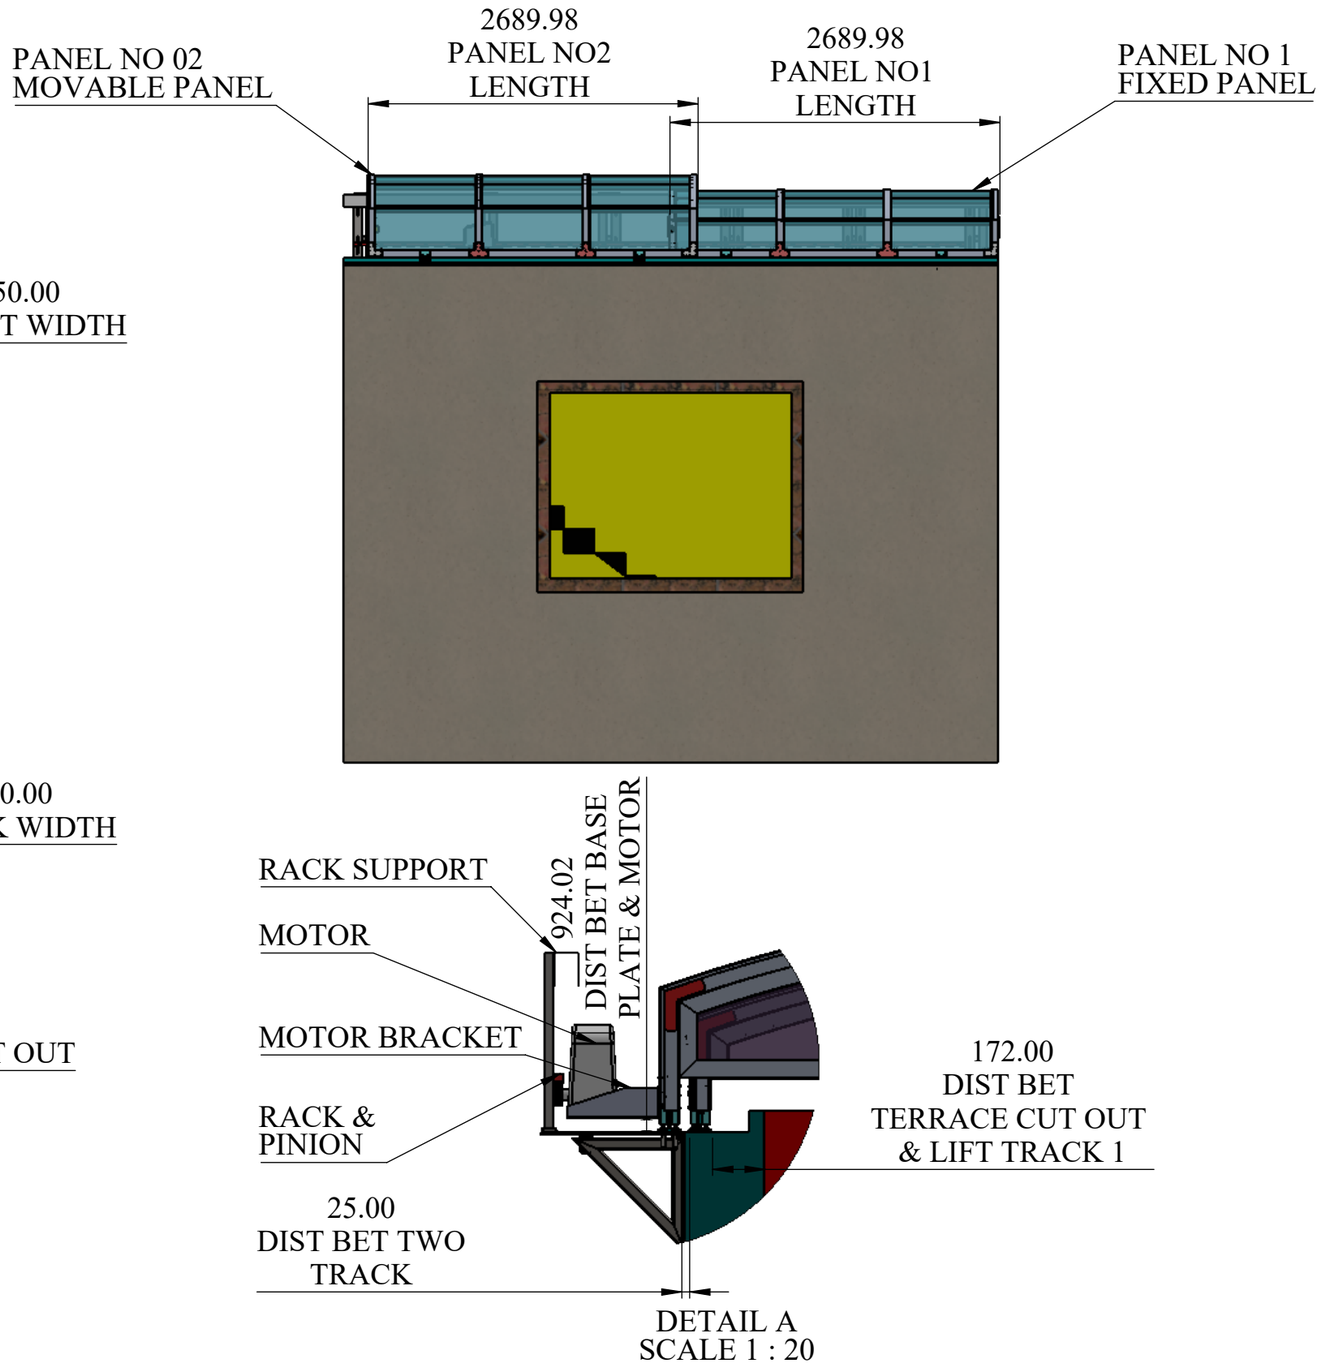


DETAIL A
SCALE 1 : 20

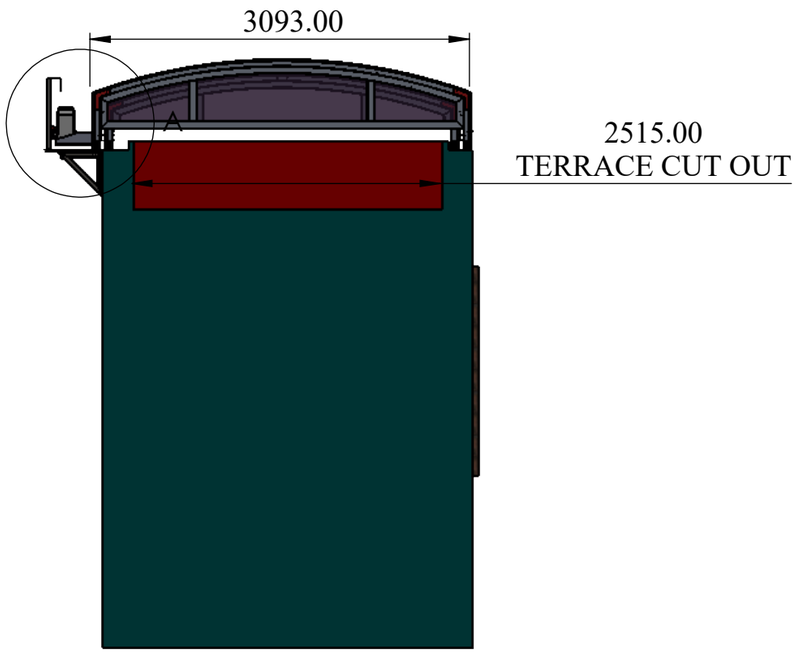

TITLE - ROOF AUTOMATION				NIHVA TECHNOLOGIES PVT.LTD.PUNE
DWG NO - NTPL-000-PM-001-00-00-00				Website - www.nihva.com
	NAME	SIGNATURE	DATE	PROJECT NO - NTPL-000-PM
DRAWN	V.W		20-05-2025	PRODUCT - RETRACTABLE ROOF
CHK'D	S.W.		20-05-2025	SITE LOCATION - LUCKNOW
APPV'D	V.T.		20-05-2025	
if any queries contact - supportautomation@nihva.com				REVISION - QTY - 1
ALL DIMENSION ARE IN mm		A3		SCALE SHEET 1 OF 21


ITEM NO.	PART NUMBER	DESCRIPTION	QTY.
1	RR_BASE STRCUTURE		1
2	GUIDE RAILS-T75-1B	STD (5 M LENGTH)	4
3	RR_PANEL NO 01 ASM		1
4	RR_PANEL NO 02 ASM		1
5	RR_RACK SUPPORT	STD (LOOSE PART)	6
6	RR_BUSBAR FLASHER	STD (LOOSE PART)	1
7	RR_RACK		1
9	RR_MOTOR (600 kg)	STD	1
10	RR_ENCLOSURE NO 02		1
11	RR_ENCLOSURE NO 01		1
12	RR_L ANGLE PLATE CORNNER JOINING PLATE	AL JOINING PLATE	8
13	RR_ Anchor Bolt M10x75	STD	48
14	NYLON STOPPER		4
15	IS 2269 - M6 x 40-N		8

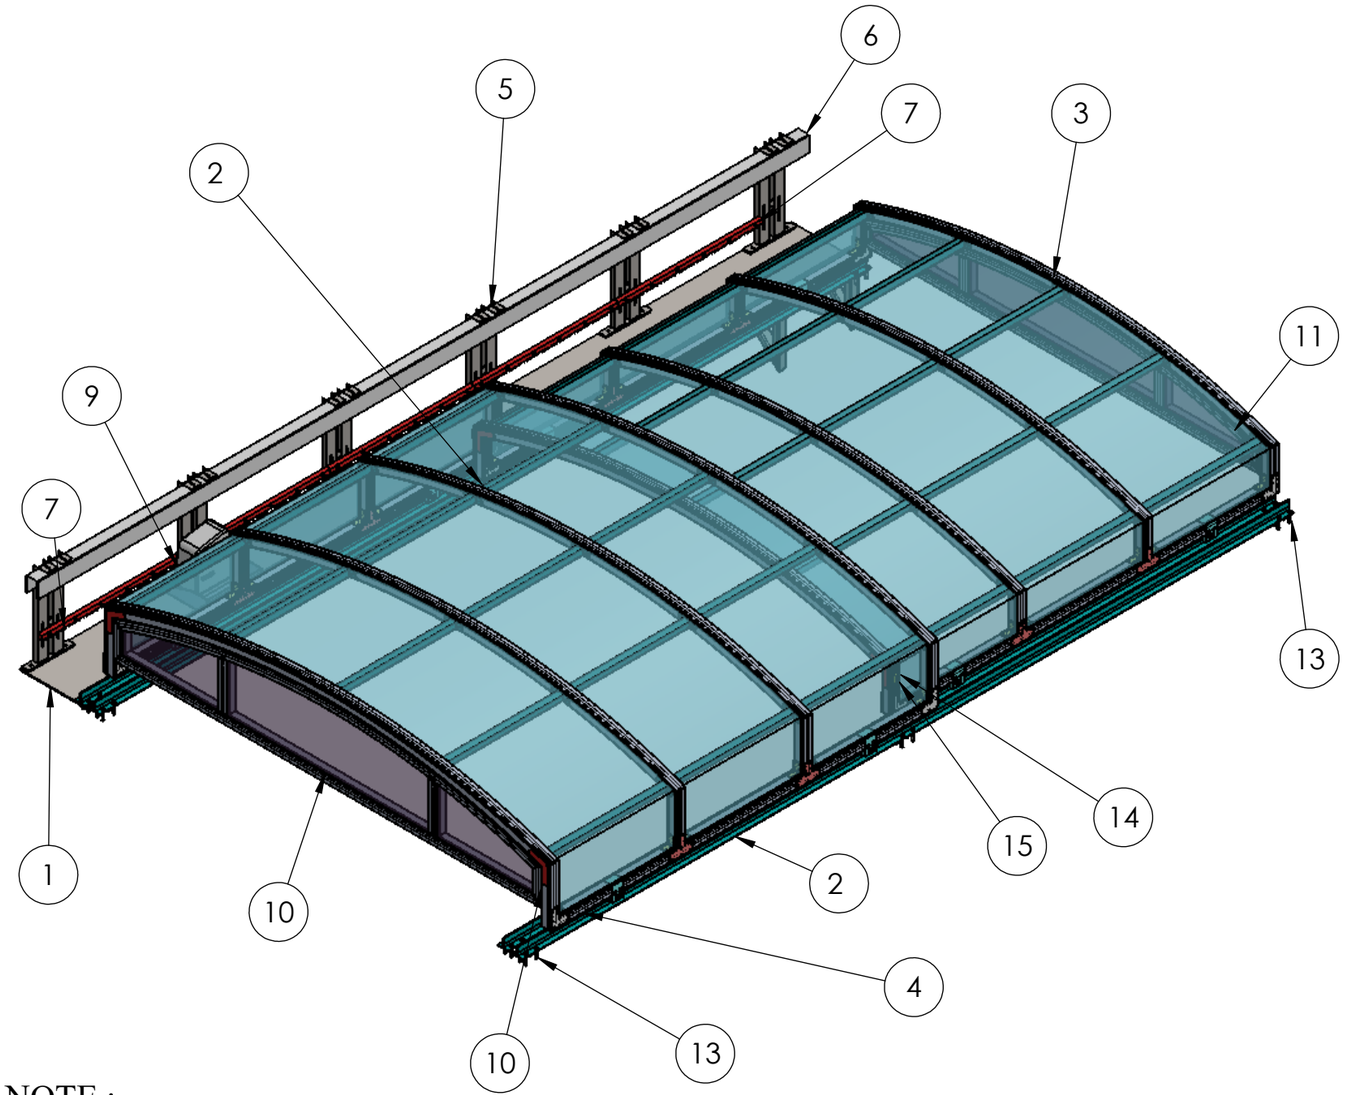


NOTE :
ISOMETRIC VIEW OF ROOF


TITLE - ROOF AUTOMATION				NIHVA TECHNOLOGIES PVT.LTD.PUNE
DWG NO - NTPL-000-PM-001-00-00-00				Website - www.nihva.com
	NAME	SIGNATURE	DATE	PROJECT NO - NTPL-000-PM
DRAWN	V.W		20-05-2025	PRODUCT - RETRACTABLE ROOF
CHK'D	S.W.		20-05-2025	SITE LOCATION - LUCKNOW
APPV'D	V.T.		20-05-2025	
if any queries contact - supportautomation@nihva.com				REVISION - QTY - 1
ALL DIMENSION ARE IN mm		A3		SCALE SHEET 2 OF 21

ITEM NO.	PART NUMBER	DESCRIPTION	QTY.
1	RR_CIVIL BASE		1
2	RR_BASE STRUCTURE		1
3	GUIDE RAILS-T75-1B	STD (5 M LENGTH)	4
4	RR_ Anchor Bolt M10x75	STD	47

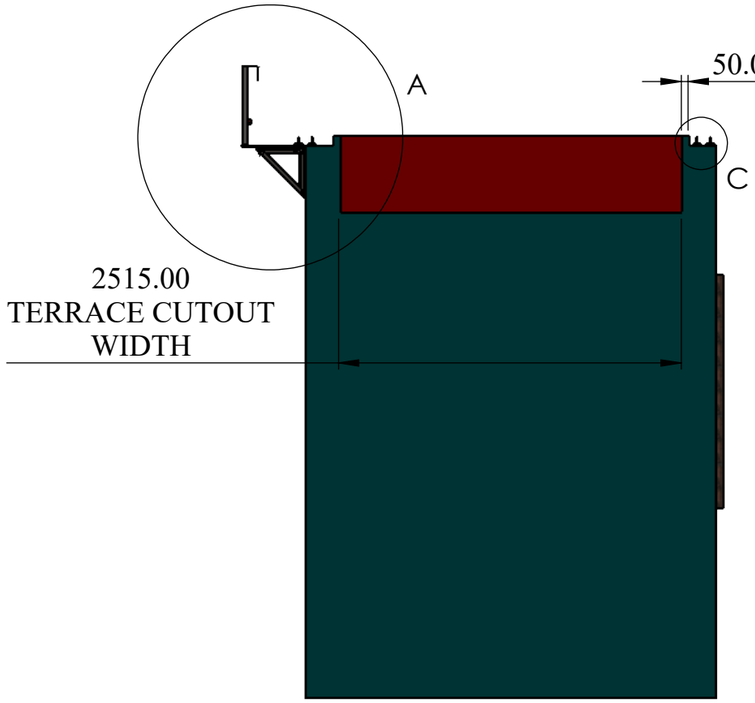


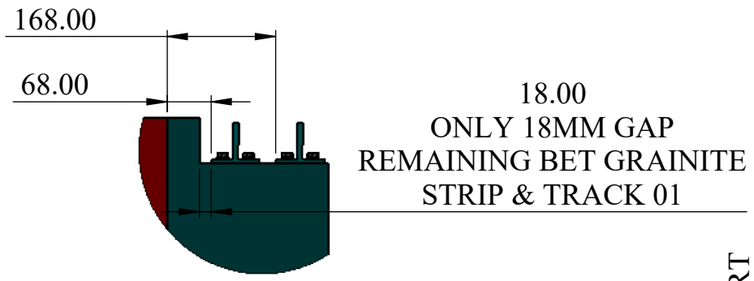


DETAIL C
SCALE 2 : 19

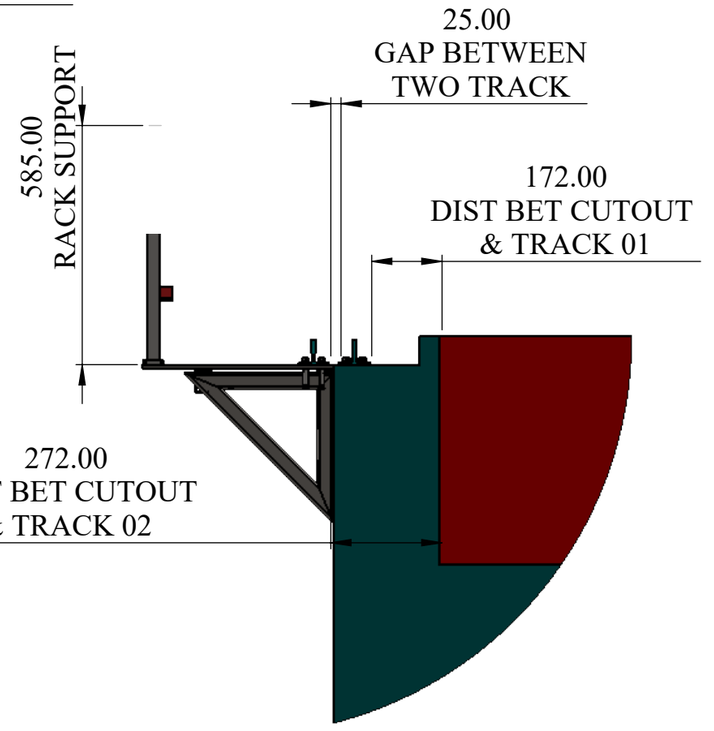

DETAIL A
SCALE 1 : 15

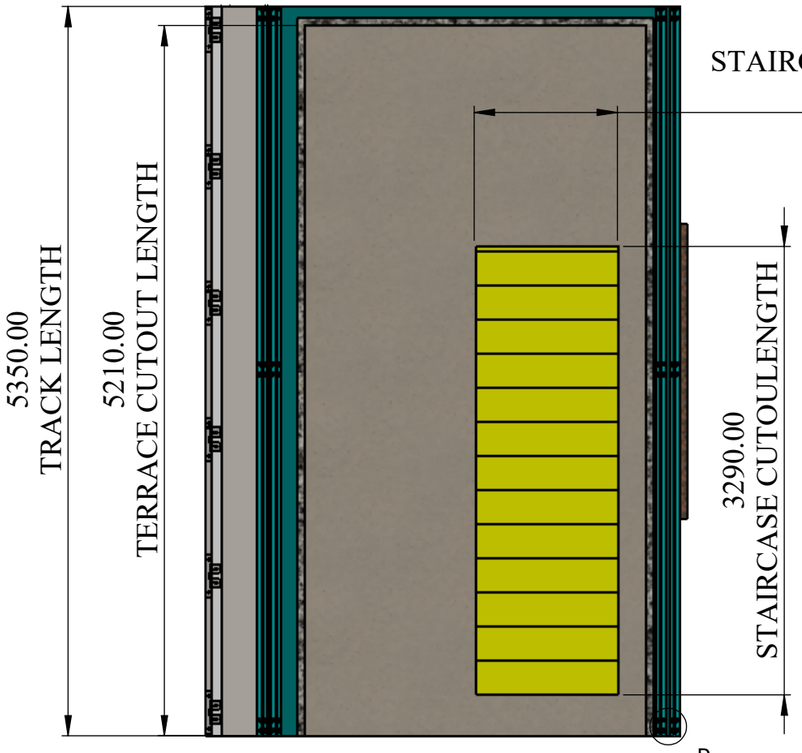

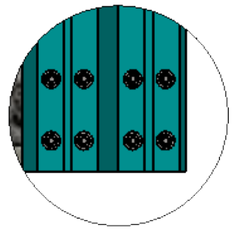


DETAIL B
SCALE 2 : 15


ANCHOR BOLT FASTENING

NOTE :
SUB ASSEMBLY NO 01
TRACK ASSEMBLY

TITLE - ROOF AUTOMATION				NIHVA TECHNOLOGIES PVT.LTD.PUNE
DWG NO - NTPL-000-PM-001-00-00-00				Website - www.nihva.com
	NAME	SIGNATURE	DATE	PROJECT NO - NTPL-000-PM
DRAWN	V.W		20-05-2025	PRODUCT - RETRACTABLE ROOF
CHK'D	S.W.		20-05-2025	SITE LOCATION - LUCKNOW
APPV'D	V.T.		20-05-2025	
if any queries contact - supportautomation@nihva.com				REVISION - QTY - 1
ALL DIMENSION ARE IN mm		A3		SCALE SHEET 3 OF 21

ITEM NO.	PART NUMBER	DESCRIPTION	QTY.
1	GUIDE RAILS-T75-1B	STD (5 M LENGTH)	4

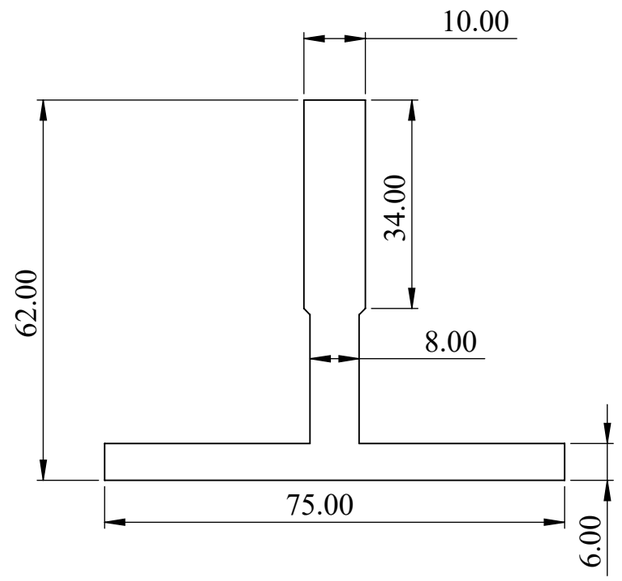


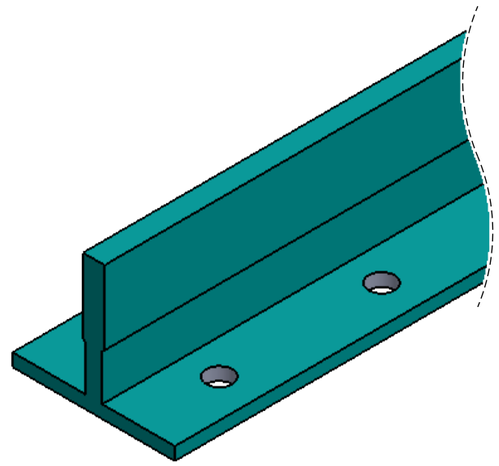


LIFT TRACK T-75


NOTE
LIFT TRACK T-75
5M UNIT LENGTH
QTY-4 No's

TITLE - ROOF AUTOMATION				NIHVA TECHNOLOGIES PVT.LTD.PUNE	
DWG NO - NTPL-000-PM-001-01-03-03				Website - www.nihva.com	
	NAME	SIGNATURE	DATE	PROJECT NO - NTPL-000-PM	
DRAWN	V.W		21-05-2025	PRODUCT - RETRACTABLE ROOF	
CHK'D	S.W.		21-05-2025	SITE LOCATION - LUCKNOW	
APPV'D	V.T.		21-05-2025		
if any queries contact - supportautomation@nihva.com				REVISION -	QTY - 1
ALL DIMENSION ARE IN mm		A3		SCALE	SHEET 4 OF 21

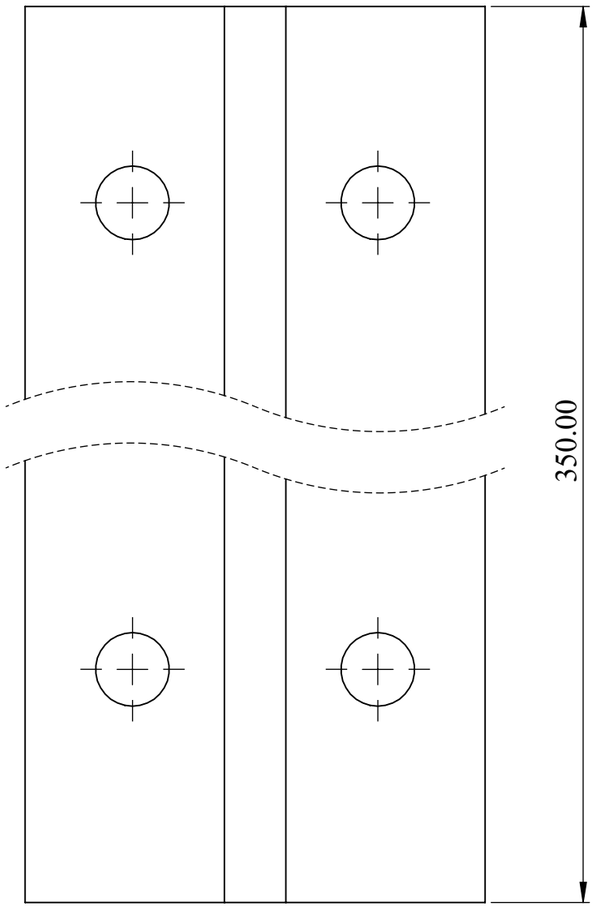

ITEM NO.	PART NUMBER	DESCRIPTION	QTY.
1	GUIDE RAILS-T75-1B	STD (5 M LENGTH)	4

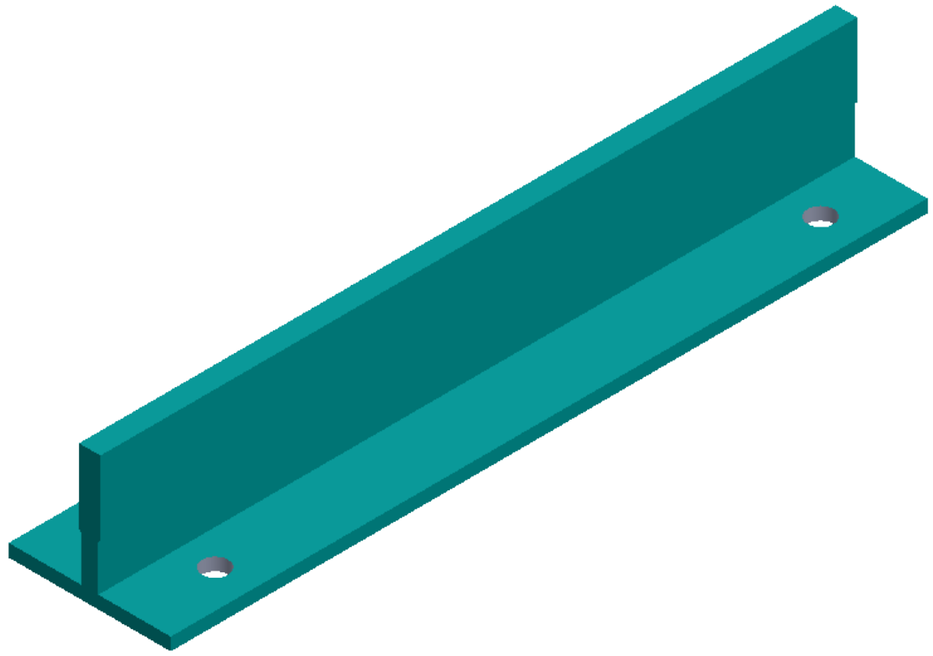


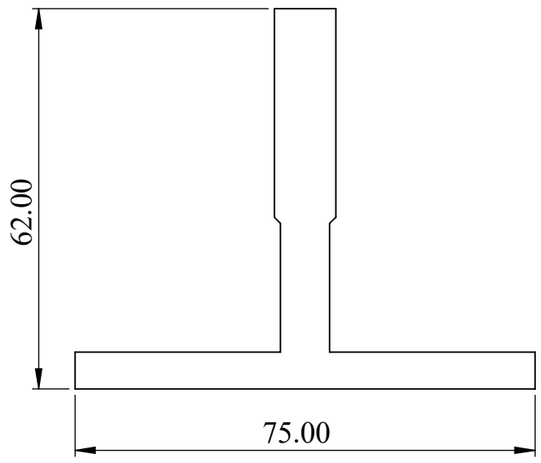


NOTE :
LIFT TRACK - T75 - 1B
PART REQUIRED TO CUT- 350MM LENGTH
QTY- 4 No's

TITLE - ROOF AUTOMATION				NIHVA TECHNOLOGIES PVT.LTD.PUNE
DWG NO - NTPL-000-PM-001-01-03-03				Website - www.nihva.com
	NAME	SIGNATURE	DATE	PROJECT NO - NTPL-000-PM
DRAWN	V.W		21-05-2025	PRODUCT - RETRACTABLE ROOF
CHK'D	S.W.		21-05-2025	SITE LOCATION - LUCKNOW
APPV'D	V.T.		21-05-2025	
if any queries contact - supportautomation@nihva.com				REVISION - QTY - 1
ALL DIMENSION ARE IN mm		A3		SCALE SHEET 5 OF 21

ITEM NO.	PART NUMBER	DESCRIPTION	QTY.
1	RR_ Anchor Bolt M10x75	STD	48

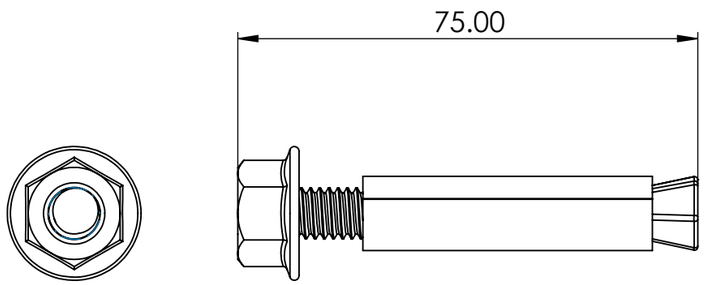


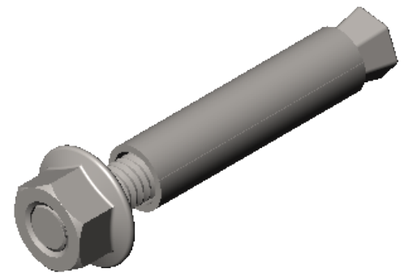


NOTE :
ANCHOR BOLT
M10x75MM


TITLE - ROOF AUTOMATION				NIHVA TECHNOLOGIES PVT.LTD.PUNE
DWG NO - NTPL-000-PM-001-01-04-04				Website - www.nihva.com
	NAME	SIGNATURE	DATE	PROJECT NO - NTPL-000-PM
DRAWN	V.W		22-05-2025	PRODUCT - RETRACTABLE ROOF
CHK'D	S.W.		22-05-2025	SITE LOCATION - LUCKNOW
APPV'D	V.T.		22-05-2025	
if any queries contact - supportautomation@nihva.com				REVISION - QTY - 1
ALL DIMENSION ARE IN mm		A3		SCALE SHEET 6 OF 21

ITEM NO.	PART NUMBER	DESCRIPTION	QTY.
1	RR_PANEL NO 01 ASM		1
2	RR_PANEL NO 02 ASM		1
3	RR_RACK SUPPORT	STD (LOOSE PART)	6
4	RR_BUSBAR FLASHER	STD (LOOSE PART)	1
5	RR_PRJ LUCKANOW RACK ASM		1
6	RR_MOTOR (600 kg)	STD	1
7	RR_ENCLOSURE NO 02		1
8	RR_ENCLOSURE NO 01		1
9	NYLON STOPPER		4
10	IS 2269 - M6 x 40-N		8

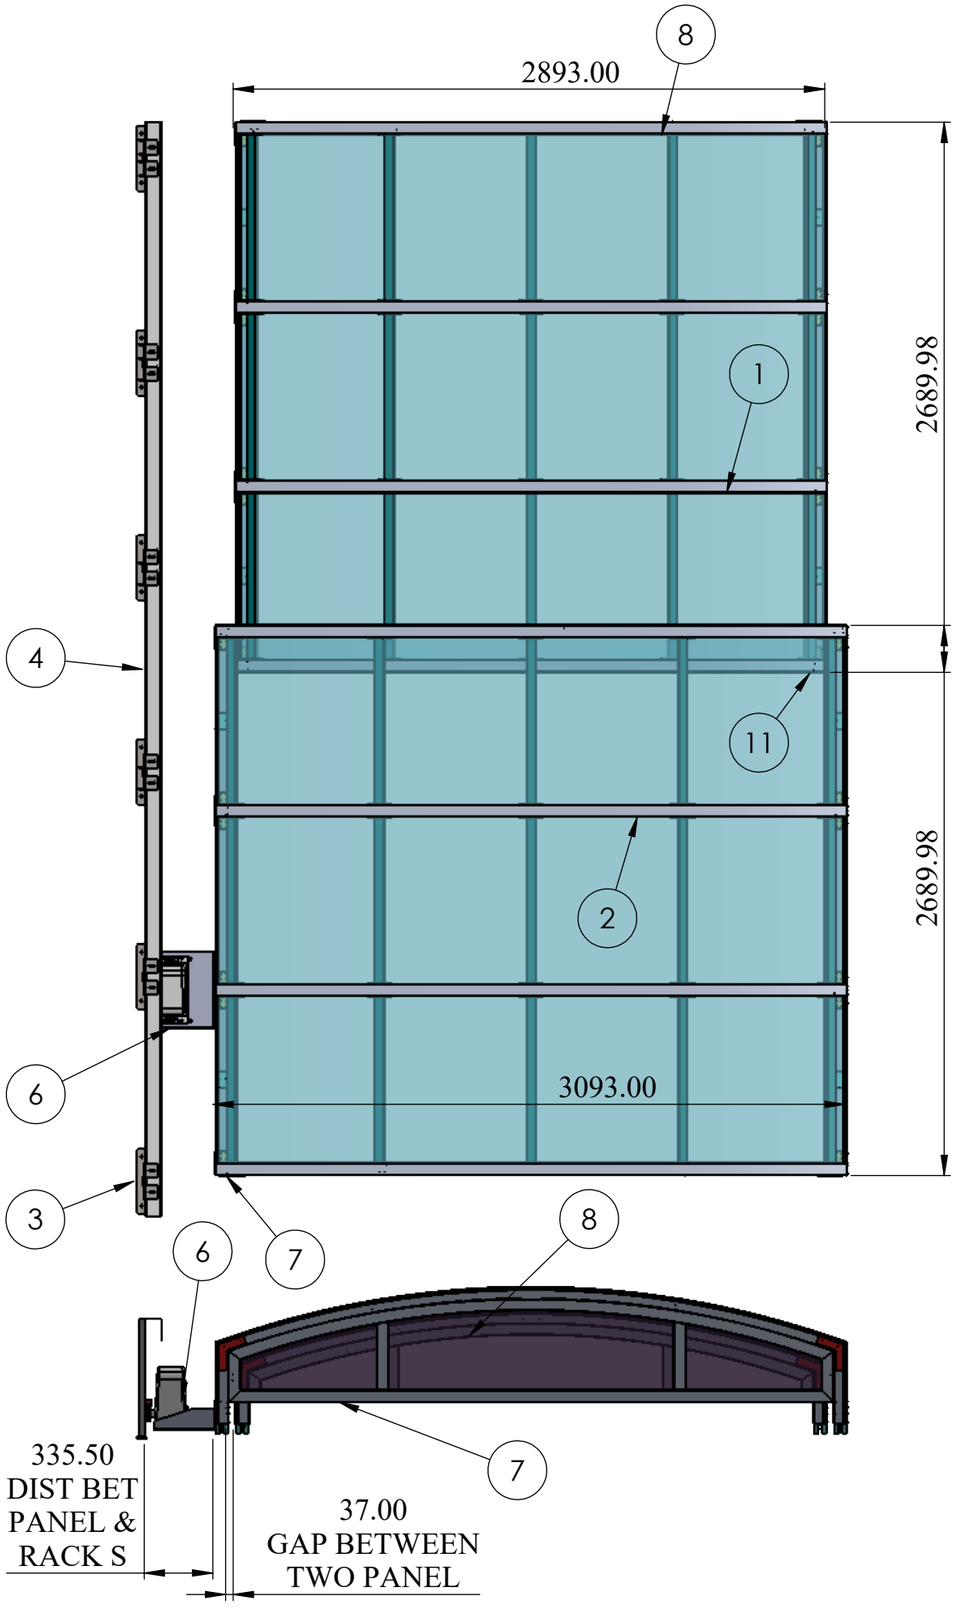


DETAIL H
SCALE 1 : 5

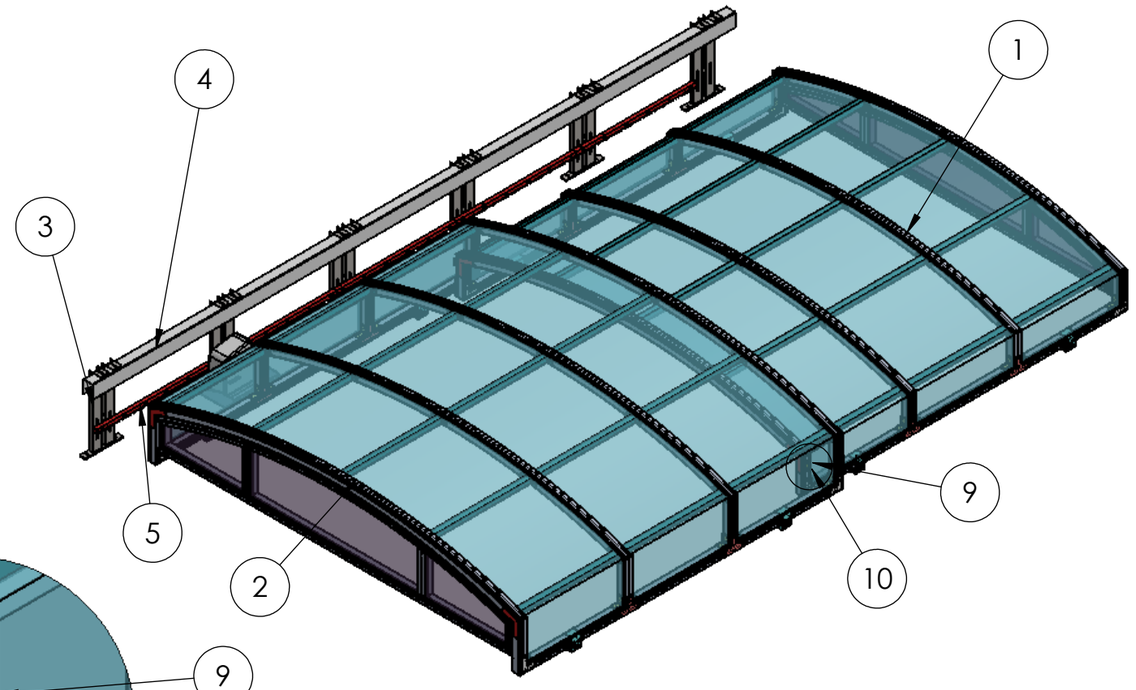


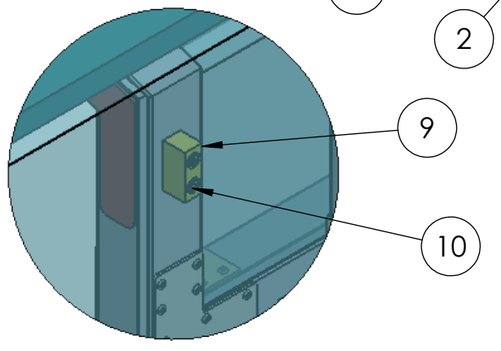


NOTE :
SUB ASSEMBLY NO 02
PANEL ASSEMBLY

TITLE - ROOF AUTOMATION				NIHVA TECHNOLOGIES PVT.LTD.PUNE
DWG NO - NTPL-000-PM-001-00-00-00				Website - www.nihva.com
	NAME	SIGNATURE	DATE	PROJECT NO - NTPL-000-PM
DRAWN	V.W		22-05-2025	PRODUCT - RETRACTABLE ROOF
CHK'D	S.W.		22-05-2025	SITE LOCATION - LUCKNOW
APPV'D	V.T.		22-05-2025	
if any queries contact - supportautomation@nihva.com				REVISION - QTY - 1
ALL DIMENSION ARE IN mm			A3	SCALE SHEET 7 OF 21

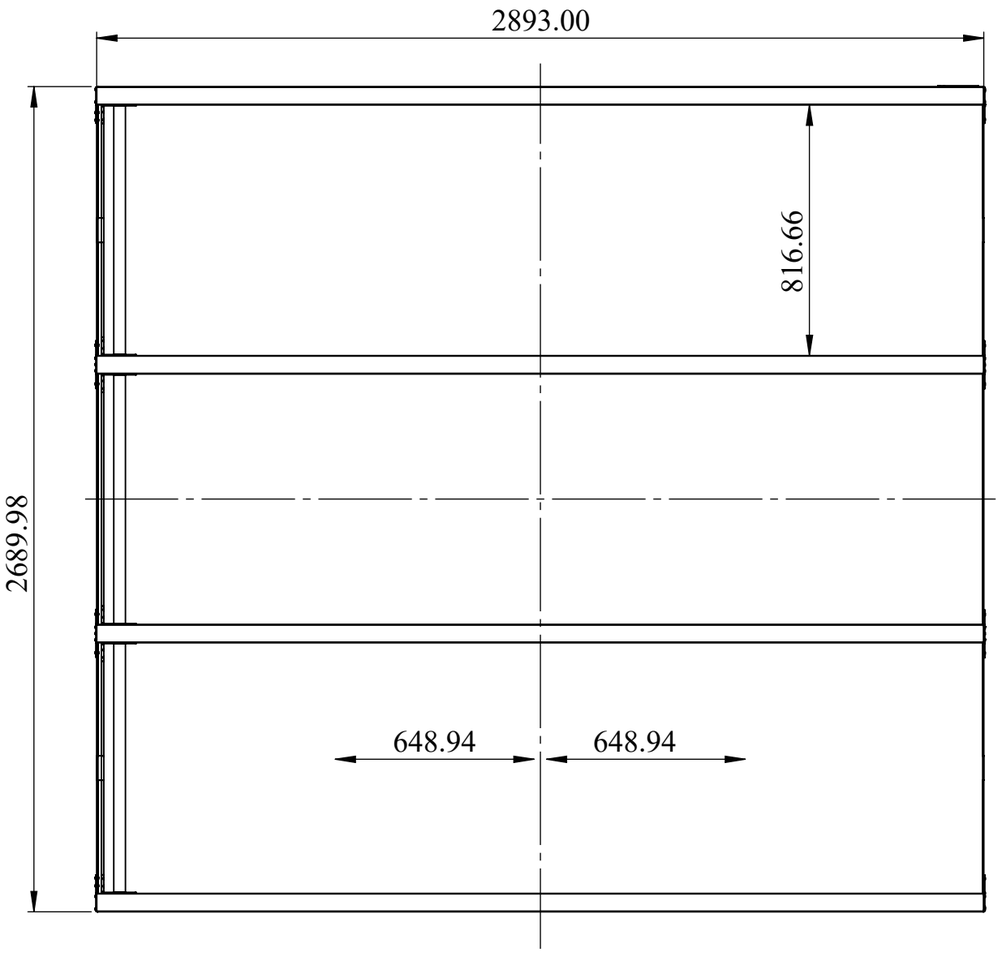

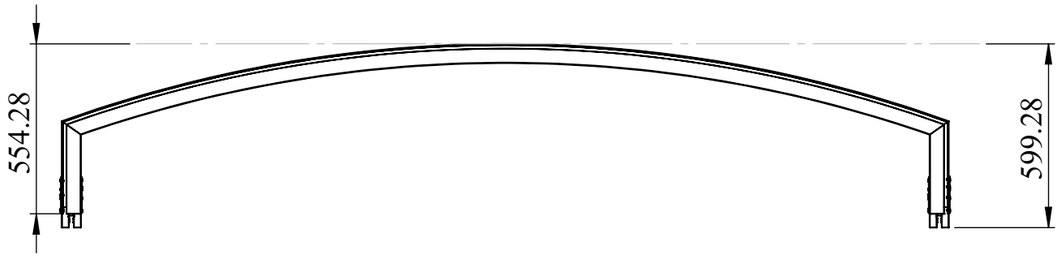


ITEM NO.	PART NUMBER	DESCRIPTION	QTY.
1	RR_ PANEL NO 01		1
2	AL Support tube SQ TUBE 40X40X1.5 MM L-816.66 MM	AL INTERMEDIAT SUPPORT TUBE	15
3	RR_BEARING BLOCK ASM WITH SHOULDER BOLT	SLIDING BLOCK	4
4	T PLATE	JOINING PLATE	8
5	L PALTE	JOINING PLATE	8
6	L ANGLE PLATE	JOINING PLATE	12
7	RR_L ANGLE PLATE CORNNER JOINING PLATE	AL JOINING PLATE	4
11	RR_ PANEL NO 01		3

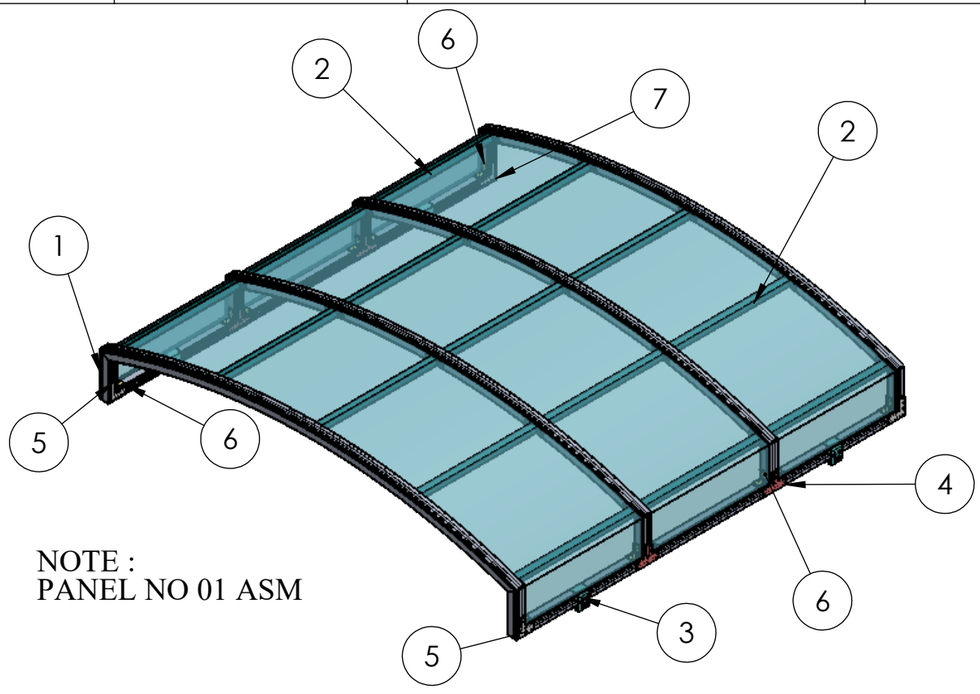


NOTE :
PANEL NO 01 ASM


TITLE - ROOF AUTOMATION				NIHVA TECHNOLOGIES PVT.LTD.PUNE
DWG NO - NTPL-000-PM-001-02-00-01				Website - www.nihva.com
	NAME	SIGNATURE	DATE	PROJECT NO - NTPL-000-PM
DRAWN	V.W		22-05-2025	PRODUCT - RETRACTABLE ROOF
CHK'D	S.W.		22-05-2025	SITE LOCATION - LUCKNOW
APPV'D	V.T.		22-05-2025	
if any queries contact - supportautomation@nihva.com				REVISION - QTY - 1
ALL DIMENSION ARE IN mm		A3		SCALE SHEET 8 OF 21

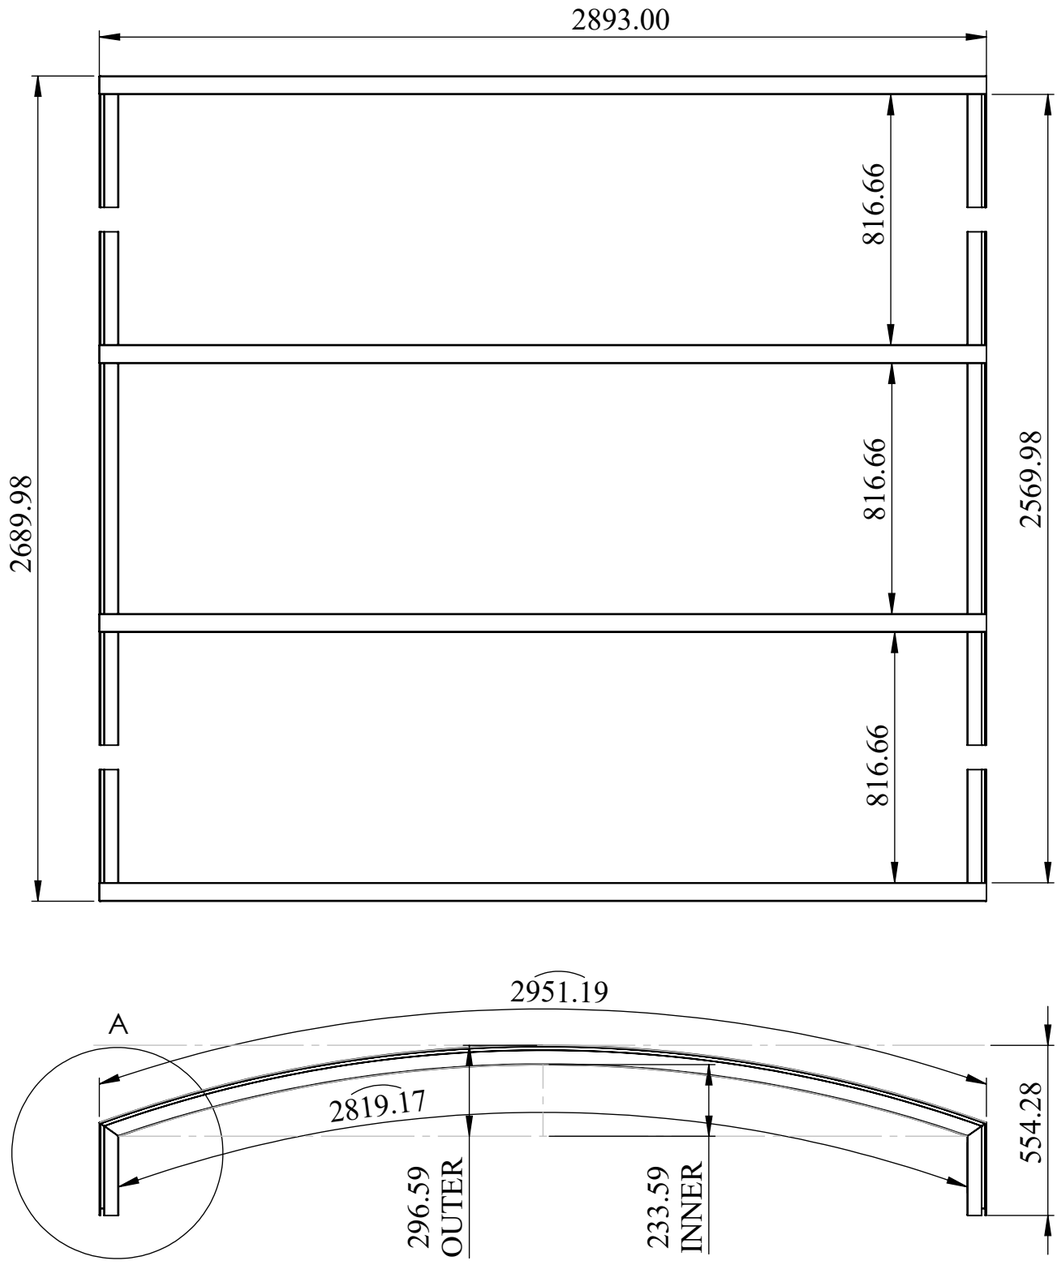

ITEM NO.	PART NUMBER	DESCRIPTION	QTY.
1	RR_ PANEL NO 01		1

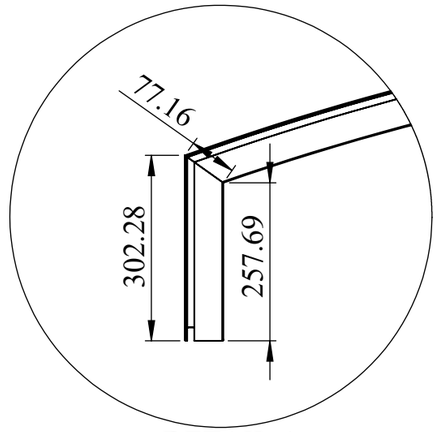


DETAIL A
SCALE 1 : 10

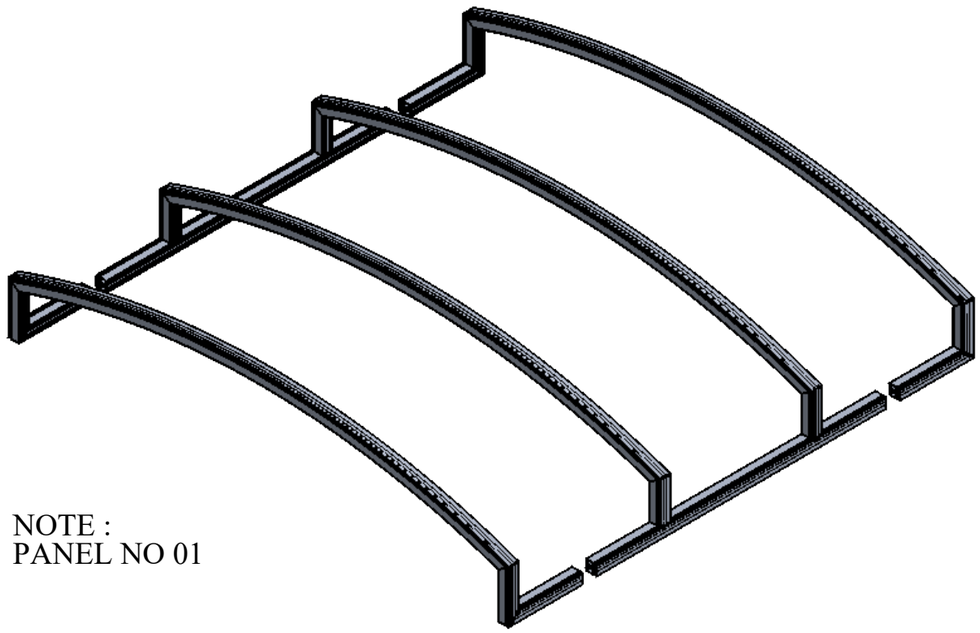


NOTE :
PANEL NO 01


TITLE - ROOF AUTOMATION				NIHVA TECHNOLOGIES PVT.LTD.PUNE
DWG NO - NTPL-000-PM-001-02-01-01				Website - www.nihva.com
	NAME	SIGNATURE	DATE	PROJECT NO - NTPL-000-PM
DRAWN	V.W		22-05-2025	PRODUCT - RETRACTABLE ROOF
CHK'D	S.W.		22-05-2025	SITE LOCATION - LUCKNOW
APPV'D	V.T.		22-05-2025	
if any queries contact - supportautomation@nihva.com				REVISION - QTY - 1
ALL DIMENSION ARE IN mm			A3	SCALE SHEET 9 OF 21

ITEM NO.	PART NUMBER	DESCRIPTION	QTY.
1	RR_ENCLOSURE NO 01		1

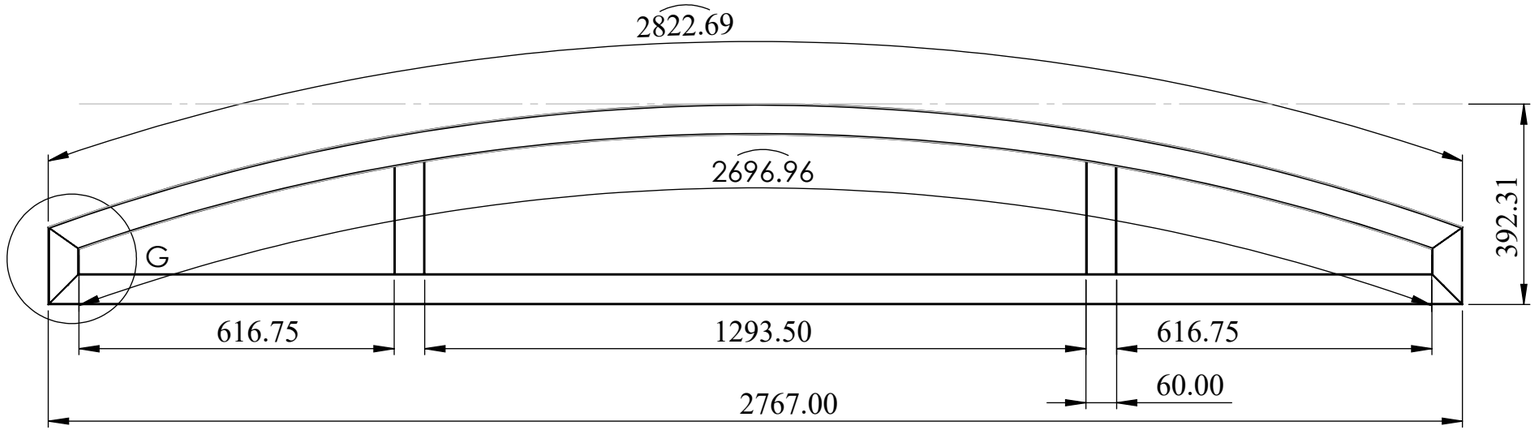

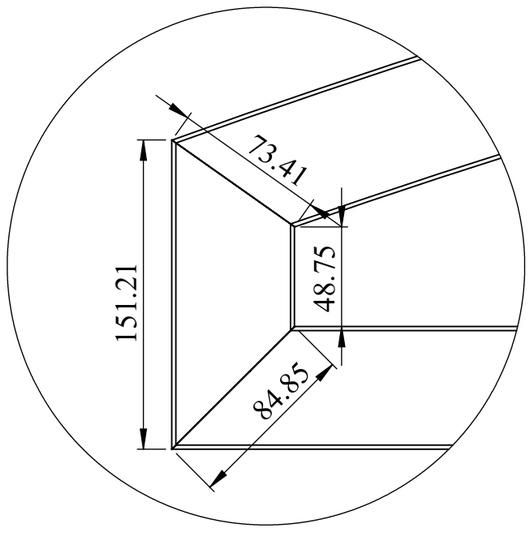

DETAIL G
SCALE 1 : 3

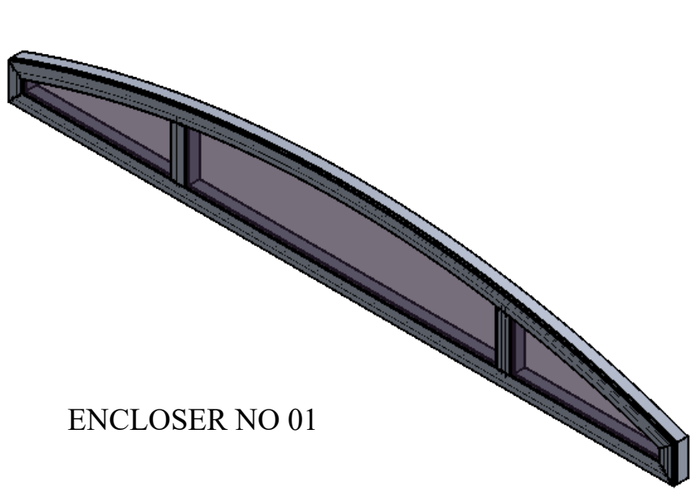



ENCLOSER NO 01

NOTE :
PANEL NO 01 ENCLOSER

TITLE - ROOF AUTOMATION				NIHVA TECHNOLOGIES PVT.LTD.PUNE
DWG NO - NTPL-000-PM-001-02-00-08				Website - www.nihva.com
	NAME	SIGNATURE	DATE	PROJECT NO - NTPL-000-PM
DRAWN	V.W		22-05-2025	PRODUCT - RETRACTABLE ROOF
CHK'D	S.W.		22-05-2025	SITE LOCATION - LUCKNOW
APPV'D	V.T.		22-05-2025	
if any queries contact - supportautomation@nihva.com				REVISION - QTY - 1
ALL DIMENSION ARE IN mm			A3	SCALE SHEET 10 OF 21


ITEM NO.	PART NUMBER	DESCRIPTION	QTY.
1	AL Support tube SQ TUBE 40X40X1.5 MM L-816.66MM	AL INTERMEDIAT SUPPORT TUBE	15

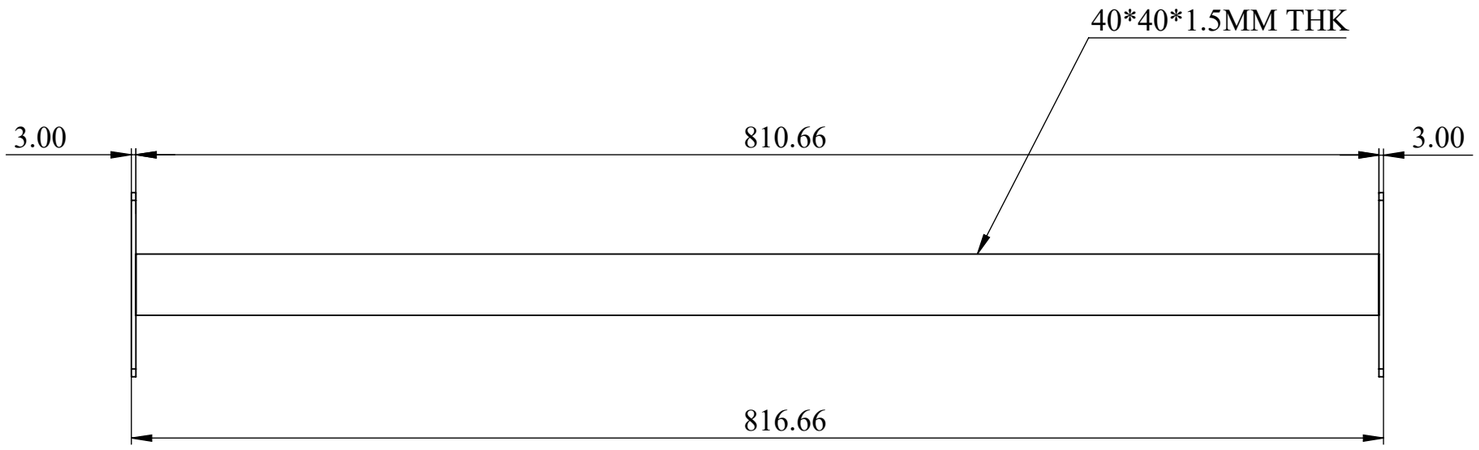


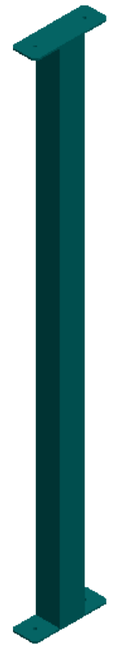


NOTE :
INTERMEDIATE SUPPORT TUBE
ONE PANEL QTY REQ - 15 No's
TOTAL REQ - 30 No's.


TITLE - ROOF AUTOMATION				NIHVA TECHNOLOGIES PVT.LTD.PUNE	
DWG NO - NTPL-000-PM-001-02-02-02				Website - www.nihva.com	
	NAME	SIGNATURE	DATE	PROJECT NO - NTPL-000-PM	
DRAWN	V.W		22-05-2025	PRODUCT - RETRACTABLE ROOF	
CHK'D	S.W.		22-05-2025	SITE LOCATION - LUCKNOW	
APPV'D	V.T.		22-05-2025		
if any queries contact - supportautomation@nihva.com				REVISION -	QTY - 1
ALL DIMENSION ARE IN mm		A3		SCALE	SHEET 11 OF 21

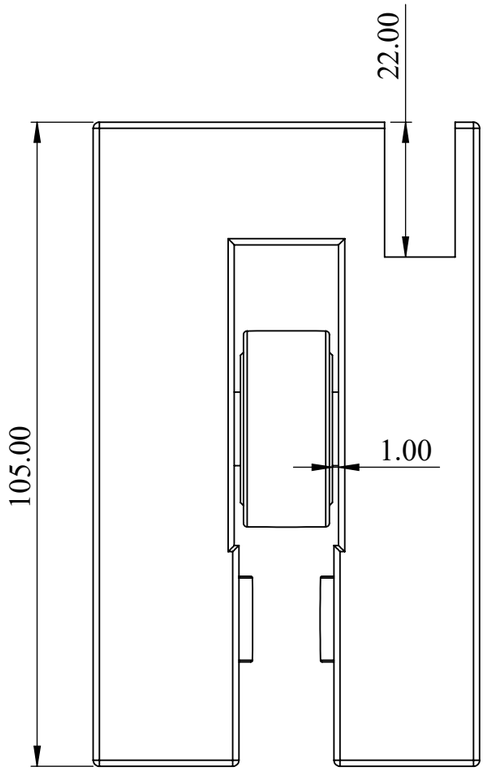

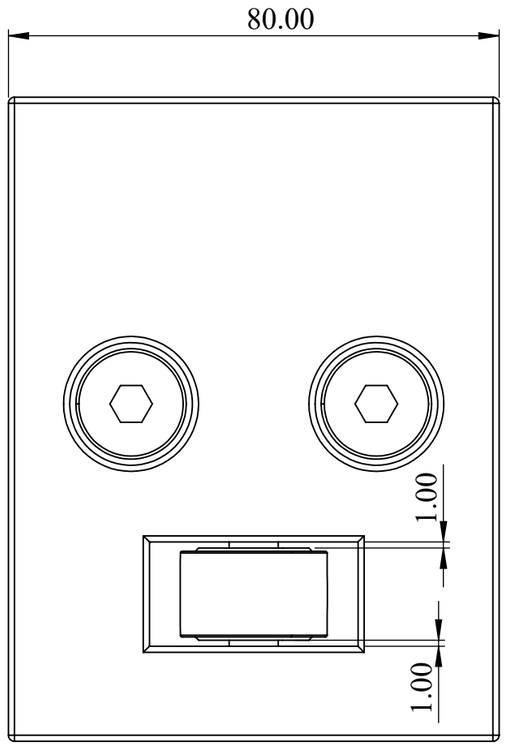


ITEM NO.	PART NUMBER	DESCRIPTION	QTY.
1	BEARING BLOCK (T75-1B)	80X105X63 MM (VMC PART)	1
2	SKF_bearing NATR 12	BRG(STD)	2
3	SKF_bearing NATR 8	BRG(STD)	2
4	RR_ SHOULDER BOLT NATR 12		2
5	RR_SHOULDER BOLT NATR 8		2

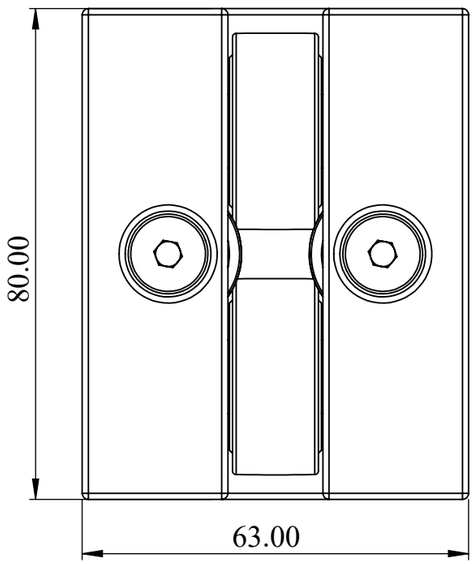

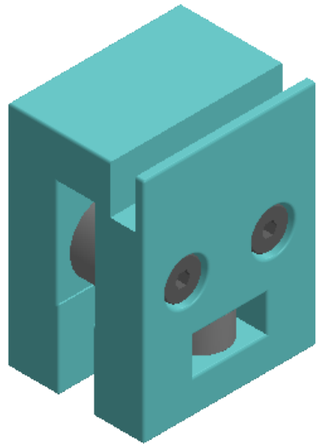



NOTE :
BAERING BLOCK ASM
THIS BEARING BLOCK ASM IS USED FOR ALL PANEL
VMC MACHINING

TITLE - ROOF AUTOMATION				NIHVA TECHNOLOGIES PVT.LTD.PUNE Website - www.nihva.com	
DWG NO - NTPL-000-PM-001-02-03-03					
	NAME	SIGNATURE	DATE	PROJECT NO - NTPL-000-PM	
DRAWN	V.W		23-05-2025	PRODUCT - RETRACTABLE ROOF	
CHK'D	S.W.		23-05-2025	SITE LOCATION - LUCKNOW	
APPV'D	V.T.		23-05-2025		
if any queries contact - supportautomation@nihva.com				REVISION -	QTY - 1
ALL DIMENSION ARE IN mm		A3		SCALE	SHEET 12 OF 21

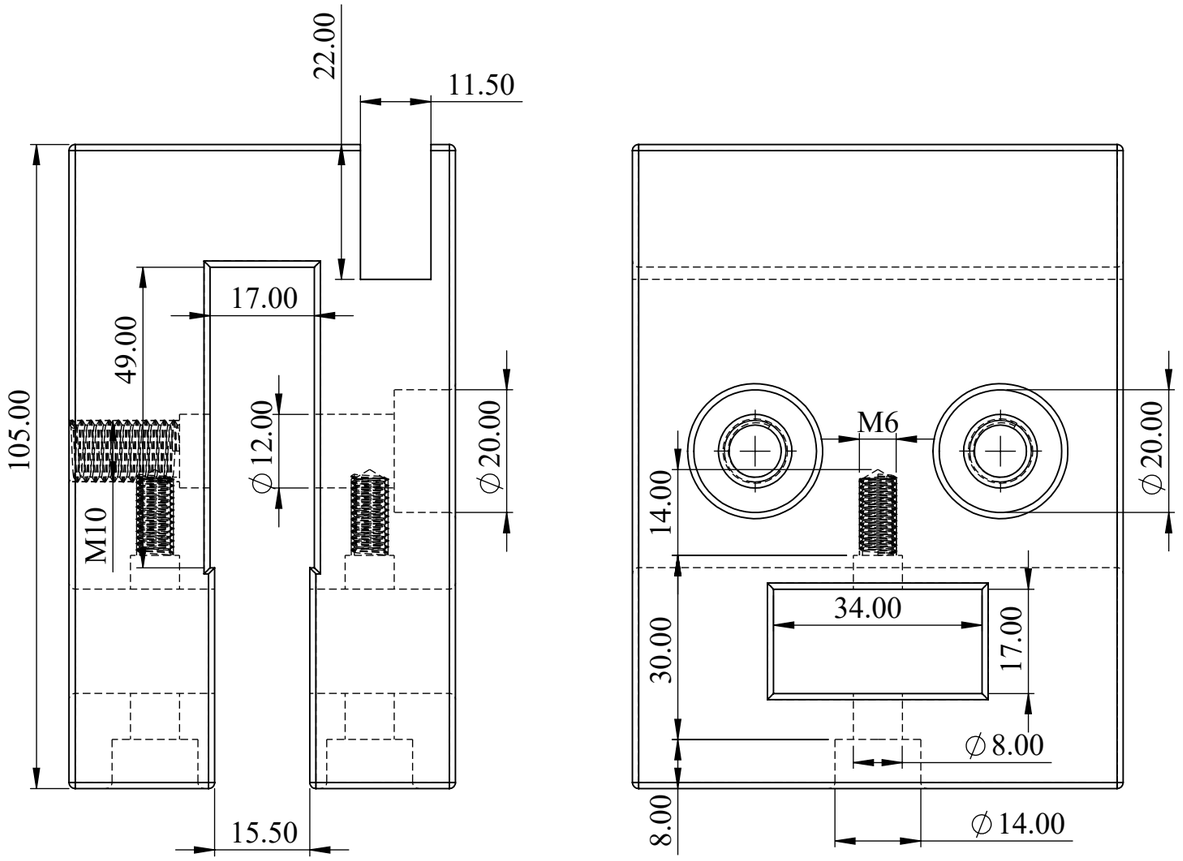

ITEM NO.	PART NUMBER	DESCRIPTION	QTY.
1	BEARING BLOCK (T75-1B)	80X105X63 MM (VMC PART)	4

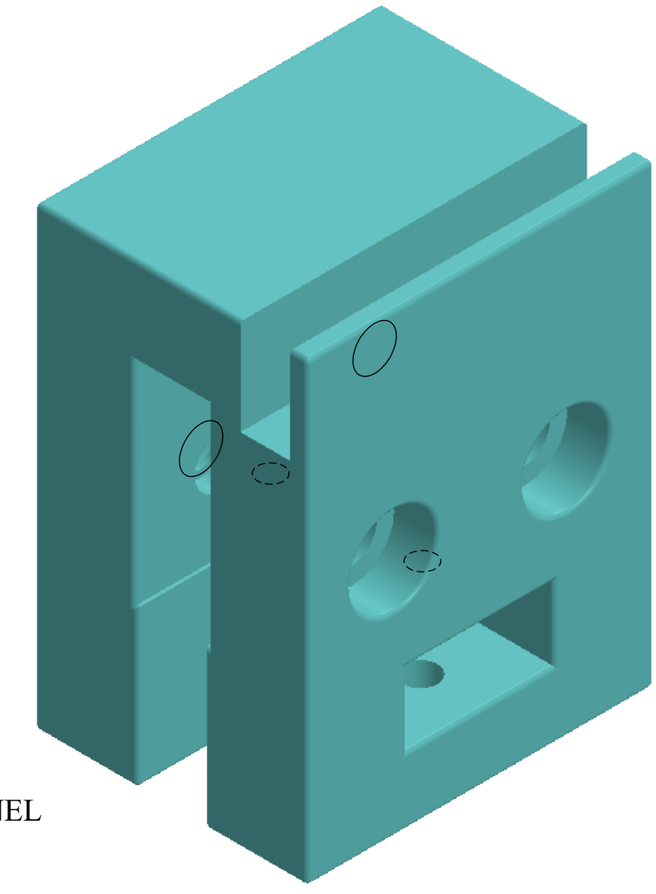


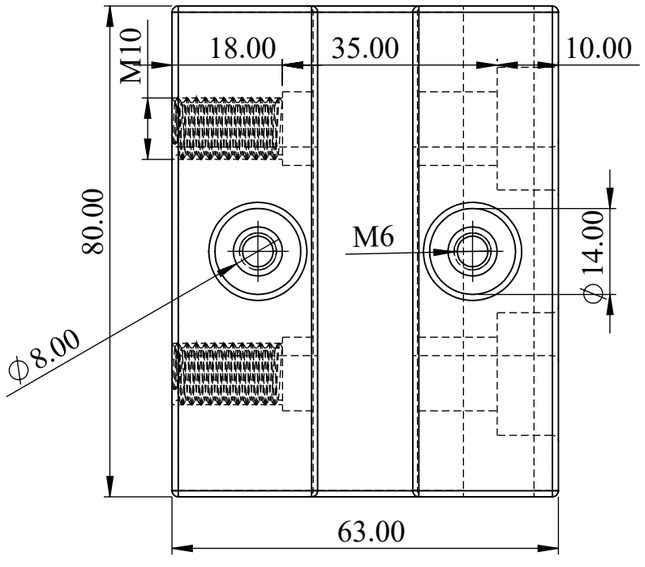


NOTE :
BEARING BLOCK
THIS BEARING BLOCK IS USED FOE ALL PANEL
VMC MACHINING

TITLE - ROOF AUTOMATION				NIHVA TECHNOLOGIES PVT.LTD.PUNE
DWG NO - NTPL-000-PM-001-02-03-03				Website - www.nihva.com
	NAME	SIGNATURE	DATE	PROJECT NO - NTPL-000-PM
DRAWN	V.W		23-05-2025	PRODUCT - RETRACTABLE ROOF
CHK'D	S.W.		23-05-2025	SITE LOCATION - LUCKNOW
APPV'D	V.T.		23-05-2025	
if any queries contact - supportautomation@nihva.com				REVISION - QTY - 1
ALL DIMENSION ARE IN mm			A3	SCALE SHEET 13 OF 21

ITEM NO.	PART NUMBER	DESCRIPTION	QTY.
1	T PLATE	SS304 -117.5X156X3 MM THK	8
2	RR_rivet_iso_15977_4_x_16_0 ss	RIVET M4X16	10

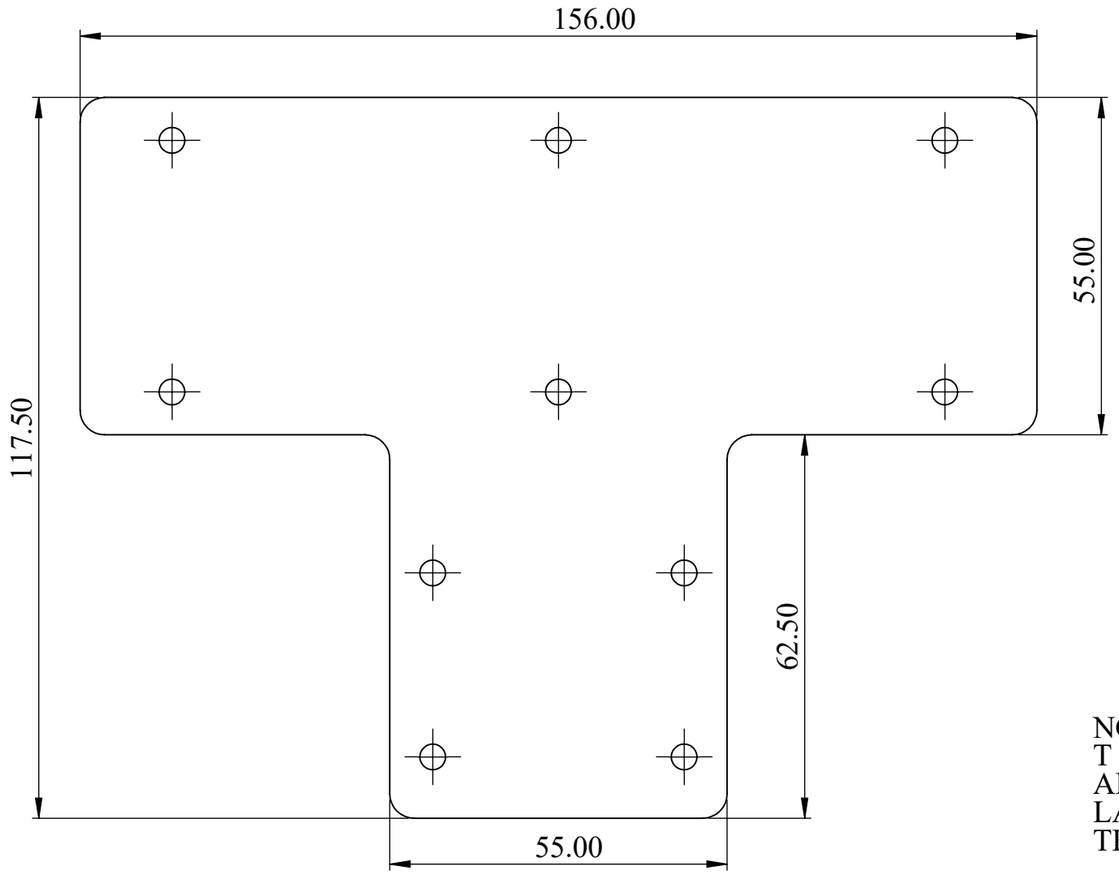


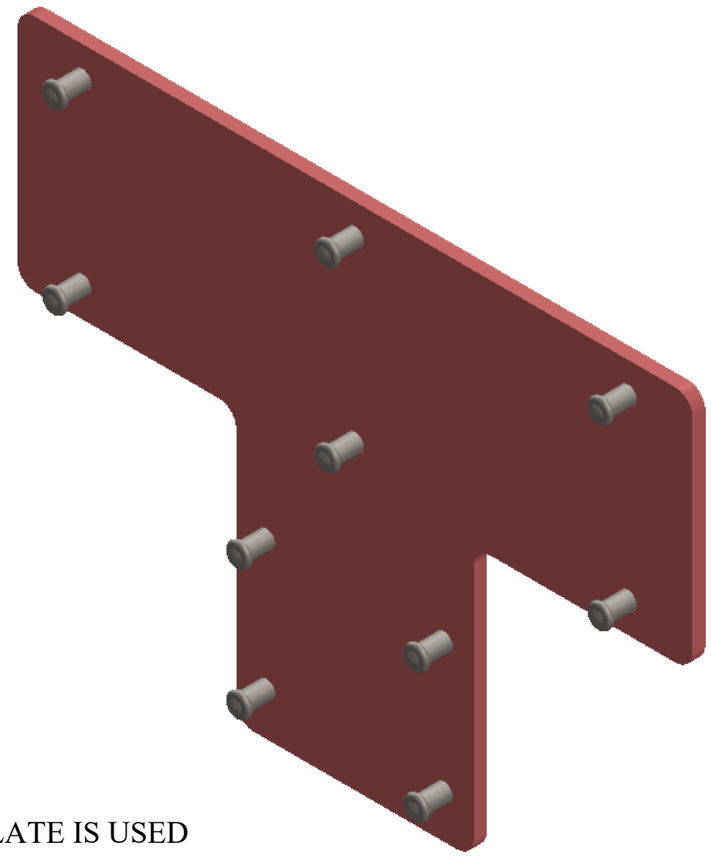


NOTE :
T PLATE
ALL PANEL THIS T PLATE IS USED
LASER CUTTING
THK-3MM

TITLE - ROOF AUTOMATION				NIHVA TECHNOLOGIES PVT.LTD.PUNE
DWG NO - NTPL-000-PM-001-02-04-04				Website - www.nihva.com
	NAME	SIGNATURE	DATE	PROJECT NO - NTPL-000-PM
DRAWN	V.W		23-05-2025	PRODUCT - RETRACTABLE ROOF
CHK'D	S.W.		23-05-2025	SITE LOCATION - LUCKNOW
APPV'D	V.T.		23-05-2025	
if any queries contact - supportautomation@nihva.com				REVISION - / QTY - 1
ALL DIMENSION ARE IN mm		A3		SCALE / SHEET 14 OF 21

ITEM NO.	PART NUMBER	DESCRIPTION	QTY.
1	L PLATE	SS304- 91X106X3 MM THK	8
2	RR_rivet_iso_15977_4_x_16_0_ss	RIVET M4X16	10

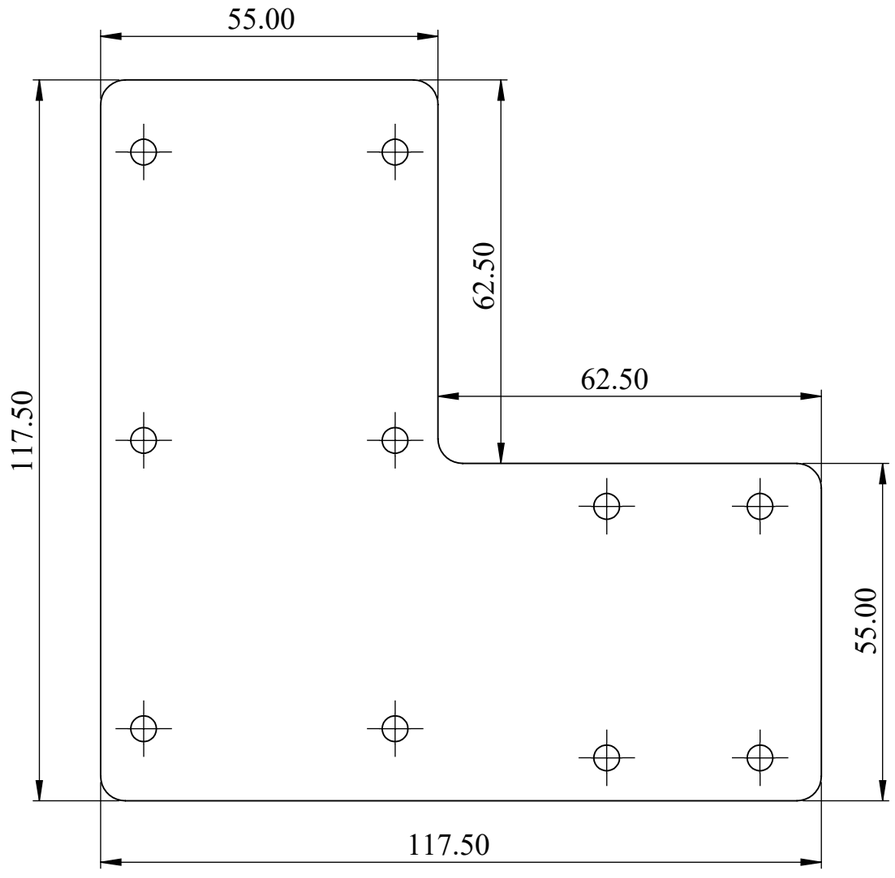


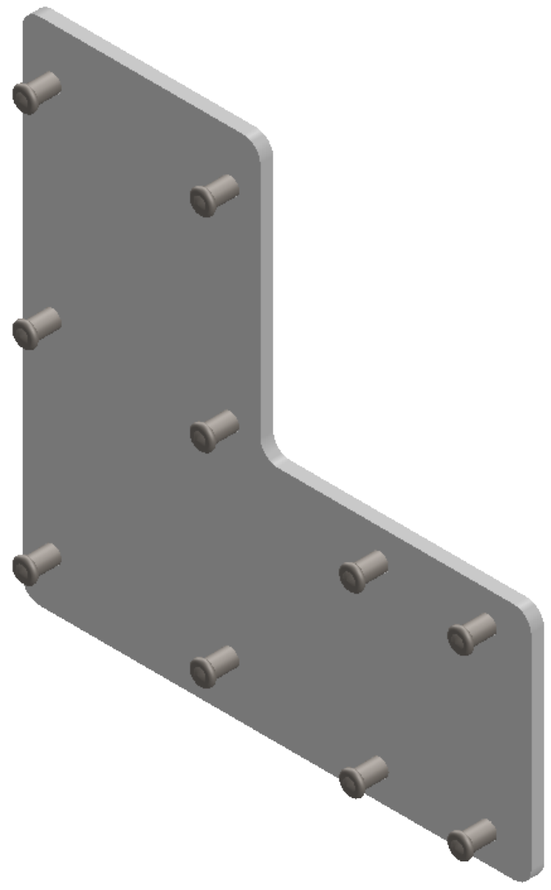


NOTE :
L PALTE
THIS L PLATE IS USED FOR ALL PANEL
LASER CUTTING
THK-3MM

TITLE - ROOF AUTOMATION				NIHVA TECHNOLOGIES PVT.LTD.PUNE
DWG NO - NTPL-000-PM-001-02-05-05				Website - www.nihva.com
	NAME	SIGNATURE	DATE	PROJECT NO - NTPL-000-PM
DRAWN	V.W		23-05-2025	PRODUCT - RETRACTABLE ROOF
CHK'D	S.W.		23-05-2025	SITE LOCATION - LUCKNOW
APPV'D	V.T.		23-05-2025	
if any queries contact - supportautomation@nihva.com				REVISION - QTY - 1
ALL DIMENSION ARE IN mm		A3		SCALE SHEET 15 OF 21

ITEM NO.	PART NUMBER	DESCRIPTION	QTY.
1	L ANGLE PLATE	SS304 - 60X60X3 MM	12
2	RR_rivet_iso_15977_4_x_16_0 SS	RIVET M4X16	8

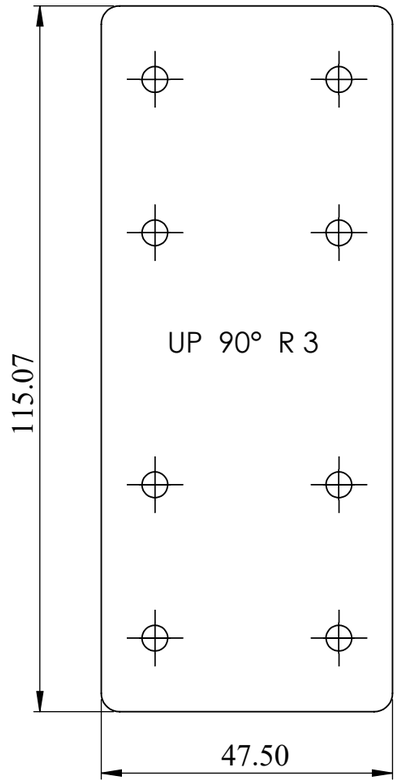


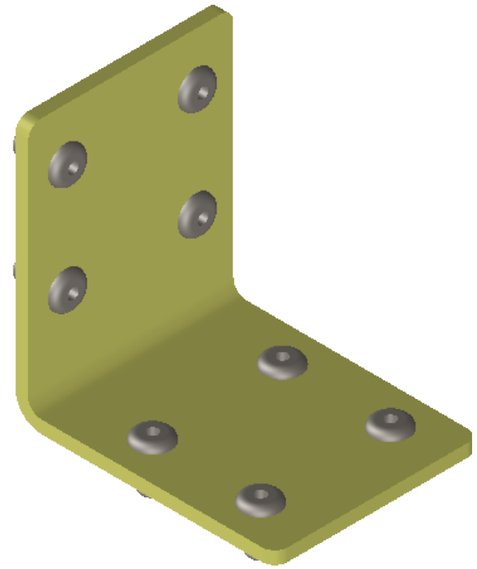


NOTE :
L ANGLE PLATE
THIS L ANGLE PLATE IS USED FOR ALL PANEL
LASER CUTTING
THK-3MM

TITLE - ROOF AUTOMATION				NIHVA TECHNOLOGIES PVT.LTD.PUNE Website - www.nihva.com	
DWG NO - NTPL-000-PM-001-02-06-06					
	NAME	SIGNATURE	DATE	PROJECT NO - NTPL-000-PM	
DRAWN	V.W		23-05-2025	PRODUCT - RETRACTABLE ROOF	
CHK'D	S.W.		23-05-2025	SITE LOCATION - LUCKNOW	
APPV'D	V.T.		23-05-2025		
if any queries contact - supportautomation@nihva.com				REVISION -	QTY - 1
ALL DIMENSION ARE IN mm		A3		SCALE	SHEET 16 OF 21


ITEM NO.	PART NUMBER	DESCRIPTION	QTY.
1	RR_L ANGLE PLATE CORNNER JOINING PLATE	AL JOINING PLATE	4

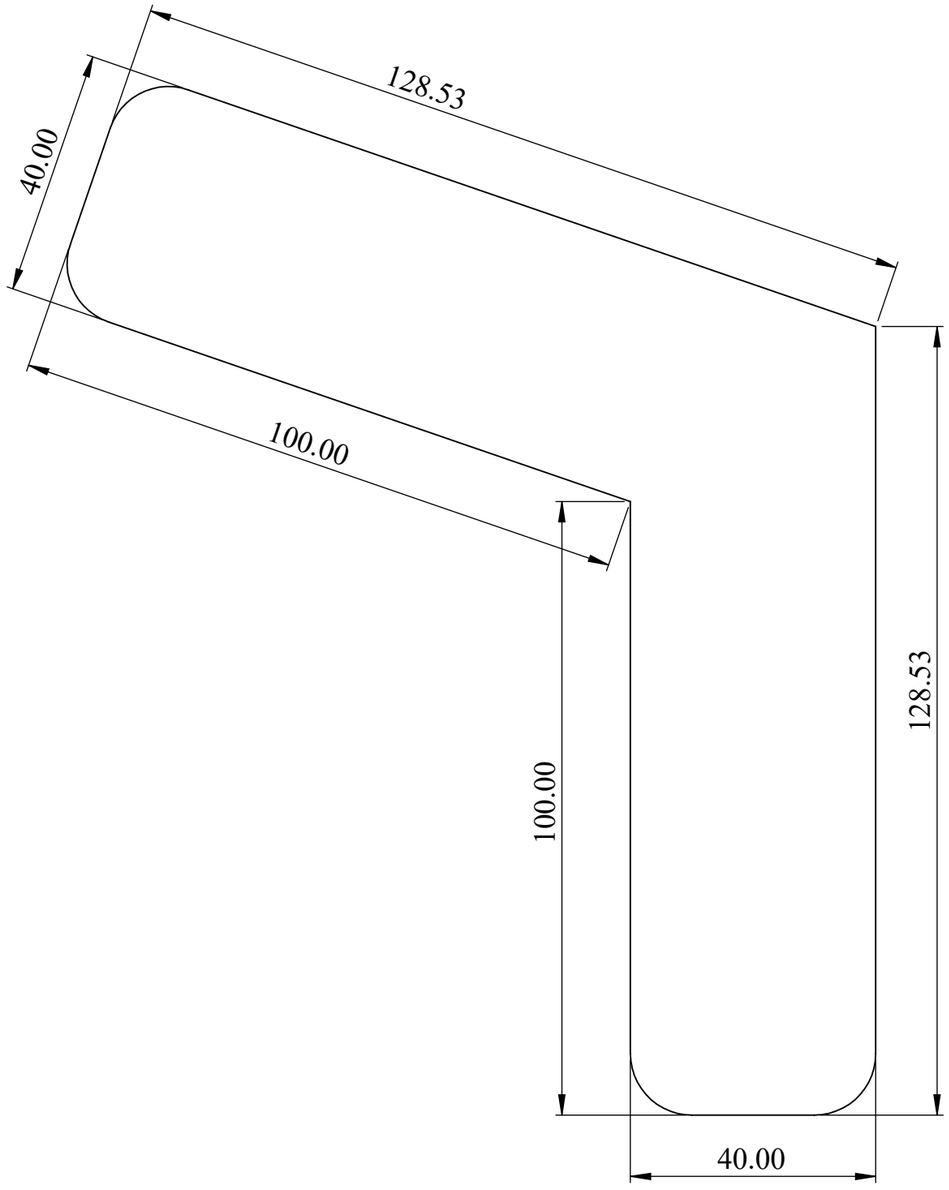


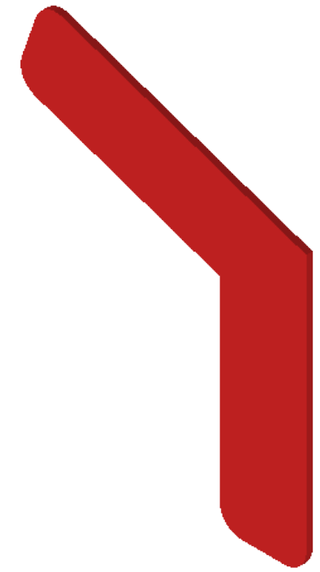


NOTE :
L ANGLE WELDING PLATE
CORNER JOINING PLATE
LASER CUTTING
ALL PANEL THIS PLATE IS USED
THK - 3MM

TITLE - ROOF AUTOMATION				NIHVA TECHNOLOGIES PVT.LTD.PUNE
DWG NO - NTPL-000-PM-001-02-07-07				Website - www.nihva.com
	NAME	SIGNATURE	DATE	PROJECT NO - NTPL-000-PM
DRAWN	V.W		23-05-2025	PRODUCT - RETRACTABLE ROOF
CHK'D	S.W.		23-05-2025	SITE LOCATION - LUCKNOW
APPV'D	V.T.		23-05-2025	
if any queries contact - supportautomation@nihva.com				REVISION - QTY - 1
ALL DIMENSION ARE IN mm		A3		SCALE SHEET 17 OF 21

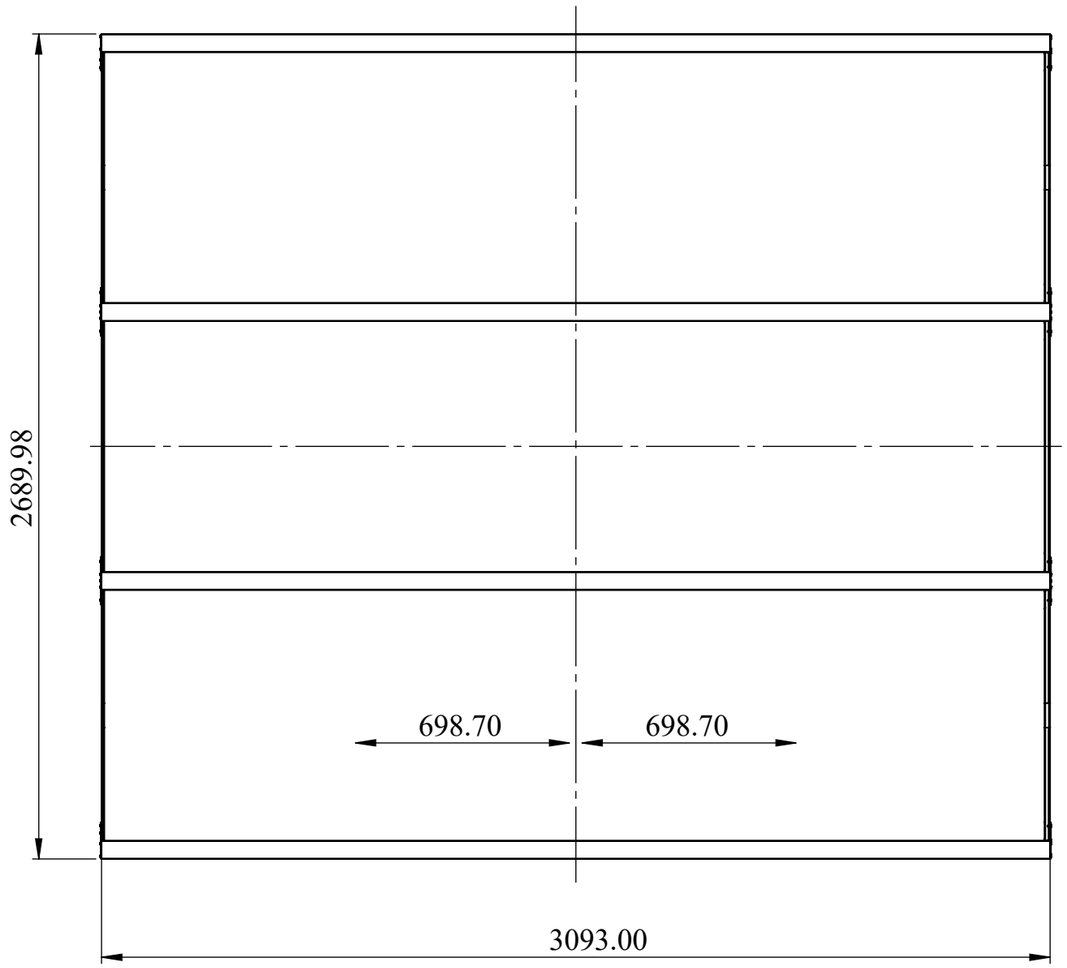

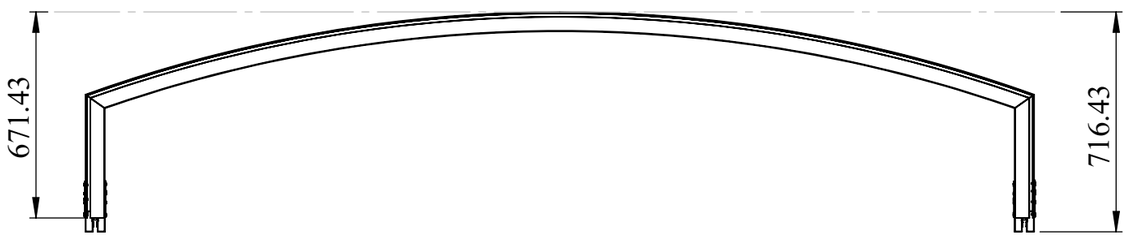


ITEM NO.	PART NUMBER	DESCRIPTION	QTY.
1	RR_ PANEL 2		1
2	AL Support tube SQ TUBE 40X40X1.5 MM L-816.66MM	AL INTERMEDIAT SUPPORT TUBE	15
3	RR_02-PRJ-LUCKANOW 02-PROJECT NO 2-rivet_iso_15977_4_x_16_0	RIVET M4X16	60
4	RR_ BEARING BLOCK ASM WITH SHOULDER BOLT	SLIDING BLOCK	4
5	T PLATE	JOINING PLATE	8
6	L PLATE	JOINING PLATE	8
7	L ANGLE PLATE	JOINING PLATE	12
8	L ANGLE CORNER JOINING PLATE	AL JOINING/WELDING PLATE	4
11	RR_ PANEL 2		3

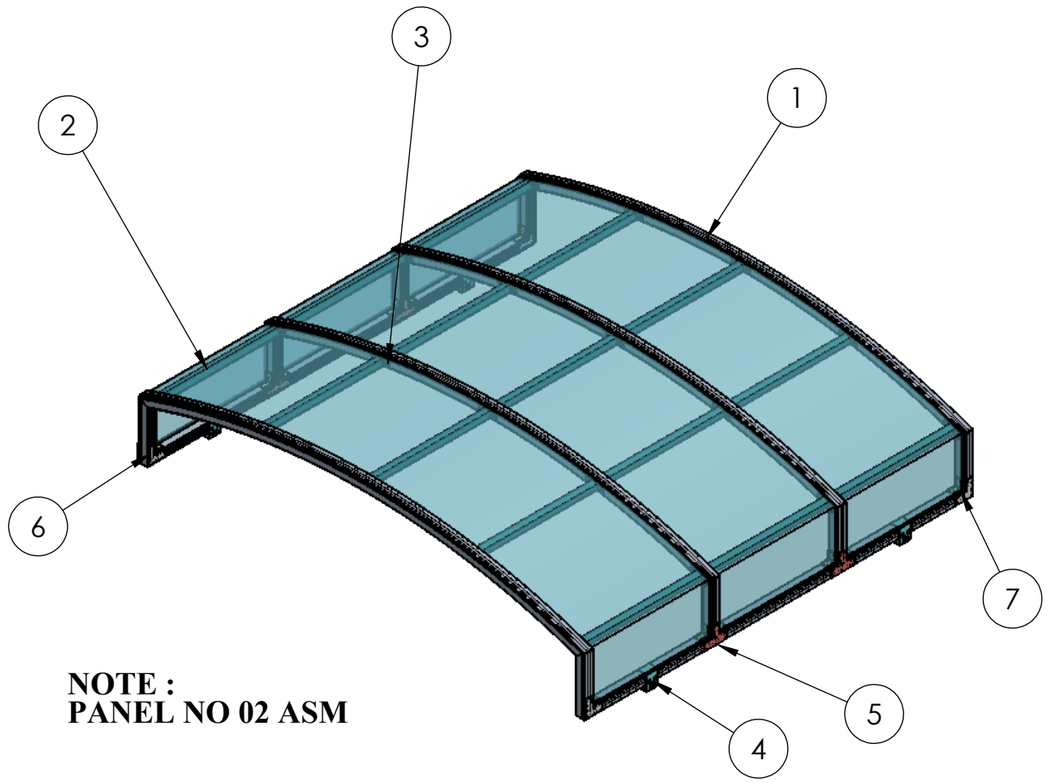


NOTE :
PANEL NO 02 ASM


TITLE - ROOF AUTOMATION				NIHVA TECHNOLOGIES PVT.LTD.PUNE
DWG NO - NTPL-000-PM-001-02-00-02				Website - www.nihva.com
	NAME	SIGNATURE	DATE	PROJECT NO - NTPL-000-PM
DRAWN	V.W		23-05-2025	PRODUCT - RETRACTABLE ROOF
CHK'D	S.W.		23-05-2025	SITE LOCATION - LUCKNOW
APPV'D	V.T.		23-05-2025	
if any queries contact - supportautomation@nihva.com				REVISION - QTY - 1
ALL DIMENSION ARE IN mm		A3		SCALE SHEET 18 OF 21

ITEM NO.	PART NUMBER	DESCRIPTION	QTY.
1	RR_ PANEL 2		1

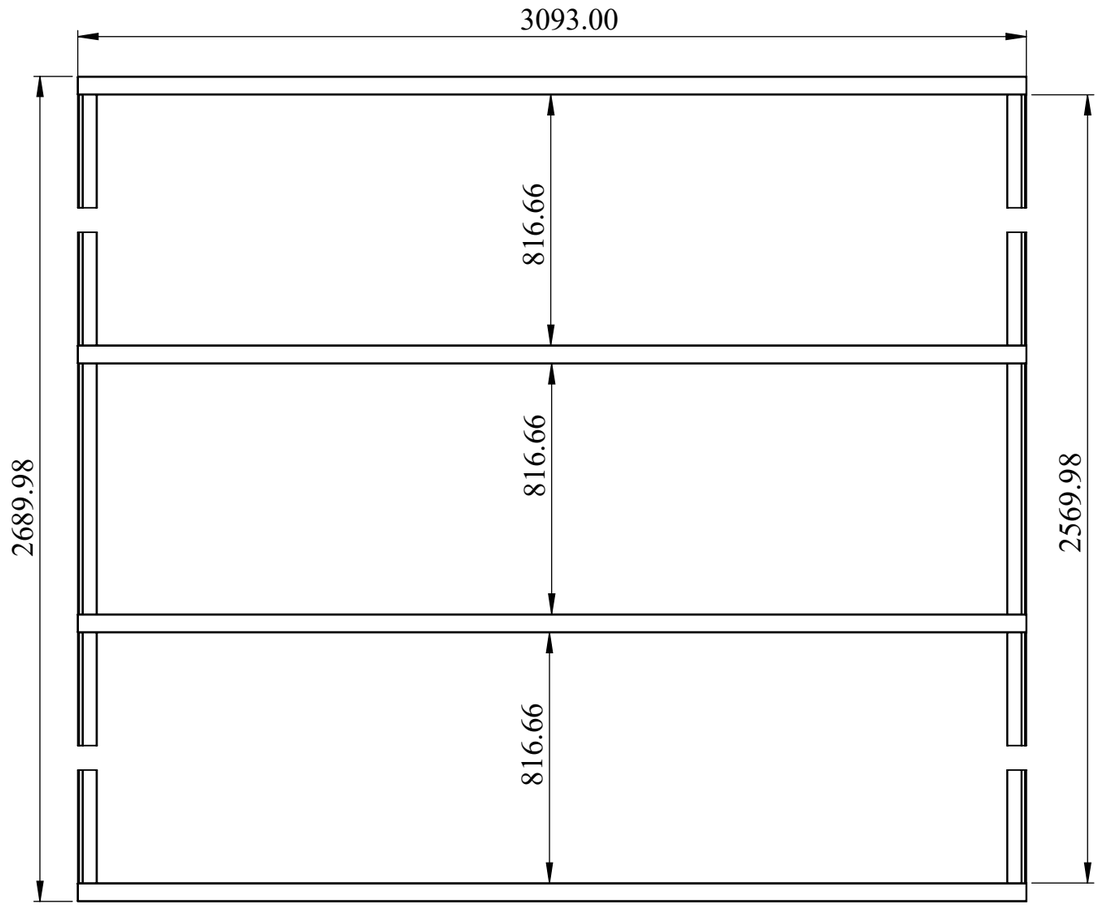


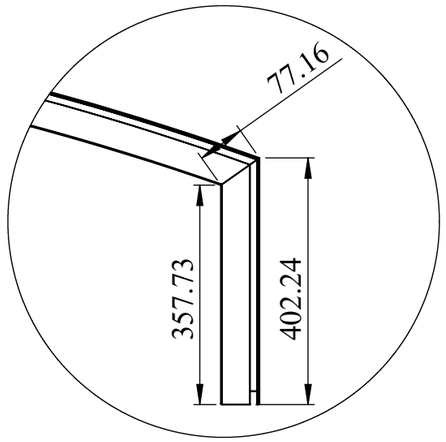

DETAIL A
SCALE 1 : 10

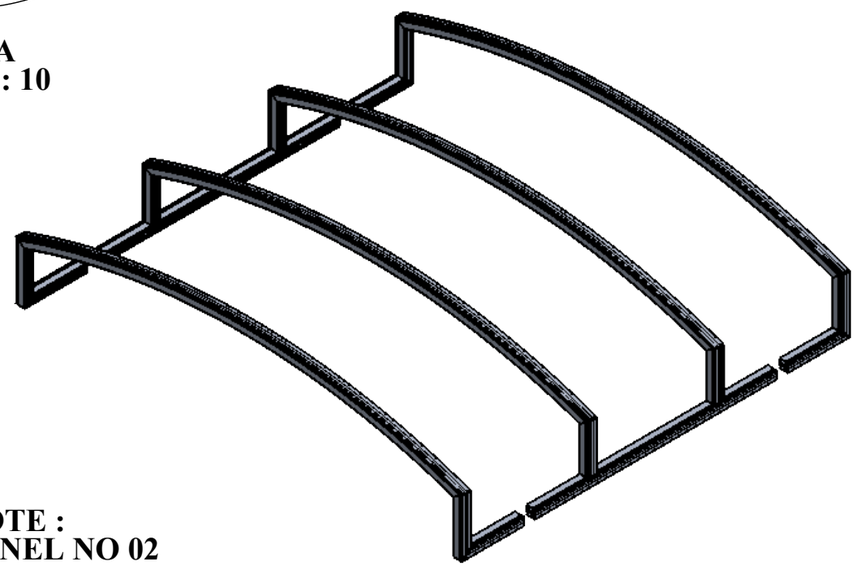



NOTE :
PANEL NO 02

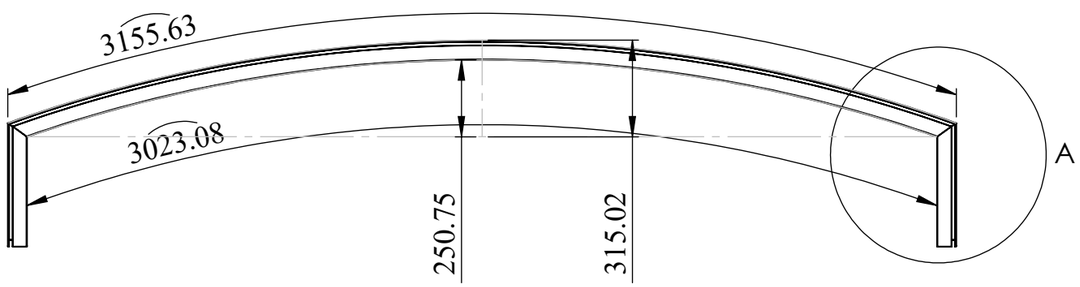


TITLE - ROOF AUTOMATION				NIHVA TECHNOLOGIES PVT.LTD.PUNE Website - www.nihva.com
DWG NO - NTPL-000-PM-001-02-01-02				
	NAME	SIGNATURE	DATE	PROJECT NO - NTPL-000-PM
DRAWN	V.W		23-05-2025	PRODUCT - RETRACTABLE ROOF
CHK'D	S.W.		23-05-2025	SITE LOCATION - LUCKNOW
APPV'D	V.T.		23-05-2025	
if any queries contact - supportautomation@nihva.com				REVISION - / QTY - 1
ALL DIMENSION ARE IN mm		A3		SCALE / SHEET 19 OF 21

ITEM NO.	PART NUMBER	DESCRIPTION	QTY.
1	RR_ENCLOSURE NO 02		1

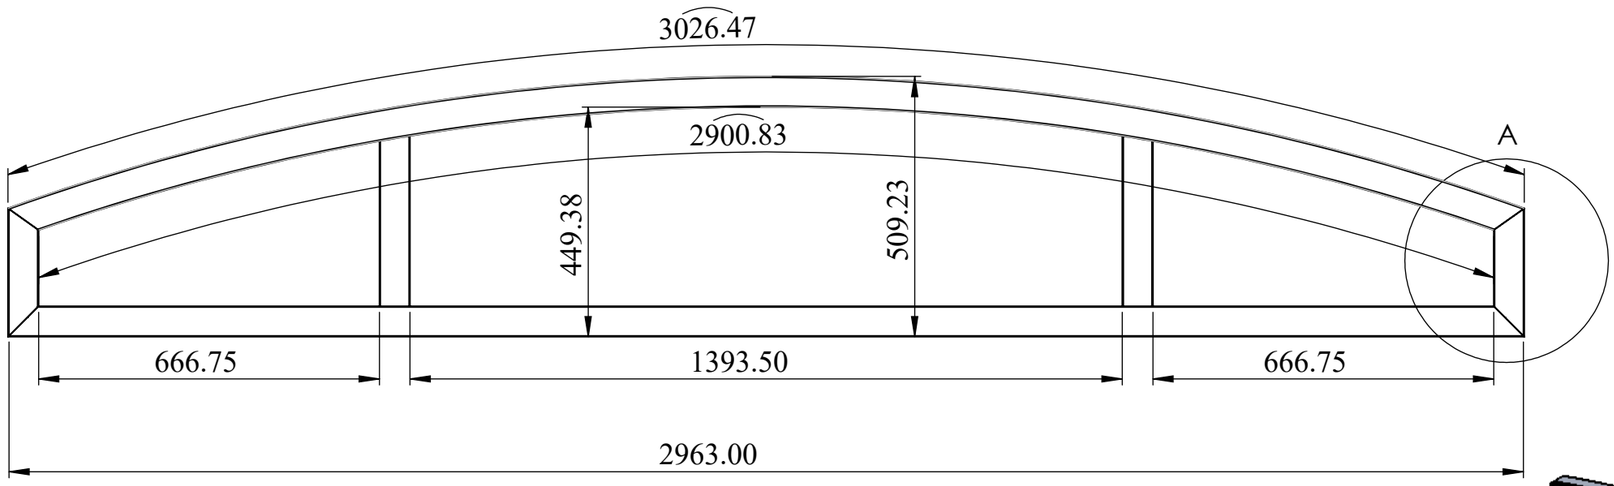

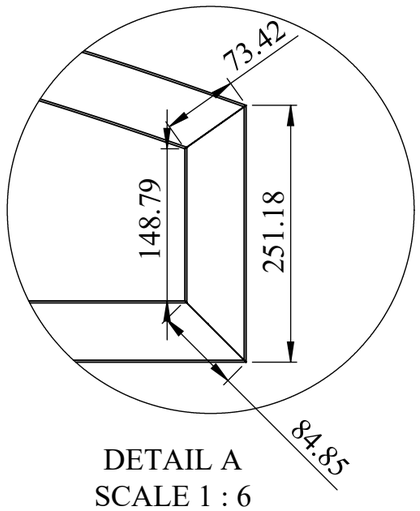

DETAIL A
SCALE 1 : 6

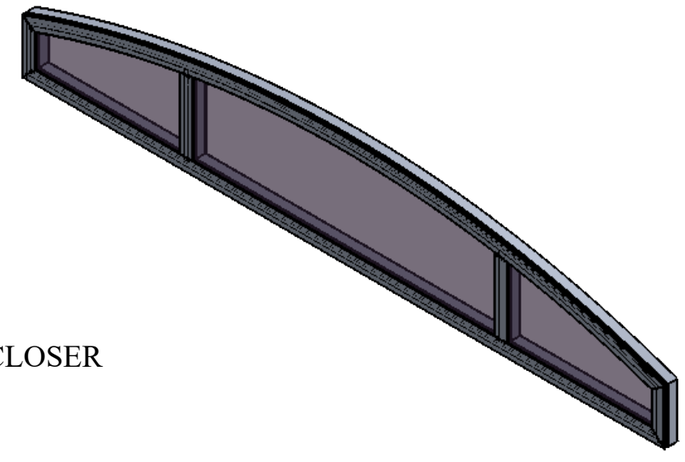

NOTE :
PANEL N0 02 ENCLOSER
ENCLOSER NO 2

TITLE - ROOF AUTOMATION				NIHVA TECHNOLOGIES PVT.LTD.PUNE Website - www.nihva.com
DWG NO - NTPL-000-PM-001-02-02-07				
	NAME	SIGNATURE	DATE	PROJECT NO - NTPL-000-PM
DRAWN	V.W		23-05-2025	PRODUCT - RETRACTABLE ROOF
CHK'D	S.W.		23-05-2025	SITE LOCATION - LUCKNOW
APPV'D	V.T.		23-05-2025	
if any queries contact - supportautomation@nihva.com				REVISION - QTY - 1
ALL DIMENSION ARE IN mm			A3	SCALE SHEET 20 OF 21

TITLE - ROOF AUTOMATION

DWG NO - NTPL-000-PM-001-00-00-00

NIHVA TECHNOLOGIES PVT.LTD.PUNE

Website - www.nihva.com

	NAME	SIGNATURE	DATE
DRAWN	V.W		20-05-2025
CHK'D	S.W.		20-05-2025
APPV'D	V.T.		20-05-2025

PROJECT NO - NTPL-000-PM

PRODUCT - RETRACTABLE ROOF

SITE LOCATION - LUCKNOW

if any queries contact - supportautomation@nihva.com

REVISION -

QTY - 1

ALL DIMENSION ARE IN mm

A3

SCALE

SHEET 21 OF 21